Govemment Of Ras Al Khaimah
R.A.K. Municipality
Buildings Administration

حكومة رأس الخيمة
دائـرة البلـدية
إدارة المباني

Approved On — اعتمد في

21 January 2026

Building Permit #: PRMT-26-0000580

Appoved By:

Ground Floor Area
BLD-25-02856

First Floor Area
BLD-25-02856

Area Statement	
Building Number	BLD-25-02856
Ground Floor Area	476m²
First Floor Area	303.m²
Total Building Area	779m²
PLOT AREA ACCORDING TO KRUKI	1457.29 m²
BUILD UP RATIO	32

Savana
Engineering Consultancy & interior design

Client	ADEL ALI ASHEHHI		
Project	DOUBLE STORY VILLA		
Drg.Title	AreaStatement		
Area	SEIH AL URAIBI	Floortype	
Case ID.	3143538	Draw. Type.	ARCH
Sec No.	1	Com. No.	
Block No.		Plot No.	208090106
Bldg. No.	BLD-25-02856	Floor No.	
Date	2026	Sht. No.	A-01
Scale	1/100	Job No.	

G.Manager	Architect	Designed By
ENG AYMEN	ENG IMEN	ENG OMAR

AREA STATMENTENT

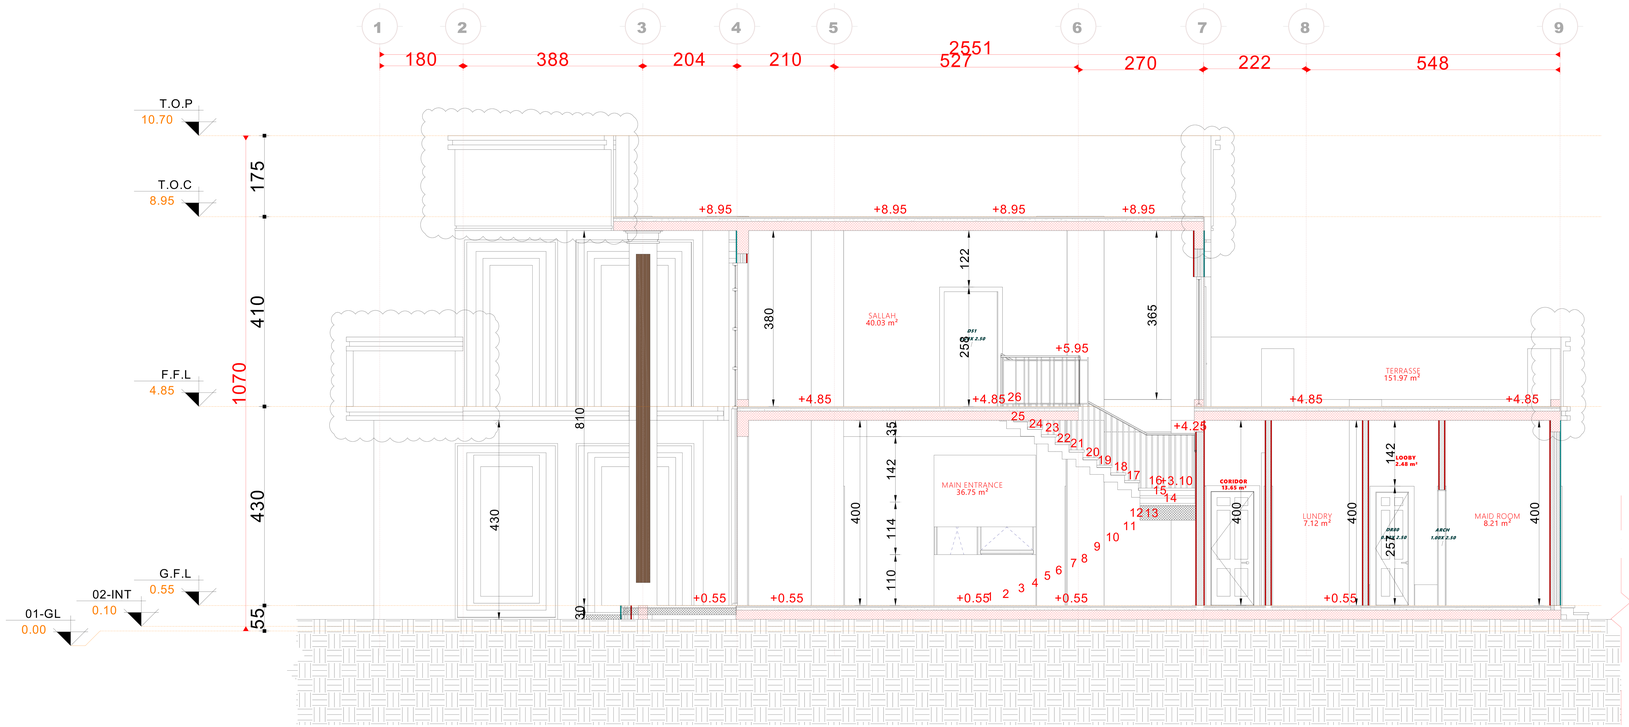

Gevernment Of Ras Al Khaimah
R.A.K. Municipality
Buildings Administration

حكومة رأس الخيمة
دائرة البلدية
إدارة المباني

Approved On — اعتمد في

21 January 2026

Building Permit #: PRMT-26-0000580

Appoved By:

GROUND FLOOR LEVEL	GFL
FRIST FLOOR FINSHING	FFL
TOP OF CONCRETE	TOC
TOP OF PARAPET	TOP

ALL GLASS MUST BE DOUBLE UNITES

GLASS SPECIFICATION:-

U-value (w/m2.k)<_ 1.8

SHADING CO- EFFICIENT (SC) <0.3

FINSHING	
1	FULL EPOXY PAINT [white]
2	FULL EPOXY BLACK PAINT
3	WOOD Aluminum
4	

Savana
Engineering Consultancy & interior design

Client	ADEL ALI ASHEHHI		
Project	DOUBLE STORY VILLA		
Drg.Title	SECTION B-B		
Area	SEIH AL URAIBI	Floortype	
Case ID.	3143538	Draw. Type.	ARCH
Sec No.	1	Com. No.	
Block No.		Plot No.	208090106
Bldg. No.	BLD-25-02856	Floor No.	
Date	2026	Sht. No.	A12
Scale	1/100	Job No.	

G.Manager	Architect	Designed By
ENG AYMEN	ENG IMEN	ENG OMAR

SECTION B-B

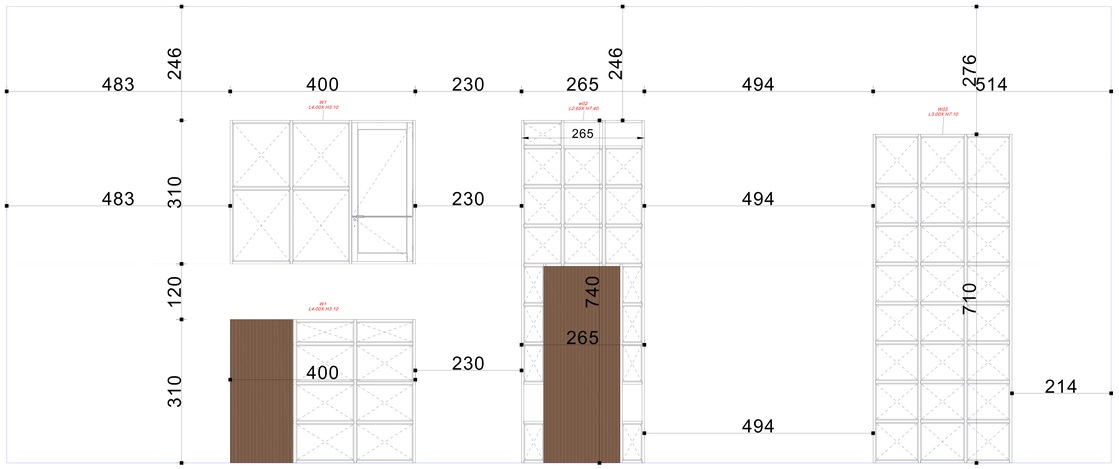

14

1 : 50

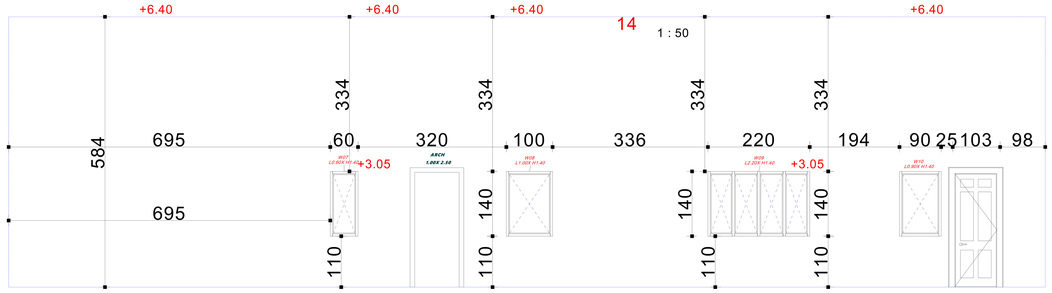

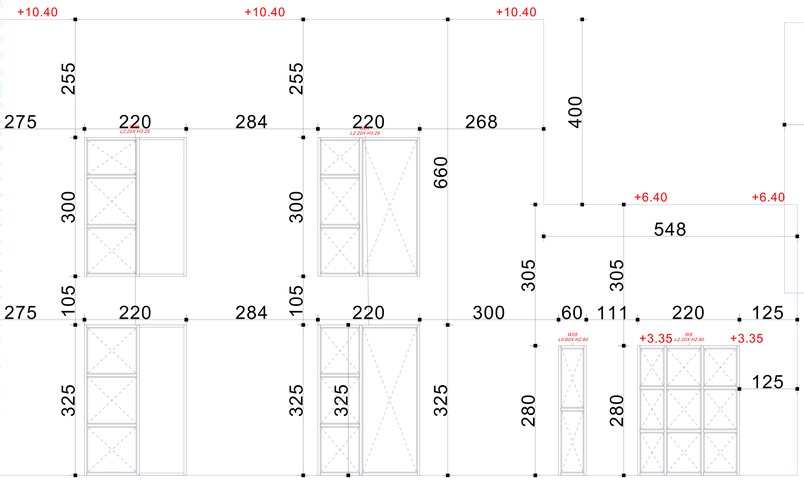

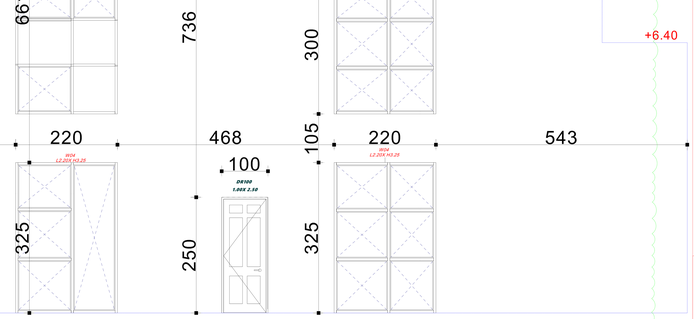

ARCH 100 (ARCH)-ELEVATION

DB 90 DOOR (DB)-ELEVATION

ND 100 DOOR (ND)-ELEVATION

PD 150 DOOR (PD)-ELEVATION

DW 200 DOOR (DW)-ELEVATION

Govemment Of Ras Al Khaimah
R.A.K. Municipality
Buildings Administration

حكومة رأس الخيمة
دائرة البلدية
إدارة المباني

Approved On — اعتمد في

21 January 2026

Building Permit #: PRMT-26-0000580

Appoved By:

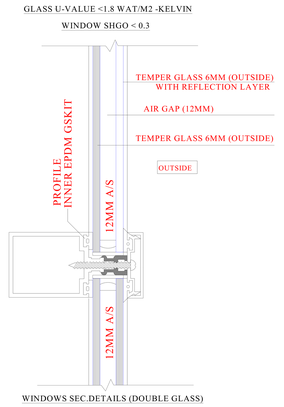

WINDOWS SEC.DETAILS (DOUBLE GLASS)

ALL GLASS MUST BE DOUBLE UNITES

GLASS SPECIFICATION:-

U-value (w/m2.k)<_ 1.8

SHADING CO- EFFICIENT (SC) <0.3

Savana
Engineering Consultancy & interior design

Client	ADEL ALI ASHEHHI		
Project	DOUBLE STORY VILLA		
Drg.Title	Opening Details		
Area	SEIH AL URAIBI	Floortype	
Case ID.	3143538	Draw. Type.	ARCH
Sec No.	1	Com. No.	
Block No.		Plot No.	208090106
Bldg. No.	BLD-25-02856	Floor No.	
Date	2026	Sht. No.	A13
Scale	1/100	Job No.	

G.Manager	Architect	Designed By
ENG AYMEN	ENG IMEN	ENG OMAR

PERSPECTIVE

Govemment Of Ras Al Khaimah
R.A.K. Municipality
Buildings Administration

حكومة رأس الخيمة
دائـرة البلـدية
إدارة المباني

Approved On — اعتمد في

21 January 2026

Building Permit #: PRMT-26-0000580

Appoved By:

Savana
Engineering Consultancy & interior design

Client	ADEL ALI ASHEHHI		
Project	DOUBLE STORY VILLA		
Drg.Title	PERSPECTIVE		
Area	SEIH AL URAIBI	Floortype	
Case ID.	3143538	Draw. Type.	ARCH
Sec No.	2	Com. No.	
Block No.		Plot No.	208090106
Bldg. No.	BLD-25-02856	Floor No.	
Date	2026	Sht. No.	A14
Scale	1/100	Job No.	

G.Manager	Architect	Designed By
ENG AYMEN	ENG IMEN	ENG OMAR

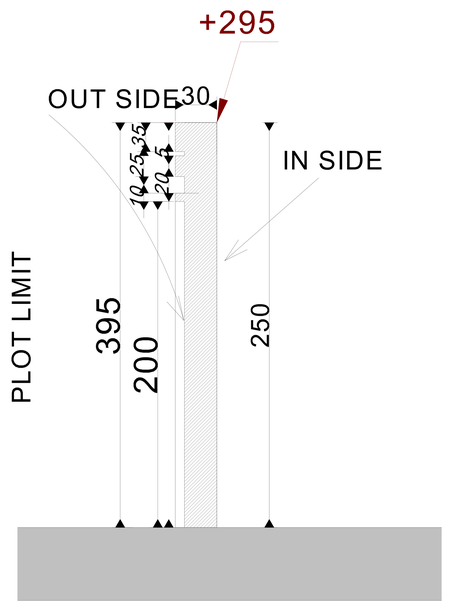

SECTION C-C

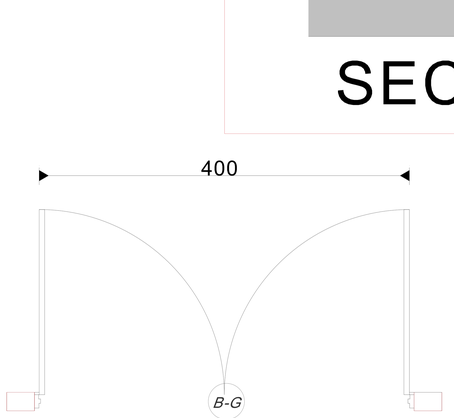

DOOR (BG)-ELEVATION

SCALE 1:50

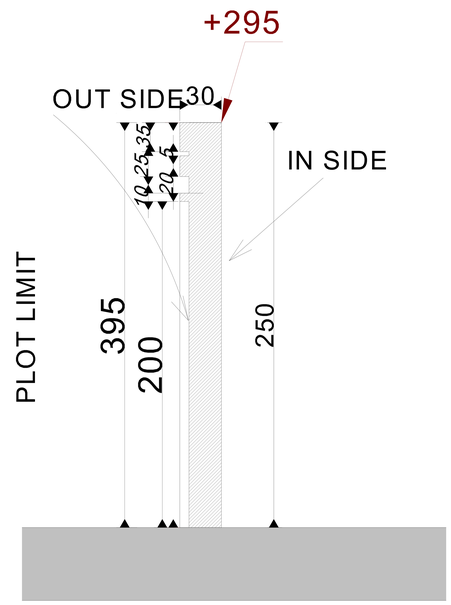

SECTION D-D

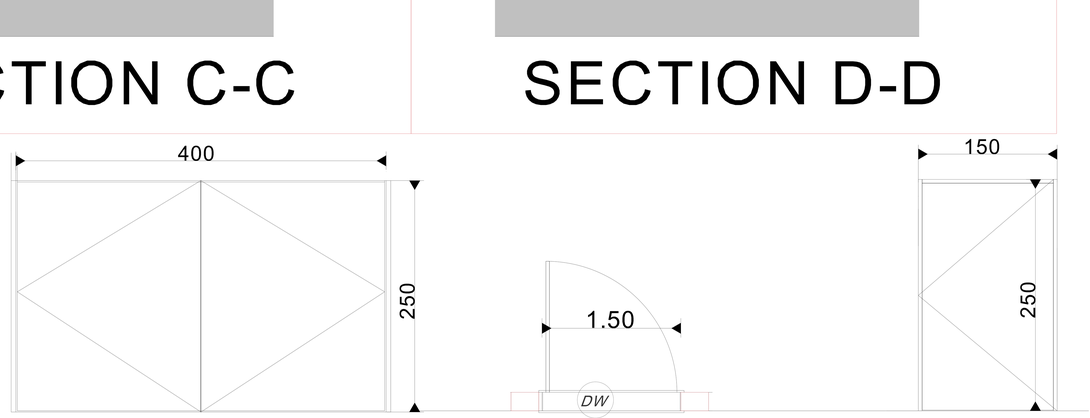

DOOR (DB)-ELEVATION

SCALE 1:50

B.WALL SECTION

Govemment Of Ras Al Khaimah
R.A.K. Municipality
Buildings Administration
حكومة رأس الخيمة
دائرة البلدية
إدارة المباني
Approved On
اعتمد في
23 January 2026
Building Permit #:
PRMT-26-0000580
Appoved By:

Savana
Engineering Consultancy & interior design

Client	ADEL ALI ASHEHHI		
Project	DOUBLE STORY VILLA		
Drg.Title	Boundary Wall DETAILS		
Area	SEIH AL URAIBI	Floortype	
Case ID.	3143538	Draw. Type.	ARCH
Sec No.	2	Com. No.	
Block No.		Plot No.	208090106
Bldg. No.	FNC-26-000197	Floor No.	
Date	2026	Sht. No.	A17
Scale	1/100	Job No.	

G.Manager	Architect	Designed By
ENG AYMEN	ENG IMEN	ENG OMAR

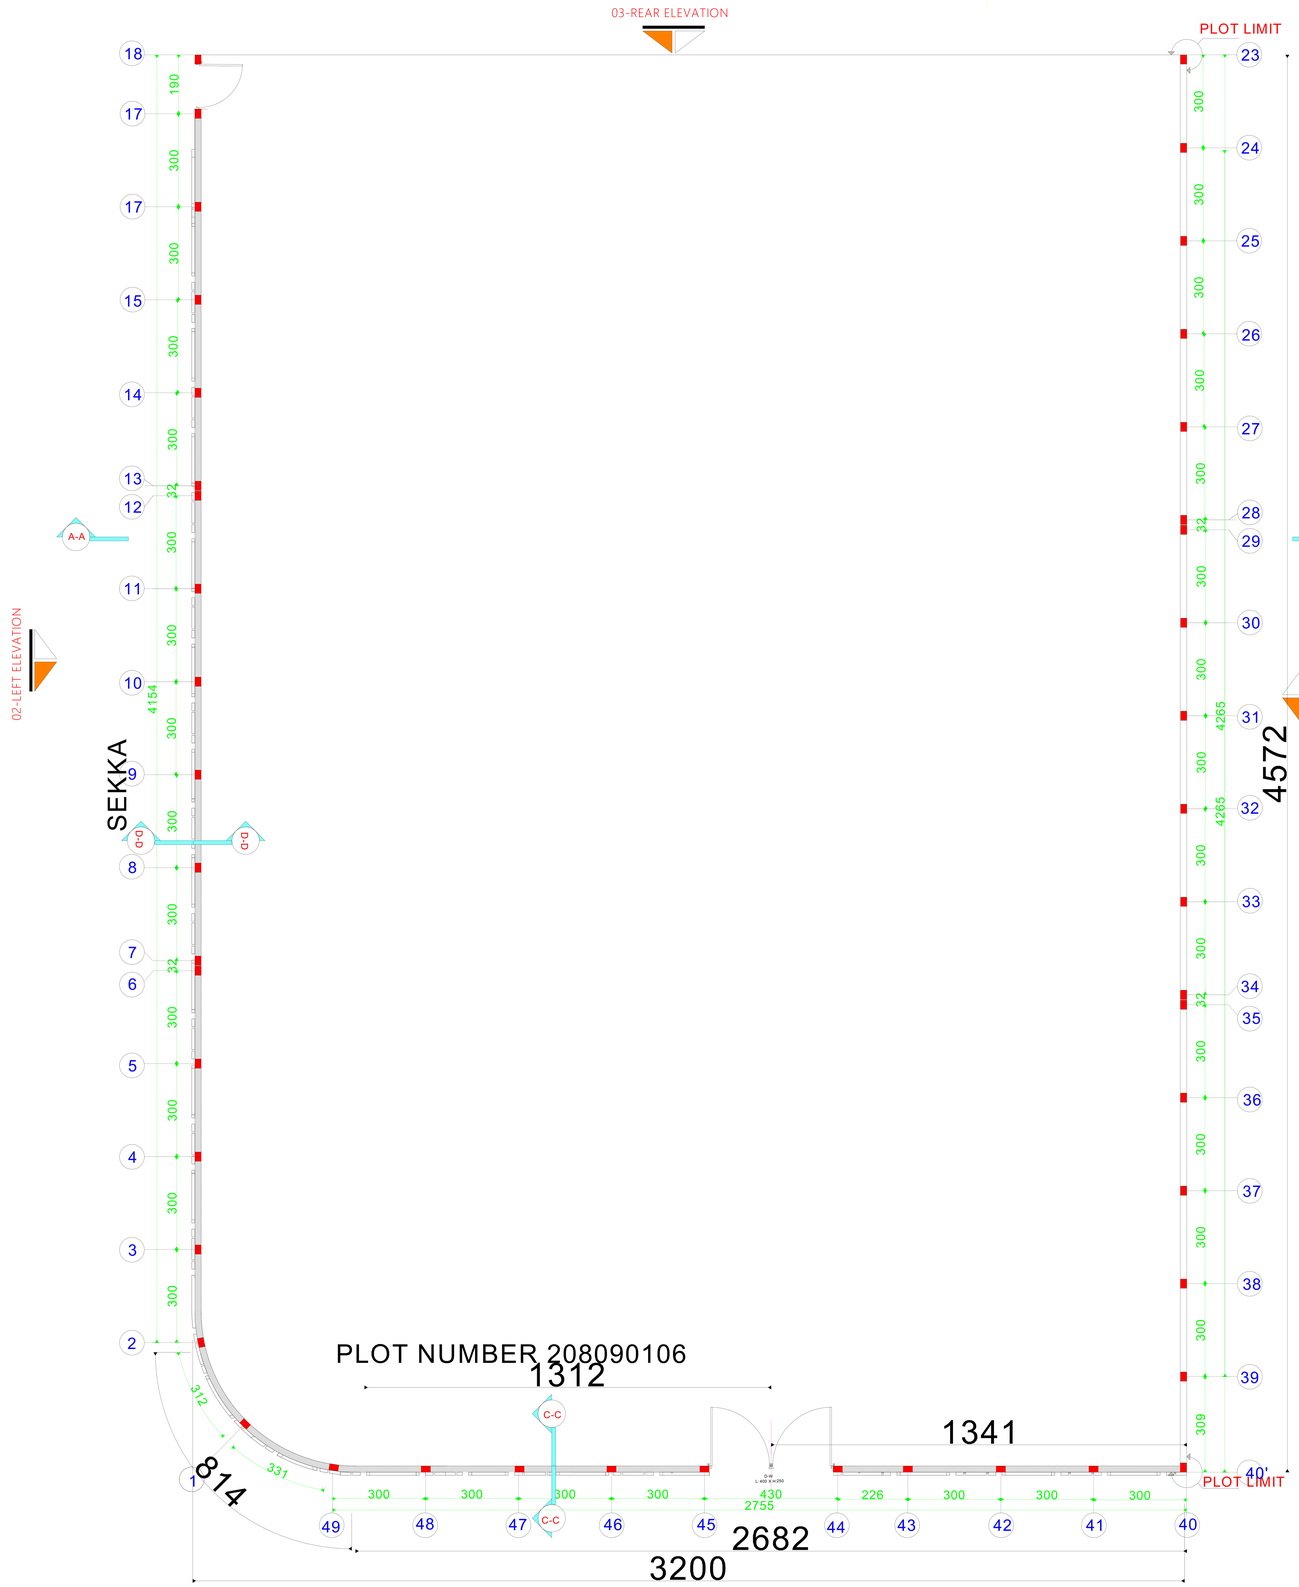

Govemment Of Ras Al Khaimah
R.A.K. Municipality
Buildings Administration

حكومة رأس الخيمة
دائرة البلدية
إدارة المباني

Approved On — اعتمد في

23 January 2026

Building Permit #: PRMT-26-0000580

Appoved By:

B.WALL SITE PLAN

Savana
Engineering Consultancy & interior design

Client	ADEL ALI ASHEHHI		
Project	DOUBLE STORY VILLA		
Drg.Title	BOUNDARY WALL LAYOUT PLAN		
Area	SEIH AL URAIBI	Floortype	
Case ID.	3143538	Draw. Type.	ARCH
Sec No.	2	Com. No.	
Block No.		Plot No.	208090106
Bldg. No.	FNC-26-000197	Floor No.	
Date	2026	Sht. No.	A15
Scale	1/100	Job No.	

G.Manager	Architect	Designed By
ENG AYMEN	ENG IMEN	ENG OMAR

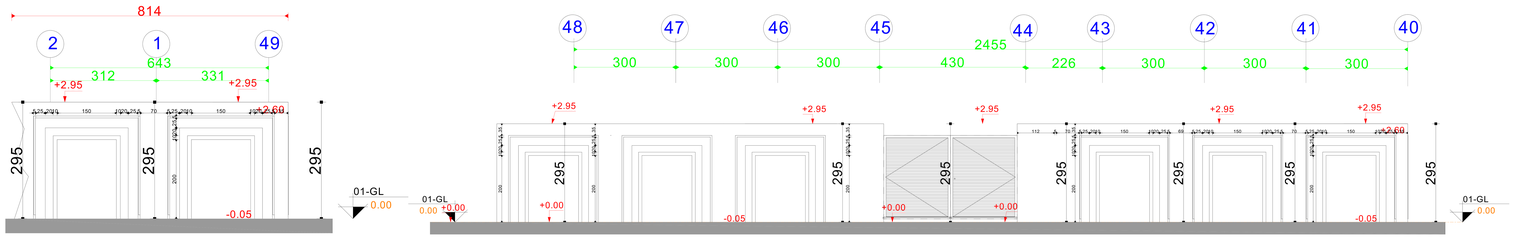

FRONT ELEVATION

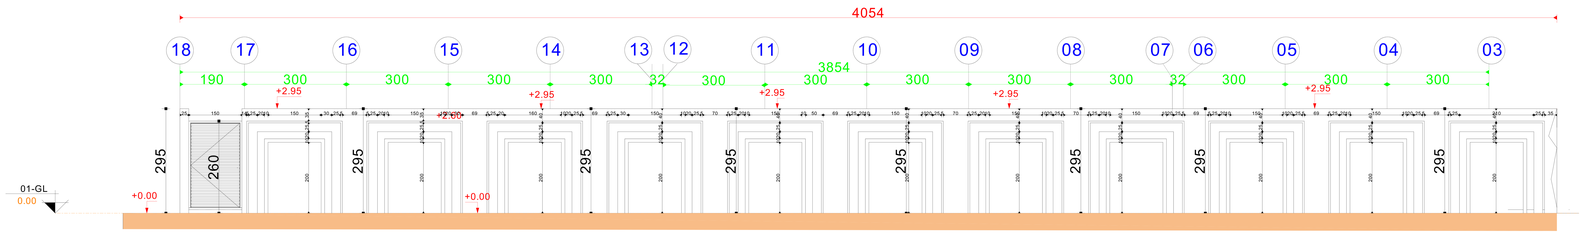

LIFT ELVATION

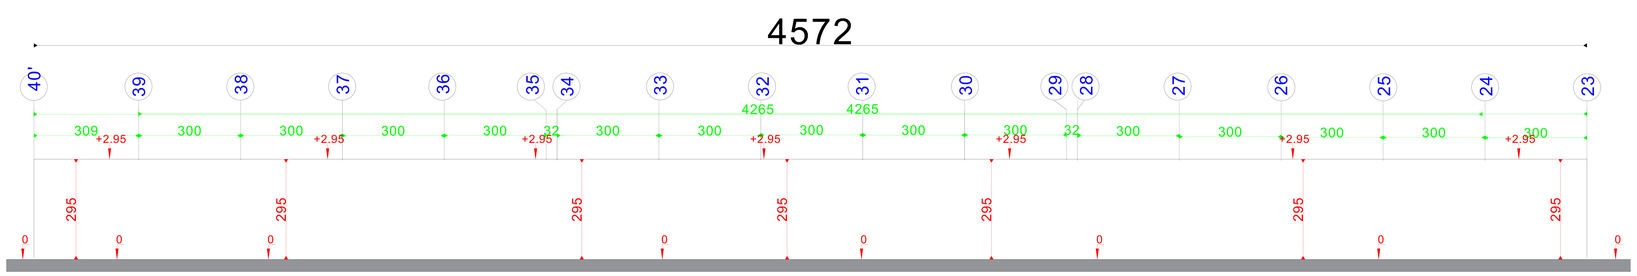

RIGHT ELEVATION

B.WALL ELEVATION

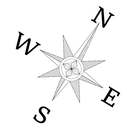

Govemment Of Ras Al Khaimah
R.A.K. Municipality
Buildings Administration

حكومة رأس الخيمة
دائـرة البلـدية
إدارة المباني

Approved On — اعتمد في

23 January 2026

Building Permit #: PRMT-26-0000580

Appoved By:

Savana
Engineering Consultancy & Interior design

Client	ADEL ALI ASHEHHI		
Project	DOUBLE STORY VILLA		
Drg.Title	Proposed Boundary Wall Elevations		
Area	SEIH AL URAIBI	Floortype	
Case ID.	3143538	Draw. Type.	ARCH
Sec No.	2	Com. No.	
Block No.		Plot No.	208090106
Bldg. No.	FNC-26-000197	Floor No.	
Date	2026	Sht. No.	A16
Scale	1/100	Job No.	

G.Manager	Architect	Designed By
ENG AYMEN	ENG IMEN	ENG OMAR

A16 B.WALL ELEVATION

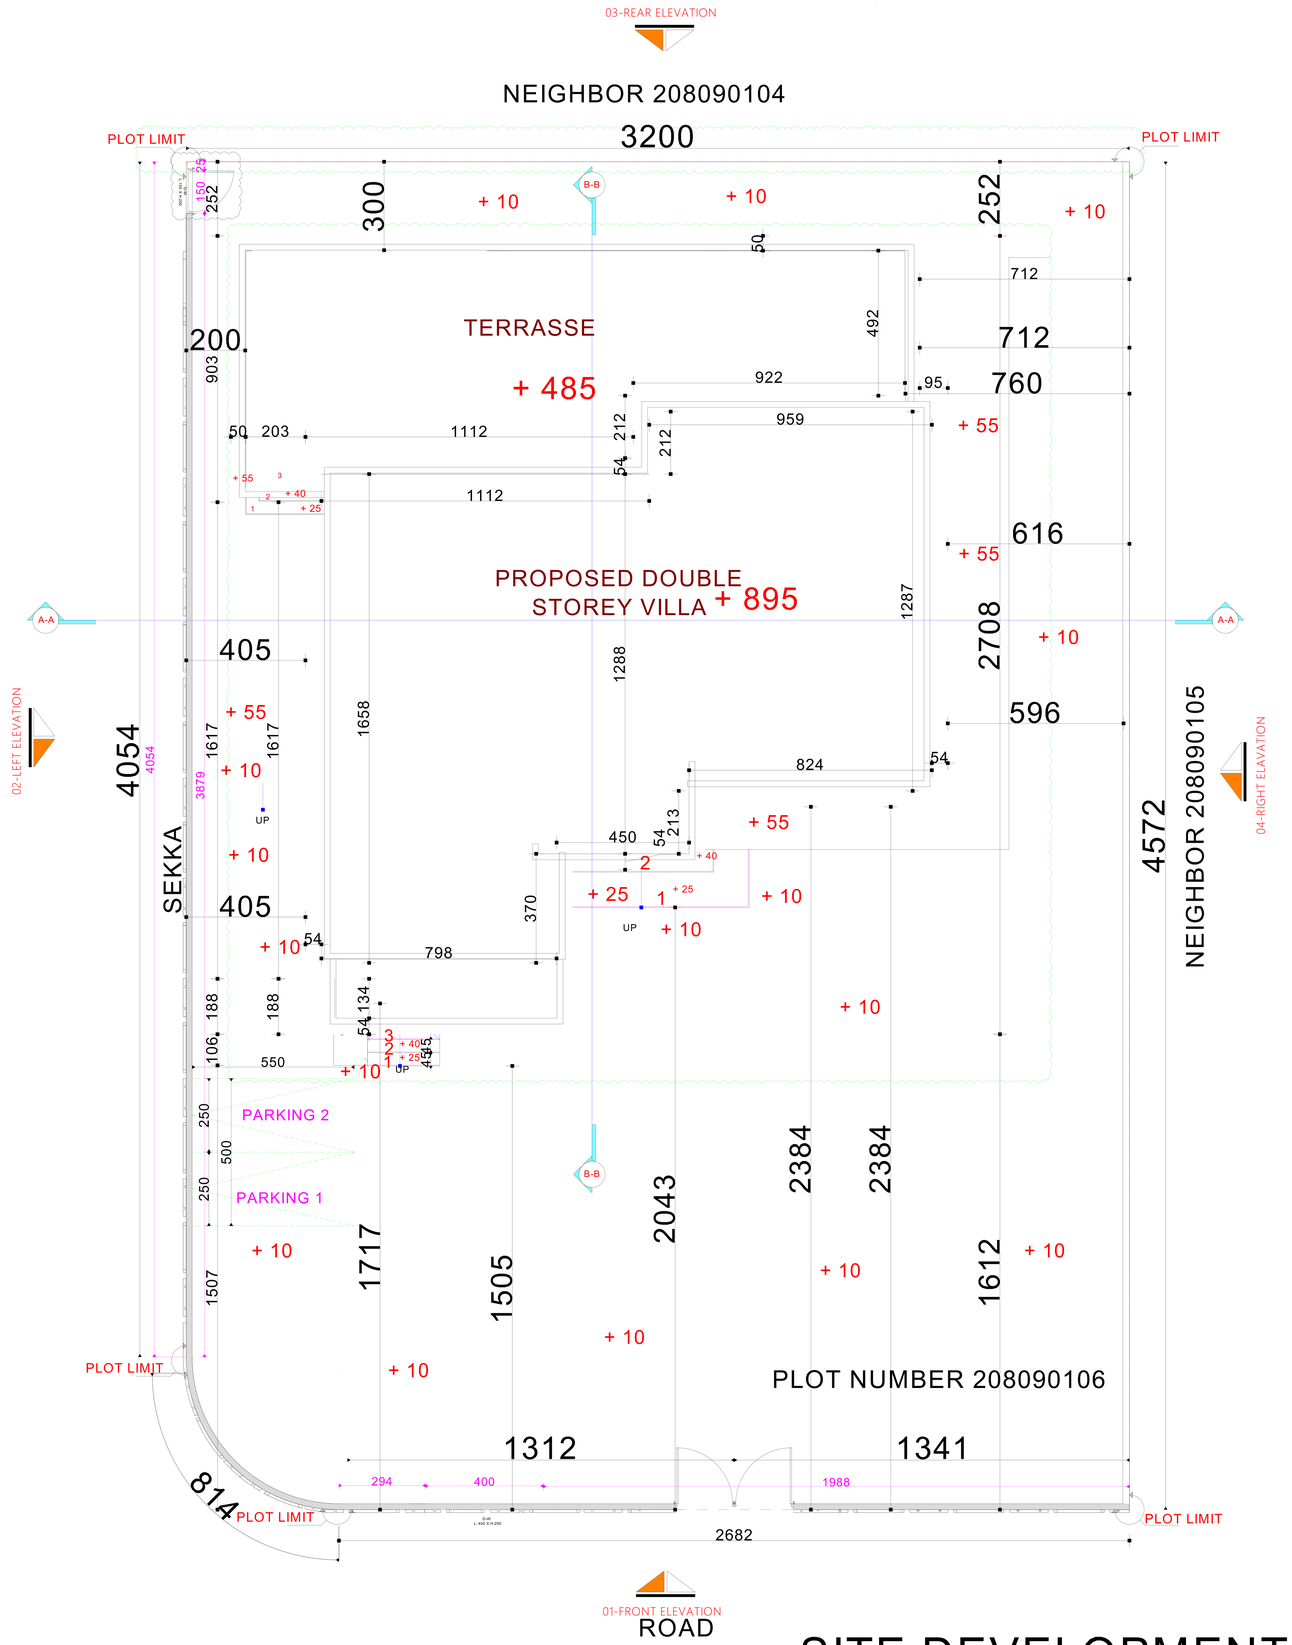

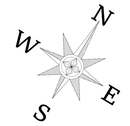

Govemment Of Ras Al Khaimah
R.A.K. Municipality
Buildings Administration

حكومة رأس الخيمة
دائـرة البلـدية
إدارة المباني

Approved On — اعتمد في

23 January 2026

Building Permit #: PRMT-26-0000580

Appoved By:

Note :-

* Rcc Lintels Must Be Made On Top Of All Doors , Arches And Windows All Of Them Are At Least 0.20 m Thick.
* All Blocks Adjacent To All Doors , Arches And Windows Must Be A Solid Block .

Savana
Engineering Consultancy & interior design

Client	ADEL ALI ASHEHHI		
Project	DOUBLE STORY VILLA		
Drg.Title	Site Development Layout Plan		
Area	SEIH AL URAIBI	Floortype	
Case ID.	3143538	Draw. Type.	ARCH
Sec No.	1	Com. No.	
Block No.		Plot No.	208090106
Bldg. No.	BLD-25-02856	Floor No.	
Date	2026	Sht. No.	A02
Scale	1/100	Job No.	

G.Manager	Architect	Designed By
ENG AYMEN	ENG IMEN	ENG OMAR

SITE DEVELOPMENT LAYOUT PLAN

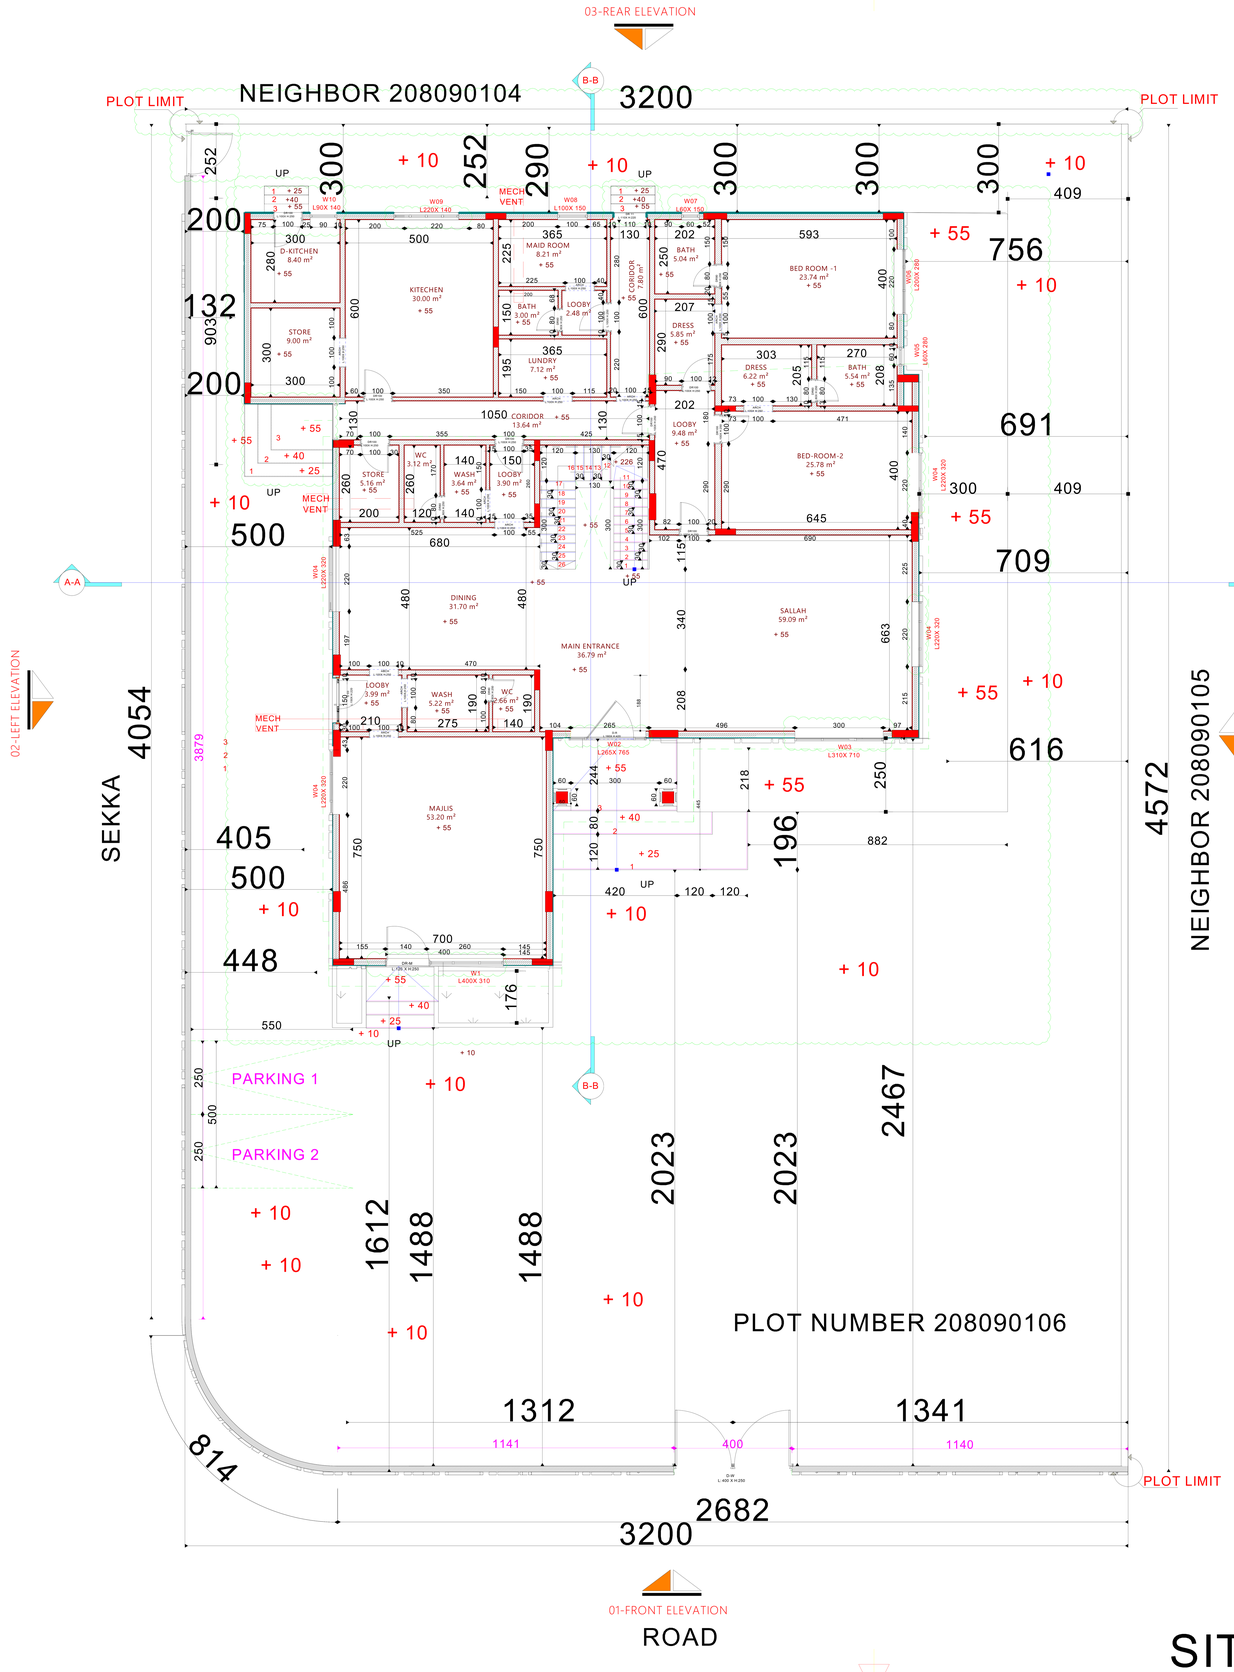

Government Of Ras Al Khaimah
R.A.K. Municipality
Buildings Administration

حكومة رأس الخيمة
دائرة البلدية
إدارة المباني

Approved On — اعتمد في

23 January 2026

Building Permit #: PRMT-26-0000580

Approved By:

Savana
Engineering Consultancy & Interior design

Client	ADEL ALI ASHEHHI		
Project	DOUBLE STORY VILLA		
Drg.Title	SITE SETTING PLAN		
Area	SEIH AL URAIBI	Floortype	
Case ID.	3143538	Draw. Type.	ARCH
Sec No.	1	Com. No.	
Block No.		Plot No.	208090106
Bldg. No.	BLD-25-02856	Floor No.	
Date	2026	Sht. No.	A03
Scale	1/100	Job No.	

G.Manager	Architect	Designed By
ENG AYMEN	ENG IMEN	ENG OMAR

SITE SETTING PLAN

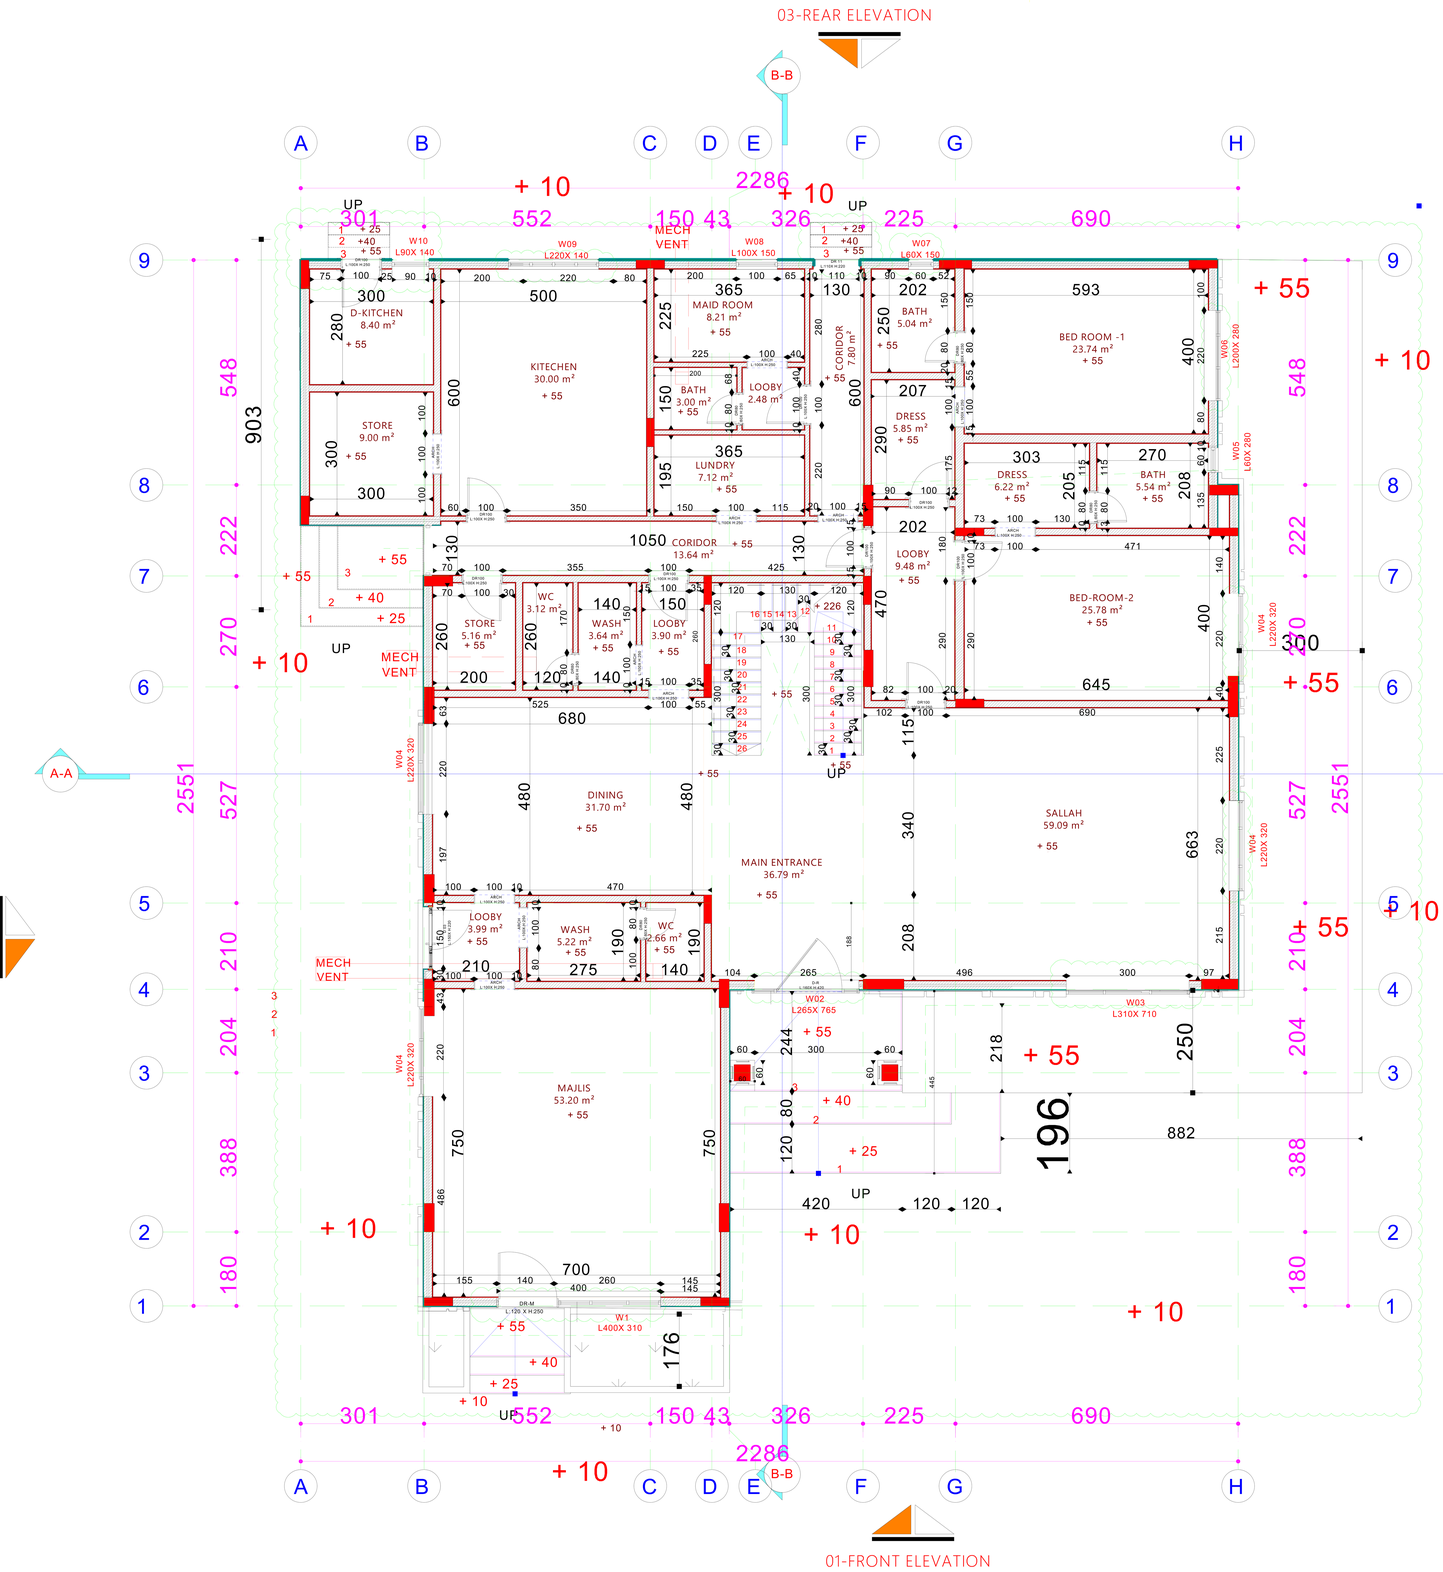

Gevernment Of Ras Al Khaimah
R.A.K. Municipality
Buildings Administration

حكومة رأس الخيمة
دائرة البلدية
إدارة المباني

Approved On — اعتمد في

28 January 2026

Building Permit #: PRMT-26-0000580

Approved By:

FINISHING FOR VERANDAH	FINISHING FOR DRESSING AREA	FINISHING FOR BATH,WC & WASH	
F3 Marble Tiles	F2 Ceramic Tiles (Non Slippery)	F1 Ceramic glazed tiles	FLOORING
W3 Epoxy paint.	W2 Ceramic tiles up to ceiling	W1 Acrylic emulsion paint	WALLS
C3 Epoxy paint.	C2 Oil Paint.	C1 Acrylic emulsion paint	CEILING
S2 Marble tiles 10cm hight		S1 Ceramic Tiles. 10cm hight	SKIRTING

Note :-

* Rcc Lintels Must Be Made On Top Of All Doors , Arches And Windows All Of Them Are At Least 0.20 m Thick.
* All Blocks Adjacent To All Doors , Arches And Windows Must Be A Solid Block .

Rooms	Space	Number
Residential	440.19	
Commercial		
Industrial		
Goverment		
Resident.-Comm.		
Total		

Savana
Engineering Consultancy & interior design

Client	ADEL ALI ASHEHHI		
Project	DOUBLE STORY VILLA		
Drg.Title	GROUND FLOOR PLAN		
Area	SEIH AL URAIBI	Floortype	G
Case ID.	3143538	Draw. Type.	ARCH
Sec No.	1	Com. No.	
Block No.		Plot No.	208090106
Bldg. No.	BLD-25-02856	Floor No.	01
Date	2026	Sht. No.	A04
Scale	1/100	Job No.	

G.Manager	Architect	Designed By
ENG AYMEN	ENG IMEN	ENG OMAR

GROUND FLOOR PLAN