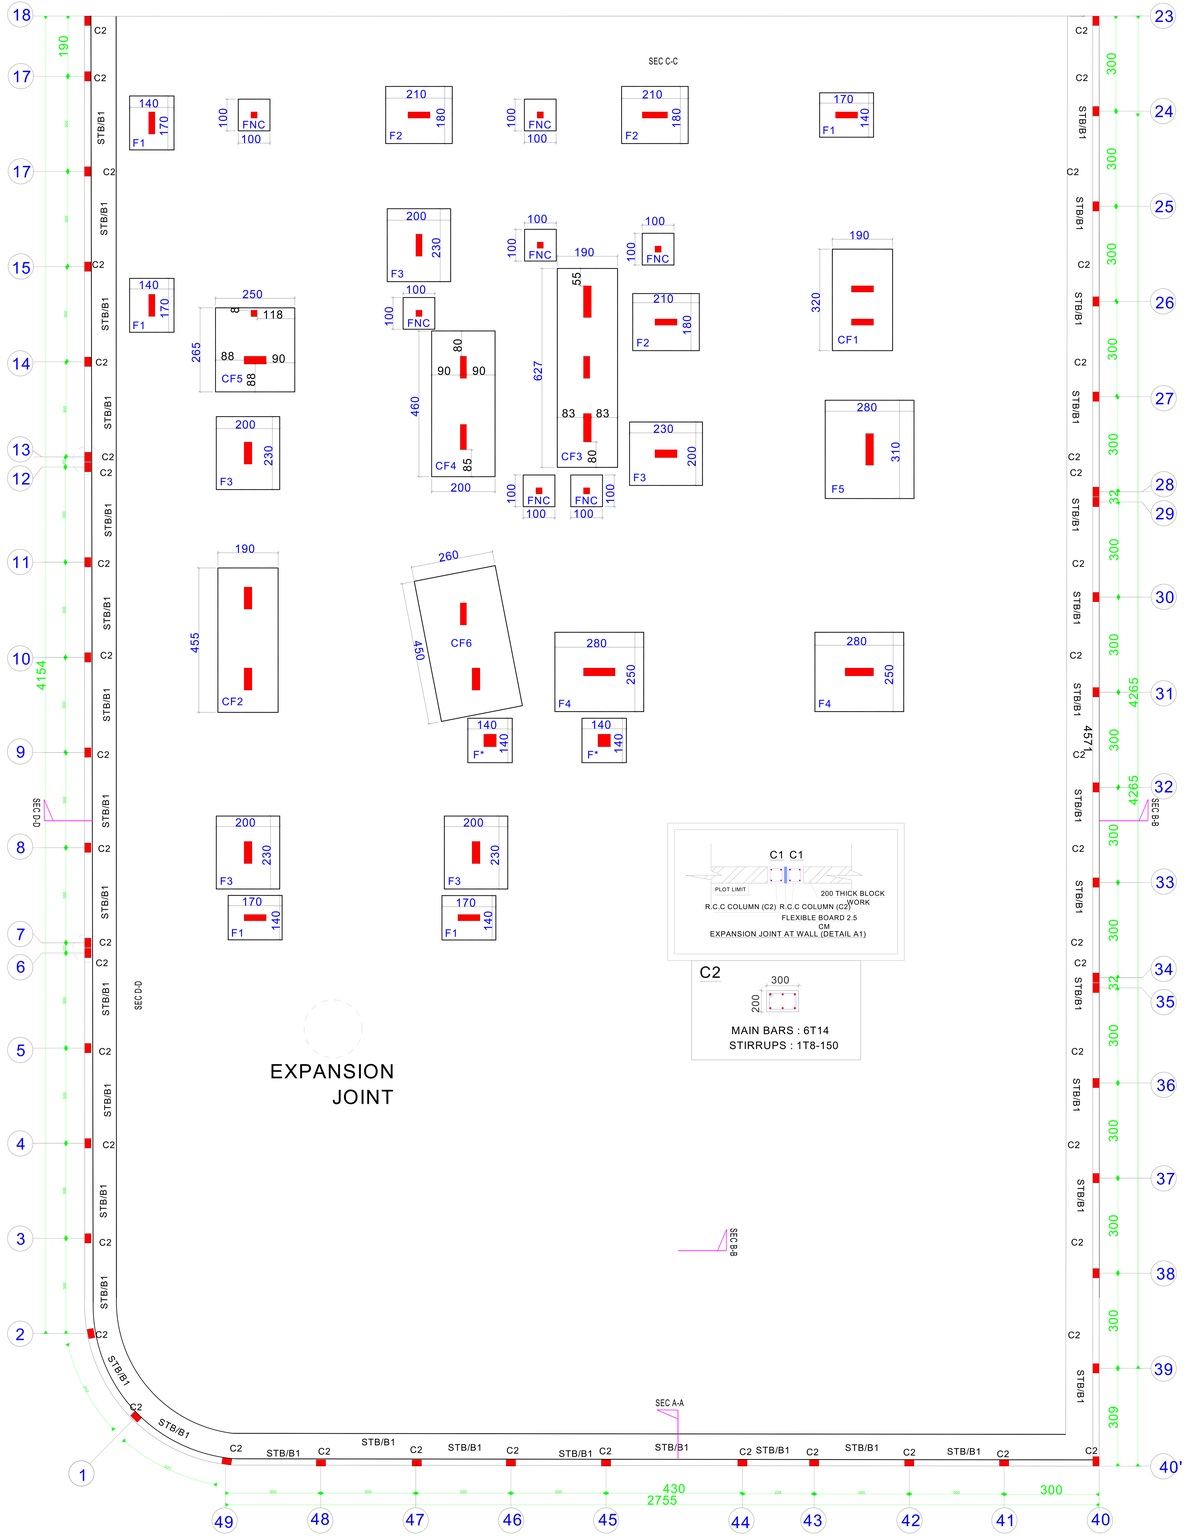

Govement Of Ras Al Khaimah
R.A.K. Municipality
Buildings Administration

حكومة رأس الخيمة
دائرة البلدية
إدارة المباني

Approved On — اعتمد في

27 January 2026

Building Permit #: PRMT-26-0000580

Approved By:

Savana
Engineering Consultancy & Interior Design

Client	ADEL ALI ALSHEHHI		
Project	DOUBLE STORY VILLA		
Drg.Title	COMPOUND WALL LAYOUT		
Area	SIEH AL URAIBI	Floortype	
Case ID.	3143538	Draw. Type.	STRC
Sec No.	1	Com. No.	
Block No.		Plot No.	208090106
Bldg. No.	FNC-26-000197	Floor No.	
Date	2026	Sht. No.	S13
Scale	1/100	Job No.	

G.Manager	Architect	Designed By
ENG AYMEN	ENG IMEN	ENG IMEN

COMPOUND WALL LAYOUT

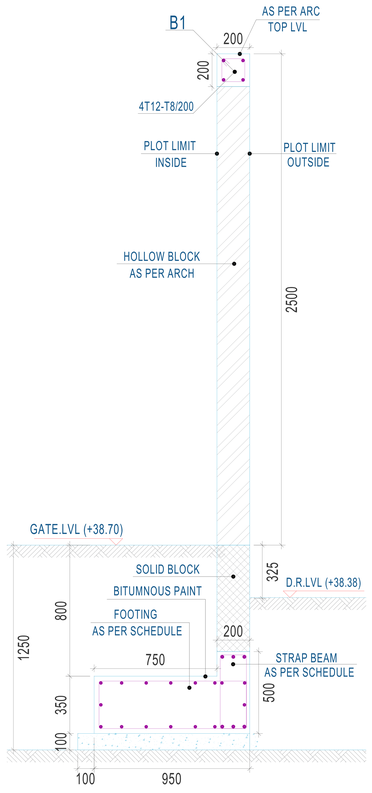

SEC (A-A)
SF1

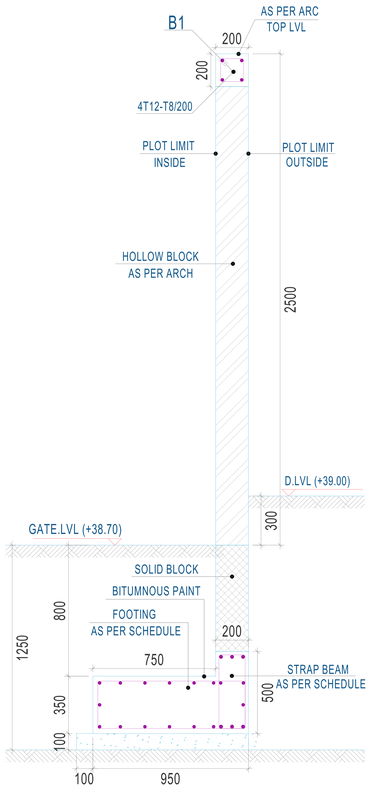

SEC (B-B)
SF1

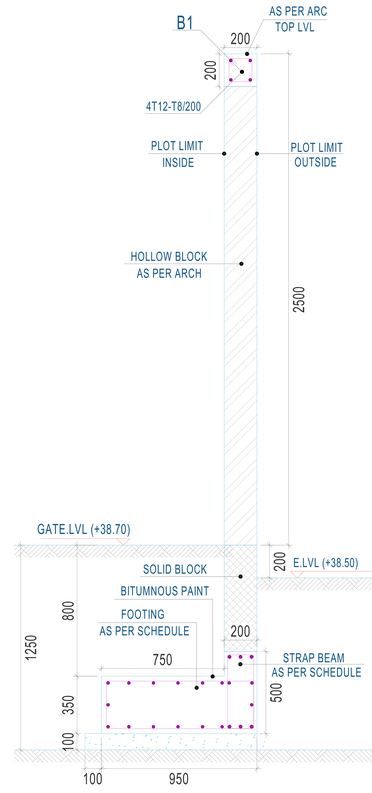

SEC (C-C)
SF1

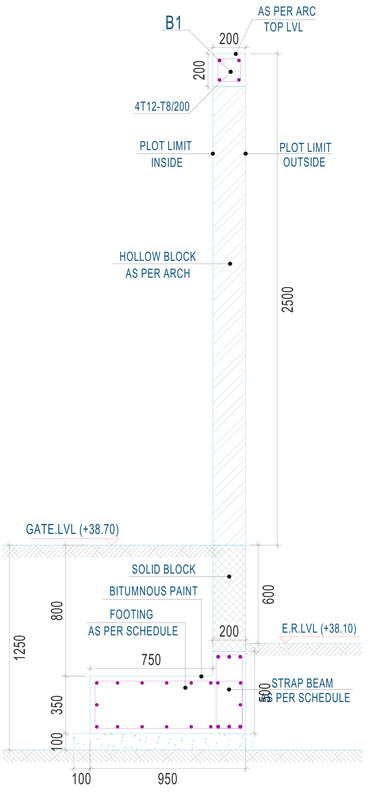

SEC (D-D)
SF1

SCHEDULE OF FOOTINGS

TYPE	SIZE			REINFORCEMENT DETAILS				REMARKS.
	WIDTH (mm)	LENGTH (mm)	DEPTH (mm)	BOTTOM MESH		TOP MESH		
				SHORT BAR	LONG BAR	SHORT BAR	LONG BAR	
SF1	AS PER LAYOUT		350	T12-150	T12-150	T12-150	T12-150	

SCHEDULE OF STB

TYPE	BEAM SIZE	BOTTOM REINFORCEMENT		TOP REINFORCEMENT			SIDE BARS O.E.F (F) EACH SIDE	STIRRUPS				NO OF LEGS	REMARKS
	MM X MM	STRAIGHT (A)	EXTRA @ MID SPAN(B)	STRAIGHT (C)	EXTRA @ CONT. SUPPORT (D)	EXTRA @ DISCONT. SUPPORT (E)		AT SUPPORT		AT MIDSPAN			
								OUTER (G1)	INNER (G2)	OUTER (H1)	INNER (H2)		
STB	200 X 500	3T14	--------	3T14	--------	--------	--------	T8-200	--------	T8-200	--------	2	

Govemment Of Ras Al Khaimah
R.A.K. Municipality
Buildings Administration

حكومة رأس الخيمة
دائرة البلدية
إدارة المباني

Approved On — اعتمد في

27 January 2026

Building Permit #: PRMT-26-0000580

Appoved By:

STRUCTURAL NOTES

ACI 318-11

F'C/FCU = 28/35 N/mm2

FY = 460N/mm2

FYt = 420N/mm2

CONCRETE COVERS :

Foundations cover = 75mm

Columns cover = 40mm

Walls cover = 30mm

Beams cover = 40mm

Slabs & Stairs cover = 25mm

LEGEND:

1) COLUMN / WALL TO BE CONTINUED

2) COLUMN / WALL TO BE TERMINATED

Savana
Engineering Consultancy & interior design

Client	ADEL ALI ALSHEHHI		
Project	DOUBLE STORY VILLA		
Drg.Title	COMPOUND WALL SCHEDULES		
Area	SIEH AL URAIBI	Floortype	
Case ID.	3143538	Draw. Type.	STRC
Sec No.	1	Com. No.	
Block No.		Plot No.	208090106
Bldg. No.	FNC-26-000197	Floor No.	
Date	2026	Sht. No.	S14
Scale	1/100	Job No.	

G.Manager	Architect	Designed By
ENG AYMEN	ENG IMEN	ENG IMEN

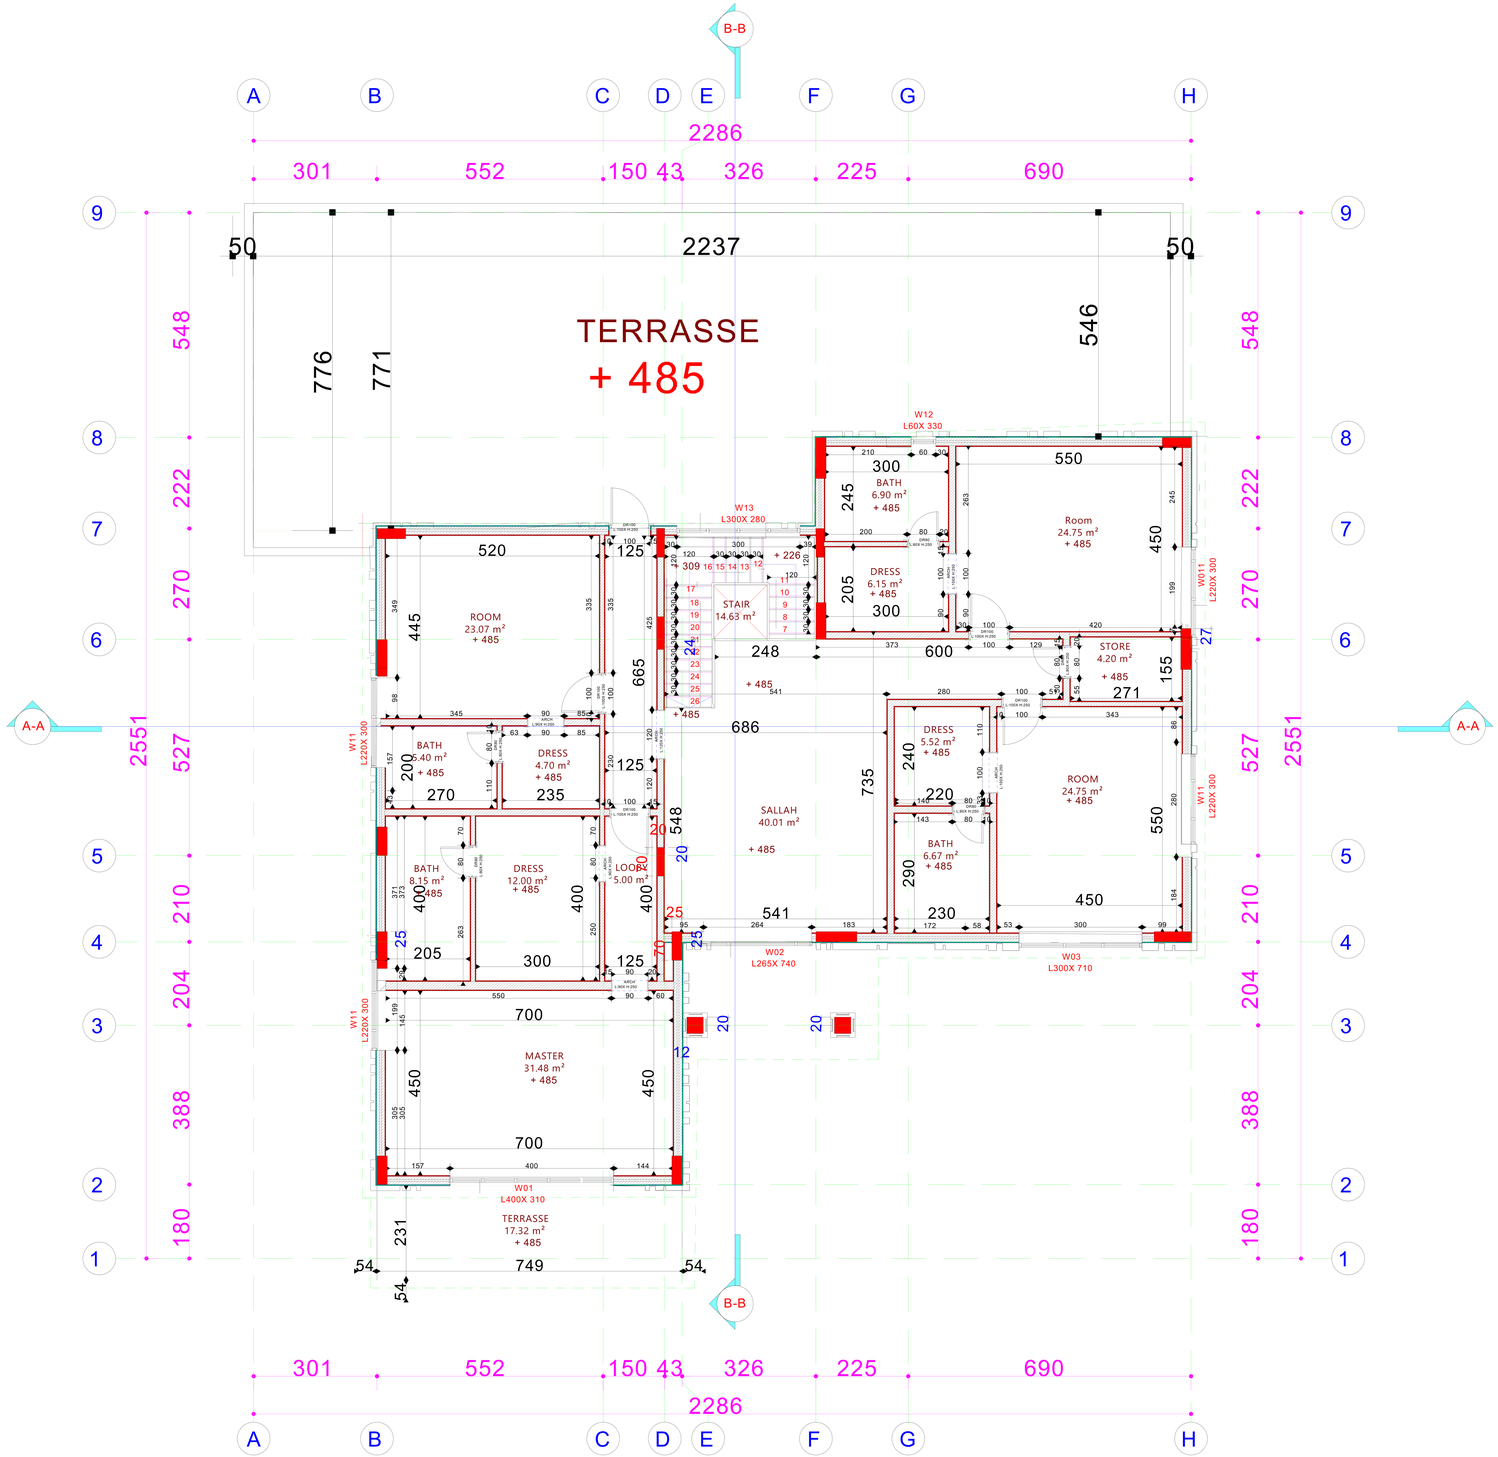

Govemment Of Ras Al Khaimah
R.A.K. Municipality
Buildings Administration

حكومة رأس الخيمة
دائرة البلدية
إدارة المباني

Approved On — اعتمد في

28 January 2026

Building Permit #: PRMT-26-0000580

Appoved By:

Note :-

* Rcc Lintels Must Be Made On Top Of All Doors , Arches And Windows All Of Them Are At Least 0.20 m Thick.
* All Blocks Adjacent To All Doors , Arches And Windows Must Be A Solid Block .

Rooms	Space	Number
Residential	272.63	
Commercial		
Industrial		
Goverment		
Resident.-Comm.		
Total		

Savana
Engineering Consultancy & interior design

Client	ADEL ALI ASHEHHI		
Project	DOUBLE STORY VILLA		
Drg.Title	FIRST FLOOR PLAN		
Area	SEIH AL URAIBI	Floortype	F
Case ID.	3143538	Draw. Type.	ARCH
Sec No.	1	Com. No.	
Block No.		Plot No.	208090106
Bldg. No.	BLD-25-02856	Floor No.	01
Date	2026	Sht. No.	A05
Scale	1/100	Job No.	

G.Manager	Architect	Designed By
ENG AYMEN	ENG IMEN	ENG OMAR

FIRST FLOOR PLAN