Govemment Of Ras Al Khaimah
R.A.K. Municipality
Buildings Administration

حكومة رأس الخيمة
دائـرة البلـدية
إدارة المباني

Approved On — اعتمد في

03 February 2026

Building Permit #: PRMT-26-0000720

Appoved By:

Ground Floor Area
BLD-25-02856

First Floor Area
BLD-25-02856

Area Statement	
Building Number	BLD-25-02856
Ground Floor Area	440.19
First Floor Area	272.63.m²
Total Building Area	712.82m²
PLOT AREA ACCORDING TO KRUKI	1457.29 m²
BUILD UP RATIO	32

Savana
Engineering Consultancy & interior design

Client	ADEL ALI ASHEHHI		
Project	DOUBLE STORY VILLA		
Drg.Title	AreaStatement		
Area	SEIH AL URAIBI	Floortype	
Case ID.	3159426	Draw. Type.	ARCH
Sec No.	1	Com. No.	
Block No.		Plot No.	208090106
Bldg. No.	BLD-25-02856	Floor No.	
Date	2026	Sht. No.	A-01
Scale	1/100	Job No.	

G.Manager	Architect	Designed By
ENG AYMEN	ENG IMEN	ENG AHMED

AREA STATMENTENT

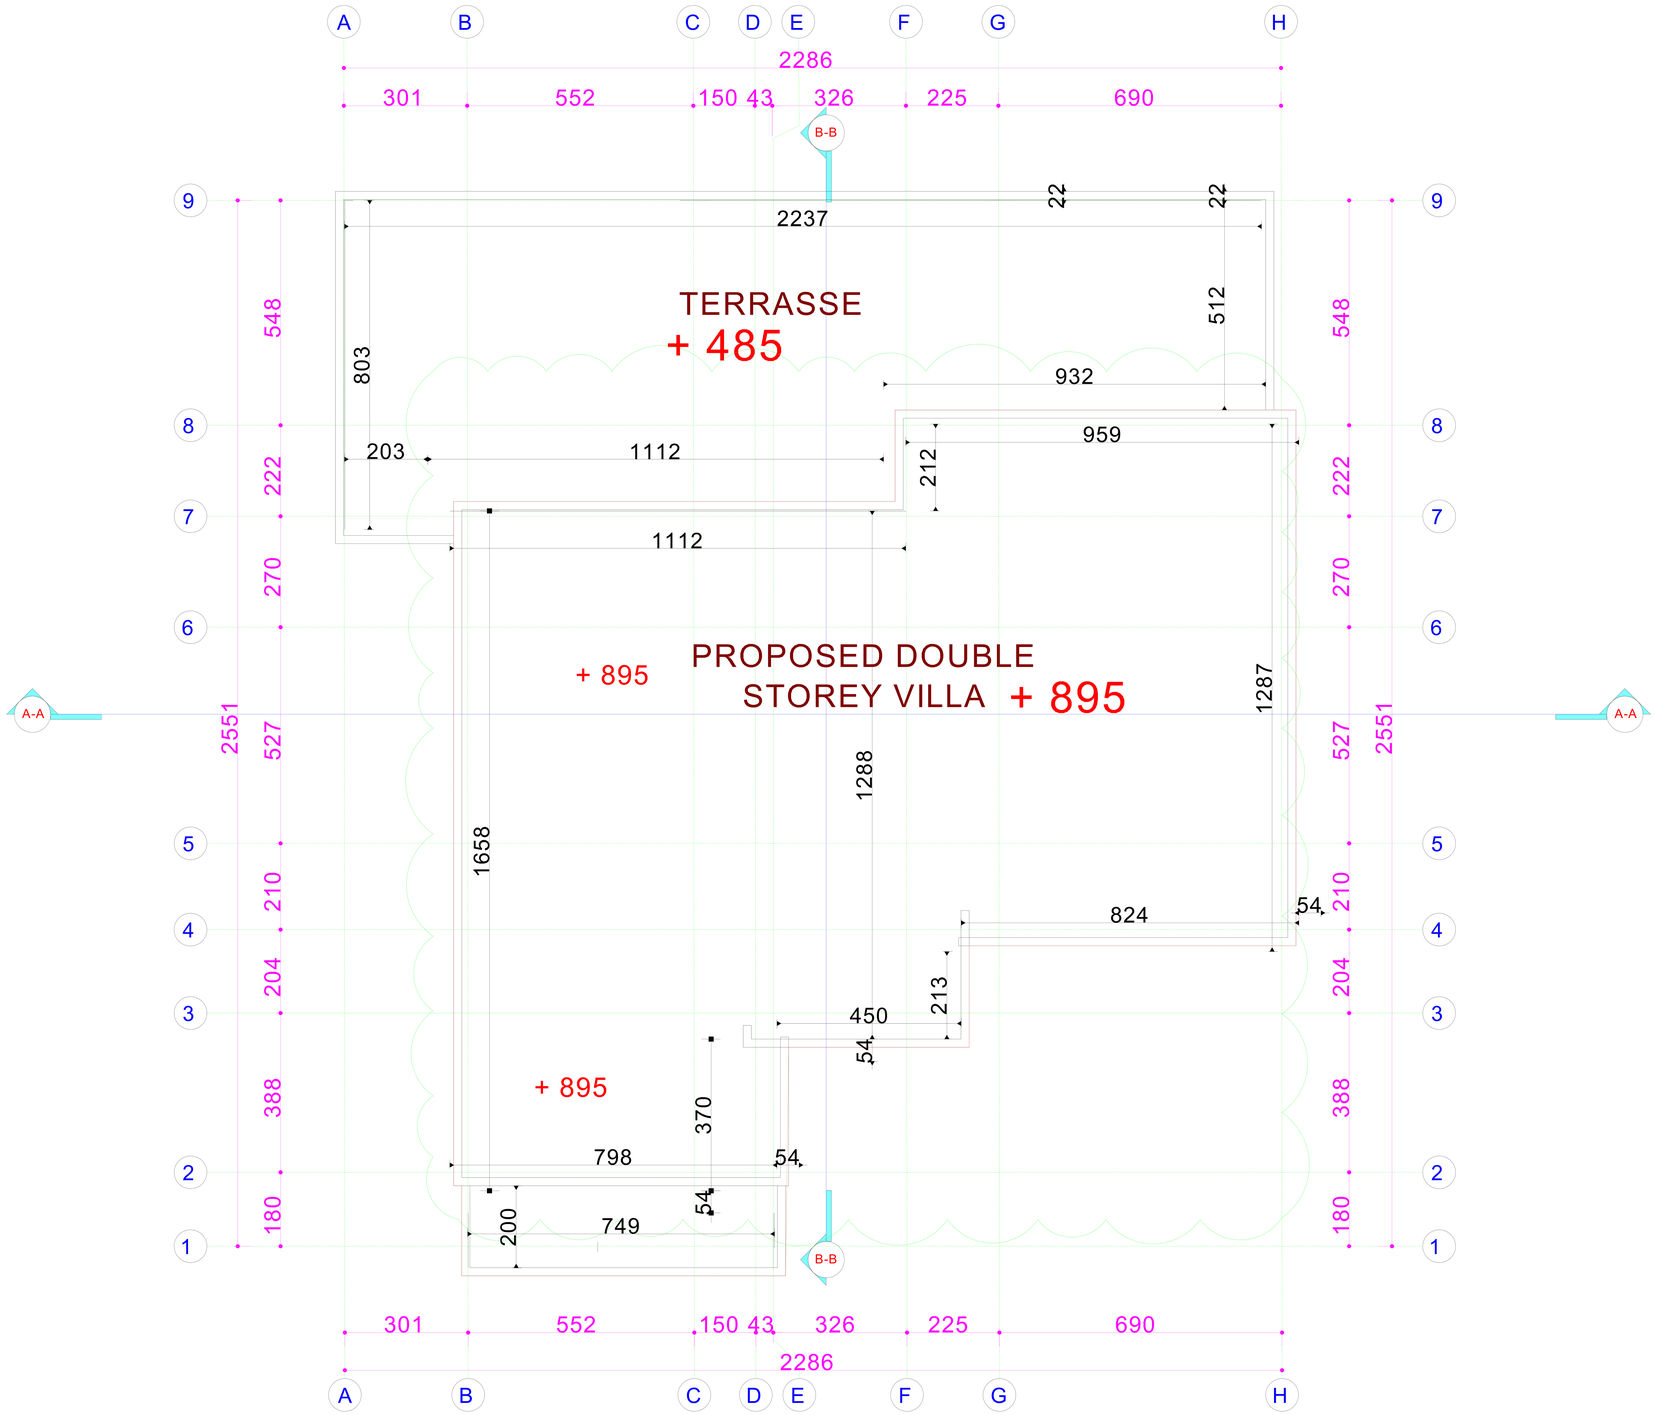

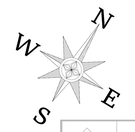

FINISHING FOR VERANDAH		FINISHING FOR DRESSING AREA		FINISHING FOR BATH,WC & WASH	
C3	W3	C1	W1	C2	W2
S2	F3	S1	F1	S2	F2

FLOORING	F1 Ceramic glazed tiles	F2 Ceramic Tiles (Non Slippery)	F3 Marble Tiles
WALLS	W1 Acrylic emulsion paint	W2 Ceramic tiles up to ceiling	W3 Epoxy paint.
SKIRTING	S1 Ceramic Tiles. 10cm hight	S2 Marble tiles 10cm hight	
CEILING	C1 Acrylic emulsion paint	C2 Oil Paint.	C3 Epoxy paint.

Govemment Of Ras Al Khaimah
R.A.K. Municipality
Buildings Administration

حكومة رأس الخيمة
دائرة البلدية
إدارة المباني

Approved On — اعتمد في

03 February 2026

Building Permit #: PRMT-26-0000720

Appoved By:

Savana
Engineering Consultancy & interior design

Client	ADEL ALI ASHEHHI		
Project	DOUBLE STORY VILLA		
Drg.Title	TOP ROOF PLAN		
Area	SEIH AL URAIBI	Floortype	
Case ID.	3159426	Draw. Type.	ARCH
Sec No.	1	Com. No.	
Block No.		Plot No.	208090106
Bldg. No.	BLD-25-02856	Floor No.	
Date	2026	Sht. No.	A06A
Scale	1/100	Job No.	

G.Manager	Architect	Designed By
ENG AYMEN	ENG IMEN	ENG AHMED

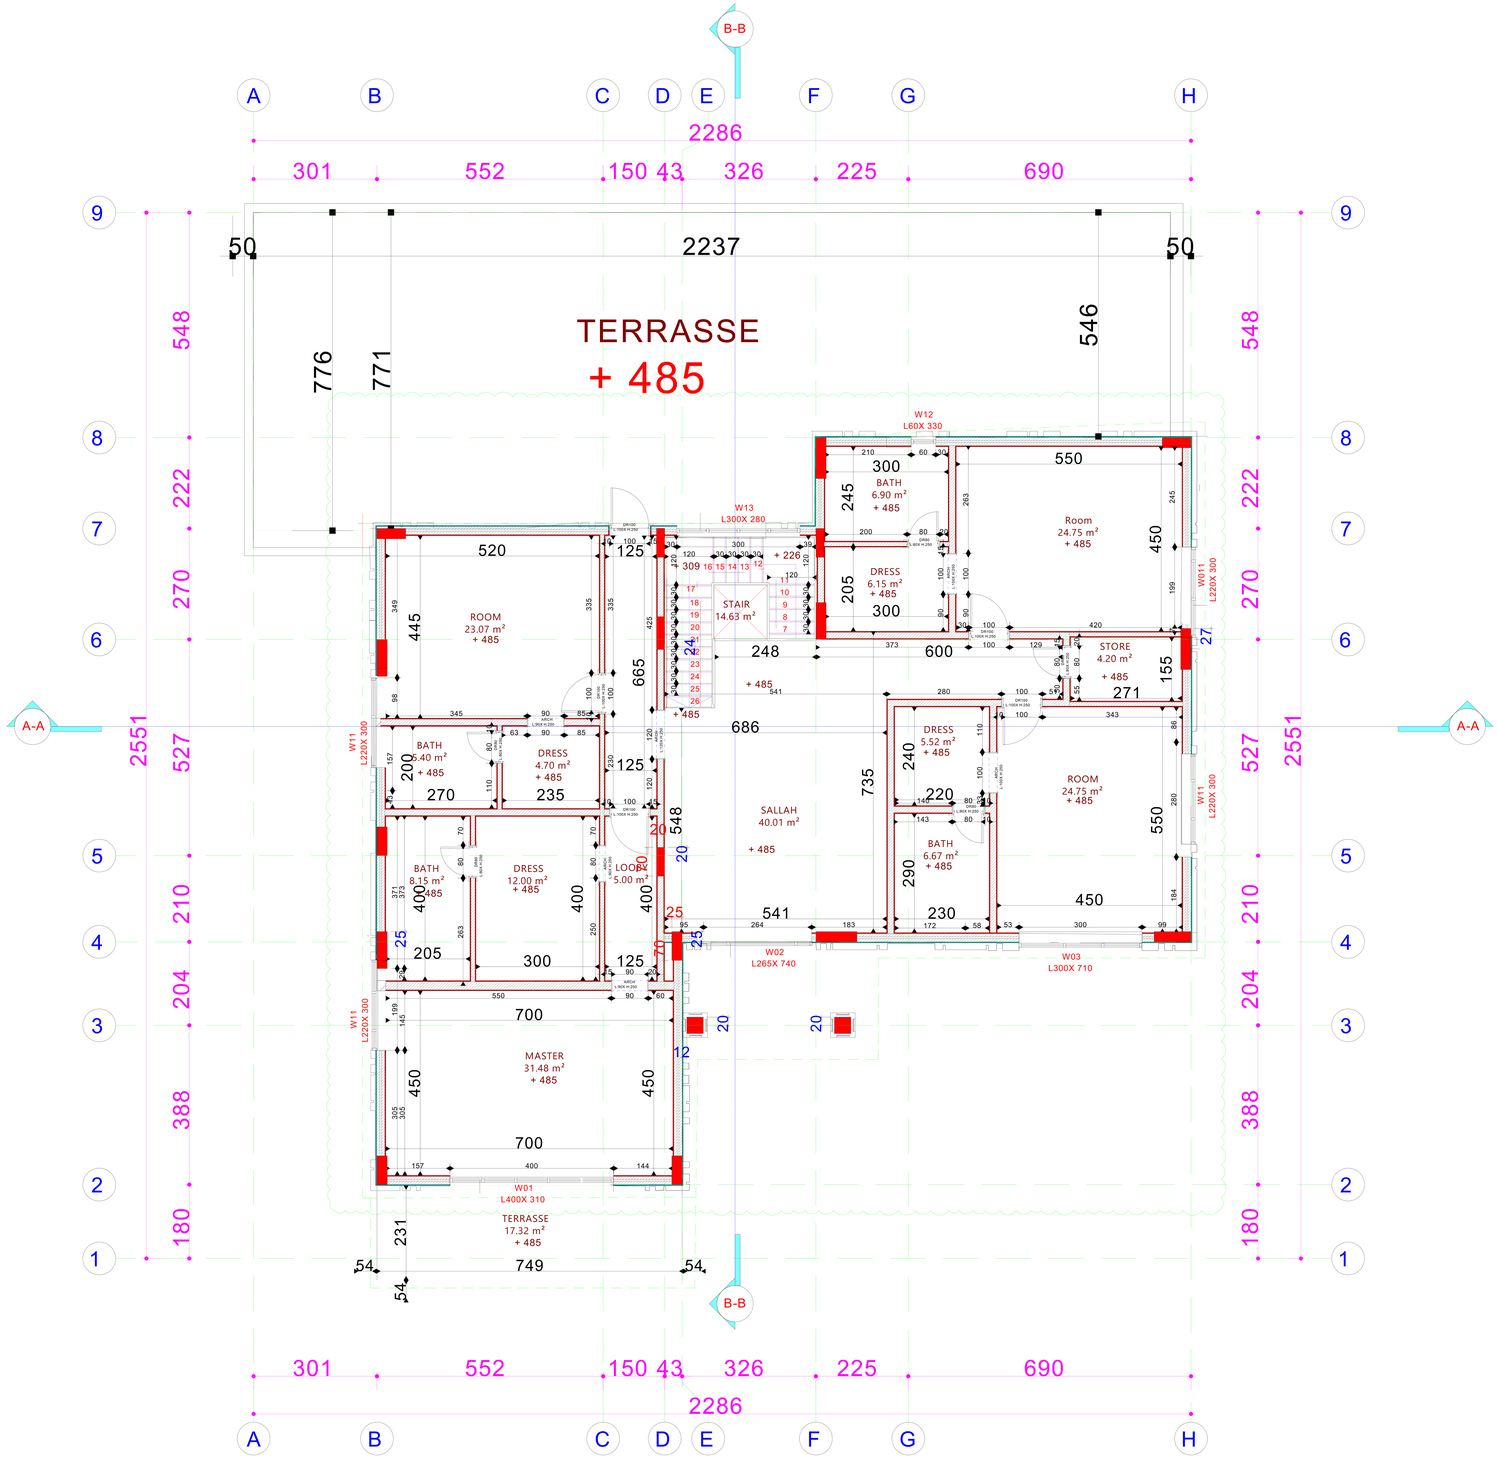

Govemment Of Ras Al Khaimah
R.A.K. Municipality
Buildings Administration

حكومة رأس الخيمة
دائرة البلدية
إدارة المباني

Approved On — اعتمد في

03 February 2026

Building Permit #: PRMT-26-0000720

Appoved By:

Note :-

* Rcc Lintels Must Be Made On Top Of All Doors , Arches And Windows All Of Them Are At Least 0.20 m Thick.
* All Blocks Adjacent To All Doors , Arches And Windows Must Be A Solid Block .

Rooms	Space	Number
Residential	272.63	
Commercial		
Industrial		
Goverment		
Resident.-Comm.		
Total		

Savana
Engineering Consultancy & interior design

Client	ADEL ALI ASHEHHI		
Project	DOUBLE STORY VILLA		
Drg.Title	FIRST FLOOR PLAN		
Area	SEIH AL URAIBI	Floortype	F
Case ID.	3159426	Draw. Type.	ARCH
Sec No.	1	Com. No.	
Block No.		Plot No.	208090106
Bldg. No.	BLD-25-02856	Floor No.	01
Date	2026	Sht. No.	A05
Scale	1/100	Job No.	

G.Manager	Architect	Designed By
ENG AYMEN	ENG IMEN	ENG AHMED

FIRST FLOOR PLAN