REAR

NEIGHBOR 406131921

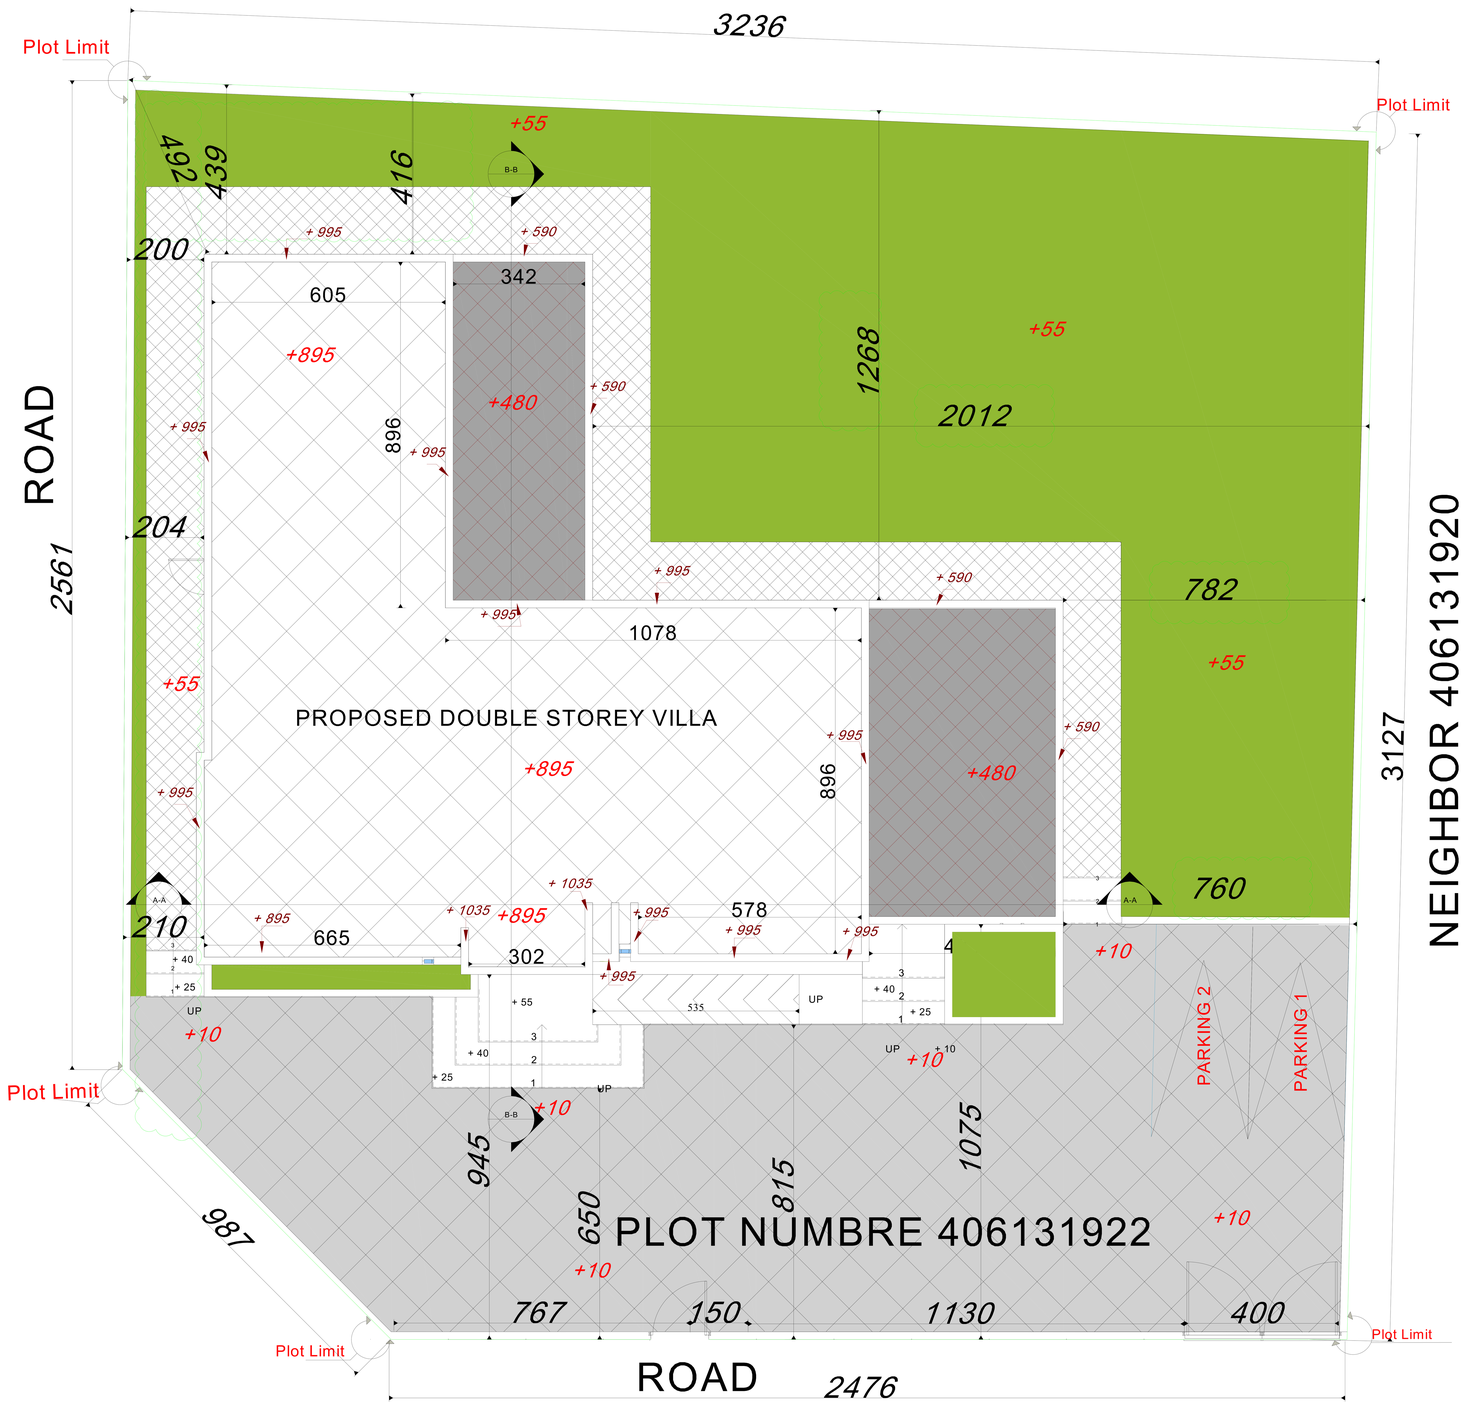

N
W E
S

Govemment Of Ras Al Khaimah
R.A.K. Municipality
Buildings Administration

حكومة رأس الخيمة
دائـرة البلـدية
إدارة المباني

Approved On — اعتمد في

24 December 2024

Building Permit #: PRMT-24-0004326

Appoved By:

Note :-

* Rcc Lintels Must Be Made On Top Of All Doors , Arches And Windows All Of Them Are At Least 0.20 m Thick.
* All Blocks Adjacent To All Doors , Arches And Windows Must Be A Solid Block .

Savana
Engineering Consultancy & interior design

Client	KHALED ALI SAEED BEN SHUOOM AL SHEHHI		
Project	Proposed Double Storey Villa		
Drg.Title	Site Development Layout Plan		
Area	AWAFI	Floortype	
Case ID.	2712017	Draw. Type.	ARCH
Sec No.	1	Com. No.	
Block No.		Plot No.	406131922
Bldg. No.	BLD-24-04245	Floor No.	
Date	DEC 2024	Sht. No.	A02
Scale	1/100	Job No.	

G.Manager	Architect	Designed By
ENG AYMEN	ENG IMEN	ENG IMEN

SITE DEVELOPMENT LAYOUT PLAN

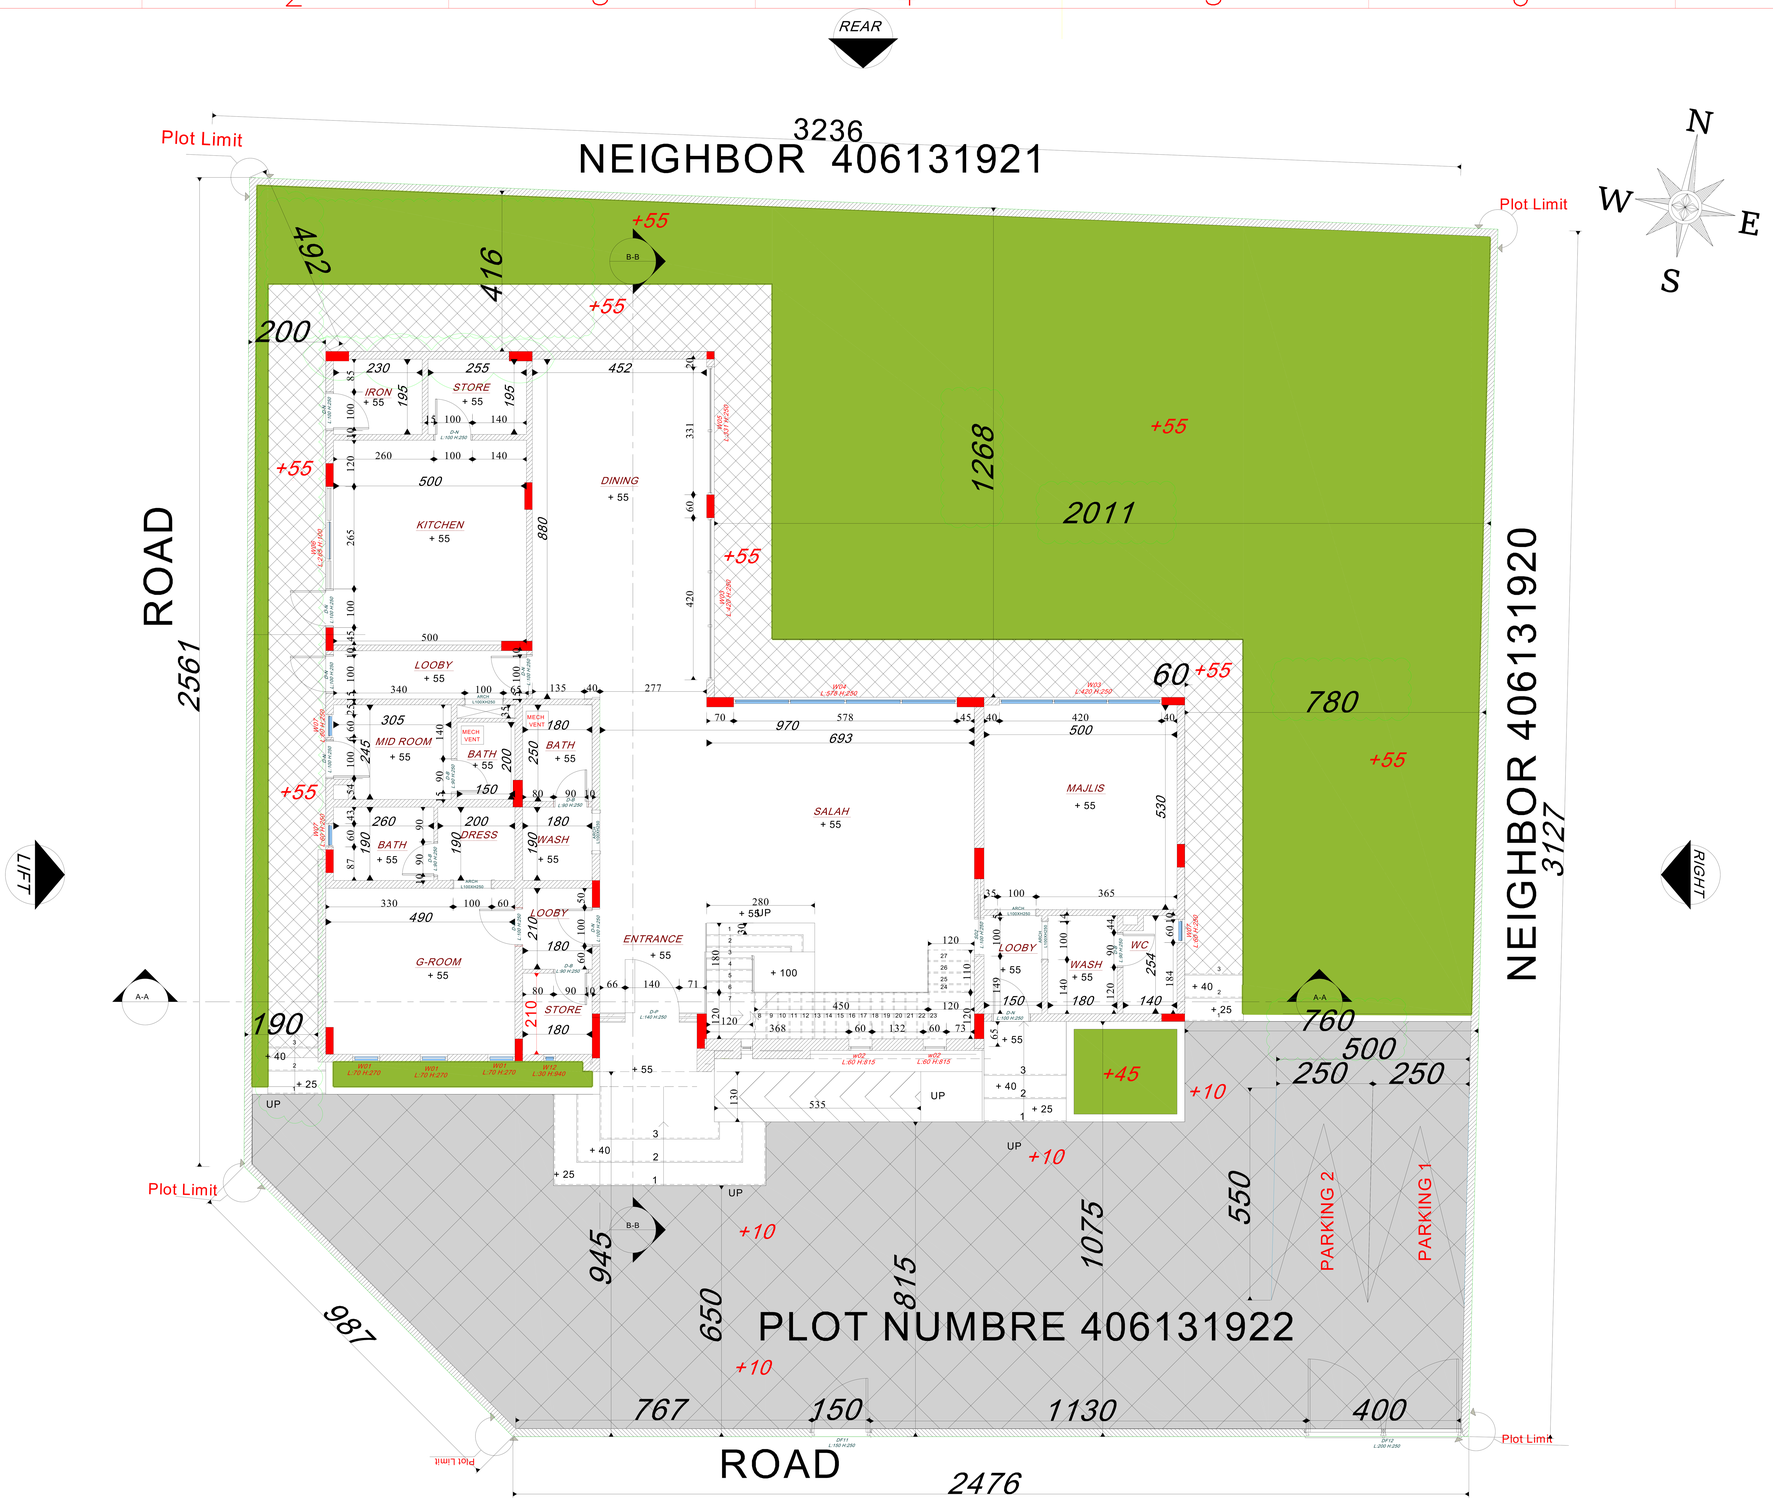

Govvernment Of Ras Al Khaimah
R.A.K. Municipality
Buildings Administration

حكومة رأس الخيمة
دائرة البلدية
إدارة المباني

Approved On — اعتمد في

24 December 2024

Building Permit #: PRMT-24-0004326

Appoved By:

Savana
Engineering Consultancy & interior design

Client	KHALED ALI SAEED BEN SHUOOM AL SHEHHI		
Project	Proposed Double Storey Villa		
Drg.Title	SITE SETTING PLAN		
Area	AWAFI	Floortype	
Case ID.	2712017	Draw. Type.	ARCH
Sec No.	1	Com. No.	
Block No.		Plot No.	406131922
Bldg. No.	BLD-24-04245	Floor No.	
Date	DEC-2024	Sht. No.	A03
Scale	1/100	Job No.	

G.Manager	Architect	Designed By
ENG AYMEN	ENG IMEN	ENG IMEN

SITE SETTING PLAN