



حكومة رأس الخيمة
Government of Ras Al Khaimah

المخطط الموقفي / ملك



بلدية رأس الخيمة
إدارة التخطيط والمساحة
Ras Al Khaimah Municipality
Town Planning and Survey
Administration

المالك : محمد احمد منصور ري

الاشتراطات التخطيطية

نسبة البناء	عدد الطوابق	مستوى الرصف : NA
الشمس	الجنوب	الشرق
الشمس	الجنوب	الشرق
الشمس	الجنوب	الشرق

ملاحظات : المشتريات : بناء قلم ، القسيمة مقبولة
تغير بعدم المطالبة بقي قسيمة أخرى بتاريخ 30/12/2012 ، تم التحديد بموجب الكف الصان من دائرة الأراضي رقم 9/2010

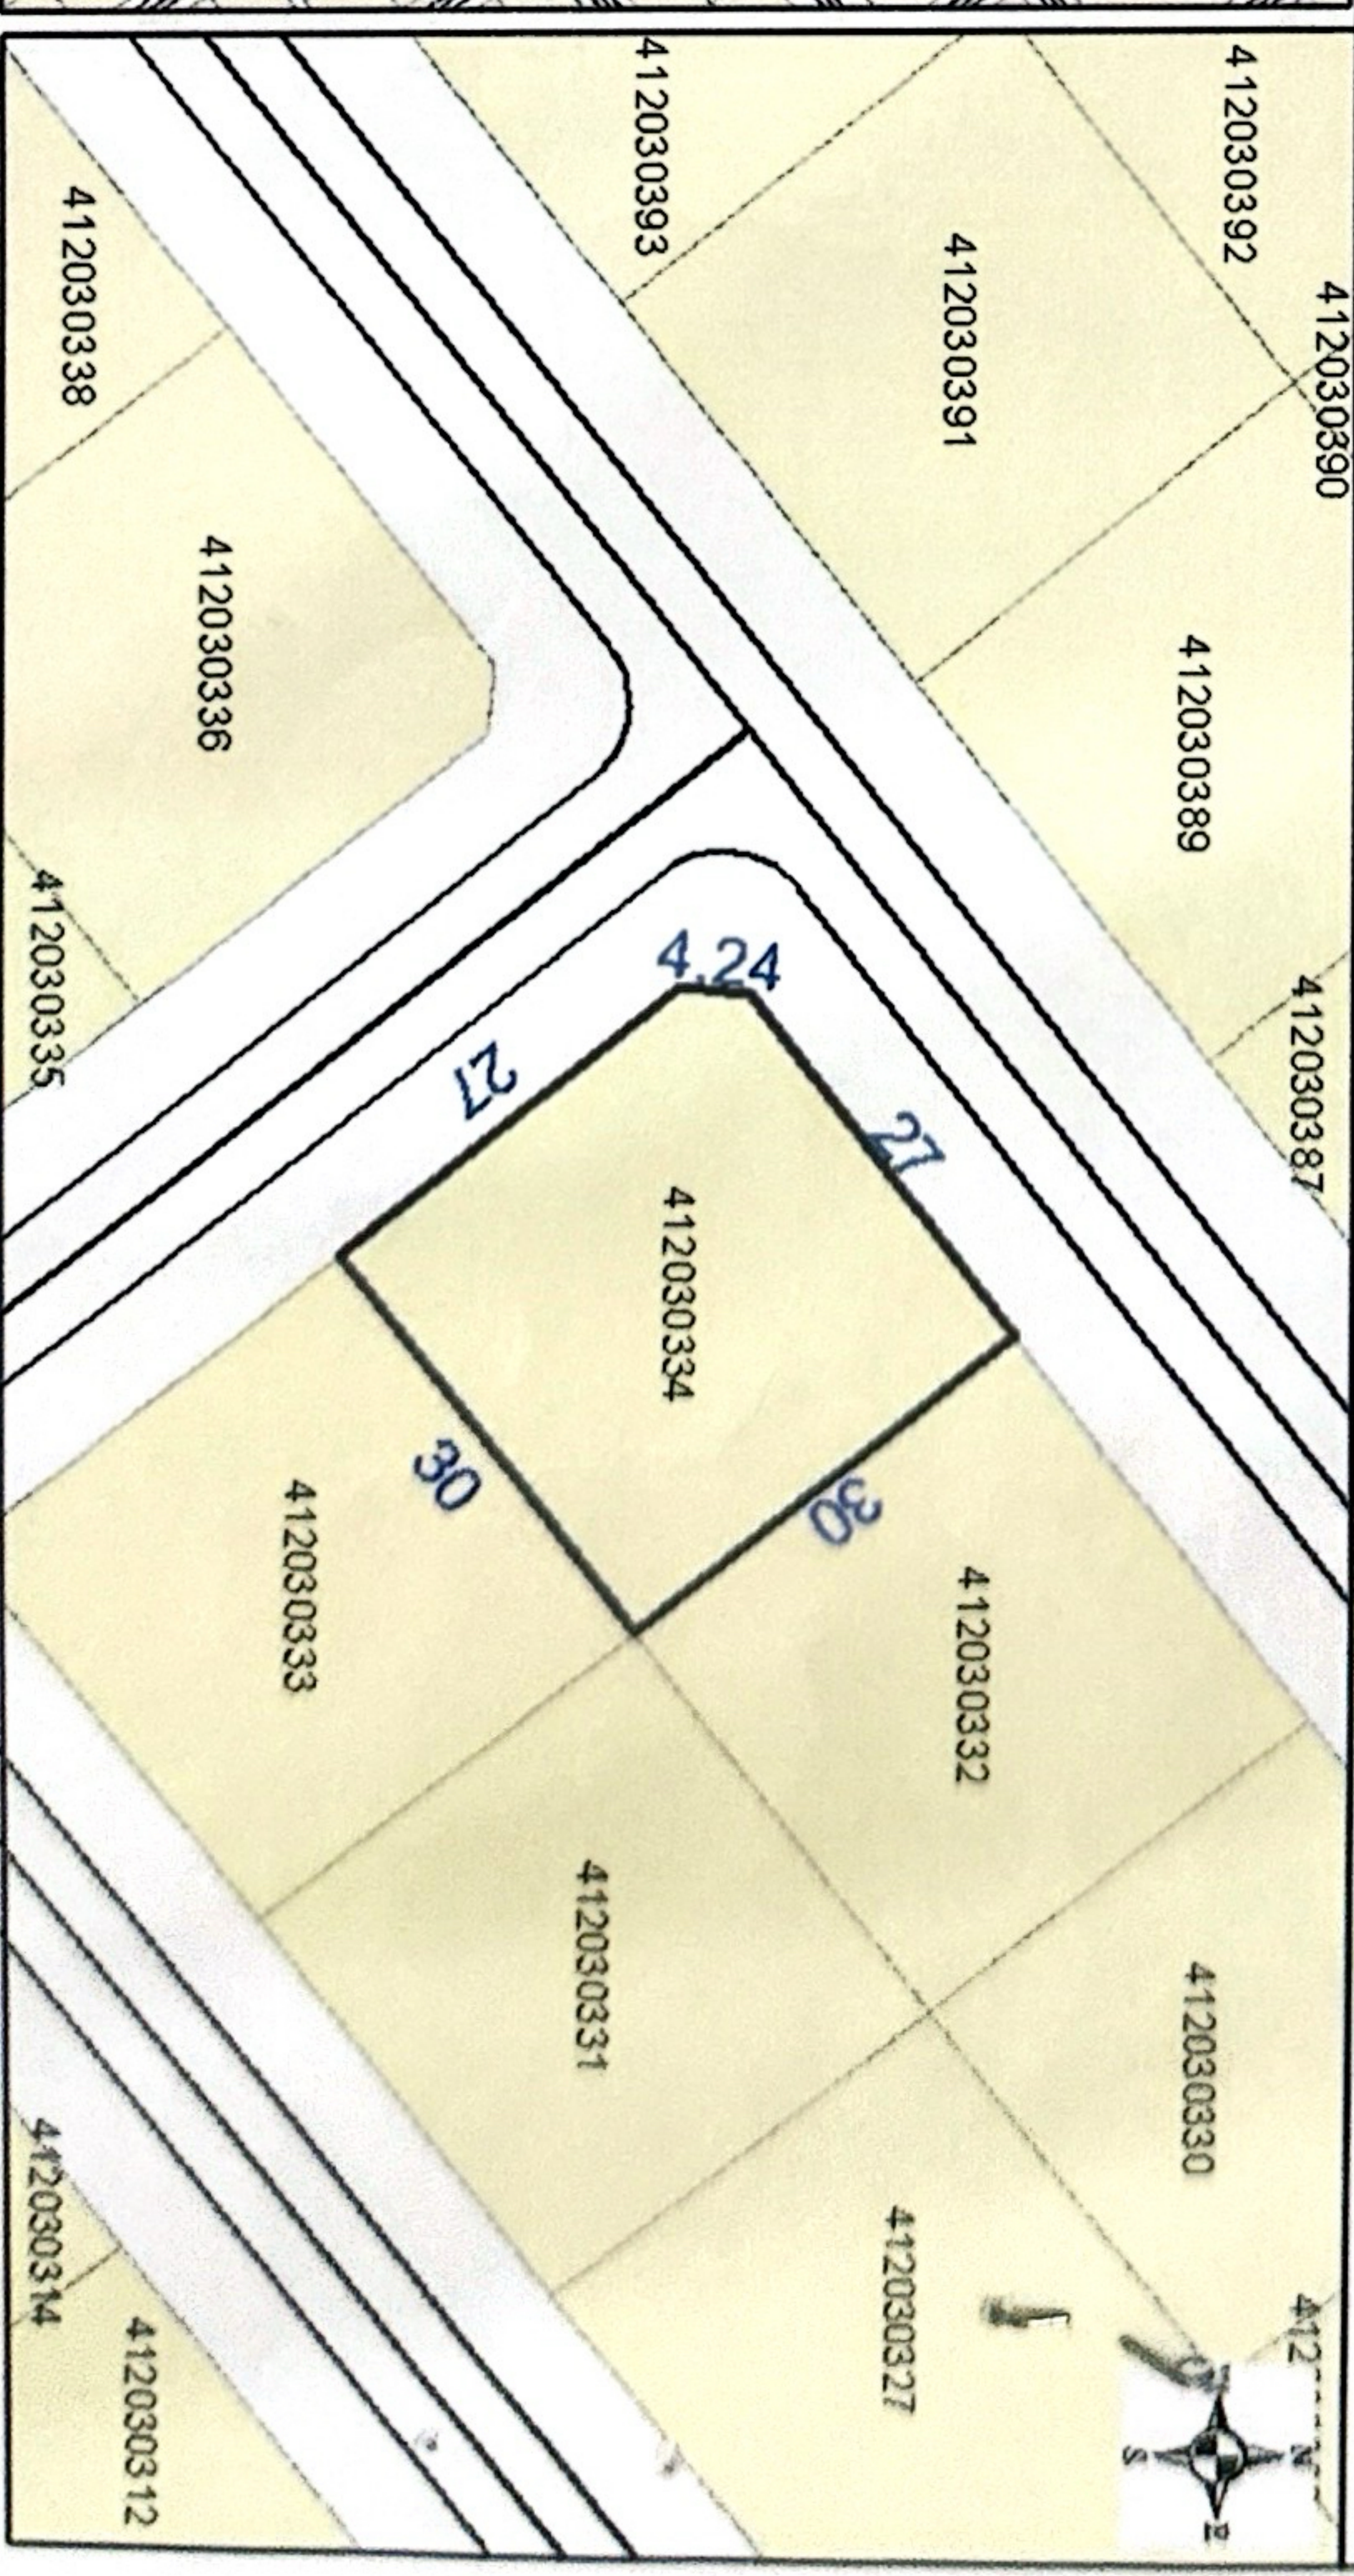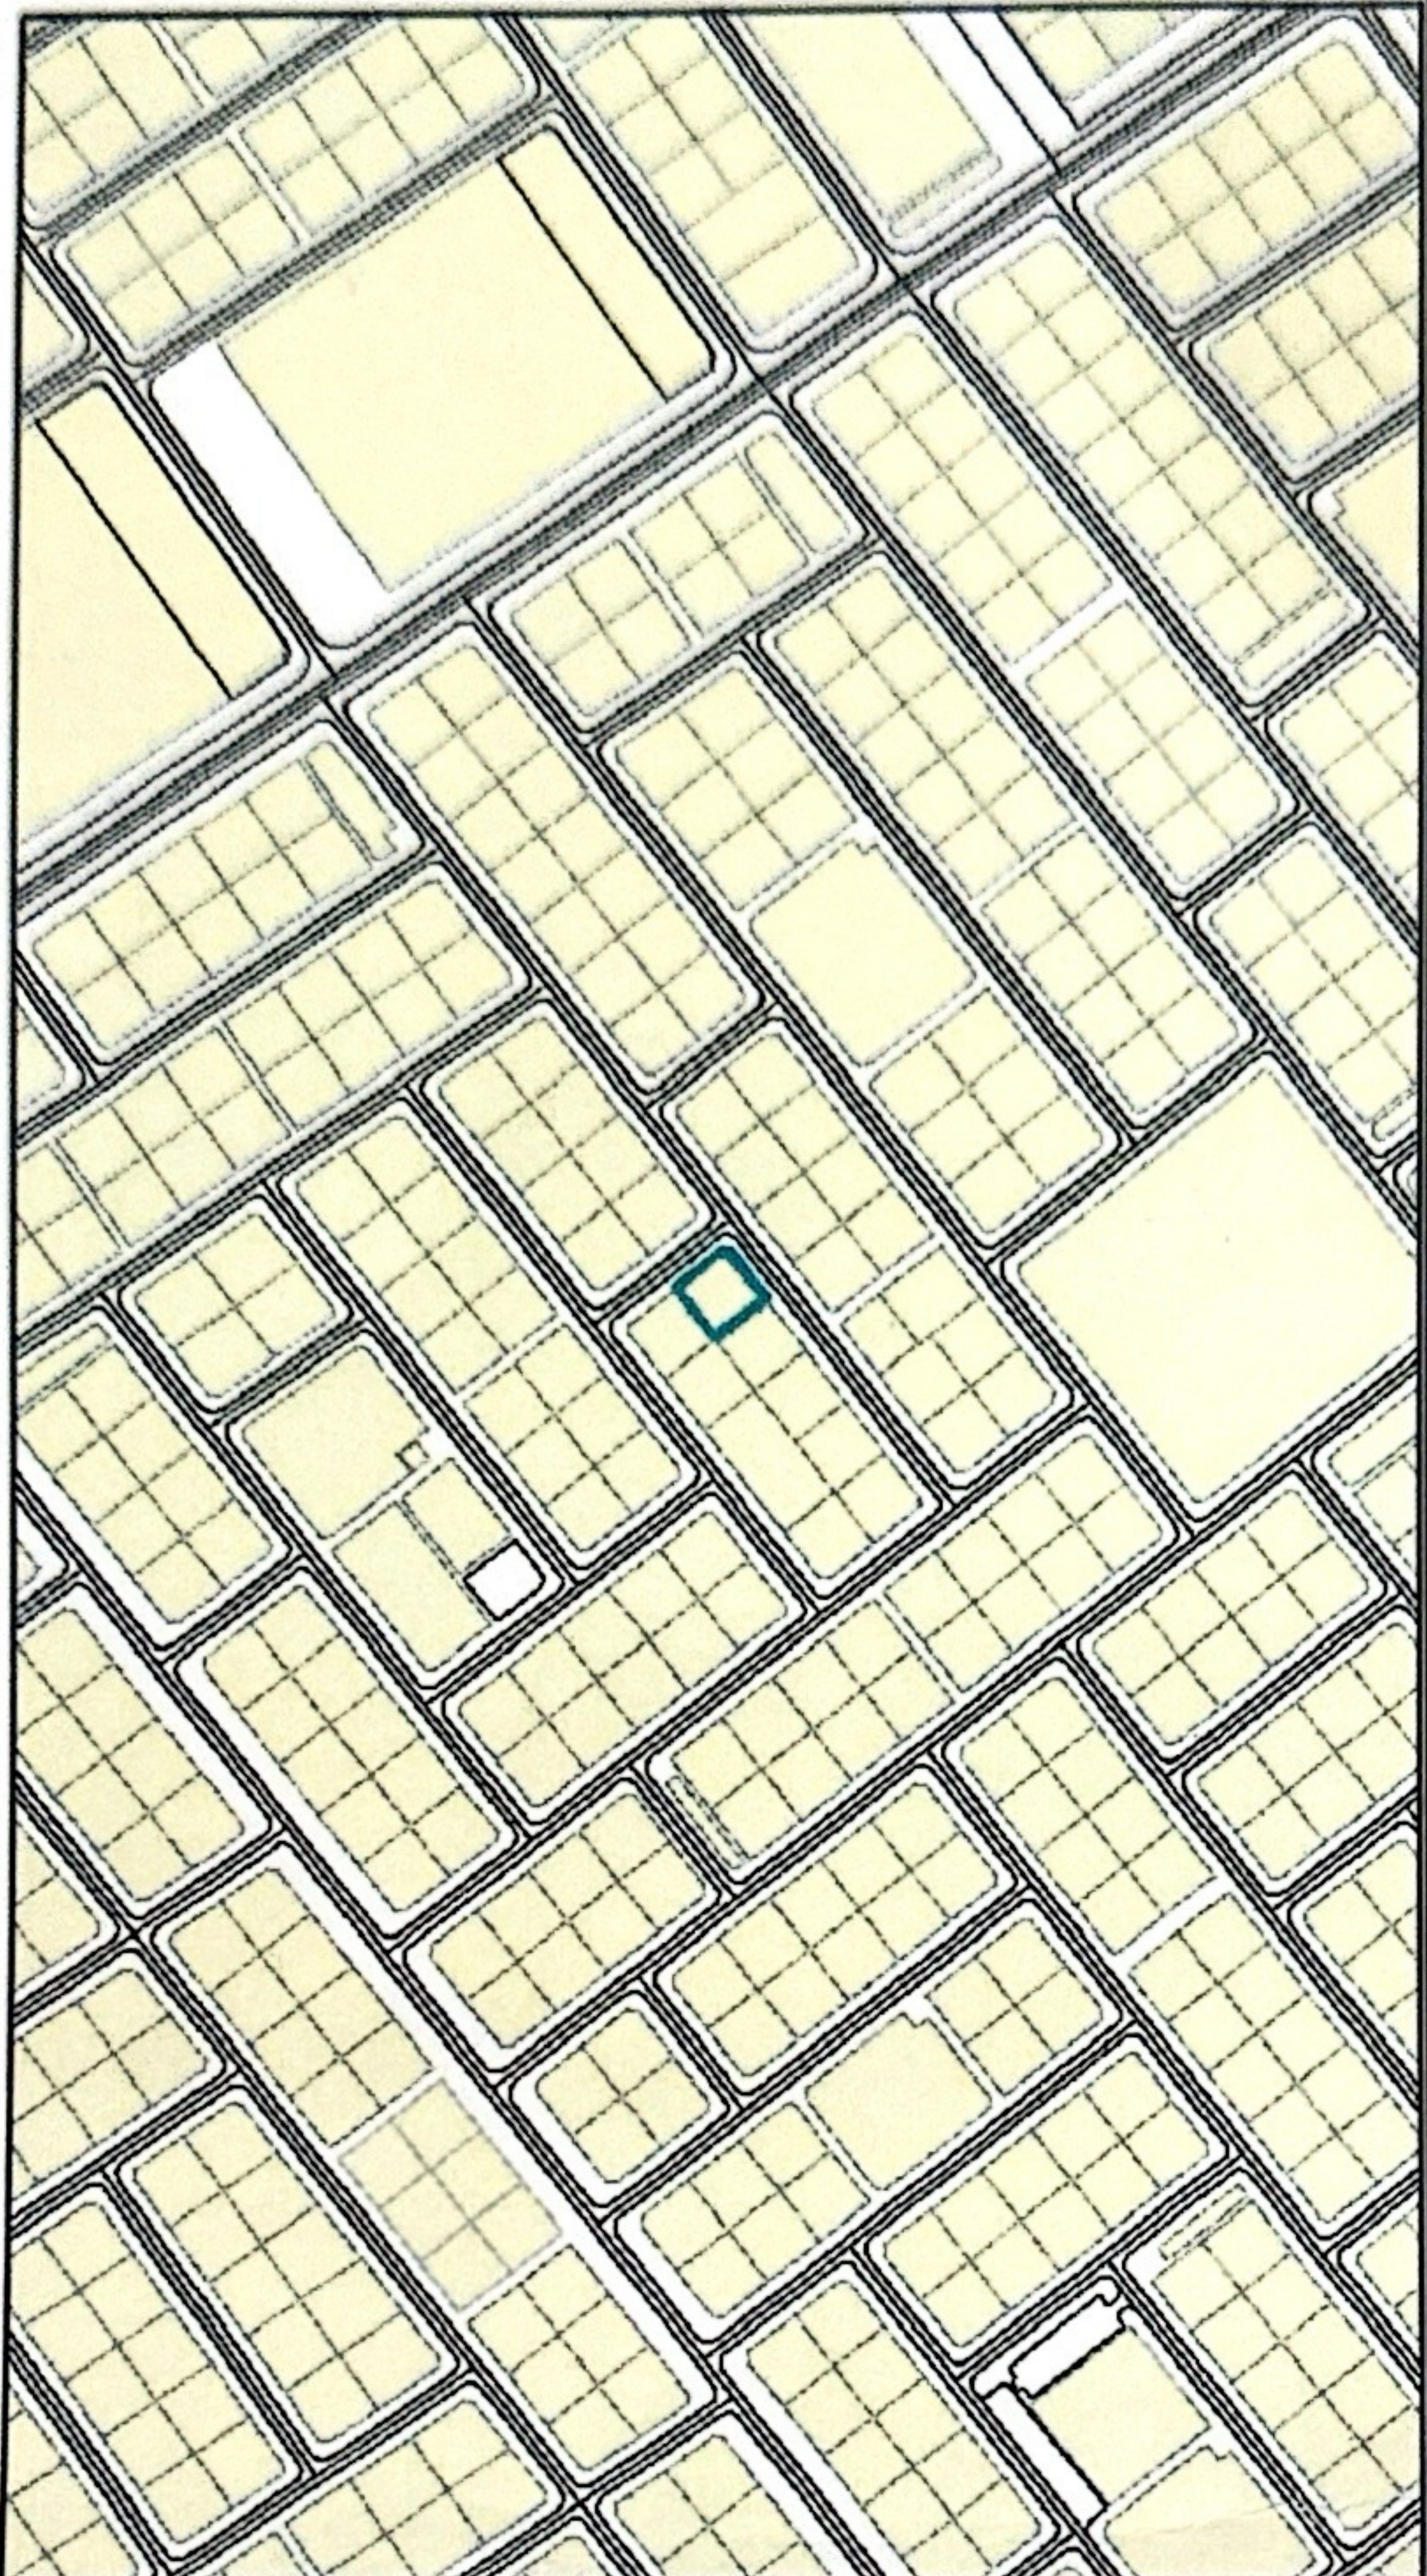


الإدارة

بلدية رأس الخيمة

الإدارة

المسح على تخطيط بلدية رأس الخيمة للمساحة والمسح والإستثمار

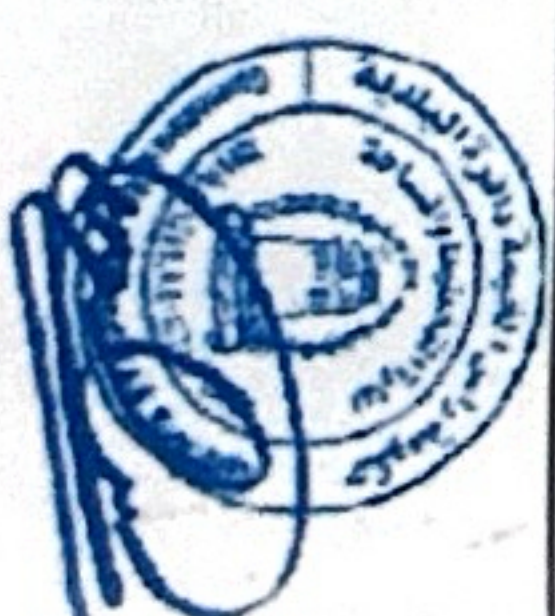

إعتماد مدير
إدارة التخطيط والمساحة

مدير التخطيط
مساحة ومسح البلدية
مساحة ومسح البلدية
مساحة ومسح البلدية