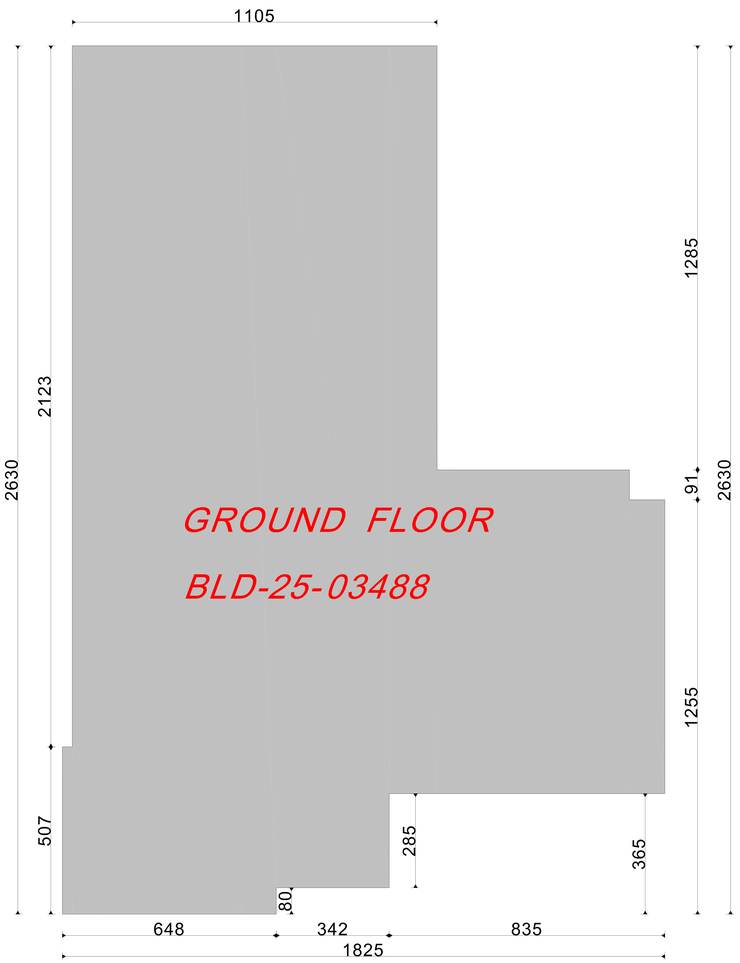

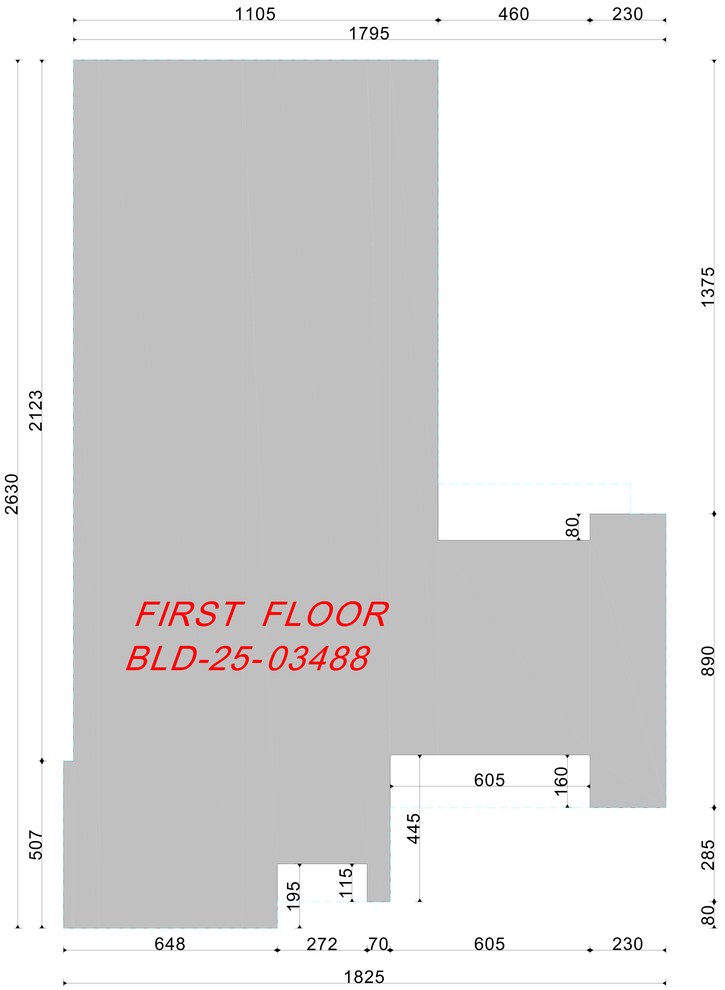

Govemment Of Ras Al Khaimah
R.A.K. Municipality
Buildings Administration

حكومة رأس الخيمة
دائرة البلدية
إدارة المباني

Approved On — اعتمد في

08 September 2025

Building Permit #:

Appoved By:

Area Statement	
Building Number	BLD-25-03488
Ground Floor Area	350.8 m²
First Floor Area	350.8m²
ROOF Floor Area	35.6m²
Total Building Area	737.2m²
PLOT AREA ACCORDING TO KRUKI	900m²
BUILD UP RATIO	38.9%

Savana
Engineering Consultancy & interior design

Client	FAHAD SULAIMAN ABDULLA ALSHEHI		
Project	DOUBLE STORY VILLA		
Drg.Title	AreaStatement		
Area	SHEIKH ZAYED	Floortype	
Case ID.	2956391	Draw. Type.	ARCH
Sec No.	1	Com. No.	
Block No.		Plot No.	412030315
Bldg. No.	BLD-25-03488	Floor No.	
Date	07/2025	Sht. No.	A-01
Scale	1/100	Job No.	

G.Manager	Architect	Designed By
ENG AYMEN	ENG IMEN	ENG IMEN

AREA STATMENTENT

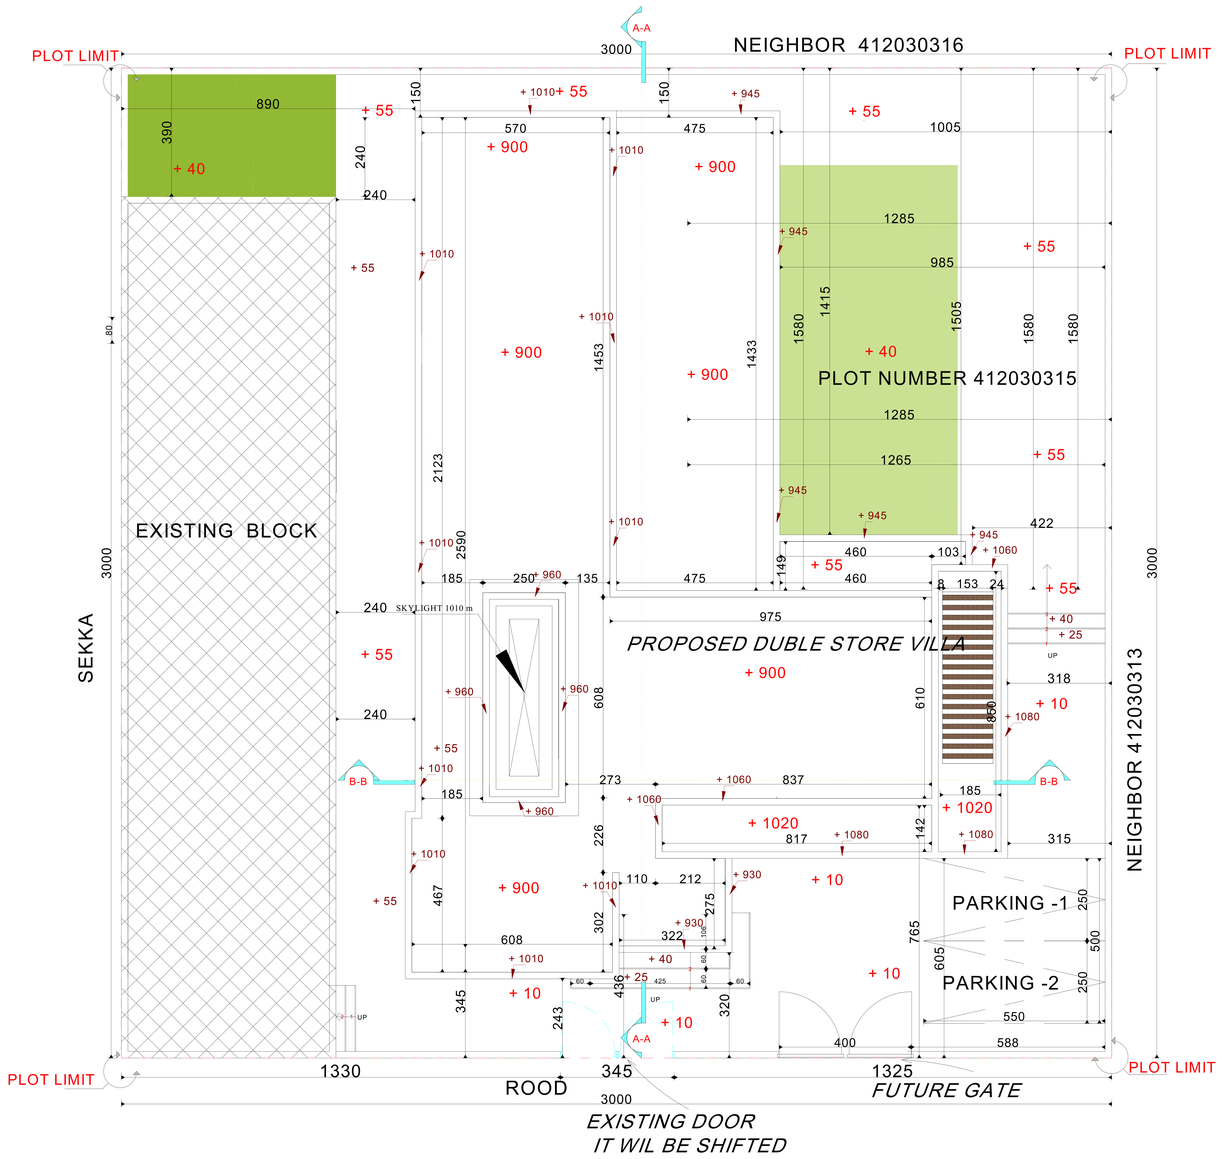

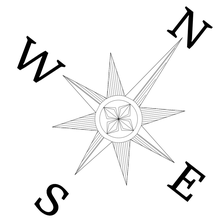

Govement Of Ras Al Khaimah
R.A.K. Municipality
Buildings Administration

حكومة رأس الخيمة
دائـرة البلـدية
إدارة المباني

Approved On — اعتمد في

08 September 2025

Building Permit #:

Appoved By:

Note :-

* Rcc Lintels Must Be Made On Top Of All Doors , Arches And Windows All Of Them Are At Least 0.20 m Thick.
* All Blocks Adjacent To All Doors , Arches And Windows Must Be A Solid Block .

Savana
Engineering Consultancy & interior design

Client	FAHAD SULAIMAN ABDULLA ALSHEHI		
Project	DOUBLE STORY VILLA		
Drg.Title	Site Development Layout Plan		
Area	SHEIKH ZAYED	Floortype	
Case ID.	2956391	Draw. Type.	ARCH
Sec No.	1	Com. No.	
Block No.		Plot No.	412030315
Bldg. No.	BLD-25-03488	Floor No.	
Date	07/2025	Sht. No.	A02
Scale	1/100	Job No.	

G.Manager	Architect	Designed By
ENG AYMEN	ENG IMEN	ENG IMEN

SITE DEVELOPMENT LAYOUT PLAN

Govement Of Ras Al Khaimah
R.A.K. Municipality
Buildings Administration

حكومة رأس الخيمة
دائـرة البلـدية
إدارة المباني

Approved On
اعتمد في

08 September 2025

Building Permit #:

Approved By:

Savana
Engineering Consultancy & interior design

Client	FAHAD SULAIMAN ABDULLA ALSHEHI		
Project	DOUBLE STORY VILLA		
Drg.Title	SITE SETTING PLAN		
Area	SHEIKH ZAYED	Floortype	
Case ID.	2956391	Draw. Type.	ARCH
Sec No.	1	Com. No.	
Block No.		Plot No.	412030315
Bldg. No.	BLD-25-03488	Floor No.	
Date	07/2025	Sht. No.	A03
Scale	1/100	Job No.	

G.Manager	Architect	Designed By
ENG AYMEN	ENG IMEN	ENG IMEN

SITE SETTING PLAN

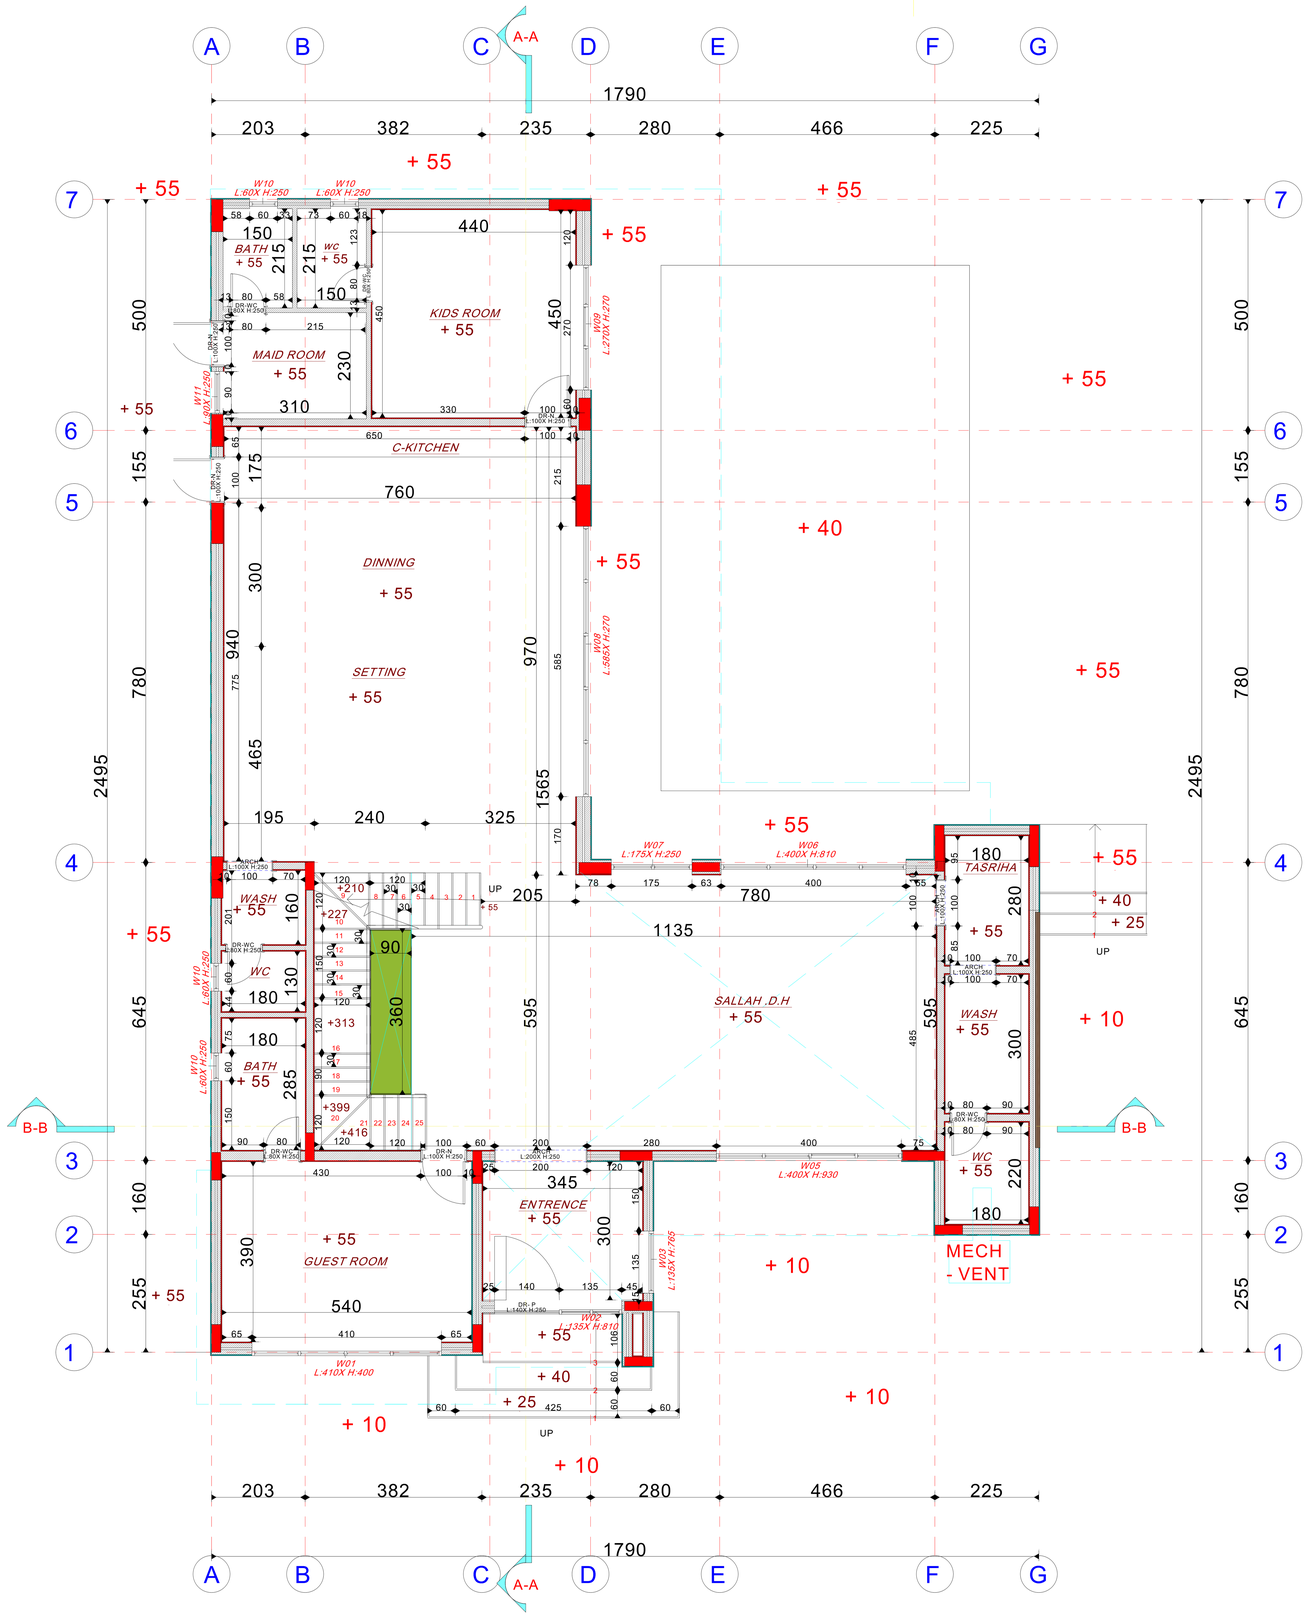

Govemment Of Ras Al Khaimah
R.A.K. Municipality
Buildings Administration

حكومة رأس الخيمة
دائرة البلدية
إدارة المباني

Approved On — اعتمد في

08 September 2025

Building Permit #:

Approved By:

FINISHING FOR VERANDAH	FINISHING FOR DRESSING AREA	FINISHING FOR BATH,WC & WASH	
			FLOORING
F3 Marble Tiles	F2 Ceramic Tiles (Non Slippery)	F1 Ceramic glazed tiles	
W3 Epoxy paint.	W2 Ceramic tiles up to ceiling	W1 Acrylic emulsion paint	WALLS
S2 Marble tiles 10cm hight		S1 Ceramic Tiles. 10cm hight	SKIRTING
C3 Epoxy paint.	C2 Oil Paint.	C1 Acrylic emulsion paint	CEILING

Note :-

* Rcc Lintels Must Be Made On Top Of All Doors , Arches And Windows All Of Them Are At Least 0.20 m Thick.
* All Blocks Adjacent To All Doors , Arches And Windows Must Be A Solid Block .

Rooms	Space	Number
Residential	350.8	
Commercial		
Industrial		
Goverment		
Resident.-Comm.		
Total		

Savana
Engineering Consultancy & interior design

Client	FAHAD SULAIMAN ABDULLA ALSHEHI		
Project	DOUBLE STORY VILLA		
Drg.Title	GROUND FLOOR PLAN		
Area	SHEIKH ZAYED	Floortype	G
Case ID.	2956391	Draw. Type.	ARCH
Sec No.	1	Com. No.	
Block No.		Plot No.	412030315
Bldg. No.	BLD-25-03488	Floor No.	01
Date	07/2025	Sht. No.	A04
Scale	1/100	Job No.	

G.Manager	Architect	Designed By
ENG AYMEN	ENG IMEN	ENG IMEN

GROUND FLOOR PLAN

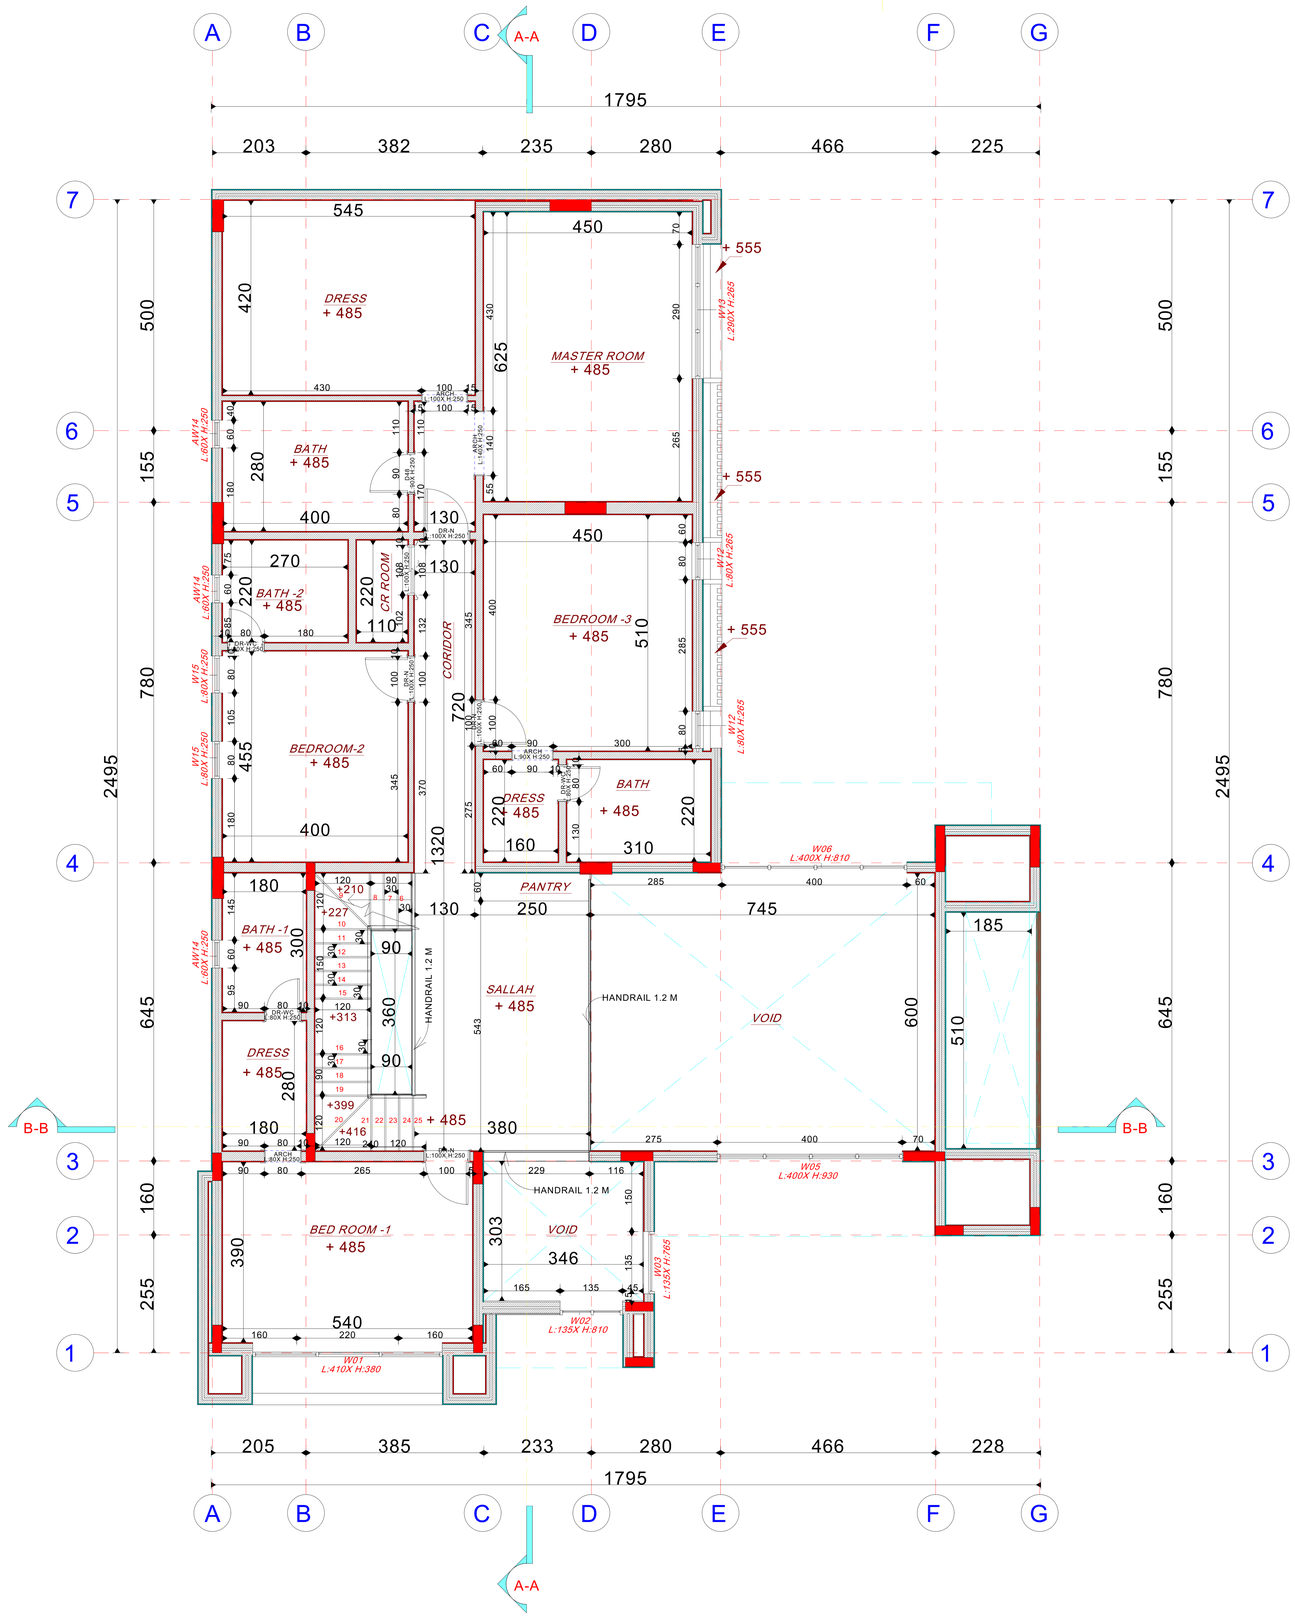

FINISHING FOR VERANDAH		FINISHING FOR DRESSING AREA		FINISHING FOR BATH,WC & WASH	
S2	Marble tiles 10cm hight	S1	Ceramic Tiles 10cm hight	F2	Ceramic Tiles (Non Slippery)
F3	Marble Tiles	F1	Ceramic glazed tiles	W2	Ceramic tiles up to ceiling
W3	Epoxy paint.	W1	Acrylic emulsion paint	C2	Oil Paint.
C3	Epoxy paint.	C1	Acrylic emulsion paint		

SKIRTING | FLOORING | WALLS | CEILING

Govemment Of Ras Al Khaimah
R.A.K. Municipality
Buildings Administration

حكومة رأس الخيمة
دائرة البلدية
إدارة المباني

Approved On — اعتمد في

08 September 2025

Building Permit #:

Appoved By:

Note :-

* Rcc Lintels Must Be Made On Top Of All Doors , Arches And Windows All Of Them Are At Least 0.20 m Thick.
* All Blocks Adjacent To All Doors , Arches And Windows Must Be A Solid Block .

Rooms	Space	Number
Residential	350.8	
Commercial		
Industrial		
Goverment		
Resident.-Comm.		
Total		

Savana
Engineering Consultancy & interior design

Client	FAHAD SULAIMAN ABDULLA ALSHEHI		
Project	DOUBLE STORY VILLA		
Drg.Title	FIRST FLOOR PLAN		
Area	SHEIKH ZAYED	Floortype	F
Case ID.	2956391	Draw. Type.	ARCH
Sec No.	1	Com. No.	
Block No.		Plot No.	412030315
Bldg. No.	BLD-25-03488	Floor No.	01
Date	07/2025	Sht. No.	A05
Scale	1/100	Job No.	

G.Manager	Architect	Designed By
ENG AYMEN	ENG IMEN	ENG IMEN

FIRST FLOOR PLAN

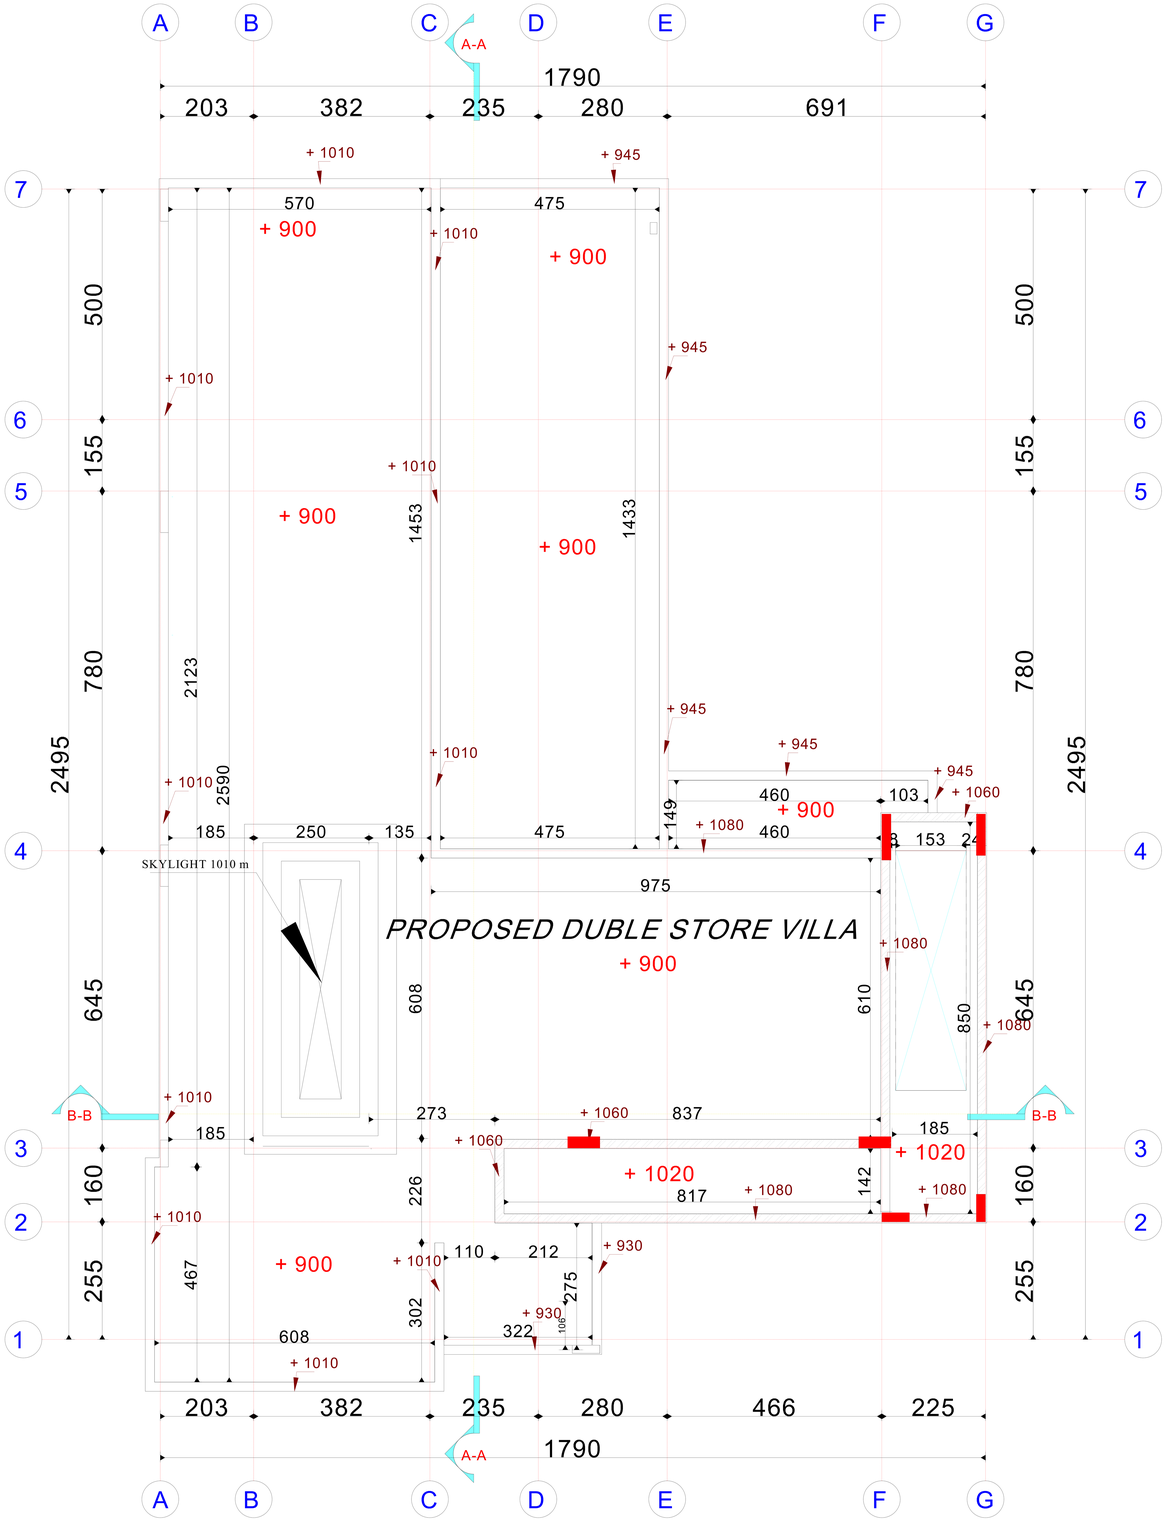

FINISHING FOR VERANDAH

FINISHING FOR DRESSING AREA

FINISHING FOR BATH,WC & WASH

	FLOORING
F1	Ceramic glazed tiles
F2	Ceramic Tiles (Non Slippery)
F3	Marble Tiles

	WALLS
W1	Acrylic emulsion paint
W2	Ceramic tiles up to ceiling
W3	Epoxy paint.

	SKIRTING
S1	Ceramic Tiles. 10cm hight
S2	Marble tiles 10cm hight

	CEILING
C1	Acrylic emulsion paint
C2	Oil Paint.
C3	Epoxy paint.

Govemment Of Ras Al Khaimah
R.A.K. Municipality
Buildings Administration

حكومة رأس الخيمة
دائـرة البلـدية
إدارة المباني

Approved On — اعتمد في

08 September 2025

Building Permit #:

Appoved By:

Rooms	Space	Number
Residential	35	
Commercial		
Industrial		
Goverment		
Resident.-Comm.		
Total		

Savana
Engineering Consultancy & interior design

Client	FAHAD SULAIMAN ABDULLA ALSHEHI		
Project	DOUBLE STORY VILLA		
Drg.Title	ROOF PLAN		
Area	SHEIKH ZAYED	Floortype	R
Case ID.	2956391	Draw. Type.	ARCH
Sec No.	1	Com. No.	
Block No.		Plot No.	412030315
Bldg. No.	BLD-25-03488	Floor No.	01
Date	07/2025	Sht. No.	A06
Scale	1/100	Job No.	

G.Manager	Architect	Designed By
ENG AYMEN	ENG IMEN	ENG IMEN

ROOF FLOOR PLAN

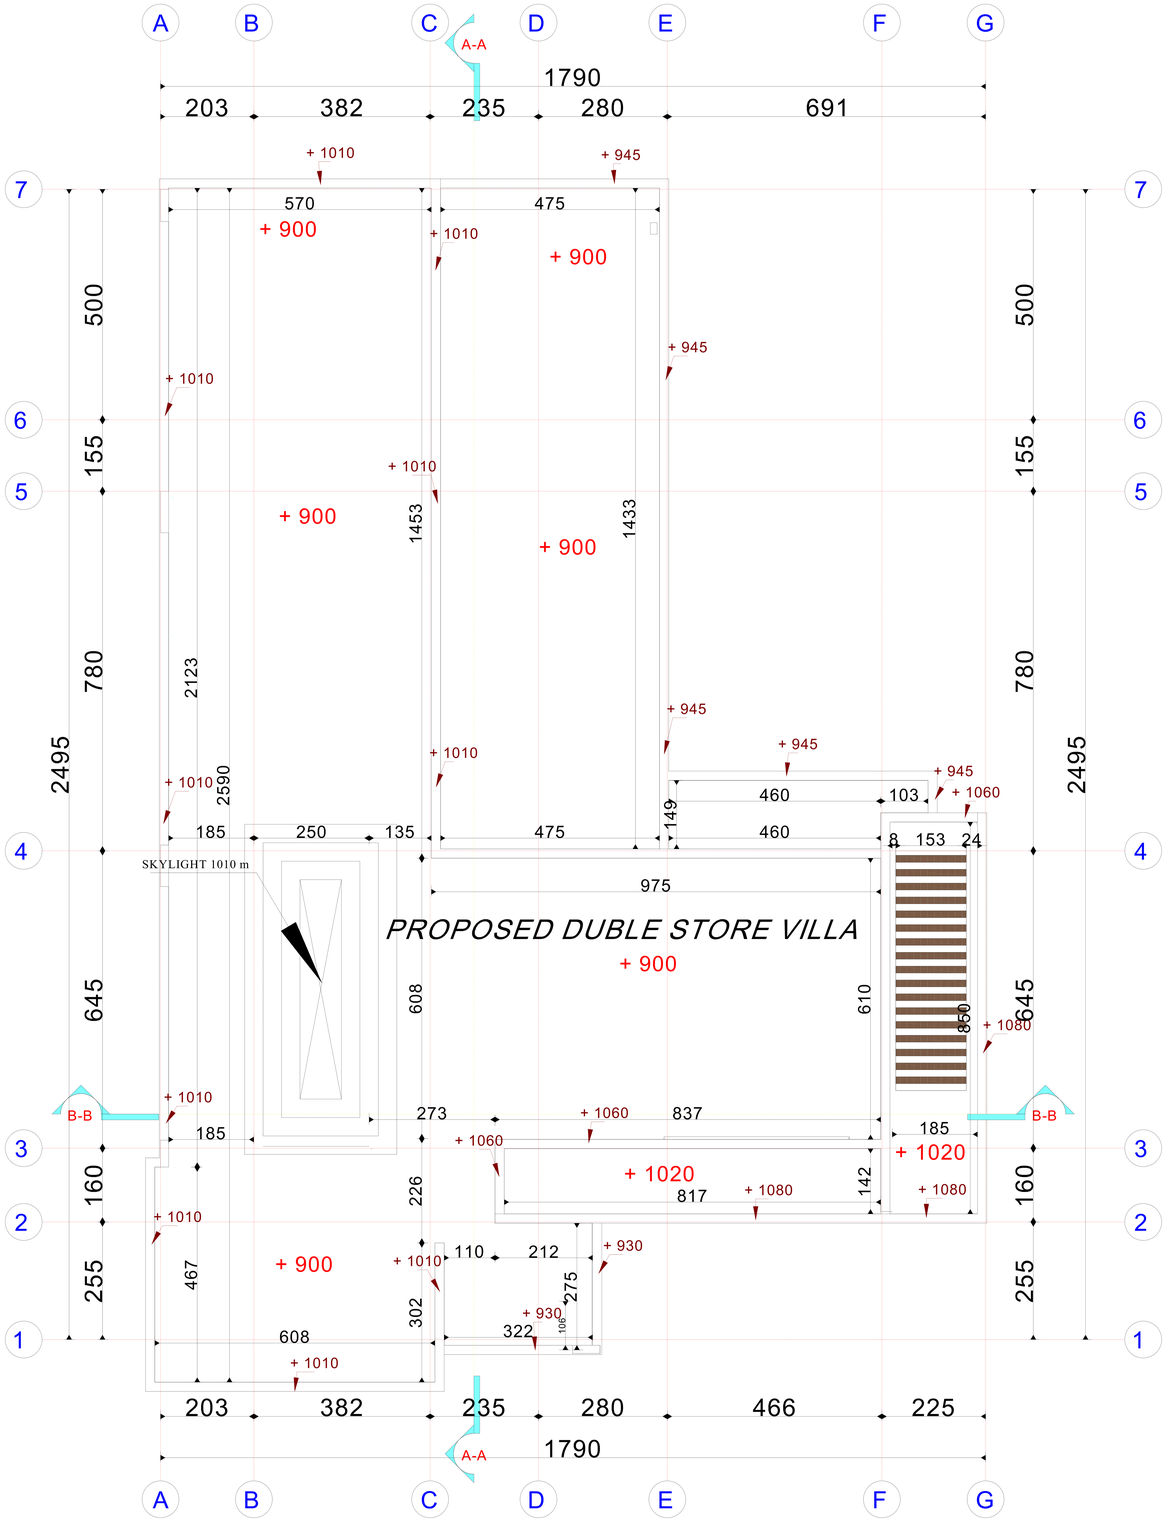

TOP ROOF FLOOR PLAN

Govemment Of Ras Al Khaimah
R.A.K. Municipality
Buildings Administration

حكومة رأس الخيمة
دائـرة البلـدية
إدارة المباني

Approved On — اعتمد في

08 September 2025

Building Permit #:

Appoved By:

FINISHING FOR BATH,WC & WASH AREA	FLOORING	F1 Ceramic glazed tiles
		F2 Ceramic Tiles (Non Slippery)
		F3 Marble Tiles
	WALLS	W1 Acrylic emulsion paint
		W2 Ceramic tiles up to ceiling
		W3 Epoxy paint.
	SKIRTING	S1 Ceramic Tiles. 10cm hight
		S2 Marble tiles 10cm hight
FINISHING FOR DRESSING AREA	CEILING	C1 Acrylic emulsion paint
		C2 Oil Paint.
		C3 Epoxy paint.
FINISHING FOR VERANDAH		

Savana
Engineering Consultancy & interior design

Client	FAHAD SULAIMAN ABDULLA ALSHEHI		
Project	DOUBLE STORY VILLA		
Drg.Title	TOP ROOF PLAN		
Area	SHEIKH ZAYED	Floortype	
Case ID.	2956391	Draw. Type.	ARCH
Sec No.	1	Com. No.	
Block No.		Plot No.	412030315
Bldg. No.	BLD-25-03488	Floor No.	
Date	07/2025	Sht. No.	A06A
Scale	1/100	Job No.	

G.Manager	Architect	Designed By
ENG AYMEN	ENG IMEN	ENG IMEN

GROUND FLOOR LEVEL	GFL
FRIST FLOOR FINSHING	FFL
TOP OF CONCRETE	TOC
TOP OF PARAPET	TOP

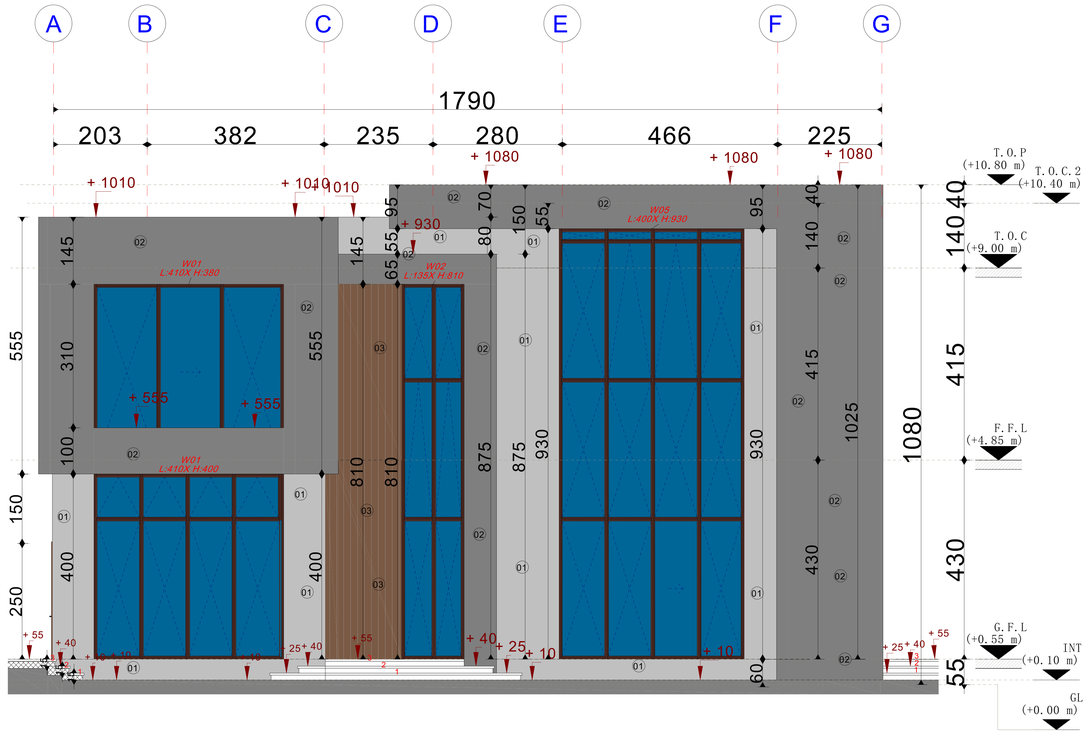

Govemment Of Ras Al Khaimah
R.A.K. Municipality
Buildings Administration

حكومة رأس الخيمة
دائرة البلدية
إدارة المباني

Approved On — اعتمد في

08 September 2025

Building Permit #:

Appoved By:

FINSHING	
1	FULL EPOXY PAINT [white]
2	FULL EPOXY BLACK PAINT
3	WOOD Aluminum
4	

Savana
Engineering Consultancy & interior design

Client	FAHAD SULAIMAN ABDULLA ALSHEHI		
Project	DOUBLE STORY VILLA		
Drg.Title	FRONT ELEVATION		
Area	SHEIKH ZAYED	Floortype	
Case ID.	2956391	Draw. Type.	ARCH
Sec No.	1	Com. No.	
Block No.		Plot No.	412030315
Bldg. No.	BLD-25-03488	Floor No.	
Date	07/2025	Sht. No.	A07
Scale	1/100	Job No.	

G.Manager	Architect	Designed By
ENG AYMEN	ENG IMEN	ENG IMEN

FRONT ELEVATION

GROUND FLOOR LEVEL	GFL
FRIST FLOOR FINSHING	FFL
TOP OF CONCRETE	TOC
TOP OF PARAPET	TOP

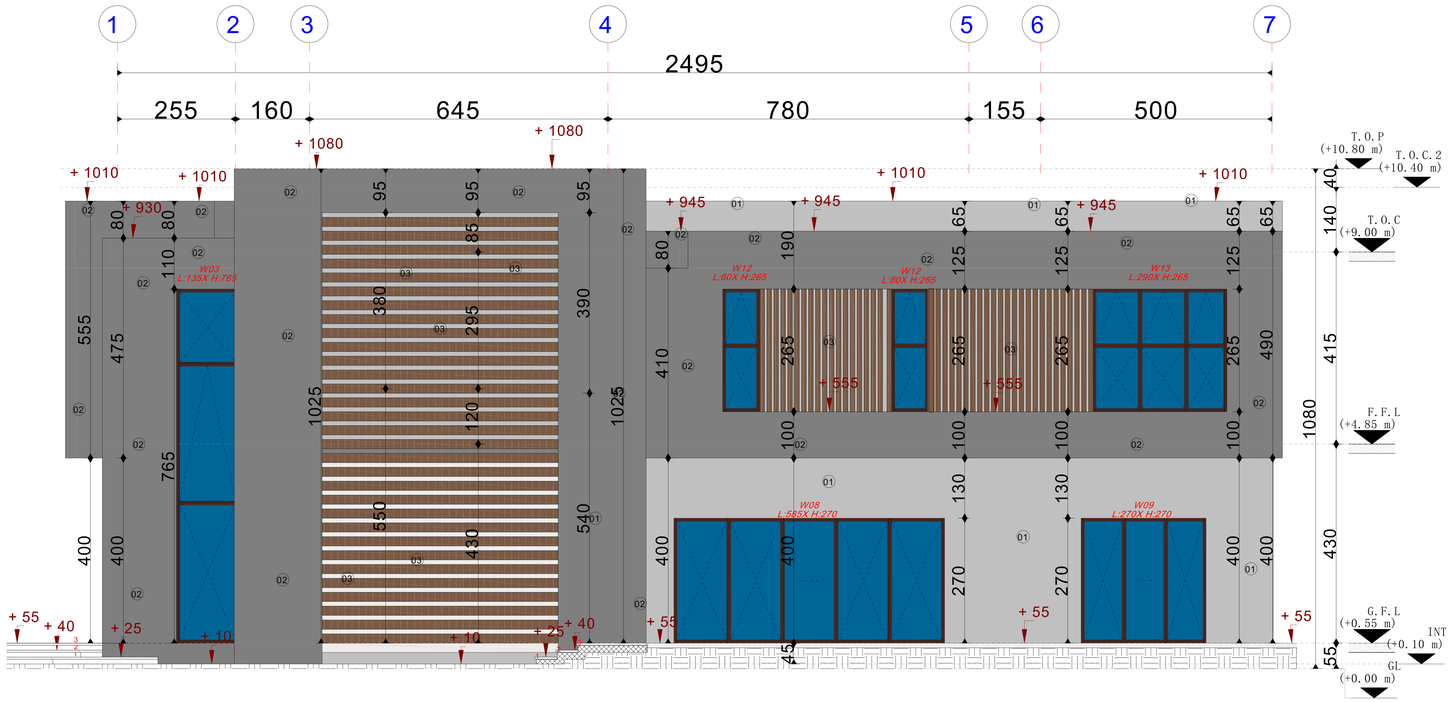

RIGHT ELEVATION

Govemment Of Ras Al Khaimah
R.A.K. Municipality
Buildings Administration

حكومة رأس الخيمة
دائرة البلدية
إدارة المباني

Approved On — اعتمد في

08 September 2025

Building Permit #:

Appoved By:

FINSHING	
1	FULL EPOXY PAINT [white]
2	FULL EPOXY BLACK PAINT
3	WOOD Aluminum
4	

Savana
Engineering Consultancy & interior design

Client	FAHAD SULAIMAN ABDULLA ALSHEHI		
Project	DOUBLE STORY VILLA		
Drg.Title	RIGHT ELEVATION		
Area	SHEIKH ZAYED	Floortype	
Case ID.	2956391	Draw. Type.	ARCH
Sec No.	1	Com. No.	
Block No.		Plot No.	412030315
Bldg. No.	BLD-25-03488	Floor No.	
Date	07/2025	Sht. No.	A08
Scale	1/100	Job No.	

G.Manager	Architect	Designed By
ENG AYMEN	ENG IMEN	ENG IMEN

GROUND FLOOR LEVEL	GFL
FRIST FLOOR FINSHING	FFL
TOP OF CONCRETE	TOC
TOP OF PARAPET	TOP

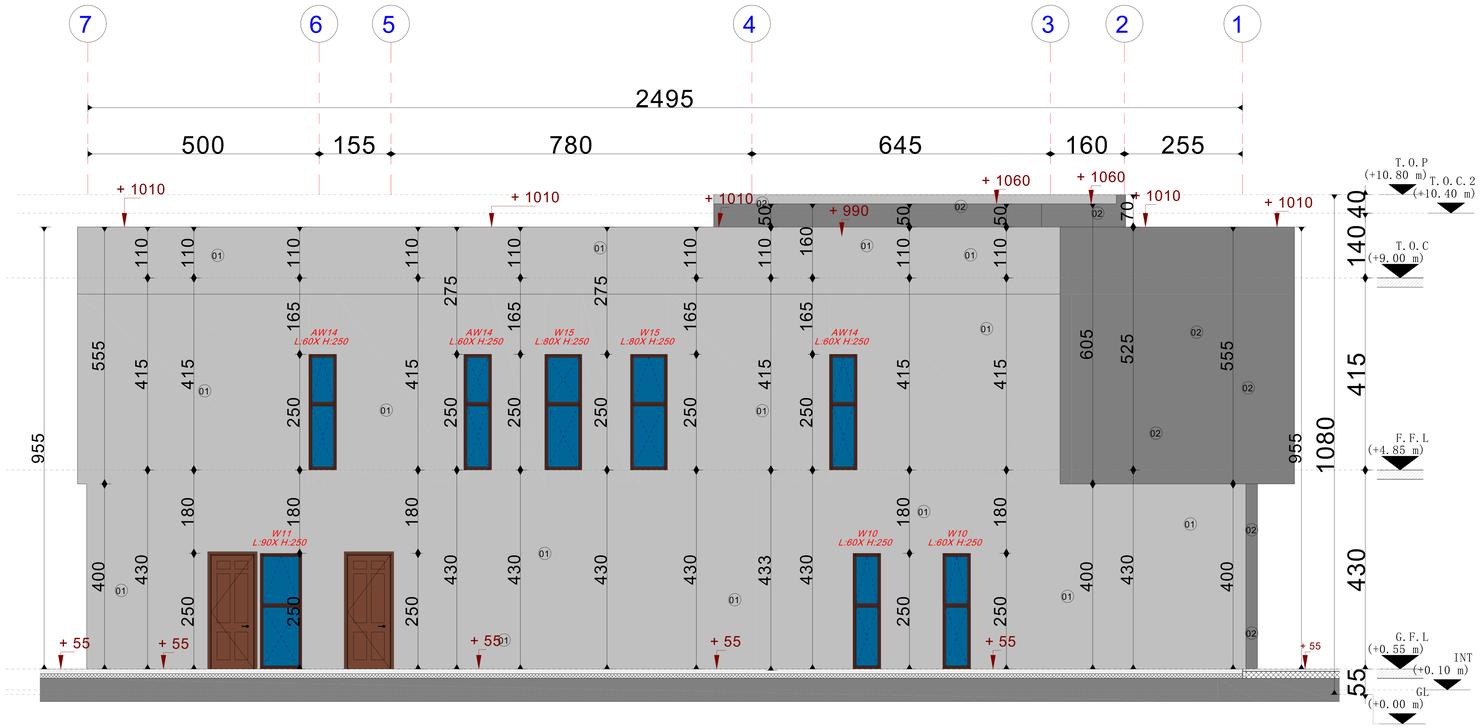

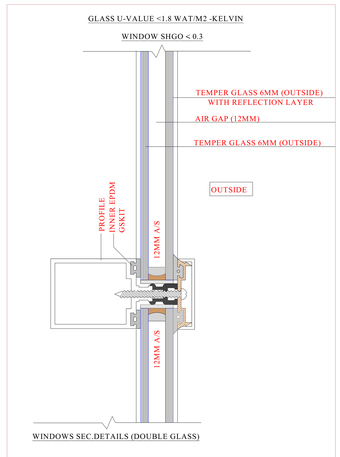

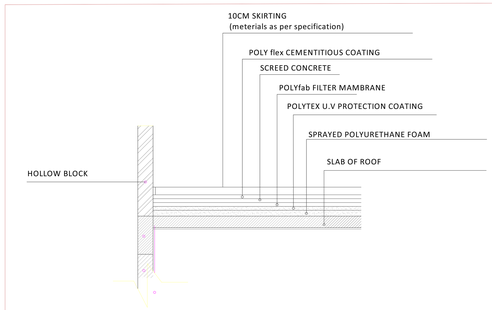

DETAIL FOR COMBO SYSTEM
U-VALUE <0.3 W/M2 K

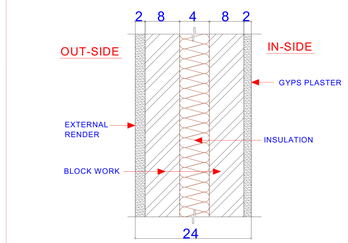

As per E. Walls Predefined Section:	W - 1 - A
DETAIL "W1"	TYPICAL FOR EXTERNAL WALL USING INSULATED CONC. BLOCK (200 mm) U-VALUE < 0.5 W/M2 K

LEFT ELEVATION

Govemment Of Ras Al Khaimah
R.A.K. Municipality
Buildings Administration

حكومة رأس الخيمة
دائرة البلدية
إدارة المباني

Approved On — اعتمد في

08 September 2025

Building Permit #:

Appoved By:

* Rcc Lintels Must Be Made On Top Of All Doors , Arches And Windows All Of Them Are At Least 0.20 m Thick.
* All Blocks Adjacent To All Doors , Arches And Windows Must Be A Solid Block .

U VALUE AND SHGC

ALL GLASS MUST BE DOUBLE UNITES

GLASS SPECIFICATION:-

U-value (w/m2.k)<_ 1.8

SHADING CO- EFFICIENT (SC) <0.3

FINSHING	
1	FULL EPOXY PAINT [white]
2	FULL EPOXY BLACK PAINT
3	WOOD Aluminum
4	

Savana
Engineering Consultancy & interior design

Client	FAHAD SULAIMAN ABDULLA ALSHEHI		
Project	DOUBLE STORY VILLA		
Drg.Title	LIFT ELEVATION		
Area	SHEIKH ZAYED	Floortype	
Case ID.	2956391	Draw. Type.	ARCH
Sec No.	1	Com. No.	
Block No.		Plot No.	412030315
Bldg. No.	BLD-25-03488	Floor No.	
Date	07/2025	Sht. No.	A09
Scale	1/100	Job No.	

G.Manager	Architect	Designed By
ENG AYMEN	ENG IMEN	ENG IMEN

GROUND FLOOR LEVEL	GFL
FRIST FLOOR FINSHING	FFL
TOP OF CONCRETE	TOC
TOP OF PARAPET	TOP

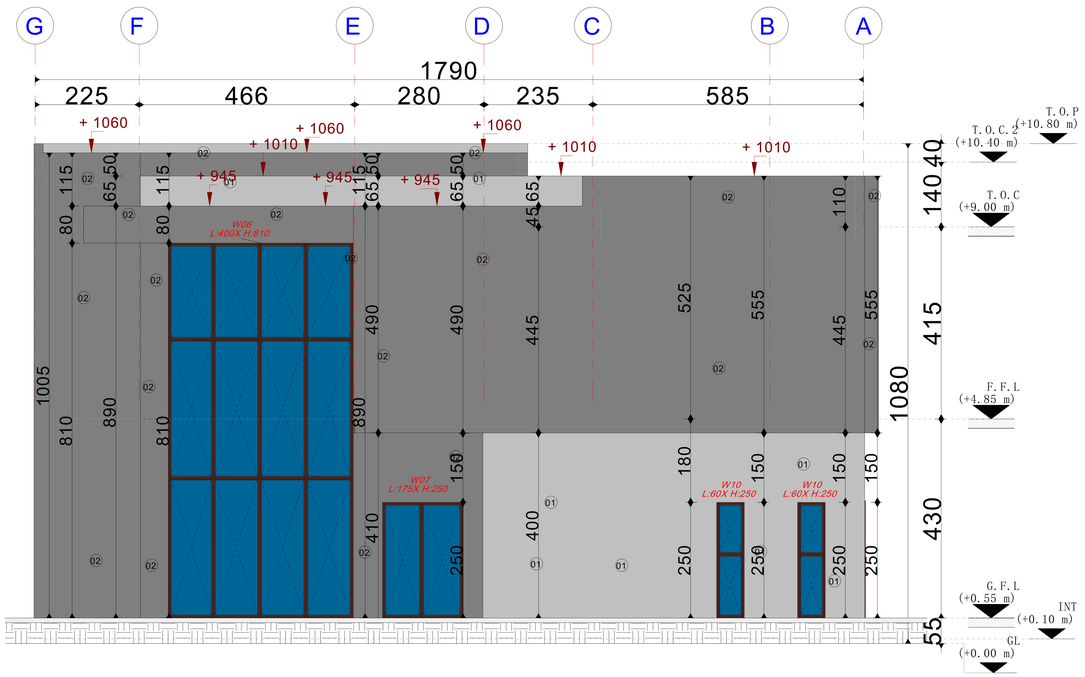

REAR ELEVATION

Govemment Of Ras Al Khaimah
R.A.K. Municipality
Buildings Administration

حكومة رأس الخيمة
دائرة البلدية
إدارة المباني

Approved On — اعتمد في

08 September 2025

Building Permit #:

Appoved By:

FINSHING	
1	FULL EPOXY PAINT [white]
2	FULL EPOXY BLACK PAINT
3	WOOD Aluminum
4	

Savana
Engineering Consultancy & interior design

Client	FAHAD SULAIMAN ABDULLA ALSHEHI		
Project	DOUBLE STORY VILLA		
Drg.Title	REAR ELEVATION		
Area	SHEIKH ZAYED	Floortype	
Case ID.	2956391	Draw. Type.	ARCH
Sec No.	1	Com. No.	
Block No.		Plot No.	412030315
Bldg. No.	BLD-25-03488	Floor No.	
Date	07/2025	Sht. No.	A10
Scale	1/100	Job No.	

G.Manager	Architect	Designed By
ENG AYMEN	ENG IMEN	ENG IMEN

GROUND FLOOR LEVEL	GFL
FRIST FLOOR FINSHING	FFL
TOP OF CONCRETE	TOC
TOP OF PARAPET	TOP

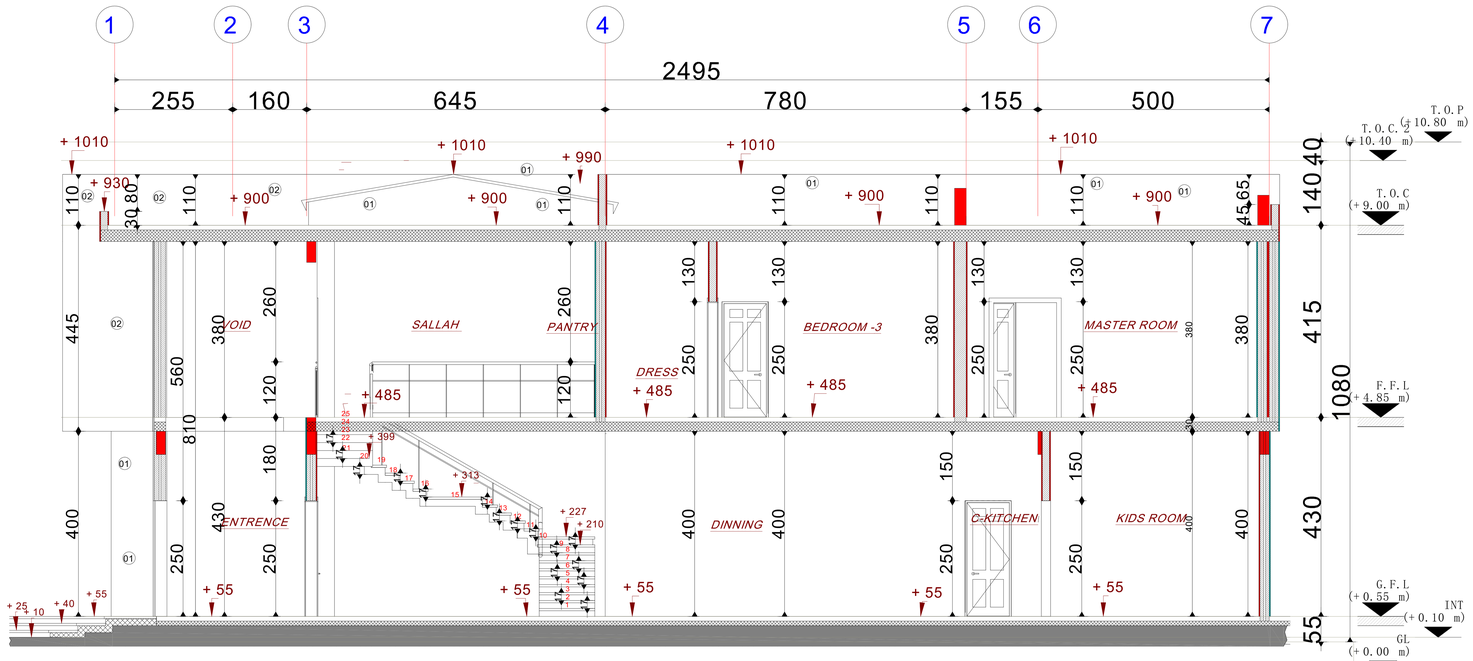

Govemment Of Ras Al Khaimah
R.A.K. Municipality
Buildings Administration

حكومة رأس الخيمة
دائرة البلدية
إدارة المباني

Approved On — اعتمد في

08 September 2025

Building Permit #:

Appoved By:

ALL GLASS MUST BE DOUBLE UNITES

U-value (w/m2.k)<_ 1.8

SHADING CO- EFFICIENT (SC) <0.3

FINSHING	
1	FULL EPOXY PAINT [white]
2	FULL EPOXY BLACK PAINT
3	WOOD Aluminum
4	

Savana
Engineering Consultancy & interior design

Client	FAHAD SULAIMAN ABDULLA ALSHEHI		
Project	DOUBLE STORY VILLA		
Drg.Title	SECTION A-A		
Area	SHEIKH ZAYED	Floortype	
Case ID.	2956391	Draw. Type.	ARCH
Sec No.	1	Com. No.	
Block No.		Plot No.	412030315
Bldg. No.	BLD-25-03488	Floor No.	
Date	07/2025	Sht. No.	A11
Scale	1/100	Job No.	

G.Manager	Architect	Designed By
ENG AYMEN	ENG IMEN	ENG IMEN

SECTION A-A

GROUND FLOOR LEVEL	GFL
FRIST FLOOR FINSHING	FFL
TOP OF CONCRETE	TOC
TOP OF PARAPET	TOP

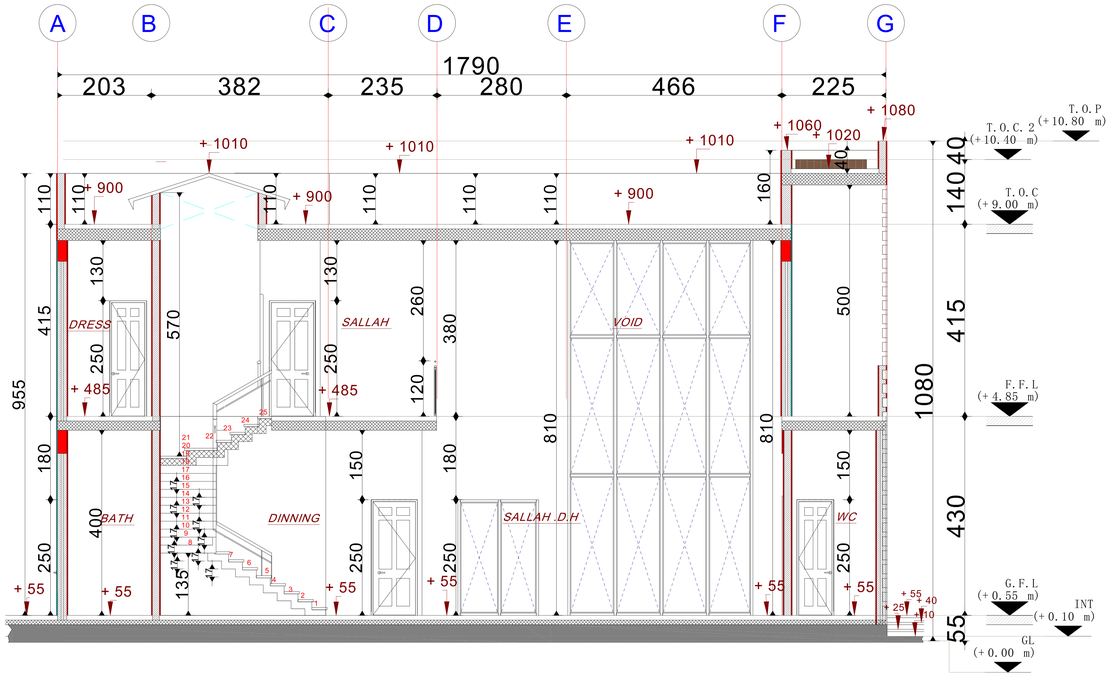

Govemment Of Ras Al Khaimah
R.A.K. Municipality
Buildings Administration

حكومة رأس الخيمة
دائرة البلدية
إدارة المباني

Approved On — اعتمد في

08 September 2025

Building Permit #:

Appoved By:

ALL GLASS MUST BE DOUBLE UNITES

GLASS SPECIFICATION:-

U-value (w/m2.k)<_ 1.8

SHADING CO- EFFICIENT (SC) <0.3

FINSHING	
1	FULL EPOXY PAINT [white]
2	FULL EPOXY BLACK PAINT
3	WOOD Aluminum
4	

Savana
Engineering Consultancy & interior design

Client	FAHAD SULAIMAN ABDULLA ALSHEHI		
Project	DOUBLE STORY VILLA		
Drg.Title	SECTION B-B		
Area	SHEIKH ZAYED	Floortype	
Case ID.	2956391	Draw. Type.	ARCH
Sec No.	1	Com. No.	
Block No.		Plot No.	412030315
Bldg. No.	BLD-25-03488	Floor No.	
Date	07/2025	Sht. No.	A12
Scale	1/100	Job No.	

G.Manager	Architect	Designed By
ENG AYMEN	ENG IMEN	ENG IMEN

SECTION B-B

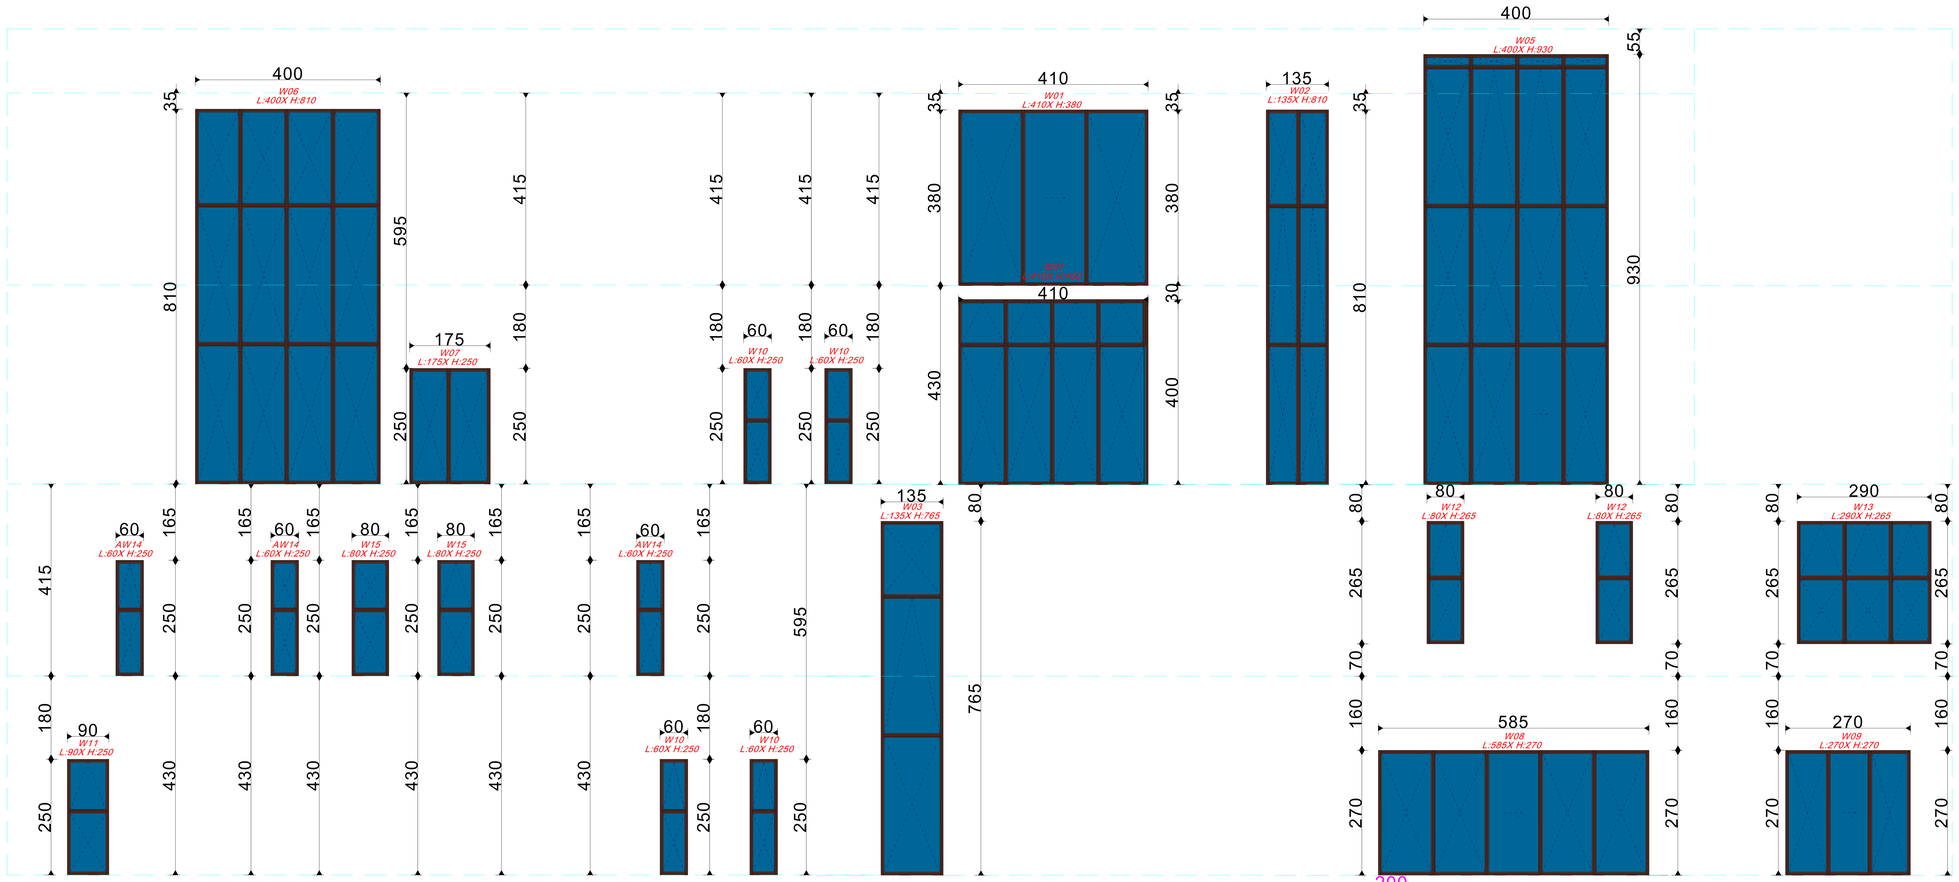

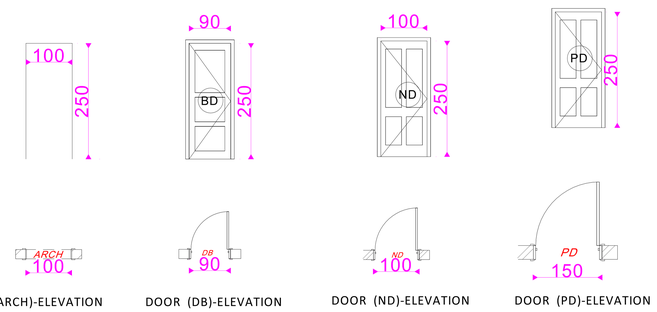

(ARCH)-ELEVATION

DOOR (DB)-ELEVATION

DOOR (ND)-ELEVATION

DOOR (PD)-ELEVATION

DOOR (DW)-ELEVATION

Govemment Of Ras Al Khaimah
R.A.K. Municipality
Buildings Administration

حكومة رأس الخيمة
دائرة البلدية
إدارة المباني

Approved On — اعتمد في

08 September 2025

Building Permit #:

Appoved By:

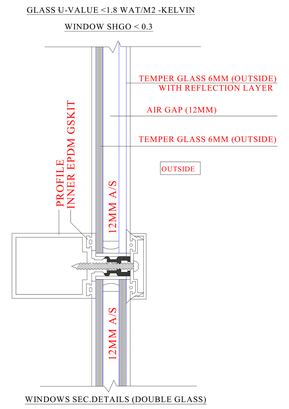

WINDOWS SEC.DETAILS (DOUBLE GLASS)

ALL GLASS MUST BE DOUBLE UNITES

GLASS SPECIFICATION:-

U-value (w/m2.k)<_ 1.8

SHADING CO- EFFICIENT (SC) <0.3

Savana
Engineering Consultancy & interior design

Client	FAHAD SULAIMAN ABDULLA ALSHEHI		
Project	DOUBLE STORY VILLA		
Drg.Title	Opening Details		
Area	SHEIKH ZAYED	Floortype	
Case ID.	2956391	Draw. Type.	ARCH
Sec No.	1	Com. No.	
Block No.		Plot No.	412030315
Bldg. No.	BLD-25-03488	Floor No.	
Date	07/2025	Sht. No.	A13
Scale	1/100	Job No.	

G.Manager	Architect	Designed By
ENG AYMEN	ENG IMEN	ENG IMEN

OPENNING DETAILS

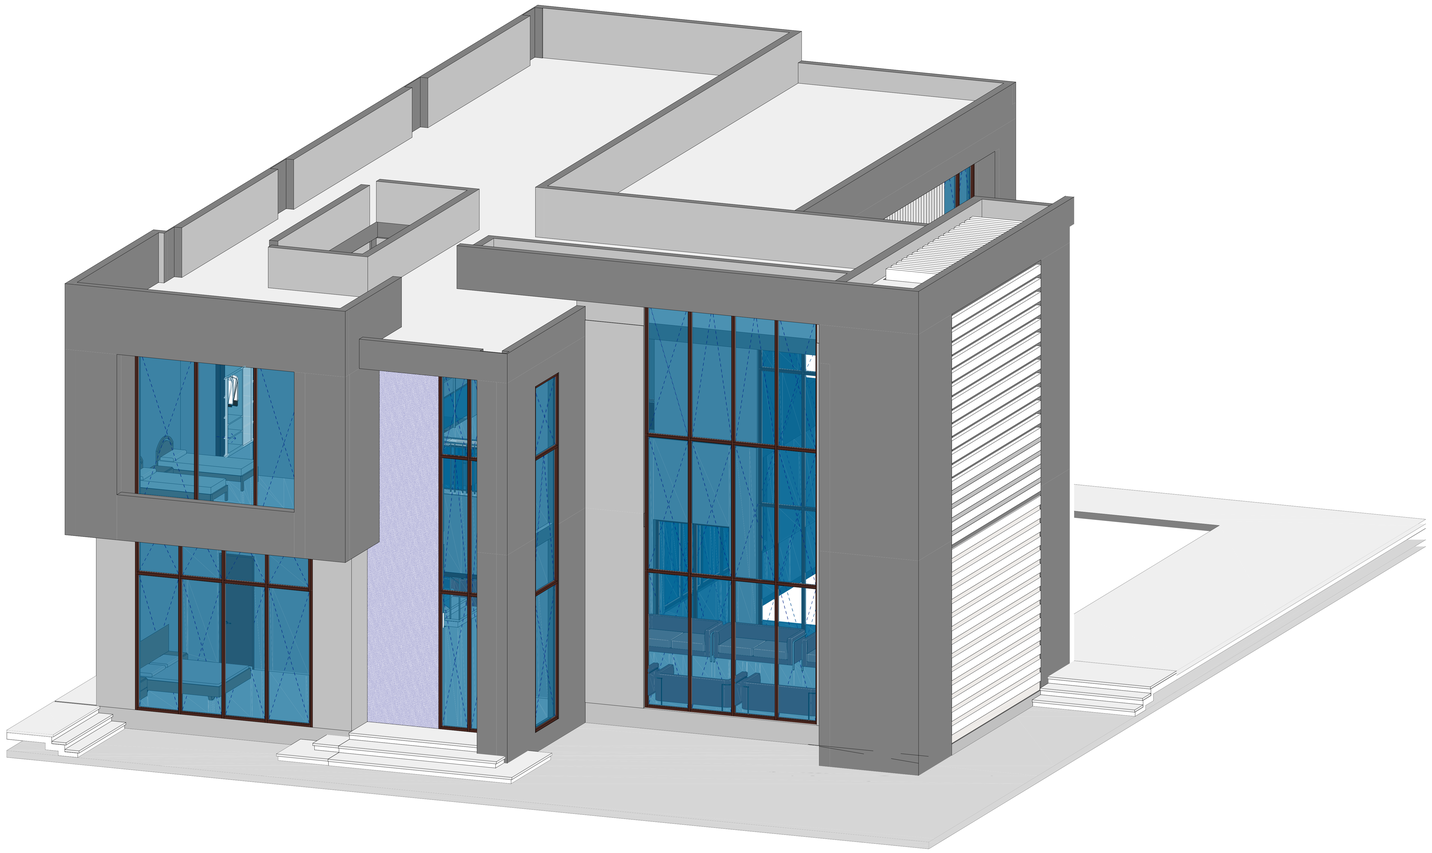

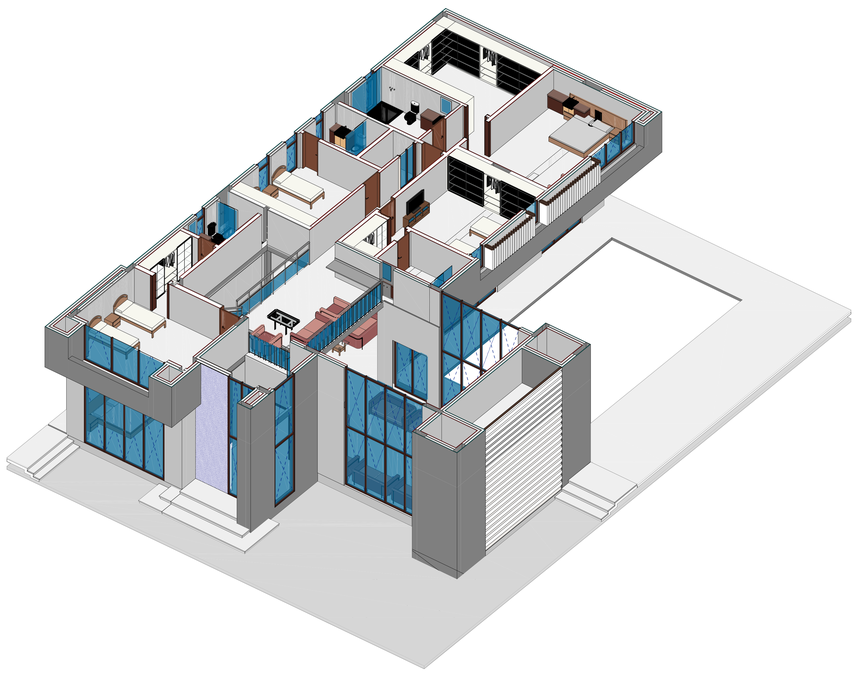

Govemment Of Ras Al Khaimah
R.A.K. Municipality
Buildings Administration

حكومة رأس الخيمة
دائرة البلدية
إدارة المباني

Approved On — اعتمد في

08 September 2025

Building Permit #:

Appoved By:

PERSPECTIVE

Savana
Engineering Consultancy & interior design

Client	FAHAD SULAIMAN ABDULLA ALSHEHI		
Project	DOUBLE STORY VILLA		
Drg.Title	PERSPECTIVE		
Area	SHEIKH ZAYED	Floortype	
Case ID.	2956391	Draw. Type.	ARCH
Sec No.	2	Com. No.	
Block No.		Plot No.	412030315
Bldg. No.	BLD-25-03488	Floor No.	
Date	07/2025	Sht. No.	A14
Scale	1/100	Job No.	

G.Manager	Architect	Designed By
ENG AYMEN	ENG IMEN	ENG IMEN

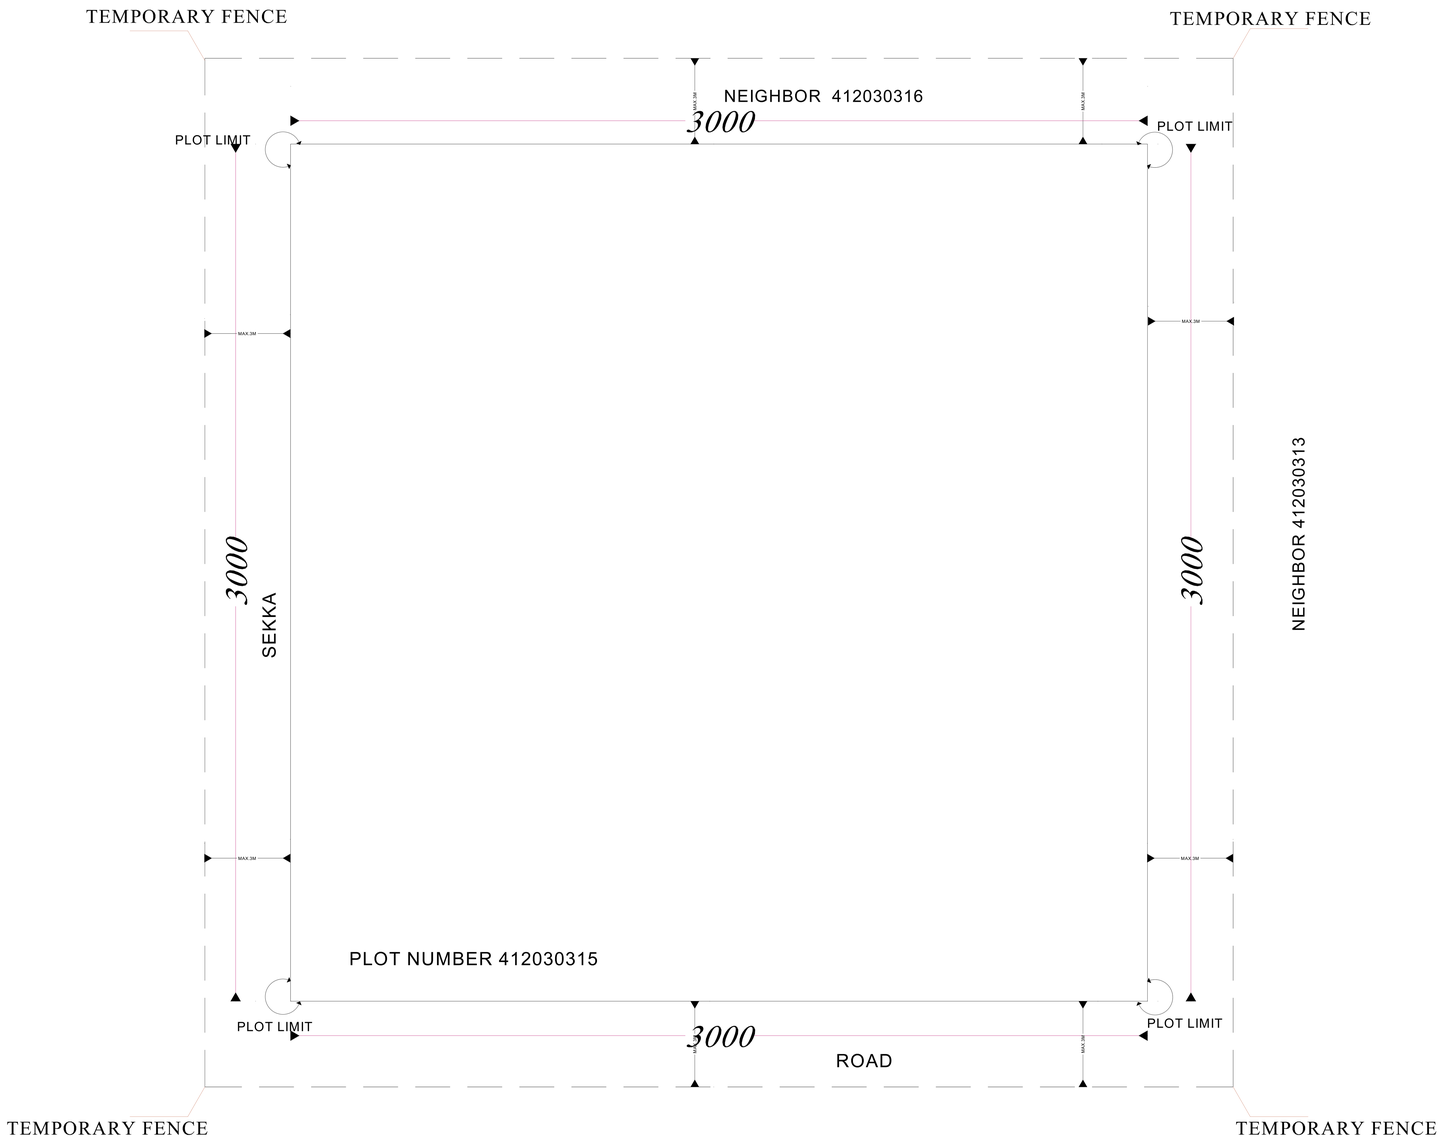

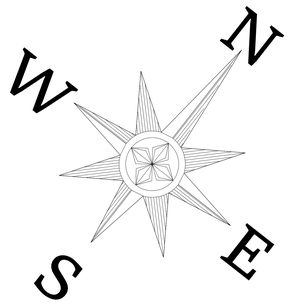

Govemment Of Ras Al Khaimah
R.A.K. Municipality
Buildings Administration

حكومة رأس الخيمة
دائرة البلدية
إدارة المباني

Approved On — اعتمد في

08 September 2025

Building Permit #:

Appoved By:

Savana
Engineering Consultancy & interior design

Client	FAHAD SULAIMAN ABDULLA ALSHEHI		
Project	DOUBLE STORY VILLA		
Drg.Title	GENERALE SITE TEMPORARY FENCE		
Area	SHEIKH ZAYED	Floortype	
Case ID.	2956391	Draw. Type.	ARCH
Sec No.	2	Com. No.	
Block No.		Plot No.	412030315
Bldg. No.	BLD-25-03488	Floor No.	
Date	07/2025	Sht. No.	A18
Scale	1/100	Job No.	

G.Manager	Architect	Designed By
ENG AYMEN	ENG IMEN	ENG IMEN

GENERALE SITE TEMPORARY FENCE

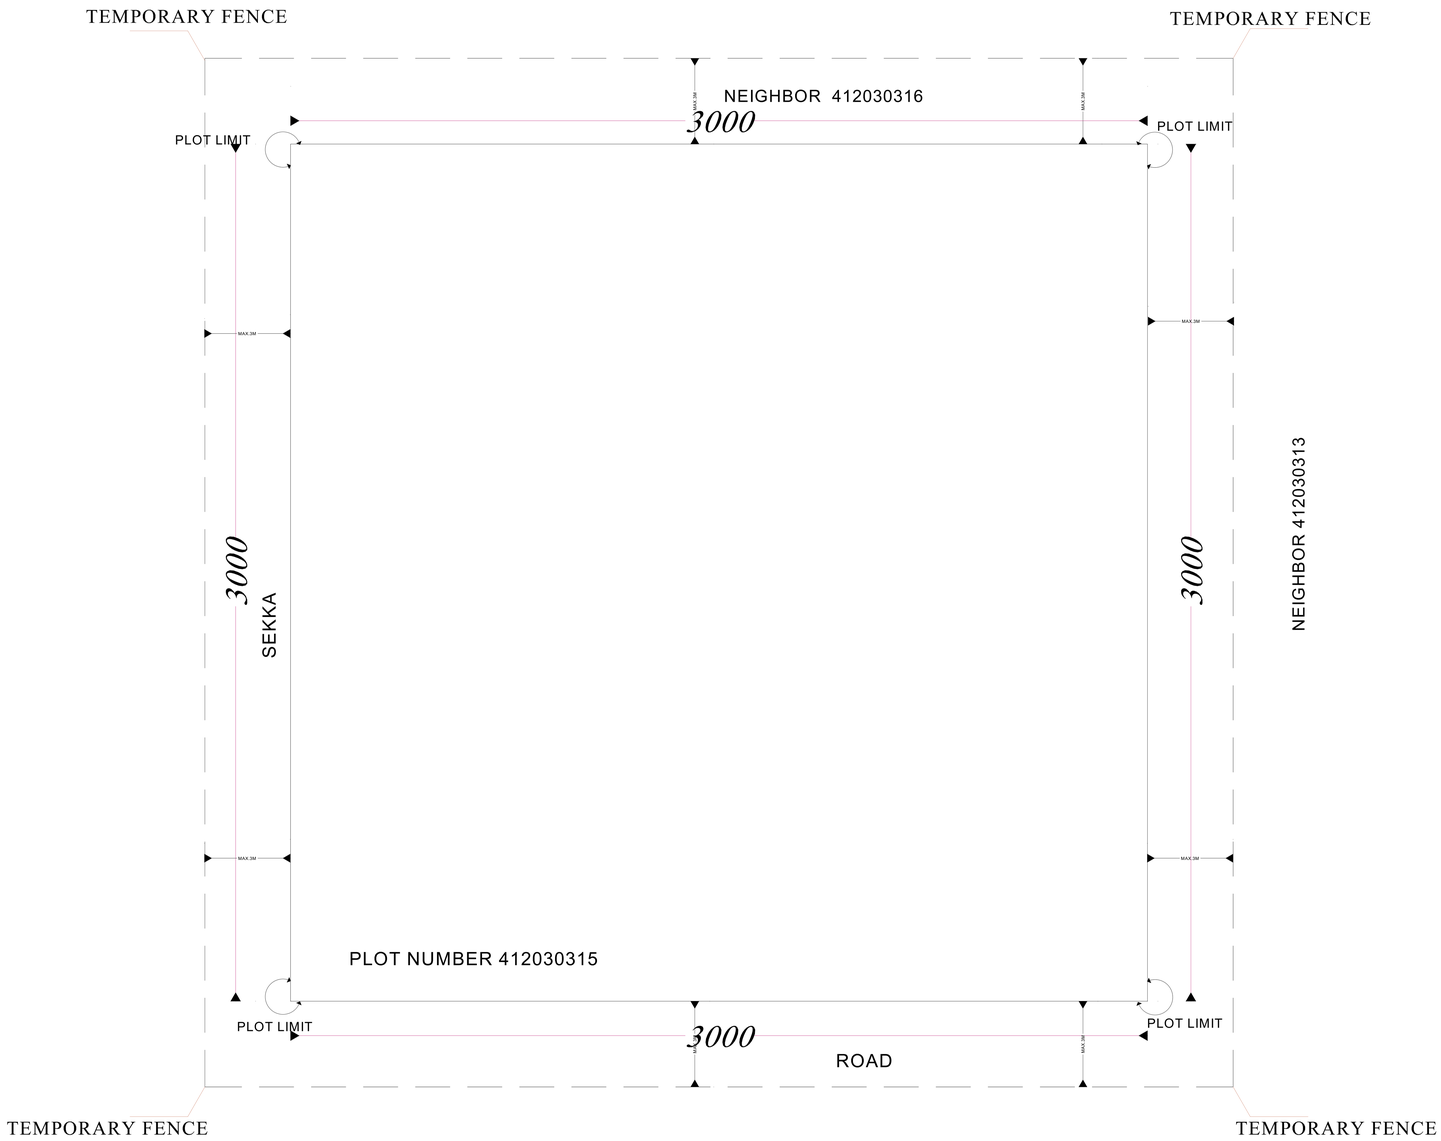

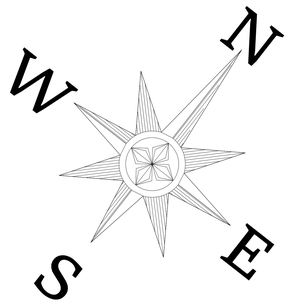

Govemment Of Ras Al Khaimah
R.A.K. Municipality
Buildings Administration

حكومة رأس الخيمة
دائرة البلدية
إدارة المباني

Approved On — اعتمد في

08 September 2025

Building Permit #:

Appoved By:

Savana
Engineering Consultancy & interior design

Client	FAHAD SULAIMAN ABDULLA ALSHEHI		
Project	DOUBLE STORY VILLA		
Drg.Title	GENERALE SITE TEMPORARY FENCE		
Area	SHEIKH ZAYED	Floortype	
Case ID.	2956391	Draw. Type.	ARCH
Sec No.	2	Com. No.	
Block No.		Plot No.	412030315
Bldg. No.	BLD-25-03488	Floor No.	
Date	07/2025	Sht. No.	A18
Scale	1/100	Job No.	

G.Manager	Architect	Designed By
ENG AYMEN	ENG IMEN	ENG IMEN

GENERALE SITE TEMPORARY FENCE

Type	SCHEDULE OF FINISHINGS
1	LIGHT IVORY

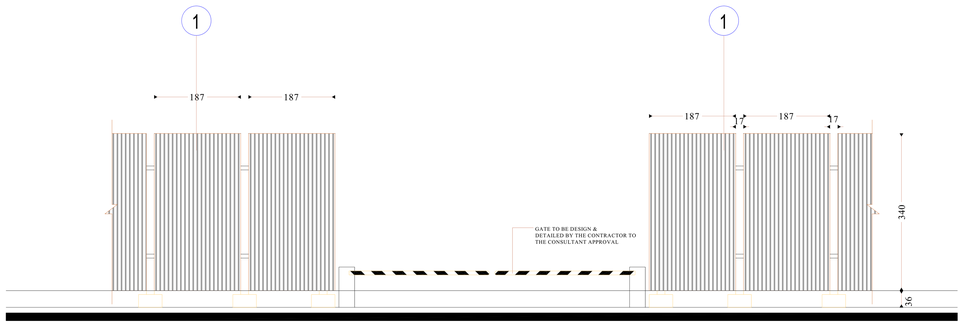

ALUMINIUM TEMPORARY FENCE

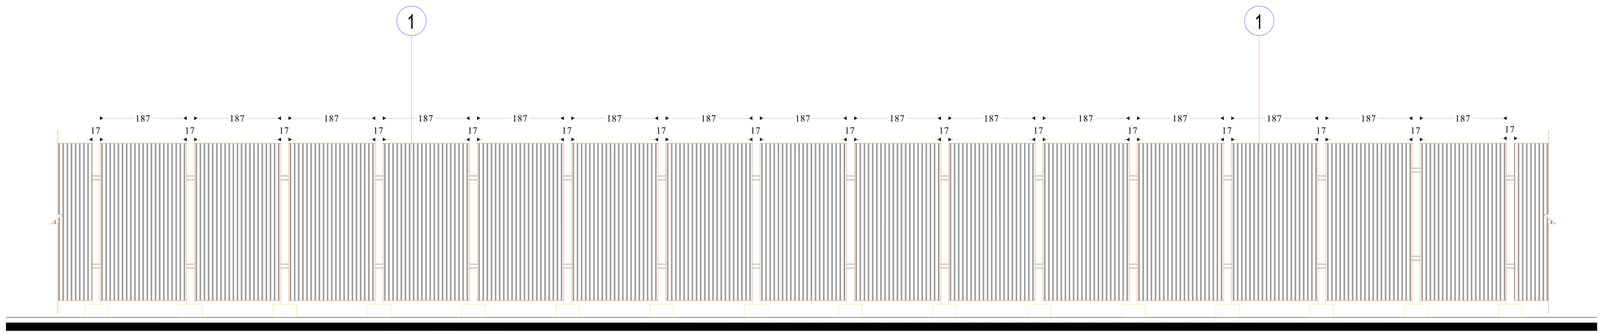

HOARDING ELEVATION

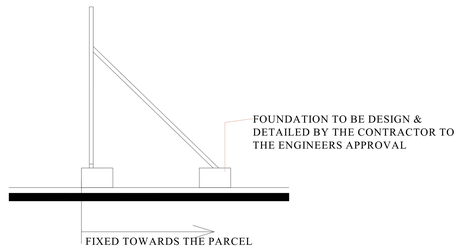

HOARDING SIDE ELEVATION

ALLUMINIUM FENCE

Govemment Of Ras Al Khaimah
R.A.K. Municipality
Buildings Administration

حكومة رأس الخيمة
دائرة البلدية
إدارة المباني

Approved On — اعتمد في

08 September 2025

Building Permit #:

Appoved By:

Savana
Engineering Consultancy & interior design

Client	FAHAD SULAIMAN ABDULLA ALSHEHI		
Project	DOUBLE STORY VILLA		
Drg.Title	ALLUMINIUM FENCE		
Area	SHEIKH ZAYED	Floortype	
Case ID.	2956391	Draw. Type.	ARCH
Sec No.	2	Com. No.	
Block No.		Plot No.	412030315
Bldg. No.	BLD-25-03488	Floor No.	
Date	07/2025	Sht. No.	A19
Scale	1/100	Job No.	

G.Manager	Architect	Designed By
ENG AYMEN	ENG IMEN	ENG IMEN

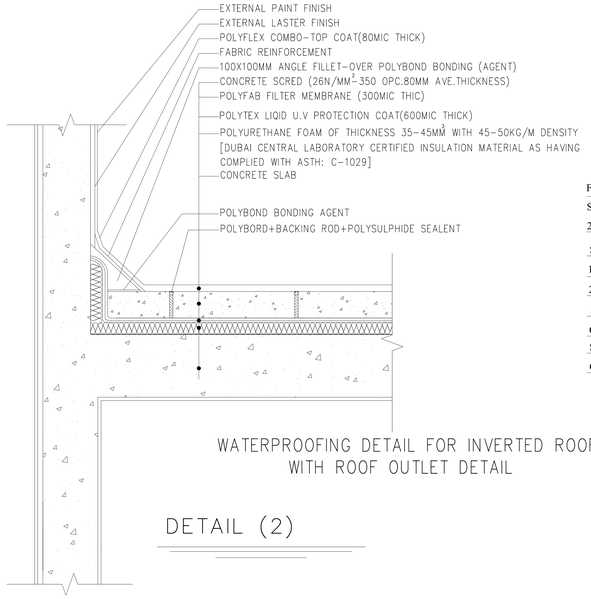

WATERPROOFING DETAIL FOR INVERTED ROOF
WITH ROOF OUTLET DETAIL

DETAIL (2)

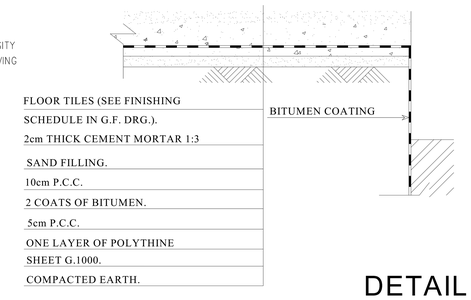

DETAIL (4)

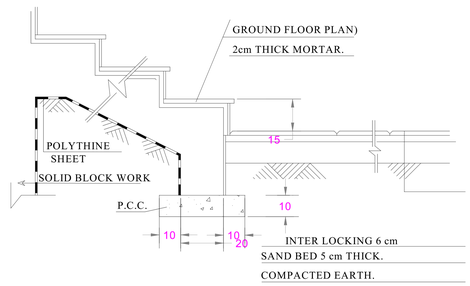

ENTRANCE STEPS DETAIL

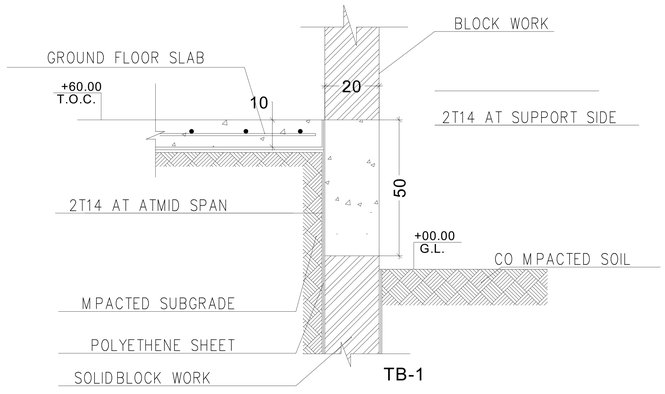

DETAIL (3)

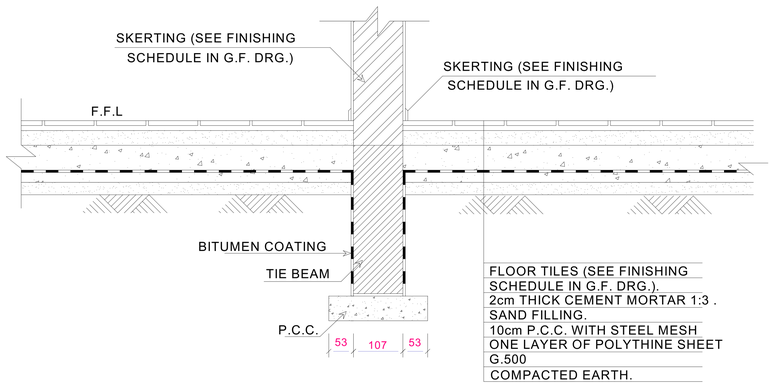

DETAIL (1)

GENERALE DETAILS

Govemment Of Ras Al Khaimah
R.A.K. Municipality
Buildings Administration

حكومة رأس الخيمة
دائرة البلدية
إدارة المباني

Approved On — اعتمد في

08 September 2025

Building Permit #:

Appoved By:

Savana
Engineering Consultancy & interior design

Client	FAHAD SULAIMAN ABDULLA ALSHEHI		
Project	DOUBLE STORY VILLA		
Drg.Title	GENERALE DETAILS		
Area	SHEIKH ZAYED	Floortype	
Case ID.	2956391	Draw. Type.	ARCH
Sec No.	2	Com. No.	
Block No.		Plot No.	412030315
Bldg. No.	BLD-25-03488	Floor No.	
Date	07/2025	Sht. No.	A20
Scale	1/100	Job No.	

G.Manager	Architect	Designed By
ENG AYMEN	ENG IMEN	ENG IMEN