

SCHEDULE OF FOOTINGS

TYPE	SIZE			REINFORCEMENT DETAILS				REMARKS.
	WIDTH (MM)	LENGTH (MM)	DEPTH (MM)	BOTTOM MESH		TOP MESH		
				SHORT BAR	LONG BAR	SHORT BAR	LONG BAR	
FNC	1000	1000	350	T12-150	T12-150	4T12	2T12	
F1	2200	2500	400	T12-150	T12-150	4T12	2T12	
F2	2400	2700	400	T12-100	T12-100	4T12	2T12	
F3	2600	2900	400	T12-100	T12-100	4T12	2T12	
F4	3400	3700	450	T16-150	T16-150	4T12	2T12	
CF1	1400	2800	400	T12-150	T12-150	T12-150	T12-150	
CF2	2200	4100	400	T14-150	T14-150	T12-150	T12-150	
CF3	3000	4700	450	T16-150	T16-150	T12-150	T12-150	
CF4	3000	3700	450	T16-150	T16-150	T12-150	T12-150	
CF5	3700	5300	500	T16-150	T16-150	T12-150	T12-150	
CF6	3800	4800	500	T16-150	T16-150	T12-150	T12-150	
CF7	3200	4000	400	T14-150	T14-150	T12-150	T12-150	
CF8	5650	9600	700	T16-150	T16-150	T12-150	T12-150	
F5	2700	3100	400	T16-150	T16-150	T12-150	T12-150	

SCHEDULE OF STRIP BEAMS

TYPE	BEAM SIZE	BOTTOM REINFORCEMENT		TOP REINFORCEMENT			SIDE BARS	STIRRUPS		NO OF LEGS
	MM X MM	(A)	(B)	(C)	(D)	(E)	(F)	AT SUPPORT	AT MID SPAN	
		STRAIGHT	EXTRA AT MID SPAN	STRAIGHT	EXTRA AT SUPPORT	EXTRA AT SUPPORT	EACH SIDE			
STB1	250 X 800	3T16	————	3T16+3T16	————	————	2T12 	T10-100	T10-150	2

SCHEDUEL FONDATION

Government Of Ras Al Khaimah
R.A.K. Municipality
Buildings Administration



حكومة رأس الخيمة
دائرة البلدية
إدارة المباني

Approved On

اعتمد في


23 October 2025

Building Permit #:
PRMT-25-0004252

Approved By:




Client	FAHAD SULAIMAN ABDULLA ALSHEHI		
Project	DOUBLE STORY VILLA		
Drg.Title	FOUNDATION SCHEDULE		
Area	SHEIKH ZAYED	Floortype	
Case ID.	3046012	Draw. Type.	STRC
Sec No.	1	Com. No.	
Block No.		Plot No.	412030315
Bldg. No.	BLD-25-03488	Floor No.	
Date	10/2025	Sht. No.	S03
Scale	1/100	Job No.	
G.Manager		Architect	Designed By
ENG AYMEN		ENG IMEN	M. AHMED

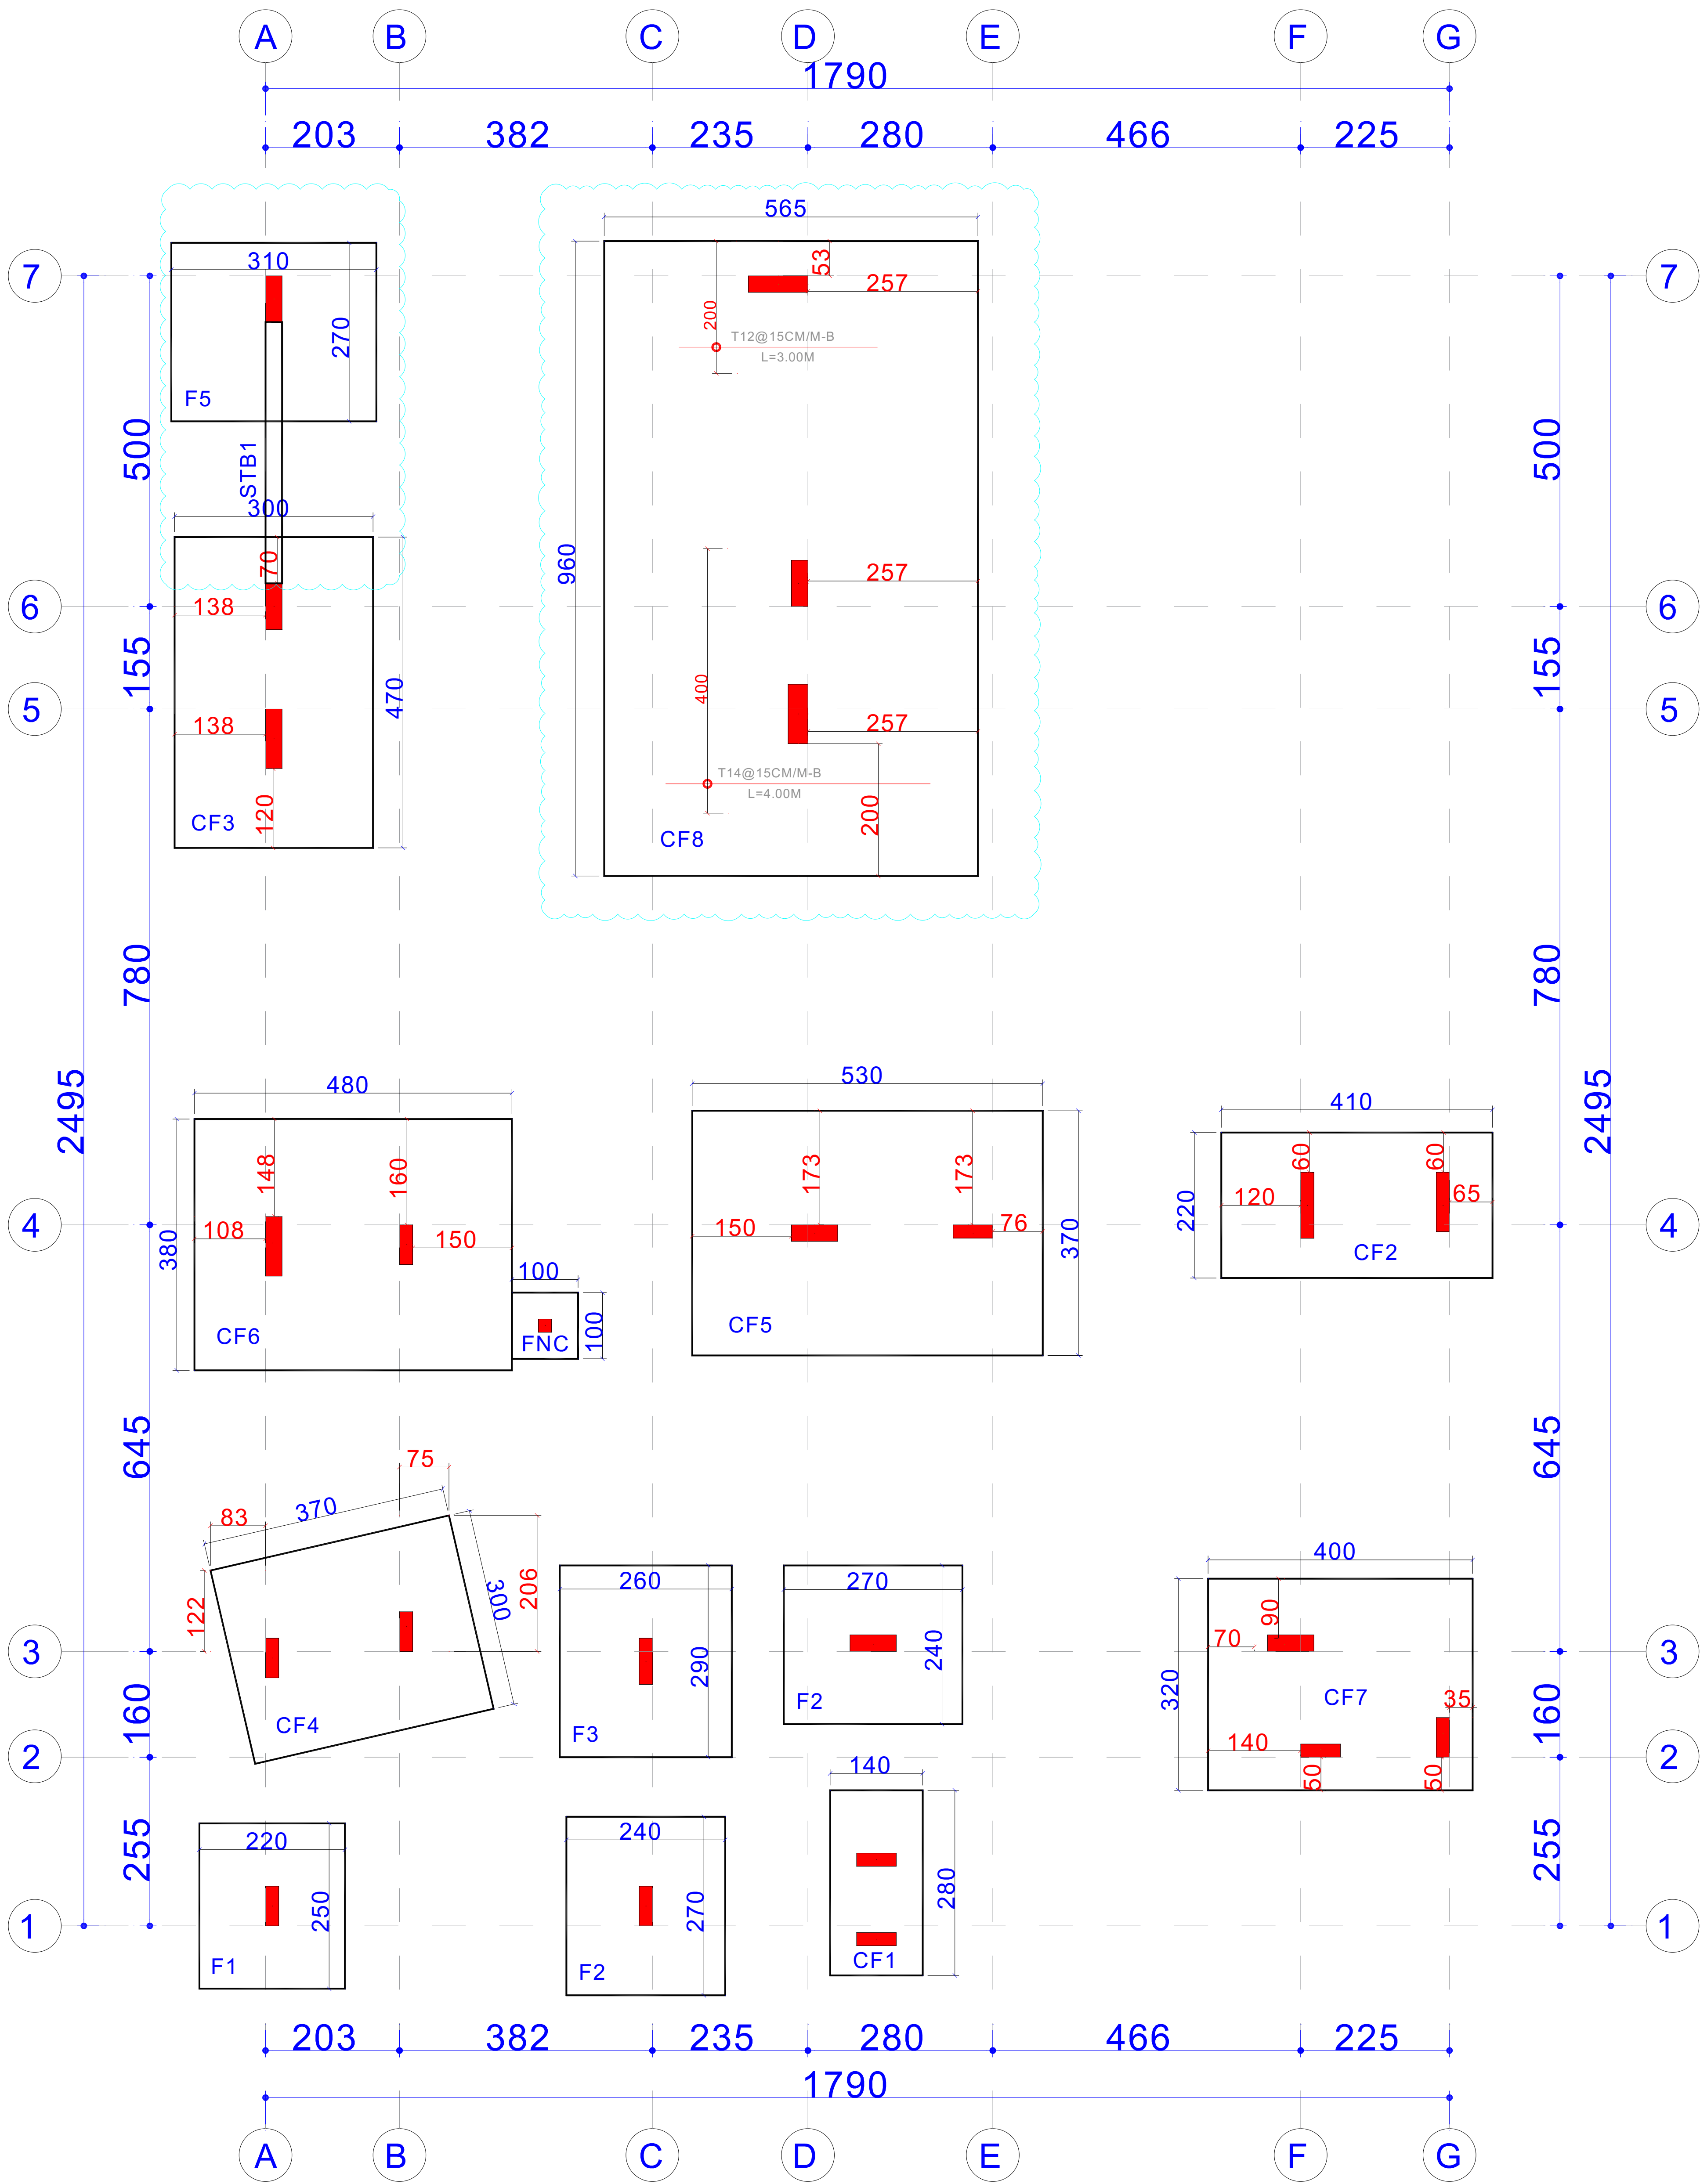

FONDATION LAYOUT

STRUCTURAL NOTES		CONCRETE COVERS :	
ACI 318-11		Foundations cover = 75mm	
F'C/FCU = 28/35 N/mm2		Columns cover = 40mm	
FY = 460N/mm2		Walls cover = 30mm	
FYt = 420N/mm2		Beams cover = 40mm	
		Slabs & Stairs cover = 25mm	



Client	FAHAD SULAIMAN ABDULLA ALSHEHI		
Project	DOUBLE STORY VILLA		
Drg.Title	FOUNDATION LAYOUT		
Area	SHEIKH ZAYED	Floortype	
Case ID.	3046012	Draw. Type.	STRC
Sec No.	1	Com. No.	
Block No.		Plot No.	412030315
Bldg. No.	BLD-25-03488	Floor No.	
Date	10/2025	Sht. No.	S02
Scale	1/100	Job No.	
G.Manager	Architect	Designed By	
ENG AYMEN	ENG IMEN	M. AHMED	