GROUND FLOOR LEVEL	GFL
FRIST FLOOR FINSHING	FFL
TOP OF CONCRETE	TOC
TOP OF PARAPET	TOP

Govemment Of Ras Al Khaimah
R.A.K. Municipality
Buildings Administration

حكومة رأس الخيمة
دائرة البلدية
إدارة المباني

Approved On — اعتمد في

19 August 2025

Building Permit #: PRMT-25-0004269

Appoved By:

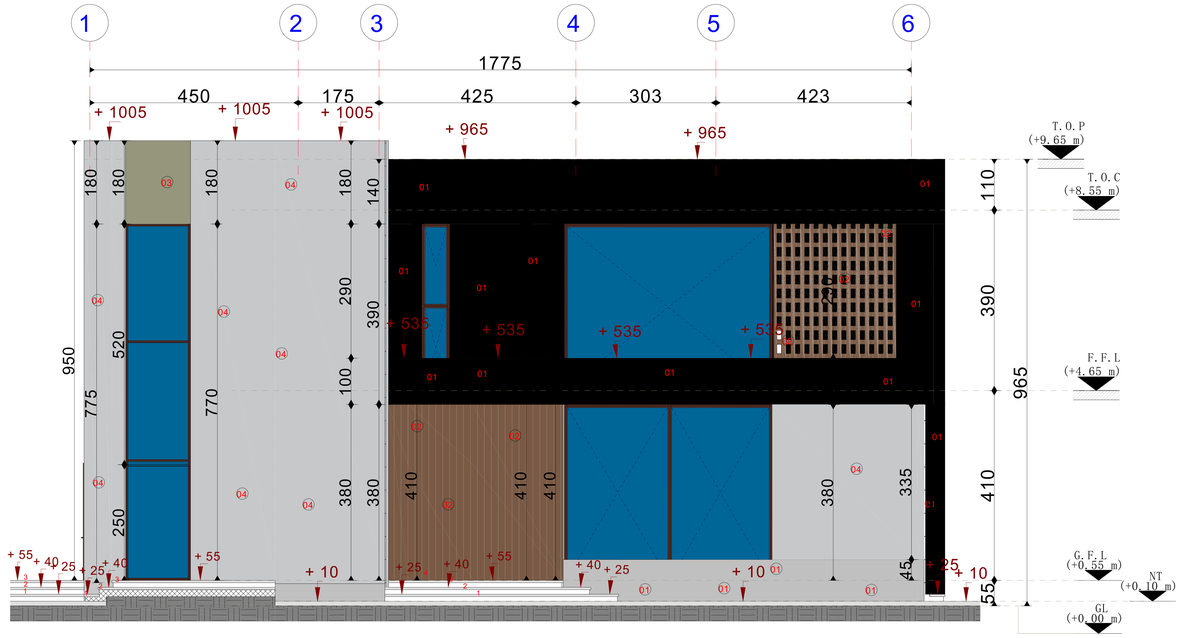

FINSHING	
1	FULL EPOXY PAINT [white]
2	FULL EPOXY BLACK PAINT
3	WOOD Aluminum
4	

Savana
Engineering Consultancy & interior design

Client	ABDULAZIZ TAHNOON AL MANSOORI		
Project	DOUBLE STORY VILLA		
Drg.Title	FRONT ELEVATION		
Area	AWAFI	Floortype	
Case ID.	2955385	Draw. Type.	ARCH
Sec No.	1	Com. No.	
Block No.		Plot No.	406132231
Bldg. No.	BLD-25-03478	Floor No.	
Date	08/2025	Sht. No.	A07
Scale	1/100	Job No.	

G.Manager	Architect	Designed By
ENG AYMEN	ENG IMEN	ENG IMEN

FRONT ELEVATION

GROUND FLOOR LEVEL	GFL
FRIST FLOOR FINSHING	FFL
TOP OF CONCRETE	TOC
TOP OF PARAPET	TOP

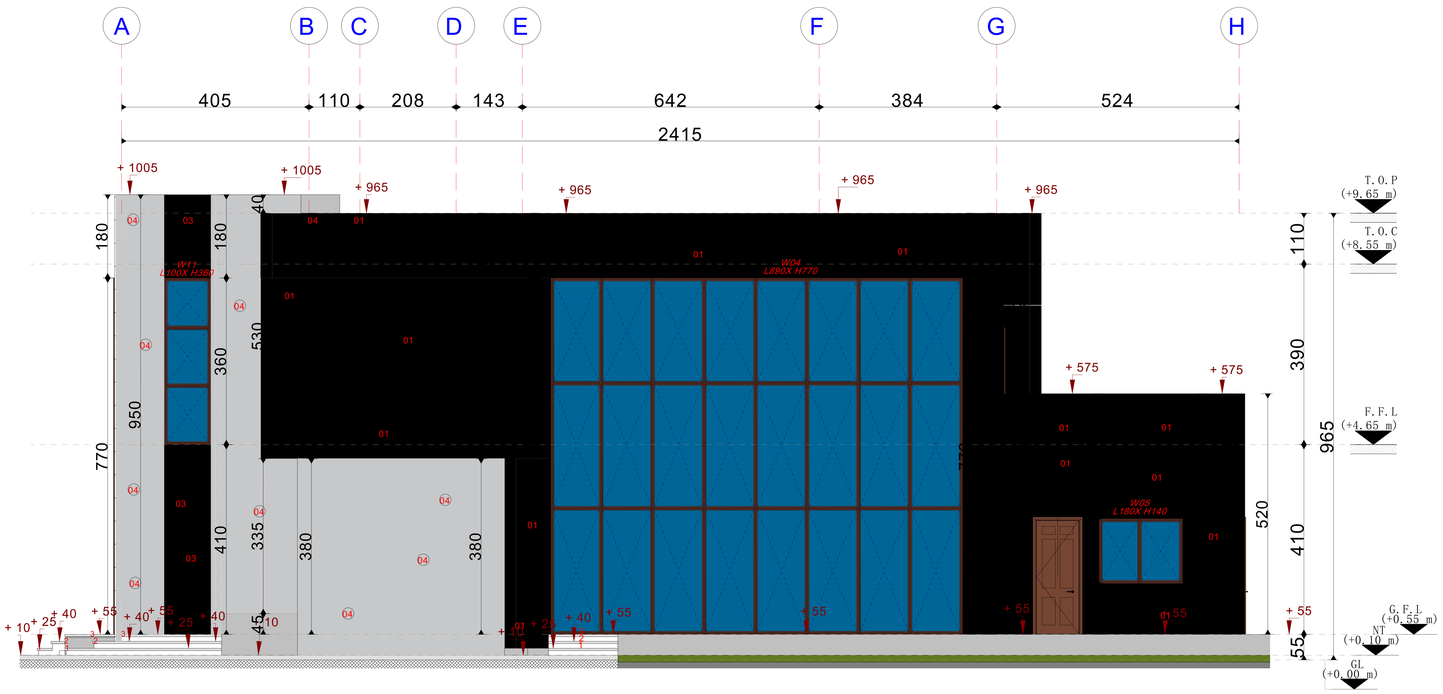

RIGHT ELEVATION

Govemment Of Ras Al Khaimah
R.A.K. Municipality
Buildings Administration

حكومة رأس الخيمة
دائرة البلدية
إدارة المباني

Approved On — اعتمد في

19 August 2025

Building Permit #: PRMT-25-0004269

Appoved By:

FINSHING	
1	FULL EPOXY PAINT [white]
2	FULL EPOXY BLACK PAINT
3	WOOD Aluminum
4	

Savana
Engineering Consultancy & interior design

Client	ABDULAZIZ TAHNOON AL MANSOORI		
Project	DOUBLE STORY VILLA		
Drg.Title	RIGHT ELEVATION		
Area	AWAFI	Floortype	
Case ID.	2955385	Draw. Type.	ARCH
Sec No.	1	Com. No.	
Block No.		Plot No.	406132231
Bldg. No.	BLD-25-03478	Floor No.	
Date	08/2025	Sht. No.	A08
Scale	1/100	Job No.	

G.Manager	Architect	Designed By
ENG AYMEN	ENG IMEN	ENG IMEN

GROUND FLOOR LEVEL	GFL
FRIST FLOOR FINSHING	FFL
TOP OF CONCRETE	TOC
TOP OF PARAPET	TOP

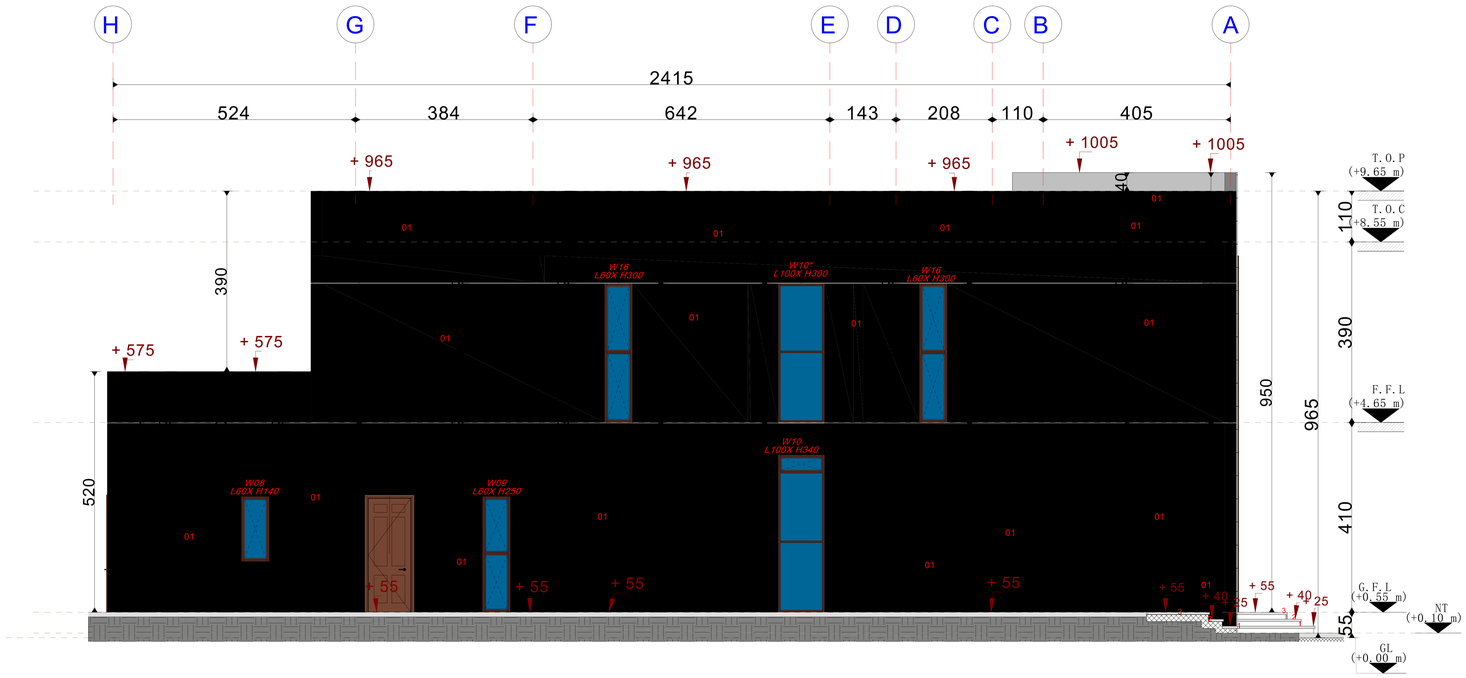

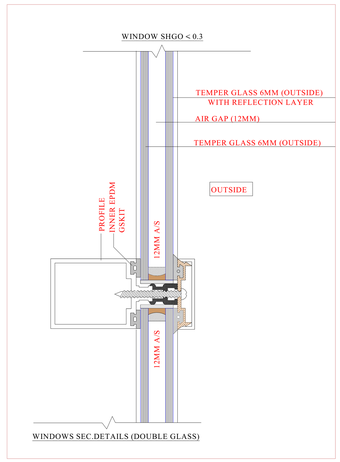

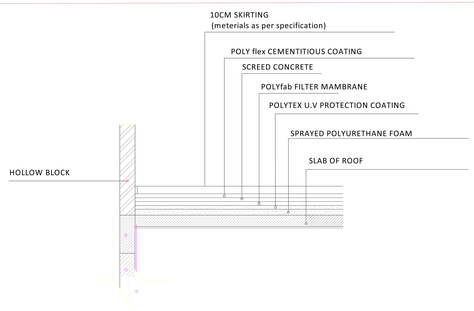

DETAIL FOR COMBO SYSTEM
U-VALUE <0.3 W/M2 K

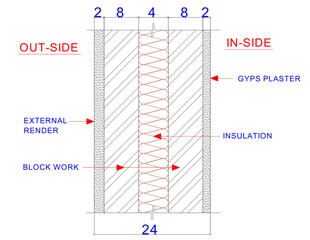

As per E. Walls Predefined Section: W - 1 - A

DETAIL "W1"	TYPICAL FOR EXTERNAL WALL USING INSULATED CONC. BLOCK (200 mm) U-VALUE < 0.5 W/M2 K

Govemment Of Ras Al Khaimah
R.A.K. Municipality
Buildings Administration

حكومة رأس الخيمة
دائرة البلدية
إدارة المباني

Approved On — اعتمد في

19 August 2025

Building Permit #: PRMT-25-0004269

Appoved By:

* Rcc Lintels Must Be Made On Top Of All Doors , Arches And Windows All Of Them Are At Least 0.20 m Thick.
* All Blocks Adjacent To All Doors , Arches And Windows Must Be A Solid Block .

U VALUE AND SHGC

ALL GLASS MUST BE DOUBLE UNITES

GLASS SPECIFICATION:-

U-value (w/m2.k)<_ 1.8

SHADING CO- EFFICIENT (SC) <0.3

FINSHING	
1	FULL EPOXY PAINT [white]
2	FULL EPOXY BLACK PAINT
3	WOOD Aluminum
4	

Savana
Engineering Consultancy & Interior design

Client	ABDULAZIZ TAHNOON AL MANSOORI		
Project	DOUBLE STORY VILLA		
Drg.Title	LIFT ELEVATION		
Area	AWAFI	Floortype	
Case ID.	2955385	Draw. Type.	ARCH
Sec No.	1	Com. No.	
Block No.		Plot No.	406132231
Bldg. No.	BLD-25-03478	Floor No.	
Date	08/2025	Sht. No.	A09
Scale	1/100	Job No.	

G.Manager	Architect	Designed By
ENG AYMEN	ENG IMEN	ENG IMEN

LEFT ELEVATION

GROUND FLOOR LEVEL	GFL
FRIST FLOOR FINSHING	FFL
TOP OF CONCRETE	TOC
TOP OF PARAPET	TOP

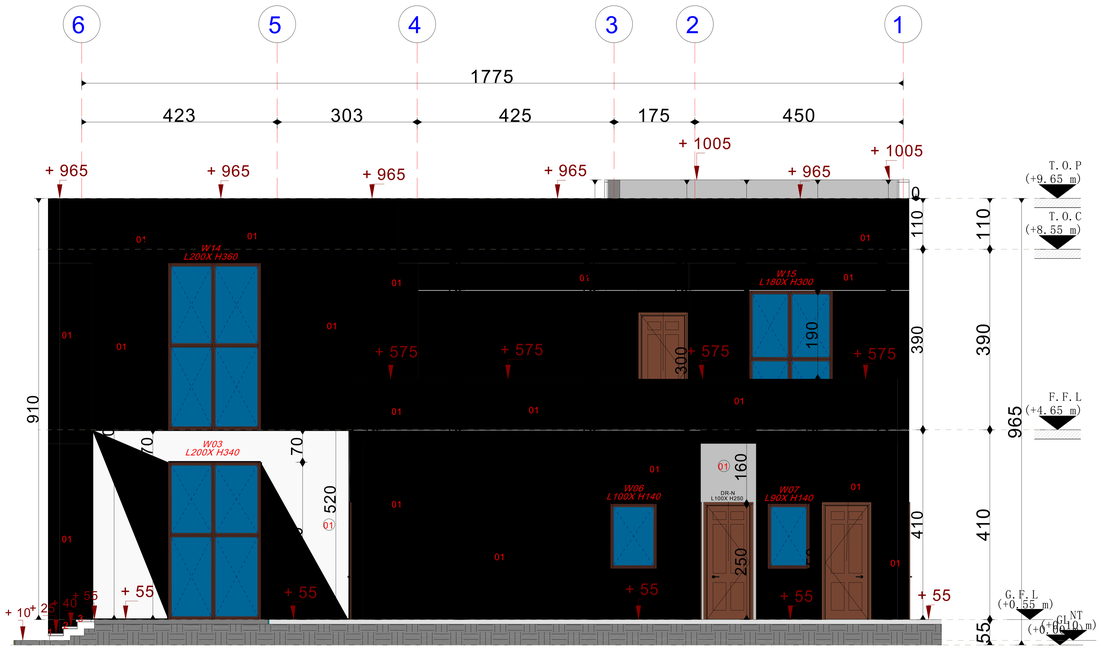

REAR ELEVATION

Govemment Of Ras Al Khaimah
R.A.K. Municipality
Buildings Administration

حكومة رأس الخيمة
دائرة البلدية
إدارة المباني

Approved On — اعتمد في

19 August 2025

Building Permit #: PRMT-25-0004269

Appoved By:

FINSHING

1	FULL EPOXY PAINT [white]
2	FULL EPOXY BLACK PAINT
3	WOOD Aluminum
4	

Savana
Engineering Consultancy & interior design

Client	ABDULAZIZ TAHNOON AL MANSOORI		
Project	DOUBLE STORY VILLA		
Drg.Title	REAR ELEVATION		
Area	AWAFI	Floortype	
Case ID.	2955385	Draw. Type.	ARCH
Sec No.	1	Com. No.	
Block No.		Plot No.	406132231
Bldg. No.	BLD-25-03478	Floor No.	
Date	08/2025	Sht. No.	A10
Scale	1/100	Job No.	

G.Manager	Architect	Designed By
ENG AYMEN	ENG IMEN	ENG IMEN

GROUND FLOOR LEVEL	GFL
FRIST FLOOR FINSHING	FFL
TOP OF CONCRETE	TOC
TOP OF PARAPET	TOP

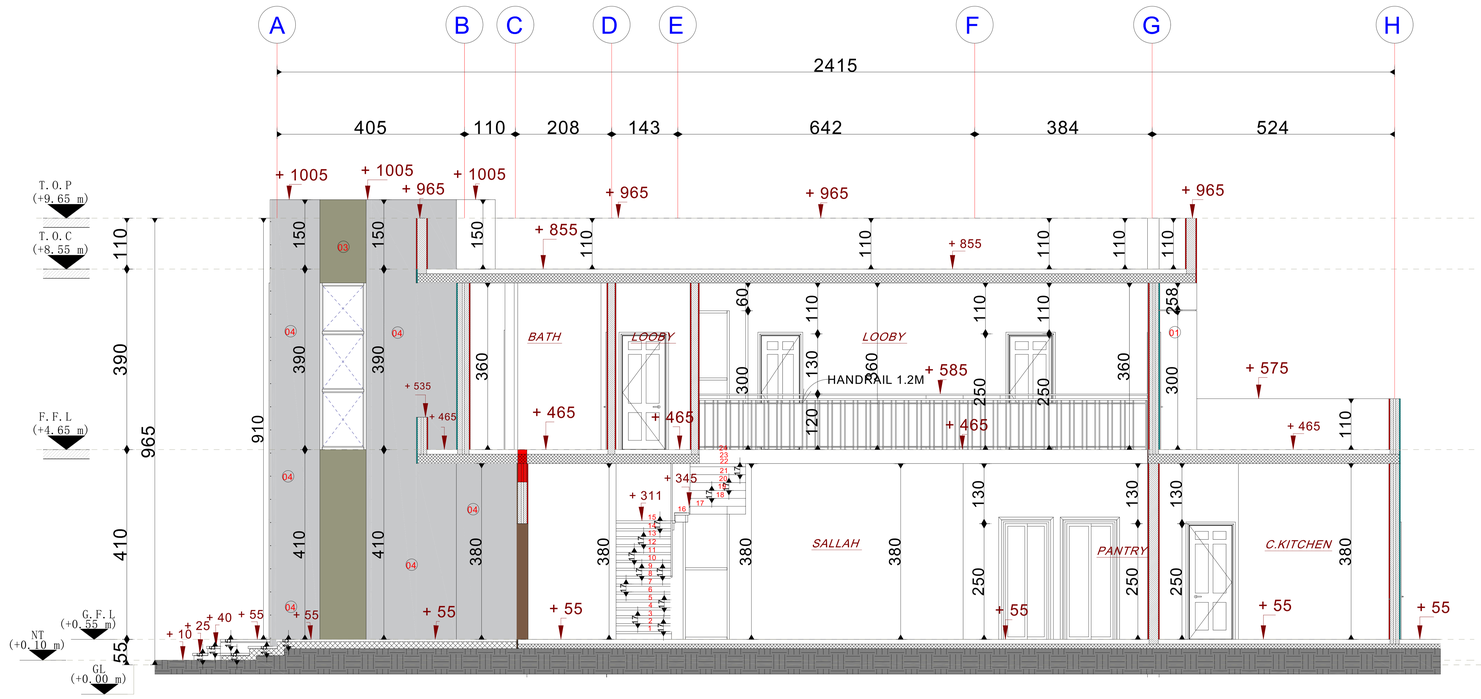

Govemment Of Ras Al Khaimah
R.A.K. Municipality
Buildings Administration

حكومة رأس الخيمة
دائرة البلدية
إدارة المباني

Approved On — اعتمد في

19 August 2025

Building Permit #: PRMT-25-0004269

Appoved By:

ALL GLASS MUST BE DOUBLE UNITES

U-value (w/m2.k)<_ 1.8

SHADING CO- EFFICIENT (SC) <0.3

FINSHING	
1	FULL EPOXY PAINT [white]
2	FULL EPOXY BLACK PAINT
3	WOOD Aluminum
4	

Savana
Engineering Consultancy & interior design

Client	ABDULAZIZ TAHNOON AL MANSOORI		
Project	DOUBLE STORY VILLA		
Drg.Title	SECTION A-A		
Area	AWAFI	Floortype	
Case ID.	2955385	Draw. Type.	ARCH
Sec No.	1	Com. No.	
Block No.		Plot No.	406132231
Bldg. No.	BLD-25-03478	Floor No.	
Date	08/2025	Sht. No.	A11
Scale	1/100	Job No.	

G.Manager	Architect	Designed By
ENG AYMEN	ENG IMEN	ENG IMEN

SECTION A-A

GROUND FLOOR LEVEL	GFL
FRIST FLOOR FINSHING	FFL
TOP OF CONCRETE	TOC
TOP OF PARAPET	TOP

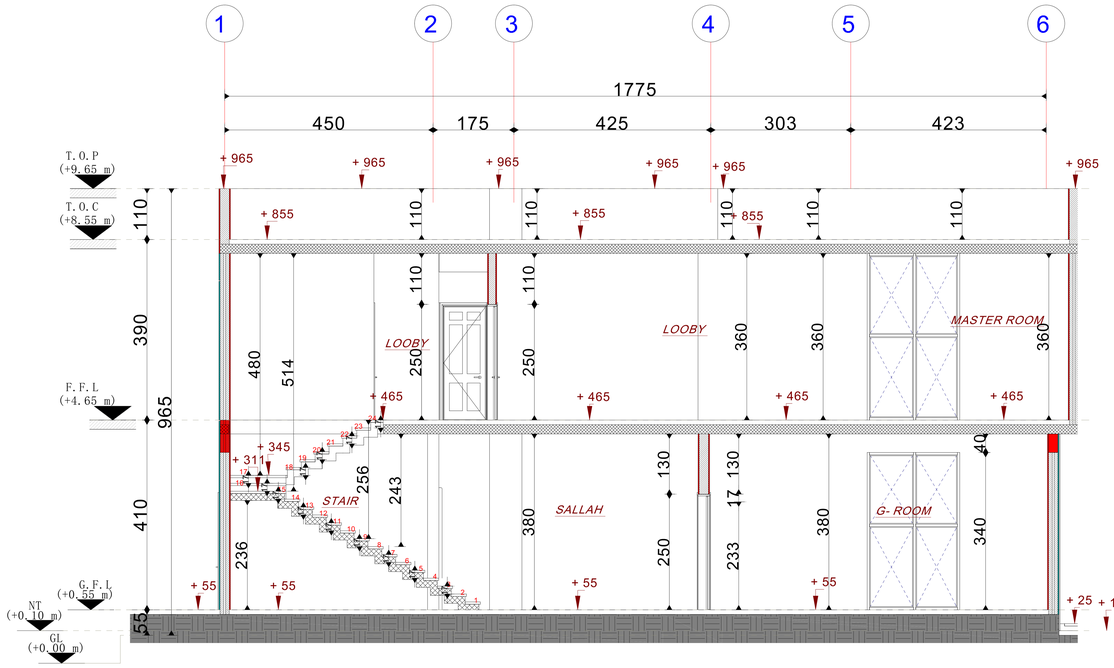

SECTION B-B

Govemment Of Ras Al Khaimah
R.A.K. Municipality
Buildings Administration

حكومة رأس الخيمة
دائرة البلدية
إدارة المباني

Approved On — اعتمد في

19 August 2025

Building Permit #: PRMT-25-0004269

Appoved By:

ALL GLASS MUST BE DOUBLE UNITES

GLASS SPECIFICATION:-

U-value (w/m2.k)<_ 1.8

SHADING CO- EFFICIENT (SC) <0.3

FINSHING	
1	FULL EPOXY PAINT [white]
2	FULL EPOXY BLACK PAINT
3	WOOD Aluminum
4	

Savana
Engineering Consultancy & interior design

Client	ABDULAZIZ TAHNOON AL MANSOORI		
Project	DOUBLE STORY VILLA		
Drg.Title	SECTION B-B		
Area	AWAFI	Floortype	
Case ID.	2955385	Draw. Type.	ARCH
Sec No.	1	Com. No.	
Block No.		Plot No.	406132231
Bldg. No.	BLD-25-03478	Floor No.	
Date	08/2025	Sht. No.	A12
Scale	1/100	Job No.	

G.Manager	Architect	Designed By
ENG AYMEN	ENG IMEN	ENG IMEN

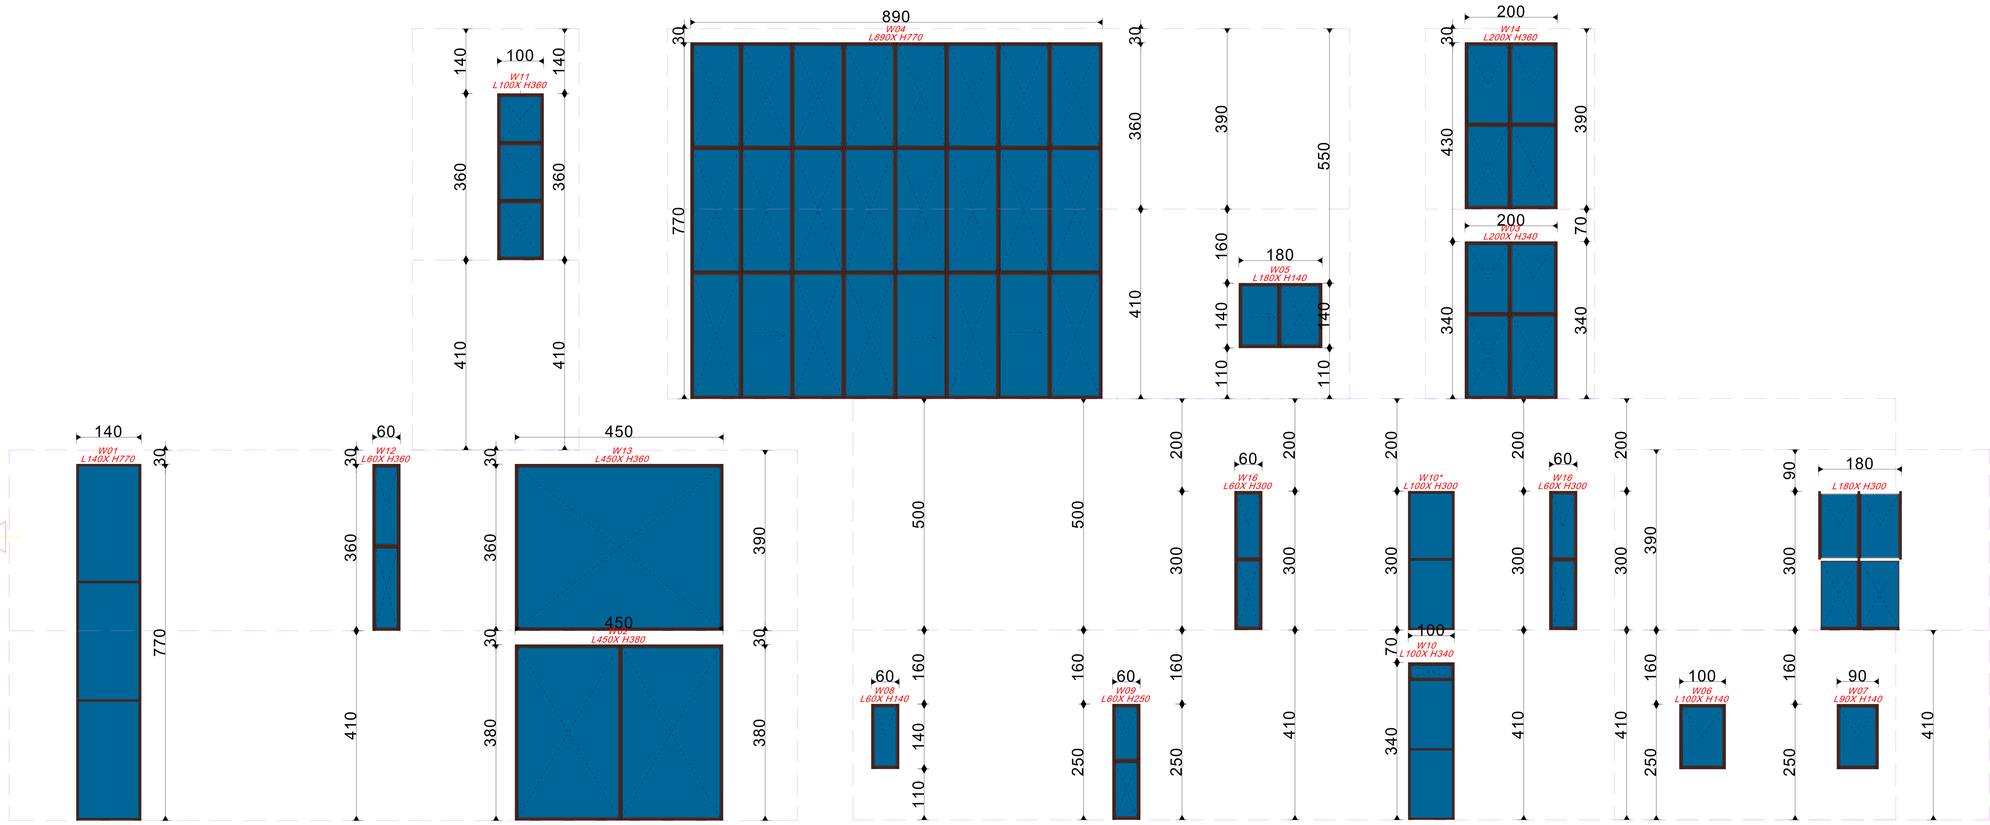

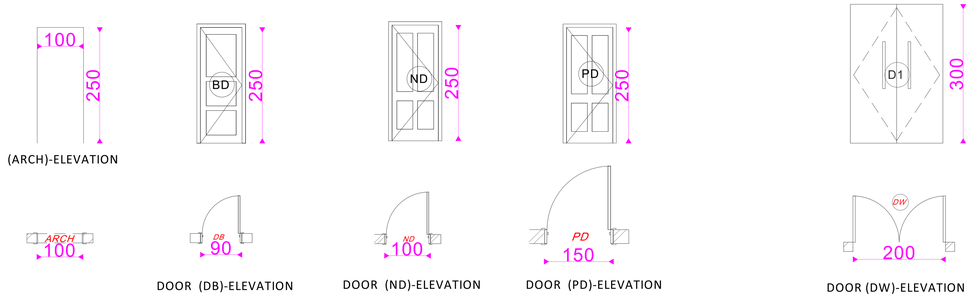

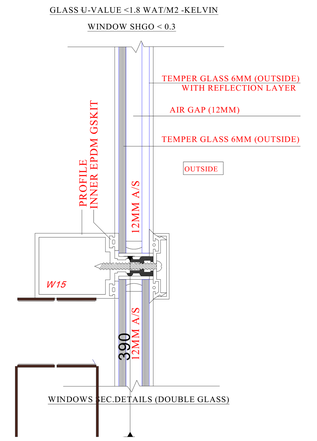

Govemment Of Ras Al Khaimah
R.A.K. Municipality
Buildings Administration

حكومة رأس الخيمة
دائرة البلدية
إدارة المباني

Approved On — اعتمد في

25 August 2025

Building Permit #: PRMT-25-0004269

Appoved By:

ALL GLASS MUST BE DOUBLE UNITES

GLASS SPECIFICATION:-

U-value (w/m2.k)<_ 1.8

SHADING CO- EFFICIENT (SC) <0.3

Savana
Engineering Consultancy & interior design

Client	ABDULAZIZ TAHNOON AL MANSOORI		
Project	DOUBLE STORY VILLA		
Drg.Title	Opening Details		
Area	AWAFI	Floortype	
Case ID.	2955385	Draw. Type.	ARCH
Sec No.	1	Com. No.	
Block No.		Plot No.	406132231
Bldg. No.	BLD-25-03478	Floor No.	
Date	08/2025	Sht. No.	A13
Scale	1/100	Job No.	

G.Manager	Architect	Designed By
ENG AYMEN	ENG IMEN	ENG IMEN

OPENNING DETAILS

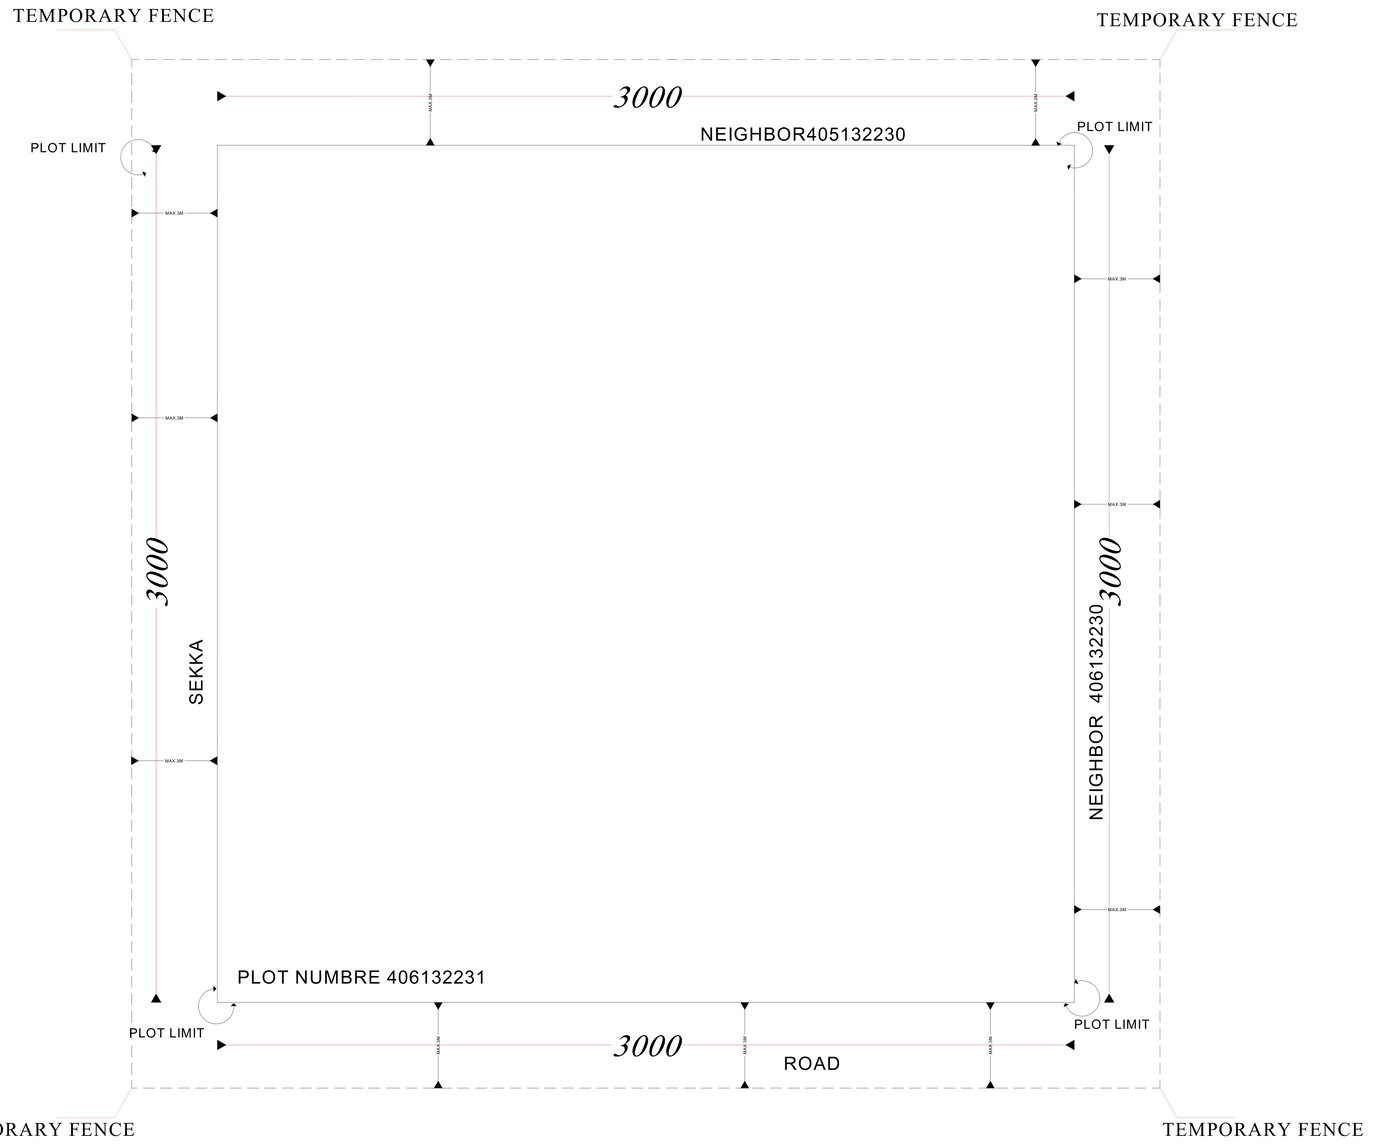

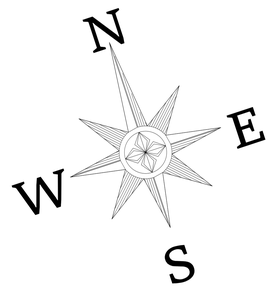

Govemment Of Ras Al Khaimah
R.A.K. Municipality
Buildings Administration

حكومة رأس الخيمة
دائرة البلدية
إدارة المباني

Approved On — اعتمد في

19 August 2025

Building Permit #: PRMT-25-0004269

Appoved By:

Savana
Engineering Consultancy & interior design

Client	ABDULAZIZ TAHNOON AL MANSOORI		
Project	DOUBLE STORY VILLA		
Drg.Title	GENERALE SITE TEMPORARY FENCE		
Area	AWAFI	Floortype	
Case ID.	2955385	Draw. Type.	ARCH
Sec No.	2	Com. No.	
Block No.		Plot No.	406132231
Bldg. No.	BLD-25-03478	Floor No.	
Date	08/2025	Sht. No.	A18
Scale	1/100	Job No.	

G.Manager	Architect	Designed By
ENG AYMEN	ENG IMEN	ENG IMEN

GENERALE SITE TEMPORARY FENCE

Type	SCHEDULE OF FINISHINGS
1	LIGHT IVORY

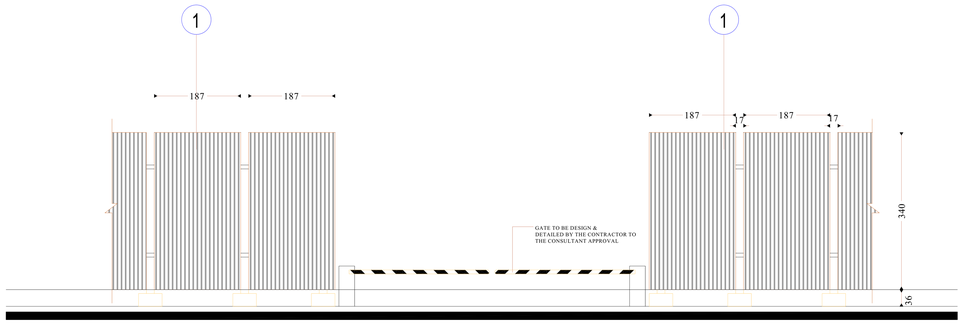

ALUMINIUM TEMPORARY FENCE

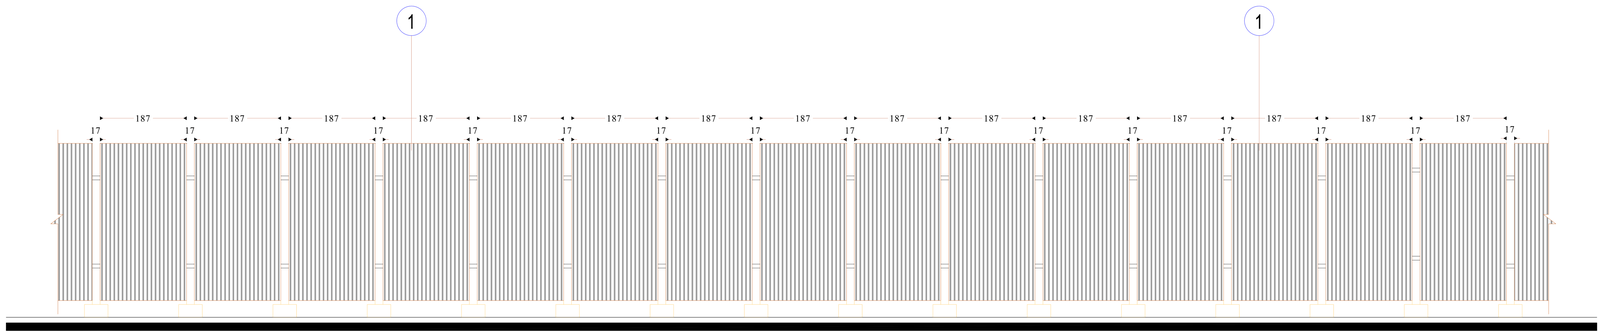

HOARDING ELEVATION

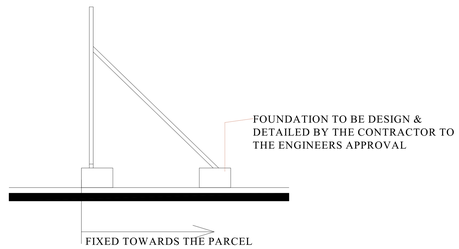

HOARDING SIDE ELEVATION

ALLUMINIUM FENCE

Govemment Of Ras Al Khaimah
R.A.K. Municipality
Buildings Administration

حكومة رأس الخيمة
دائرة البلدية
إدارة المباني

Approved On — اعتمد في

19 August 2025

Building Permit #: PRMT-25-0004269

Appoved By:

Savana
Engineering Consultancy & interior design

Client	ABDULAZIZ TAHNOON AL MANSOORI		
Project	DOUBLE STORY VILLA		
Drg.Title	ALLUMINIUM FENCE		
Area	AWAFI	Floortype	
Case ID.	2955385	Draw. Type.	ARCH
Sec No.	2	Com. No.	
Block No.		Plot No.	406132231
Bldg. No.	BLD-25-03478	Floor No.	
Date	08/2025	Sht. No.	A19
Scale	1/100	Job No.	

G.Manager	Architect	Designed By
ENG AYMEN	ENG IMEN	ENG IMEN

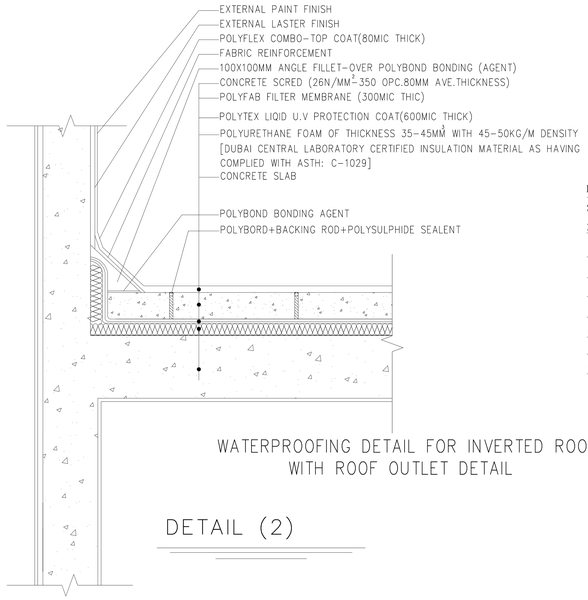

WATERPROOFING DETAIL FOR INVERTED ROOF
WITH ROOF OUTLET DETAIL

DETAIL (2)

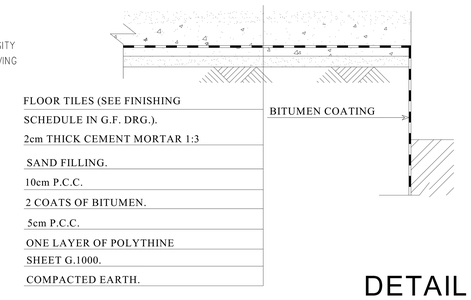

DETAIL (4)

ENTRANCE STEPS DETAIL

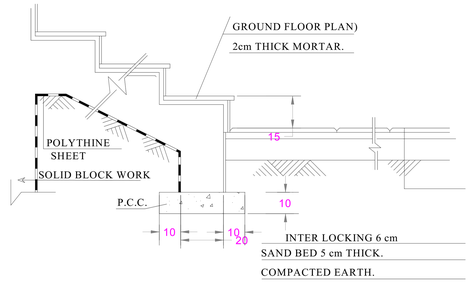

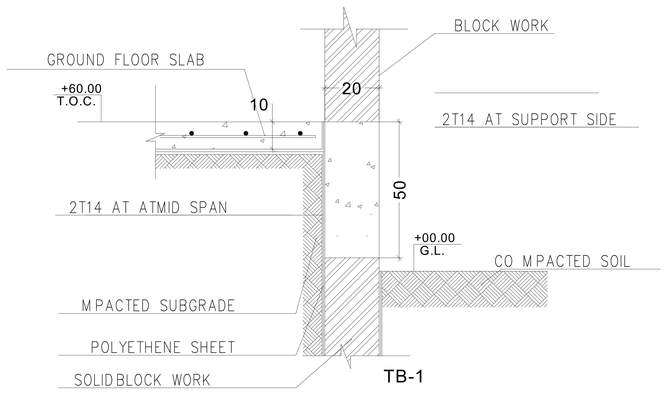

DETAIL (3)

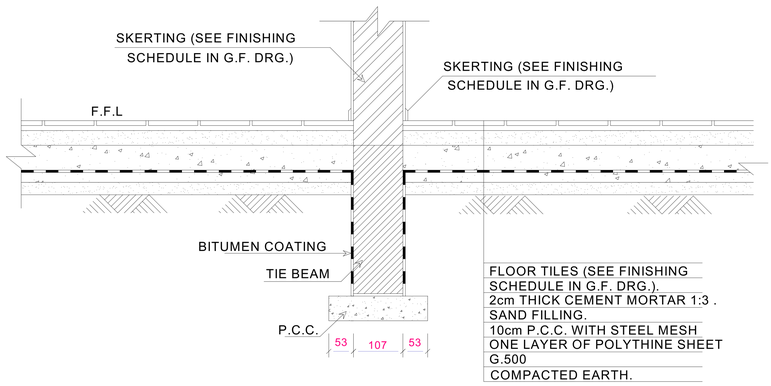

DETAIL (1)

GENERALE DETAILS

Govemment Of Ras Al Khaimah
R.A.K. Municipality
Buildings Administration
حكومة رأس الخيمة
دائرة البلدية
إدارة المباني

Approved On — اعتمد في

19 August 2025

Building Permit #: PRMT-25-0004269

Appoved By:

Savana
Engineering Consultancy & interior design

Client	ABDULAZIZ TAHNOON AL MANSOORI		
Project	DOUBLE STORY VILLA		
Drg.Title	GENERALE DETAILS		
Area	AWAFI	Floortype	
Case ID.	2955385	Draw. Type.	ARCH
Sec No.	2	Com. No.	
Block No.		Plot No.	406132231
Bldg. No.	BLD-25-03478	Floor No.	
Date	08/2025	Sht. No.	A20
Scale	1/100	Job No.	

G.Manager	Architect	Designed By
ENG AYMEN	ENG IMEN	ENG IMEN

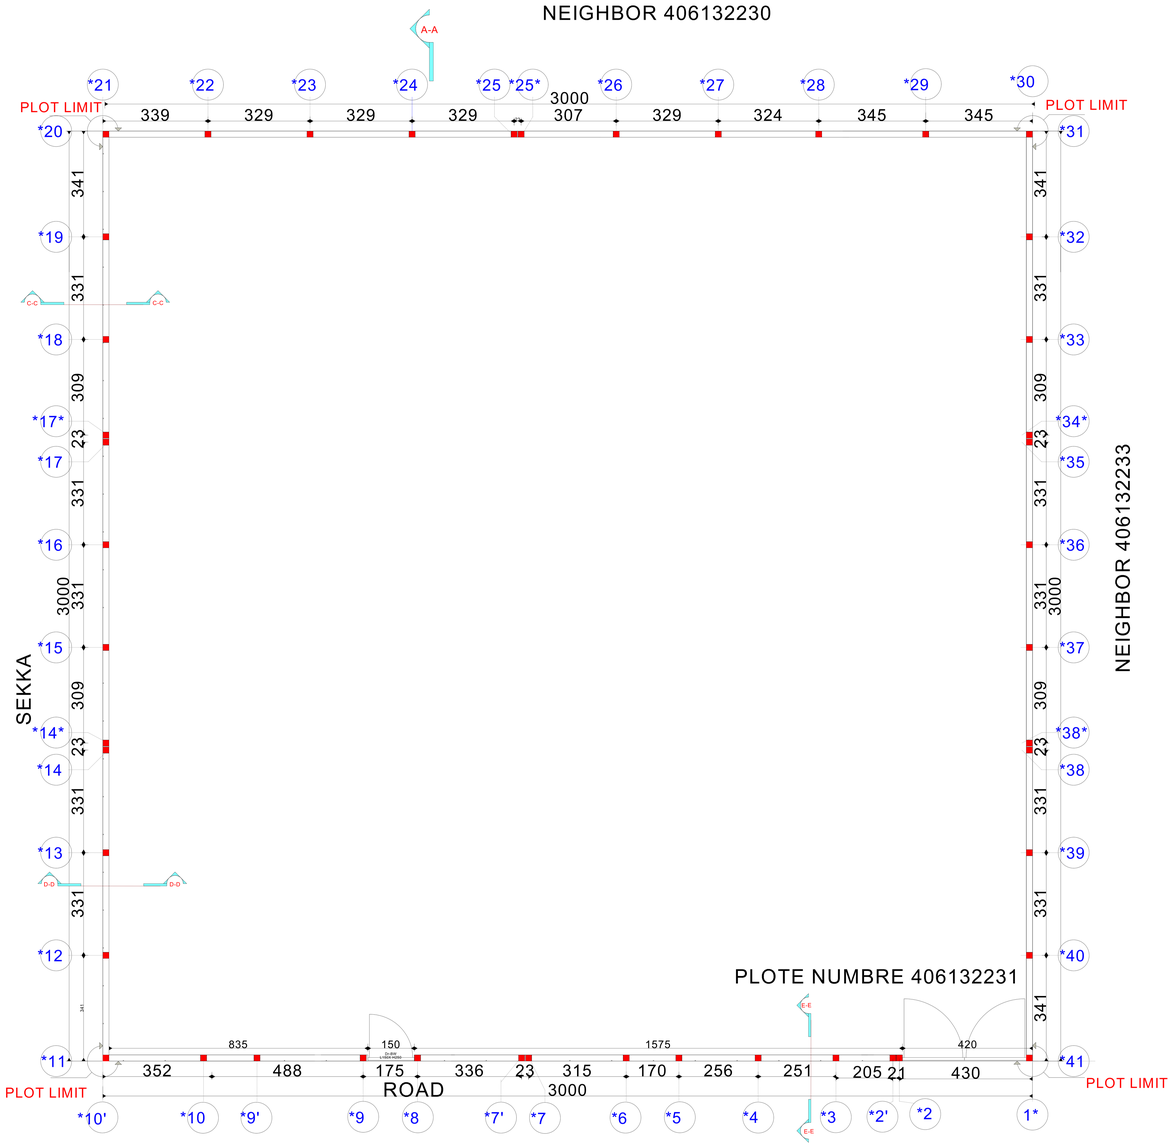

N

W E

S

Govemment Of Ras Al Khaimah
R.A.K. Municipality
Buildings Administration

حكومة رأس الخيمة
دائرة البلدية
إدارة المباني

Approved On — اعتمد في

19 August 2025

Building Permit #: PRMT-25-0004269

Appoved By:

B.WALL SITE PLAN

Savana
Engineering Consultancy & Interior design

Client	ABDULAZIZ TAHNOON AL MANSOORI		
Project	DOUBLE STORY VILLA		
Drg.Title	BOUNDARY WALL LAYOUT PLAN		
Area	AWAFI	Floortype	
Case ID.	2955385	Draw. Type.	ARCH
Sec No.	2	Com. No.	
Block No.		Plot No.	406132231
Bldg. No.	FNC-25-001807	Floor No.	
Date	08/2025	Sht. No.	A15
Scale	1/100	Job No.	

G.Manager	Architect	Designed By
ENG AYMEN	ENG IMEN	ENG IMEN

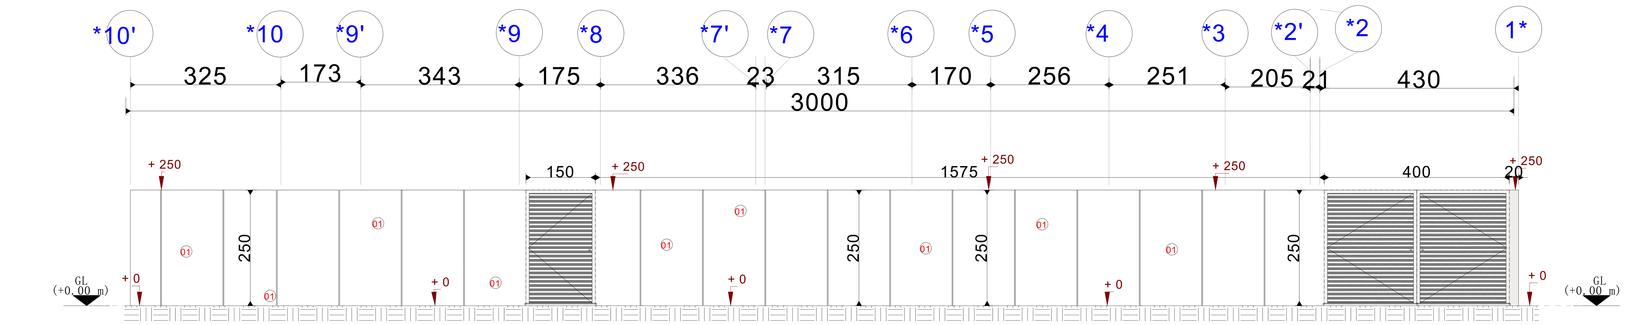

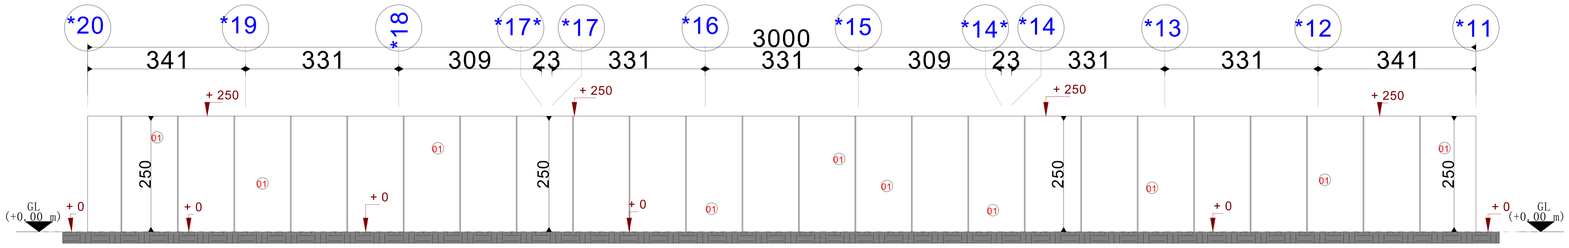

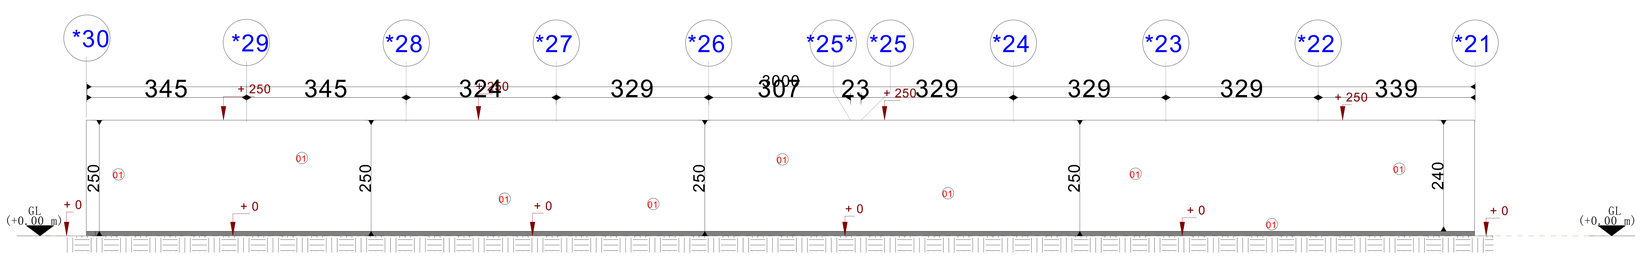

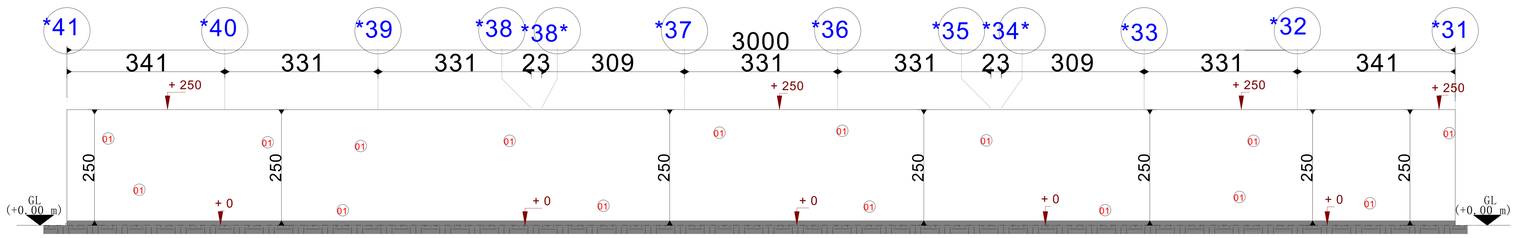

B.WALL ELEVATION

Govemment Of Ras Al Khaimah
R.A.K. Municipality
Buildings Administration

حكومة رأس الخيمة
دائرة البلدية
إدارة المباني

Approved On — اعتمد في

19 August 2025

Building Permit #: PRMT-25-0004269

Appoved By:

Savana
Engineering Consultancy & interior design

Client	ABDULAZIZ TAHNOON AL MANSOORI		
Project	DOUBLE STORY VILLA		
Drg.Title	Proposed Boundary Wall Elevations		
Area	AWAFI	Floortype	
Case ID.	2955385	Draw. Type.	ARCH
Sec No.	2	Com. No.	
Block No.		Plot No.	406132231
Bldg. No.	FNC-25-001807	Floor No.	
Date	08/2025	Sht. No.	A16
Scale	1/100	Job No.	

G.Manager	Architect	Designed By
ENG AYMEN	ENG IMEN	ENG IMEN

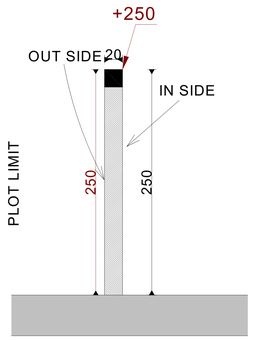

SECTION C-C

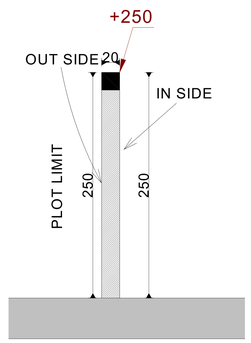

SECTION D-D

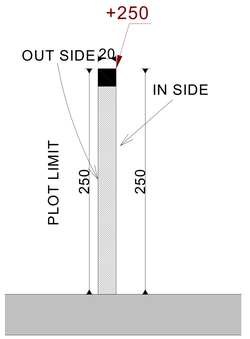

SECTION E-E

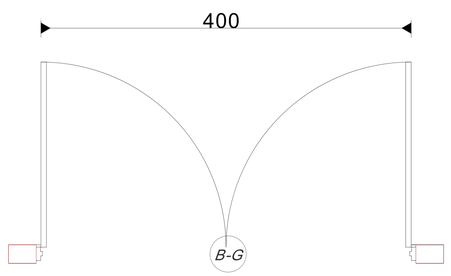

DOOR (BG)-ELEVATION

SCALE 1:50

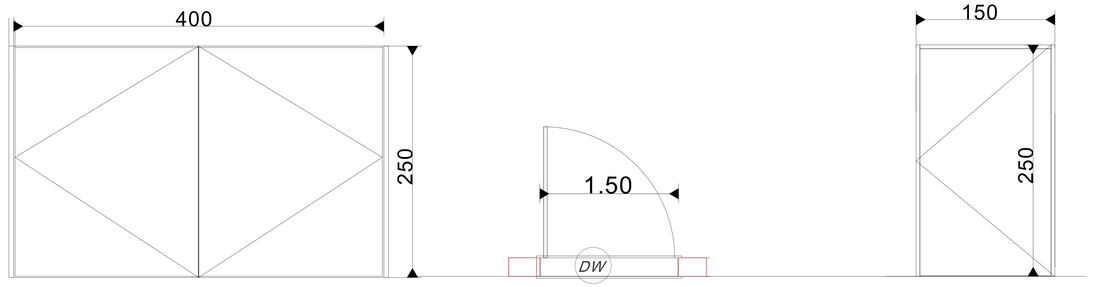

DOOR (DB)-ELEVATION

SCALE 1:50

B.WALL SECTION

Govemment Of Ras Al Khaimah
R.A.K. Municipality
Buildings Administration

حكومة رأس الخيمة
دائرة البلدية
إدارة المباني

Approved On — اعتمد في

19 August 2025

Building Permit #: PRMT-25-0004269

Appoved By:

Savana
Engineering Consultancy & interior design

Client	ABDULAZIZ TAHNOON AL MANSOORI		
Project	DOUBLE STORY VILLA		
Drg.Title	Boundary Wall DETAILS		
Area	AWAFI	Floortype	
Case ID.	2955385	Draw. Type.	ARCH
Sec No.	2	Com. No.	
Block No.		Plot No.	406132231
Bldg. No.	FNC-25-001807	Floor No.	
Date	08/2025	Sht. No.	A17
Scale	1/100	Job No.	

G.Manager	Architect	Designed By
ENG AYMEN	ENG IMEN	ENG IMEN

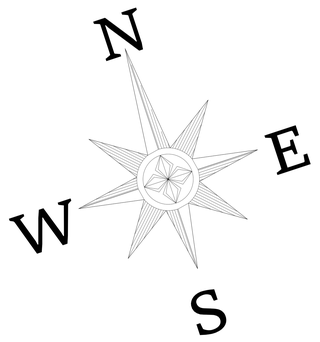

Govemment Of Ras Al Khaimah
R.A.K. Municipality
Buildings Administration

حكومة رأس الخيمة
دائرة البلدية
إدارة المباني

Approved On — اعتمد في

19 August 2025

Building Permit #: PRMT-25-0004269

Appoved By:

Area Statement	
Building Number	BLD-25-03478
Ground Floor Area	308m²
first Floor Area	254m²
Total Building Area	562m²
PLOT AREA ACCORDING TO KRUKI	900m²
BUILD UP RATIO	34%

Savana
Engineering Consultancy & interior design

Client	ABDULAZIZ TAHNOON AL MANSOORI		
Project	DOUBLE STORY VILLA		
Drg.Title	AreaStatement		
Area	AWAFI	Floortype	
Case ID.	2955385	Draw. Type.	ARCH
Sec No.	1	Com. No.	
Block No.		Plot No.	406132231
Bldg. No.	BLD-25-03478	Floor No.	
Date	08/2025	Sht. No.	A-01
Scale	1/100	Job No.	

G.Manager	Architect	Designed By
ENG AYMEN	ENG IMEN	ENG IMEN

AREA STATMENTENT

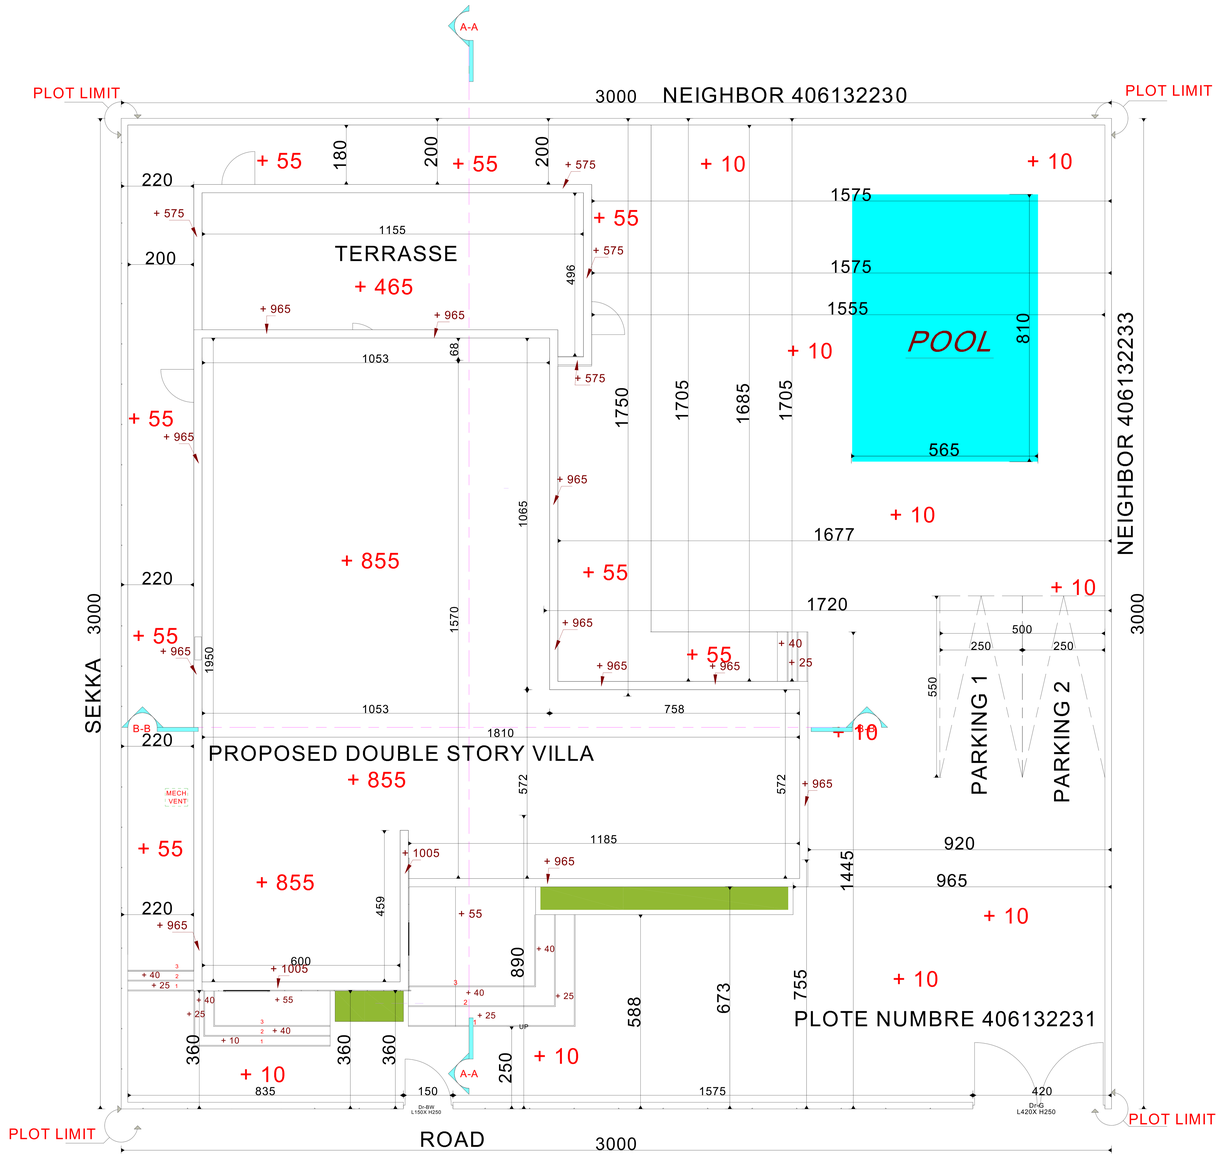

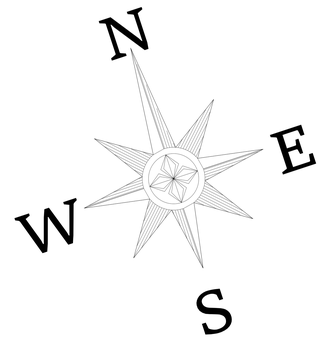

Govvernment Of Ras Al Khaimah
R.A.K. Municipality
Buildings Administration

حكومة رأس الخيمة
دائرة البلدية
إدارة المباني

Approved On — اعتمد في

19 August 2025

Building Permit #: PRMT-25-0004269

Appoved By:

Note :-

* Rcc Lintels Must Be Made On Top Of All Doors , Arches And Windows All Of Them Are At Least 0.20 m Thick.
* All Blocks Adjacent To All Doors , Arches And Windows Must Be A Solid Block .

Savana
Engineering Consultancy & Interior design

Client	ABDULAZIZ TAHNOON AL MANSOORI		
Project	DOUBLE STORY VILLA		
Drg.Title	Site Development Layout Plan		
Area	AWAFI	Floortype	
Case ID.	2955385	Draw. Type.	ARCH
Sec No.	1	Com. No.	
Block No.		Plot No.	406132231
Bldg. No.	BLD-25-03478	Floor No.	
Date	08/2025	Sht. No.	A02
Scale	1/100	Job No.	

G.Manager	Architect	Designed By
ENG AYMEN	ENG IMEN	ENG IMEN

SITE DEVELOPMENT LAYOUT PLAN

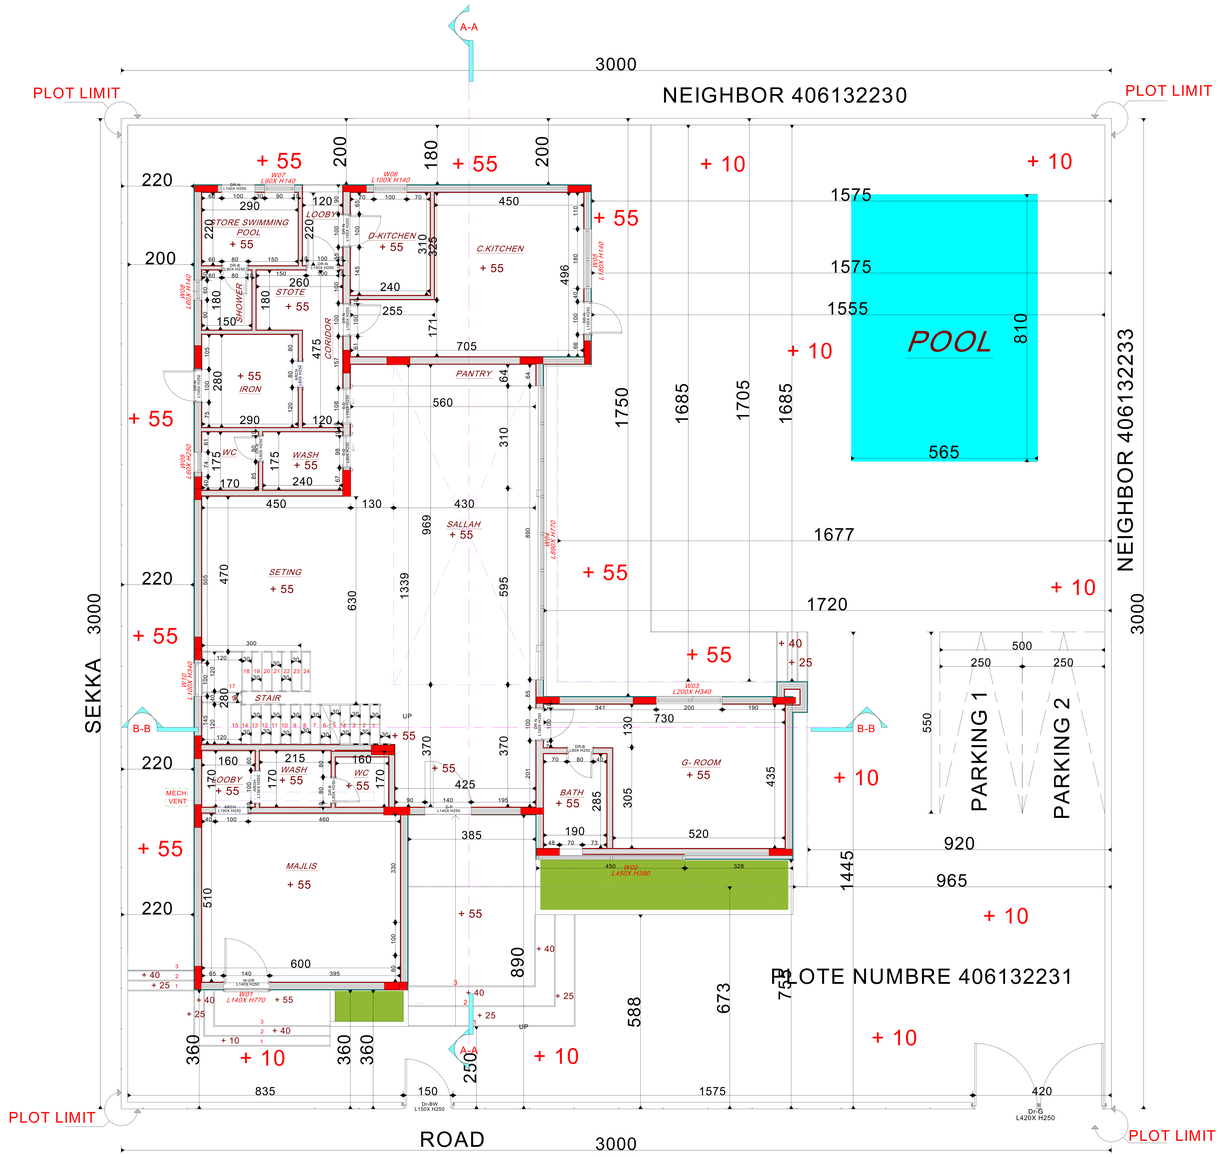

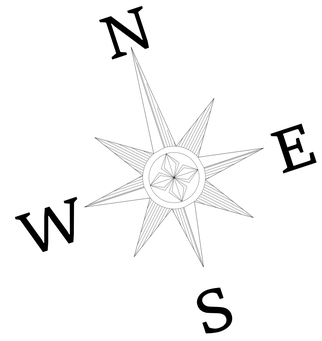

Govemment Of Ras Al Khaimah
R.A.K. Municipality
Buildings Administration

حكومة رأس الخيمة
دائرة البلدية
إدارة المباني

Approved On — اعتمد في

19 August 2025

Building Permit #: PRMT-25-0004269

Appoved By:

Savana
Engineering Consultancy & interior design

Client	ABDULAZIZ TAHNOON AL MANSOORI		
Project	DOUBLE STORY VILLA		
Drg.Title	SITE SETTING PLAN		
Area	AWAFI	Floortype	
Case ID.	2955385	Draw. Type.	ARCH
Sec No.	1	Com. No.	
Block No.		Plot No.	406132231
Bldg. No.	BLD-25-03478	Floor No.	
Date	08/2025	Sht. No.	A03
Scale	1/100	Job No.	

G.Manager	Architect	Designed By
ENG AYMEN	ENG IMEN	ENG IMEN

SITE SETTING PLAN

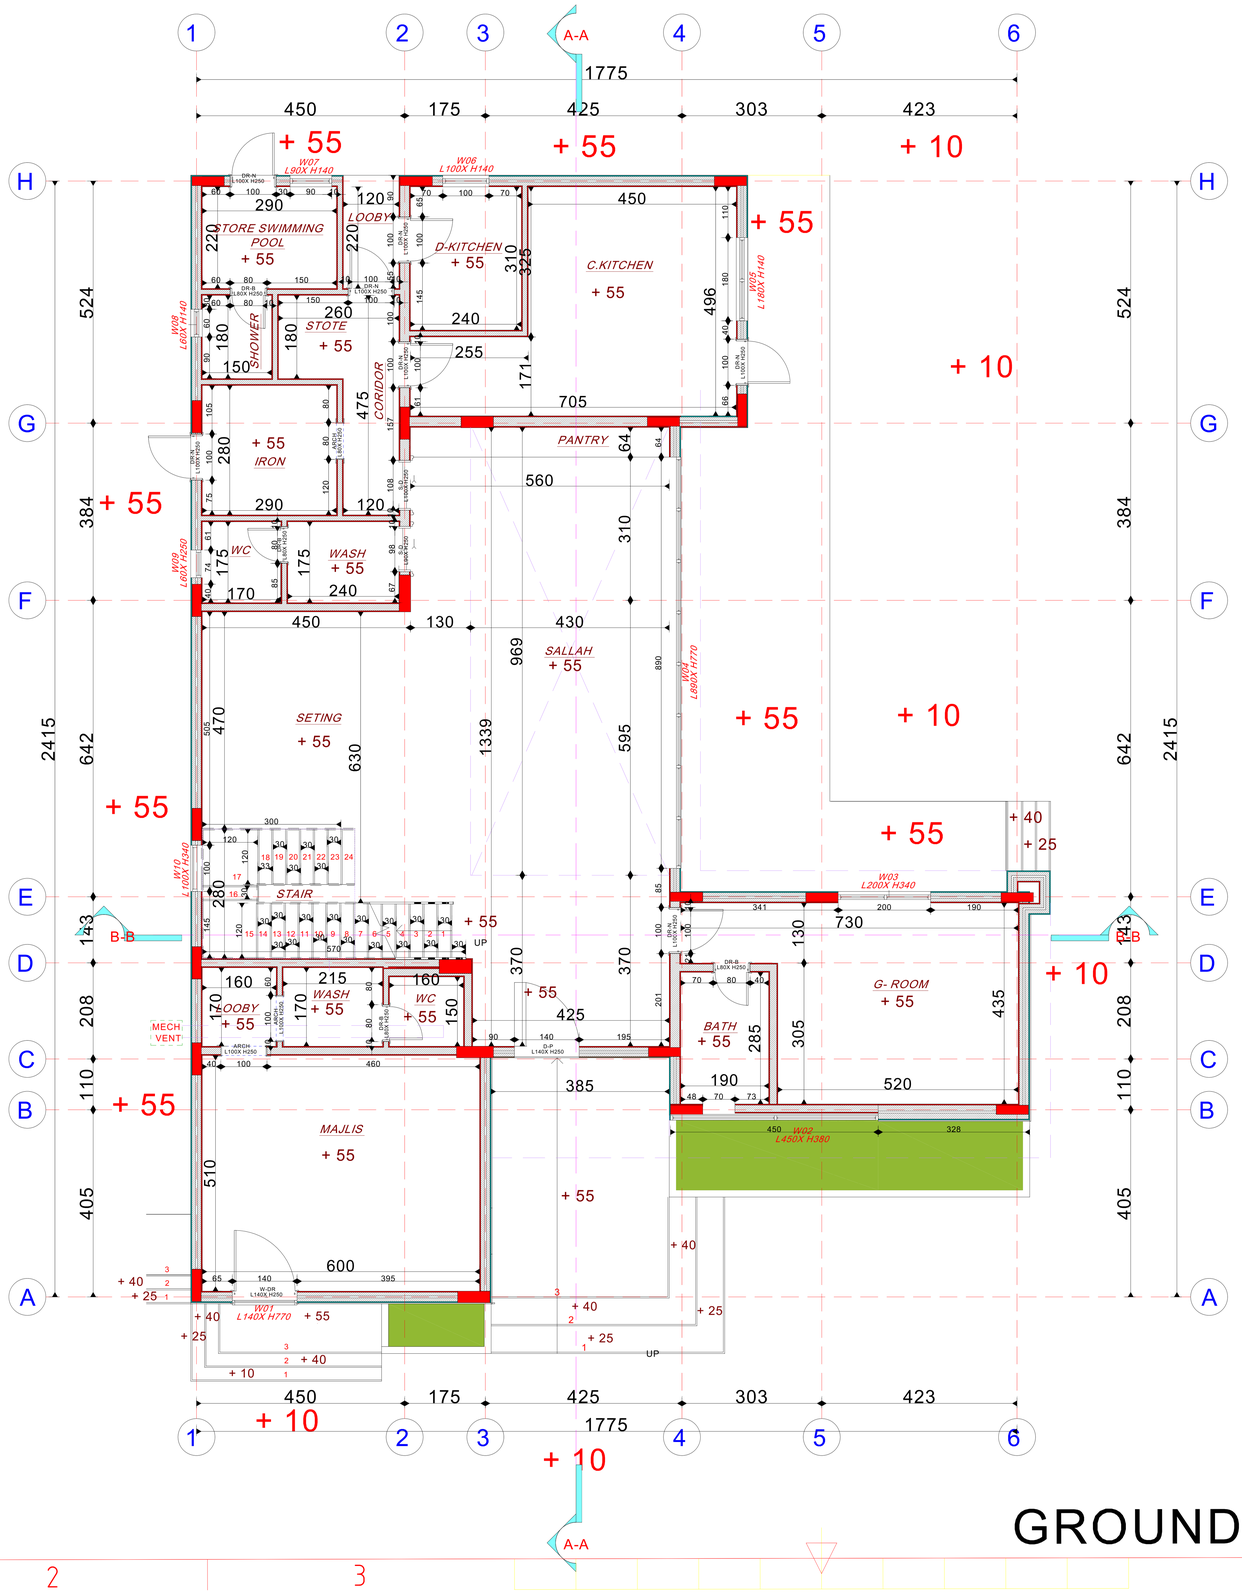

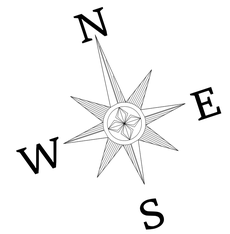

FINISHING FOR VERANDAH	FINISHING FOR DRESSING AREA	FINISHING FOR BATH,WC & WASH
F3 Marble Tiles	F2 Ceramic Tiles (Non Slippery)	F1 Ceramic glazed tiles
W3 Epoxy paint.	W2 Ceramic tiles up to ceiling	W1 Acrylic emulsion paint
C3 Epoxy paint.	C2 Oil Paint.	C1 Acrylic emulsion paint
	S2 Marble tiles 10cm hight	S1 Ceramic Tiles 10cm hight

FLOORING | WALLS | SKIRTING | CEILING

Govemment Of Ras Al Khaimah
R.A.K. Municipality
Buildings Administration

حكومة رأس الخيمة
دائرة البلدية
إدارة المباني

Approved On — اعتمد في

19 August 2025

Building Permit #: PRMT-25-0004269

Appoved By:

Note :-

* Rcc Lintels Must Be Made On Top Of All Doors , Arches And Windows All Of Them Are At Least 0.20 m Thick.
* All Blocks Adjacent To All Doors , Arches And Windows Must Be A Solid Block .

Rooms	Space	Number
Residential	308	
Commercial		
Industrial		
Goverment		
Resident.-Comm.		
Total		

Savana
Engineering Consultancy & interior design

Client	ABDULAZIZ TAHNOON AL MANSOORI		
Project	DOUBLE STORY VILLA		
Drg.Title	GROUND FLOOR PLAN		
Area	AWAFI	Floortype	G
Case ID.	2955385	Draw. Type.	ARCH
Sec No.	1	Com. No.	
Block No.		Plot No.	406132231
Bldg. No.	BLD-25-03478	Floor No.	01
Date	08/2025	Sht. No.	A04
Scale	1/100	Job No.	

G.Manager	Architect	Designed By
ENG AYMEN	ENG IMEN	ENG IMEN

GROUND FLOOR PLAN

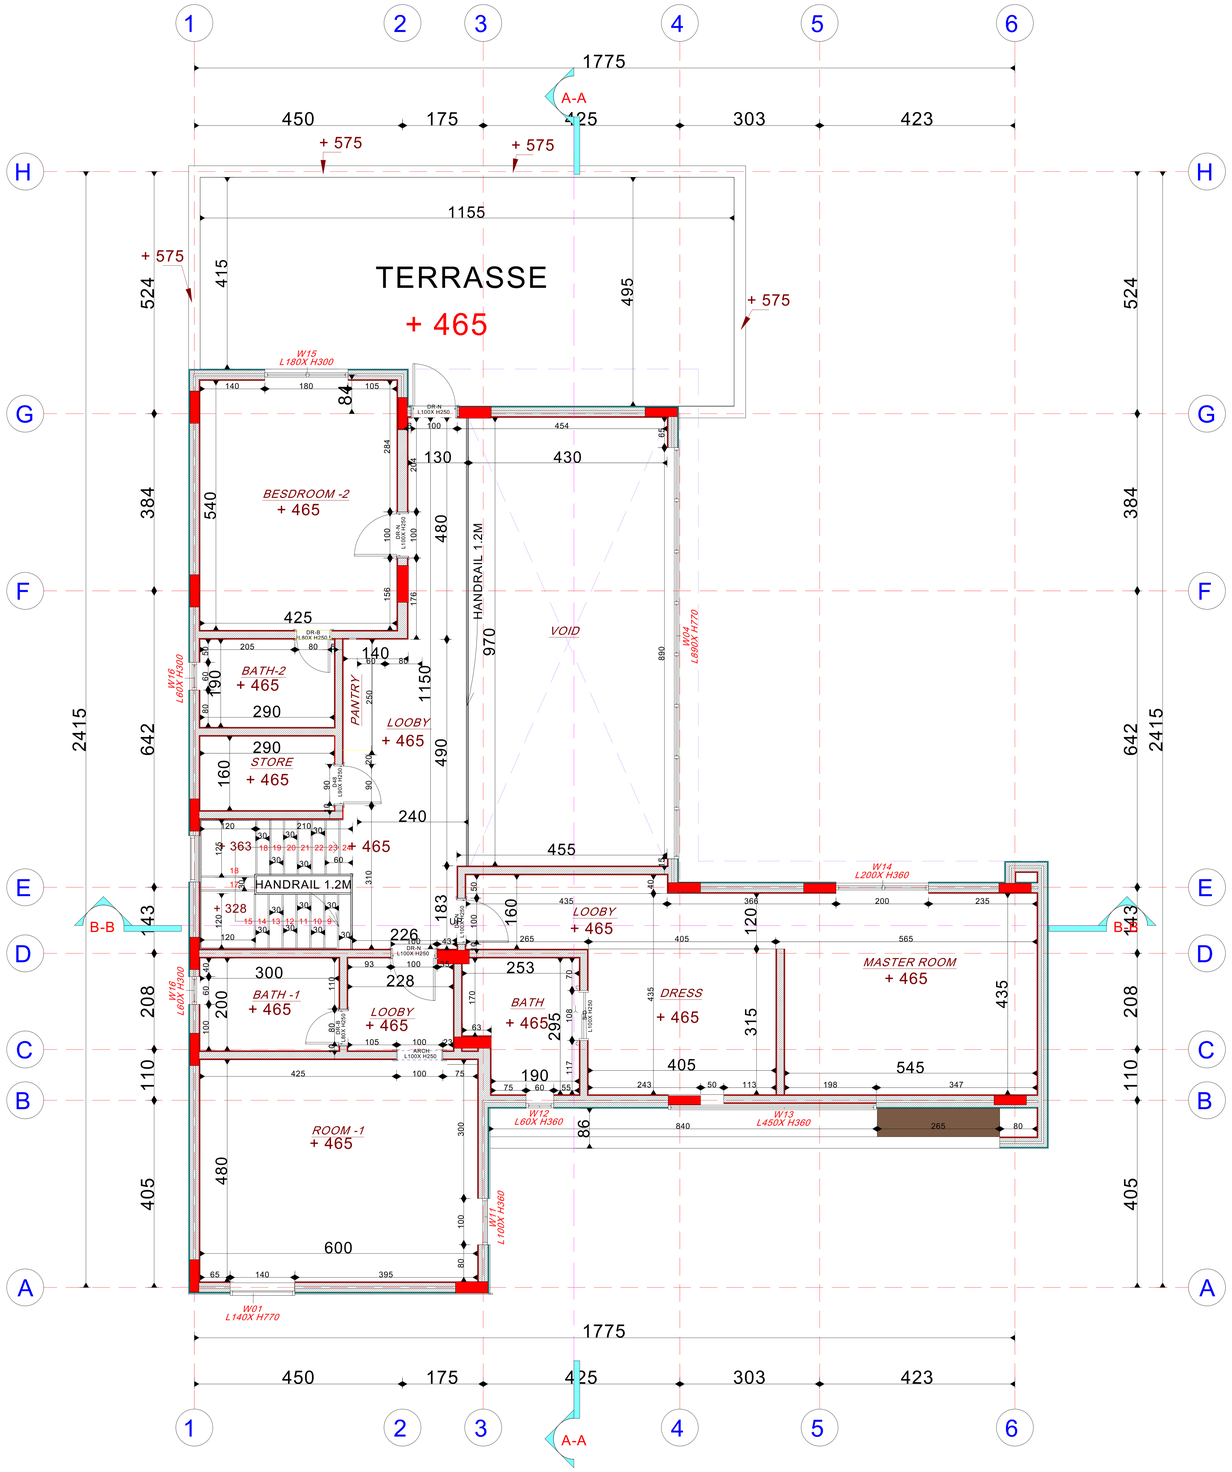

N

E

W

S

FINISHING FOR VERANDAH	FINISHING FOR DRESSING AREA	FINISHING FOR BATH,WC & WASH
FLOORING		
F3 Marble Tiles	F1 Ceramic glazed tiles	F2 Ceramic Tiles (Non Slippery)
WALLS		
W3 Epoxy paint.	W1 Acrylic emulsion paint	W2 Ceramic tiles up to ceiling
SKIRTING		
	S1 Ceramic Tiles 10cm hight	S2 Marble tiles 10cm hight
CEILING		
C3 Epoxy paint.	C1 Acrylic emulsion paint	C2 Oil Paint.

Govemment Of Ras Al Khaimah
R.A.K. Municipality
Buildings Administration

حكومة رأس الخيمة
دائرة البلدية
إدارة المباني

Approved On — اعتمد في

19 August 2025

Building Permit #: PRMT-25-0004269

Approved By:

Note :-

* Rcc Lintels Must Be Made On Top Of All Doors , Arches And Windows All Of Them Are At Least 0.20 m Thick.
* All Blocks Adjacent To All Doors , Arches And Windows Must Be A Solid Block .

Rooms	Space	Number
Residential	254	
Commercial		
Industrial		
Goverment		
Resident.-Comm.		
Total		

Savana
Engineering Consultancy & interior design

Client	ABDULAZIZ TAHNOON AL MANSOORI		
Project	DOUBLE STORY VILLA		
Drg.Title	FIRST FLOOR PLAN		
Area	AWAFI	Floortype	F
Case ID.	2955385	Draw. Type.	ARCH
Sec No.	1	Com. No.	
Block No.		Plot No.	406132231
Bldg. No.	BLD-25-03478	Floor No.	01
Date	08/2025	Sht. No.	A05
Scale	1/100	Job No.	

G.Manager	Architect	Designed By
ENG AYMEN	ENG IMEN	ENG IMEN

FIRST FLOOR PLAN

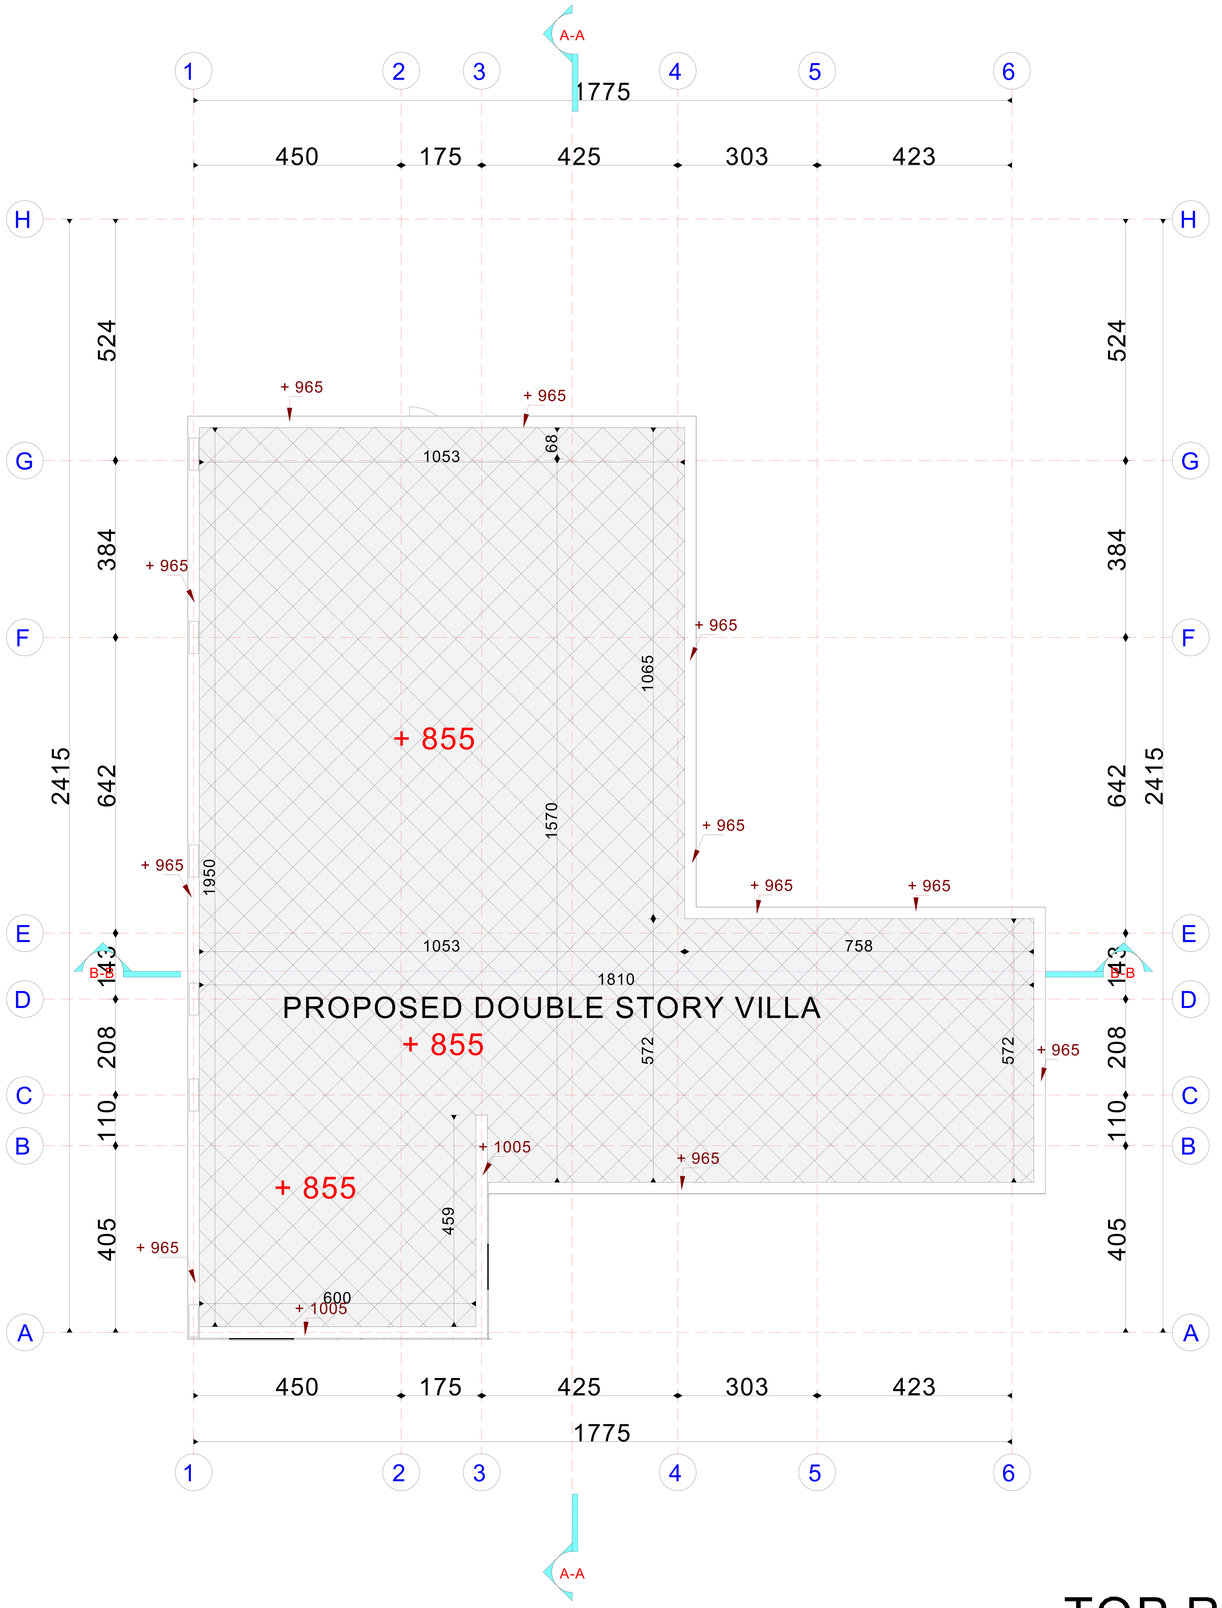

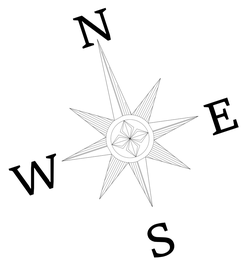

FINISHING FOR VERANDAH		FINISHING FOR DRESSING AREA		FINISHING FOR BATH,WC & WASH	
C3	W3	C1	W1	C2	W2
S2	F3	S1	F1	S2	F2

FLOORING	
F1	Ceramic glazed tiles
F2	Ceramic Tiles (Non Slippery)
F3	Marble Tiles

WALLS	
W1	Acrylic emulsion paint
W2	Ceramic tiles up to ceiling
W3	Epoxy paint.

SKIRTING	
S1	Ceramic Tiles. 10cm hight
S2	Marble tiles 10cm hight

CEILING	
C1	Acrylic emulsion paint
C2	Oil Paint.
C3	Epoxy paint.

Govemment Of Ras Al Khaimah
R.A.K. Municipality
Buildings Administration

حكومة رأس الخيمة
دائـرة البلـدية
إدارة المباني

Approved On — اعتمد في

19 August 2025

Building Permit #: PRMT-25-0004269

Approved By:

Savana
Engineering Consultancy & interior design

Client	ABDULAZIZ TAHNOON AL MANSOORI		
Project	DOUBLE STORY VILLA		
Drg.Title	TOP ROOF PLAN		
Area	AWAFI	Floortype	
Case ID.	2955385	Draw. Type.	ARCH
Sec No.	1	Com. No.	
Block No.		Plot No.	406132231
Bldg. No.	BLD-25-03478	Floor No.	
Date	08/2025	Sht. No.	A06A
Scale	1/100	Job No.	

G.Manager	Architect	Designed By
ENG AYMEN	ENG IMEN	ENG IMEN

TOP ROOF FLOOR PLAN