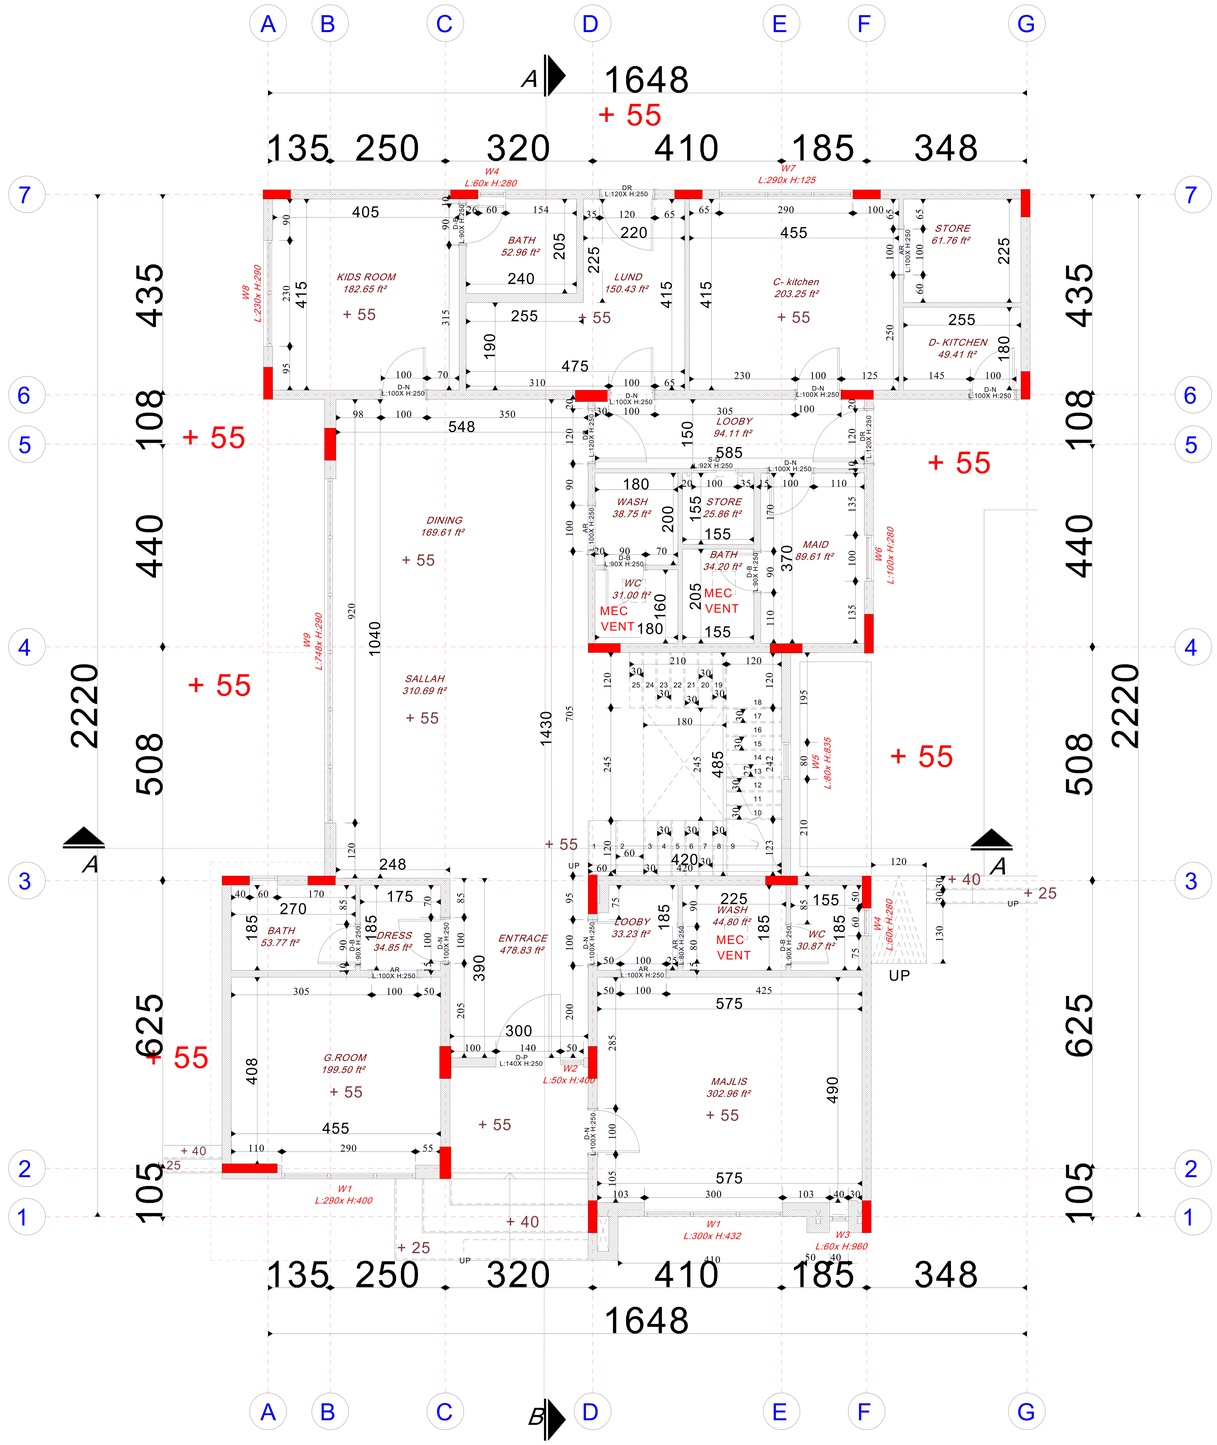

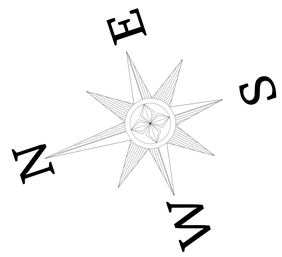

FINISHING FOR VERANDAH		FINISHING FOR DRESSING AREA		FINISHING FOR BATH,WC & WASH	
F3 Marble Tiles	FLOORING	F2 Ceramic Tiles (Non Slippery)	FLOORING	F1 Ceramic glazed tiles	FLOORING
W3 Epoxy paint.	WALLS	W2 Ceramic tiles up to ceiling	WALLS	W1 Acrylic emulsion paint	WALLS
S2 Marble tiles 10cm hight	SKIRTING	S2 Marble tiles 10cm hight	SKIRTING	S1 Ceramic Tiles. 10cm hight	SKIRTING
C3 Epoxy paint.	CEILING	C2 Oil Paint.	CEILING	C1 Acrylic emulsion paint	CEILING

Govemment Of Ras Al Khaimah
R.A.K. Municipality
Buildings Administration

حكومة رأس الخيمة
دائرة البلدية
إدارة المباني

Approved On — اعتمد في

28 July 2025

Building Permit #:

Approved By:

Note :-

* Rcc Lintels Must Be Made On Top Of All Doors , Arches And Windows All Of Them Are At Least 0.20 m Thick.
* All Blocks Adjacent To All Doors , Arches And Windows Must Be A Solid Block .

Rooms	Space	Number
Residential	310.975	
Commercial		
Industrial		
Goverment		
Resident.-Comm.		
Total		

Savana
Engineering Consultancy & interior design

Client	NAYEF ABDULLA MOHAMMED KANAR ALAHMED		
Project	DOUBLE STORY VILLA		
Drg.Title	GROUND FLOOR PLAN		
Area	AWAFI	Floortype	G
Case ID.	2918676	Draw. Type.	ARCH
Sec No.	1	Com. No.	
Block No.		Plot No.	406132384
Bldg. No.	BLD-25-02935	Floor No.	01
Date	2025	Sht. No.	A04
Scale	1/100	Job No.	

G.Manager	Architect	Designed By
ENG AYMEN	ENG IMEN	ENG AHMED

GROUND FLOOR PLAN

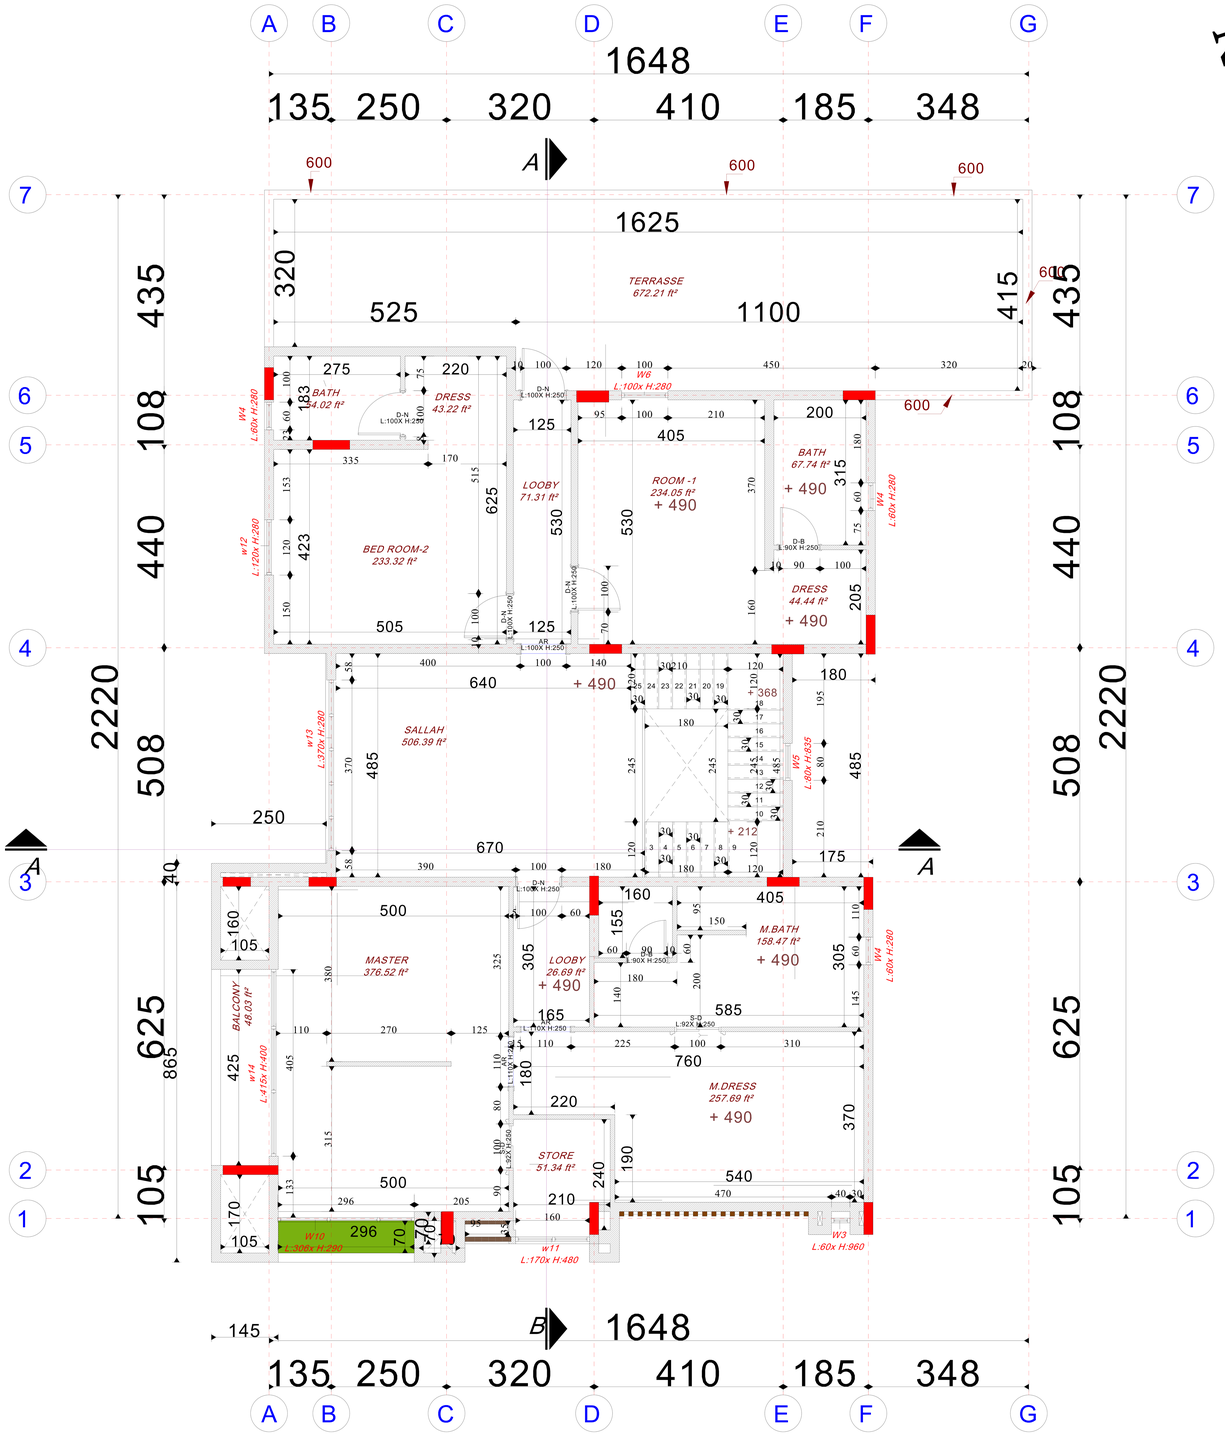

Govemment Of Ras Al Khaimah
R.A.K. Municipality
Buildings Administration

حكومة رأس الخيمة
دائرة البلدية
إدارة المباني

Approved On — اعتمد في

28 July 2025

Building Permit #:

Appoved By:

Note :-

* Rcc Lintels Must Be Made On Top Of All Doors , Arches And Windows All Of Them Are At Least 0.20 m Thick.
* All Blocks Adjacent To All Doors , Arches And Windows Must Be A Solid Block .

Rooms	Space	Number
Residential	243.04	
Commercial		
Industrial		
Goverment		
Resident.-Comm.		
Total		

Savana
Engineering Consultancy & interior design

Client	NAYEF ABDULLA MOHAMMED KANAR ALAHMED		
Project	DOUBLE STORY VILLA		
Drg.Title	FIRST FLOOR PLAN		
Area	AWAFI	Floortype	F
Case ID.	2918676	Draw. Type.	ARCH
Sec No.	1	Com. No.	
Block No.		Plot No.	406132384
Bldg. No.	BLD-25-02935	Floor No.	01
Date	2025	Sht. No.	A05
Scale	1/100	Job No.	

G.Manager	Architect	Designed By
ENG AYMEN	ENG IMEN	ENG AHMED

FIRST FLOOR PLAN

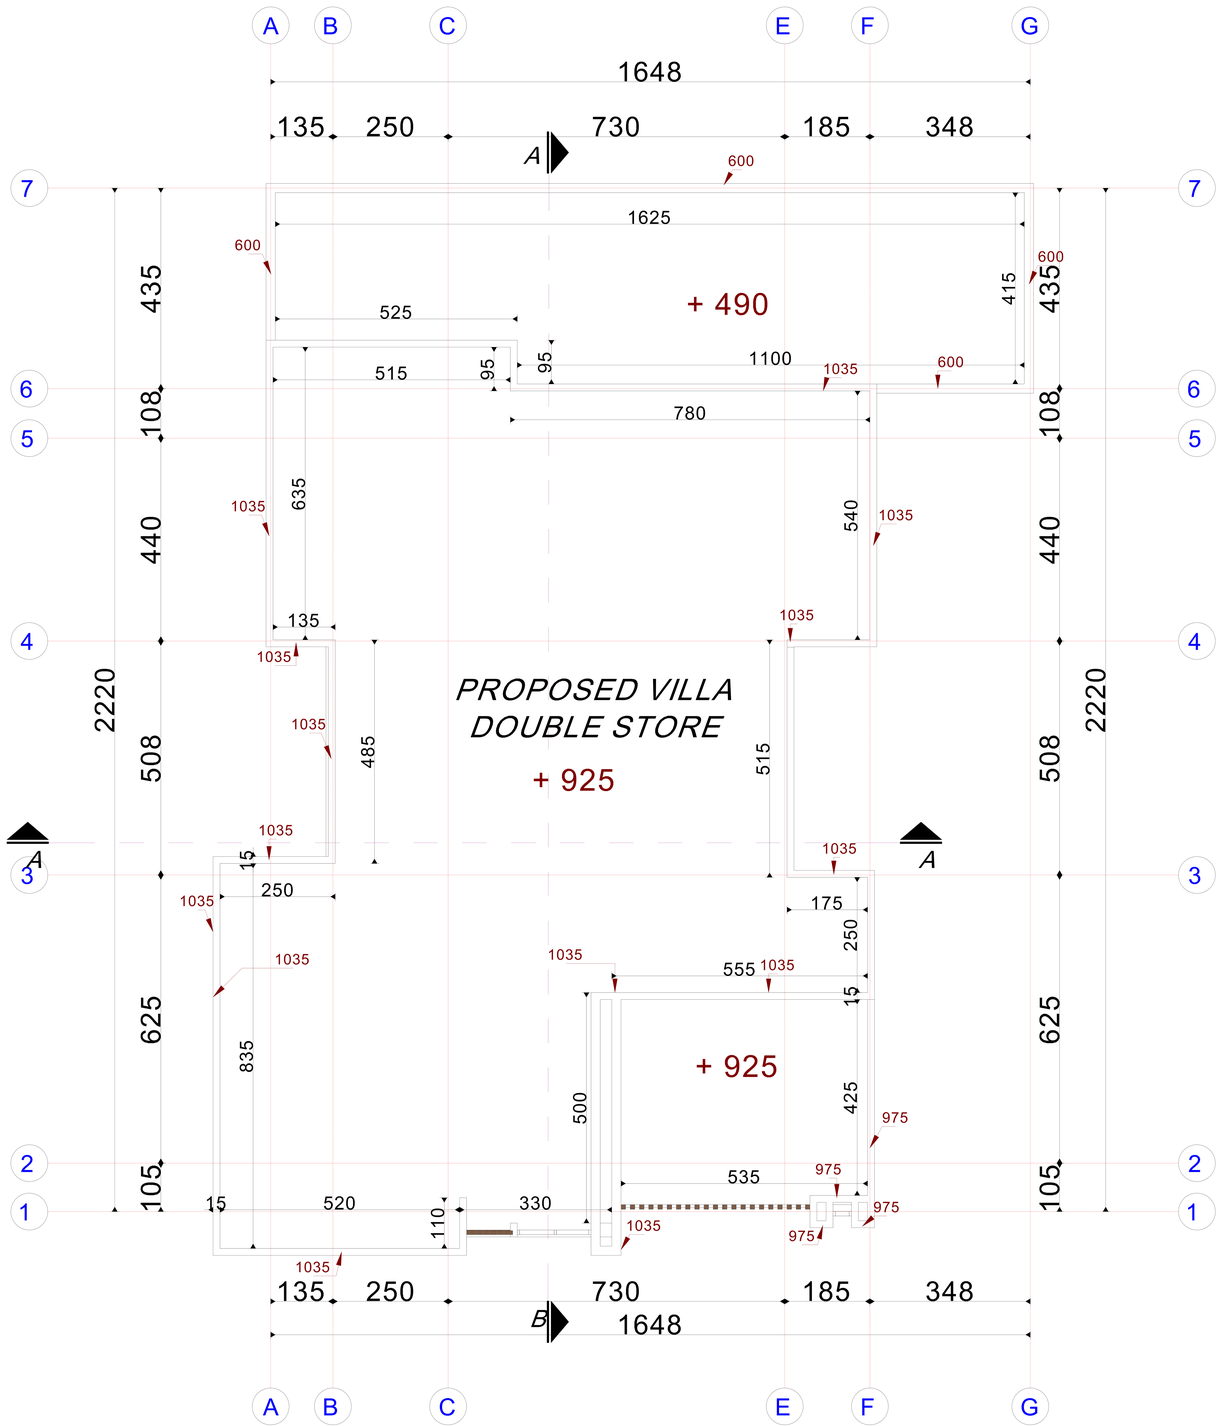

Govvernment Of Ras Al Khaimah
R.A.K. Municipality
Buildings Administration

حكومة رأس الخيمة
دائرة البلدية
إدارة المباني

Approved On — اعتمد في

28 July 2025

Building Permit #:

Approved By:

FINISHING FOR VERANDAH		FINISHING FOR BATH,WC & WASH AREA	
FLOORING		FLOORING	
F3	Marble Tiles	F1	Ceramic glazed tiles
		F2	Ceramic Tiles (Non Slippery)
WALLS		WALLS	
W3	Epoxy paint.	W1	Acrylic emulsion paint
		W2	Ceramic tiles up to ceiling
SKIRTING		SKIRTING	
		S1	Ceramic Tiles. 10cm hight
		S2	Marble tiles 10cm hight
CEILING		CEILING	
C3	Epoxy paint.	C1	Acrylic emulsion paint
		C2	Oil Paint.

Savana
Engineering Consultancy & interior design

Client	NAYEF ABDULLA MOHAMMED KANAR ALAHMED		
Project	DOUBLE STORY VILLA		
Drg.Title	TOP ROOF PLAN		
Area	AWAFI	Floortype	
Case ID.	2918676	Draw. Type.	ARCH
Sec No.	1	Com. No.	
Block No.		Plot No.	406132384
Bldg. No.	BLD-25-02935	Floor No.	
Date	2025	Sht. No.	A06A
Scale	1/100	Job No.	

G.Manager	Architect	Designed By
ENG AYMEN	ENG IMEN	ENG AHMED

FRONT ELEVATION

Govemment Of Ras Al Khaimah
R.A.K. Municipality
Buildings Administration

حكومة رأس الخيمة
دائرة البلدية
إدارة المباني

Approved On — اعتمد في

28 July 2025

Building Permit #:

Appoved By:

FINSHING	
1	FULL EPOXY PAINT [white]
2	WOOD Aluminum
3	FULL EPOXY BLACK PAINT
4	

Savana
Engineering Consultancy & interior design

Client	NAYEF ABDULLA MOHAMMED KANAR ALAHMED		
Project	DOUBLE STORY VILLA		
Drg.Title	FRONT ELEVATION		
Area	AWAFI	Floortype	
Case ID.	2918676	Draw. Type.	ARCH
Sec No.	1	Com. No.	
Block No.		Plot No.	406132384
Bldg. No.	BLD-25-02935	Floor No.	
Date	2025	Sht. No.	A07
Scale	1/100	Job No.	

G.Manager	Architect	Designed By
ENG AYMEN	ENG IMEN	ENG AHMED

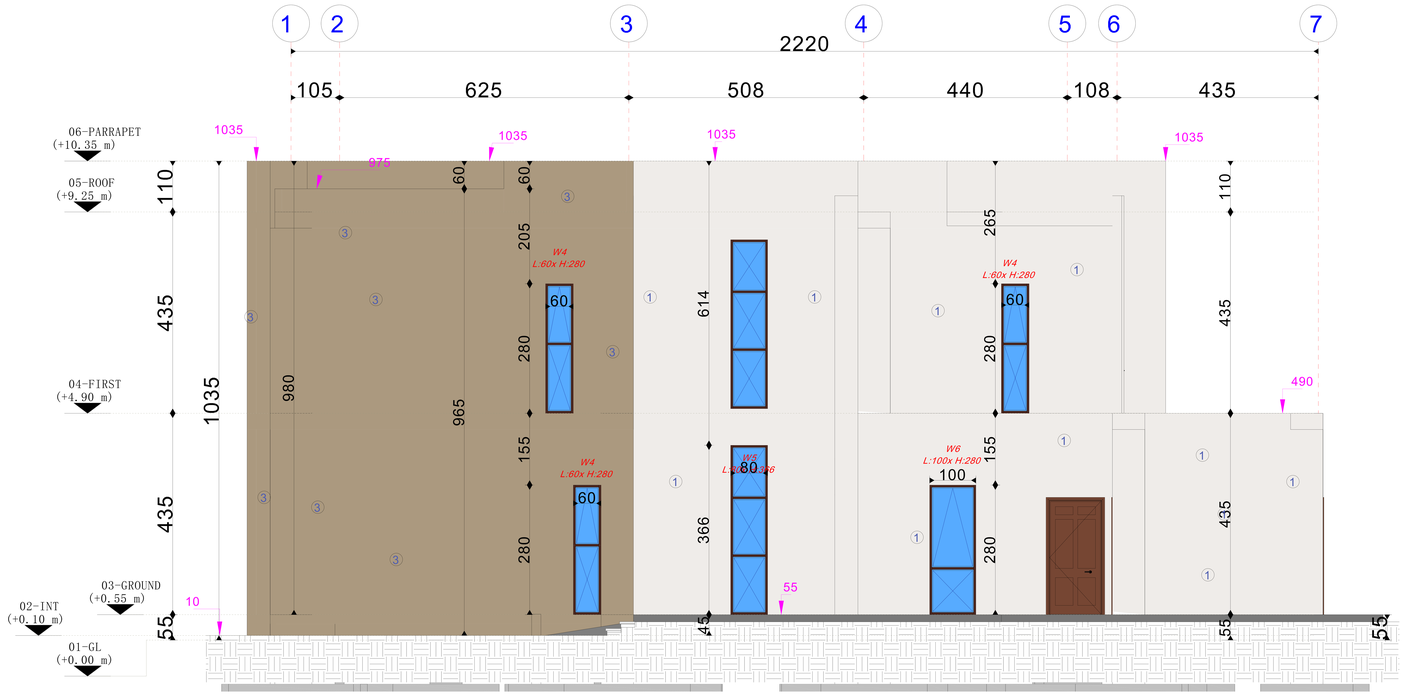

Govement Of Ras Al Khaimah
R.A.K. Municipality
Buildings Administration

حكومة رأس الخيمة
دائرة البلدية
إدارة المباني

Approved On — اعتمد في

28 July 2025

Building Permit #:

Appoved By:

FINSHING	
1	FULL EPOXY PAINT [white]
2	WOOD Aluminum
3	FULL EPOXY BLACK PAINT
4	

Savana
Engineering Consultancy & interior design

Client	NAYEF ABDULLA MOHAMMED KANAR ALAHMED		
Project	DOUBLE STORY VILLA		
Drg.Title	RIGHT ELEVATION		
Area	AWAFI	Floortype	
Case ID.	2918676	Draw. Type.	ARCH
Sec No.	1	Com. No.	
Block No.		Plot No.	406132384
Bldg. No.	BLD-25-02935	Floor No.	
Date	2025	Sht. No.	A08
Scale	1/100	Job No.	

G.Manager	Architect	Designed By
ENG AYMEN	ENG IMEN	ENG AHMED

RIGHT ELEVATION

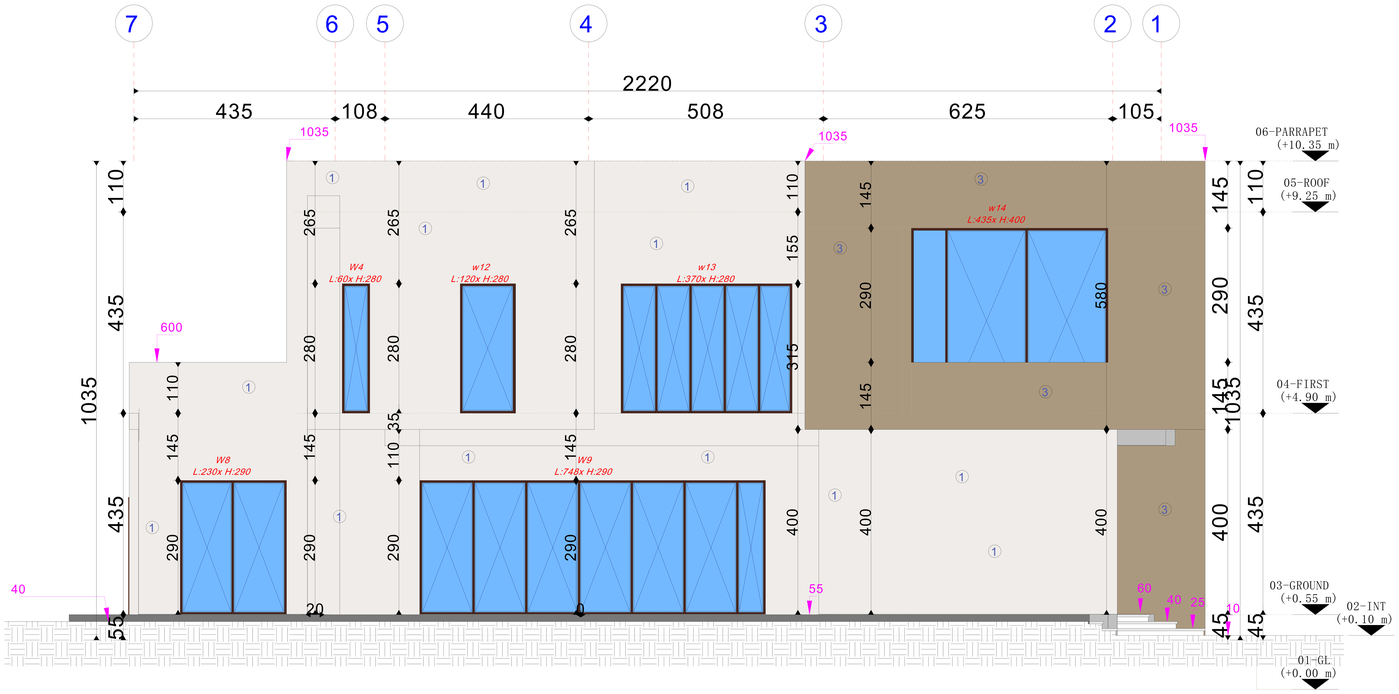

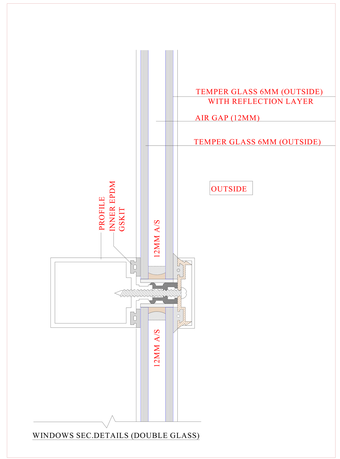

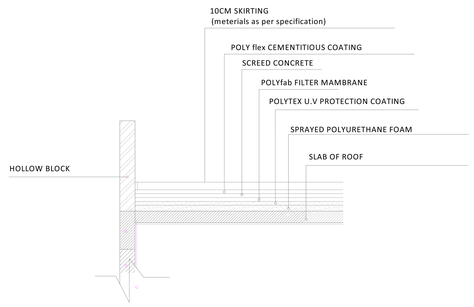

DETAIL FOR COMBO SYSTEM
U-VALUE <0.3 W/M2 K

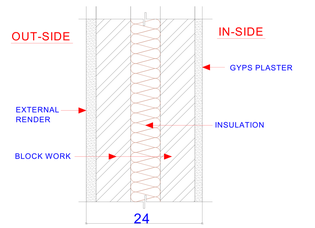

As per E. Walls Predefined Section:W - 1 - A

DETAIL 'W1'	TYPICAL FOR EXTERNAL WALL USING INSULATED CONC. BLOCK (200 mm) U-VALUE < 0.5 W/M2 K

LEFT ELEVATION

Government Of Ras Al Khaimah
R.A.K. Municipality
Buildings Administration

حكومة رأس الخيمة
دائرة البلدية
إدارة المباني

Approved On — اعتمد في

28 July 2025

Building Permit #:

Appoved By:

* Rcc Lintels Must Be Made On Top Of All Doors , Arches And Windows All Of Them Are At Least 0.20 m Thick.
* All Blocks Adjacent To All Doors , Arches And Windows Must Be A Solid Block .

U VALUE AND SHGC

ALL GLASS MUST BE DOUBLE UNITES

GLASS SPECIFICATION:-

U-value (w/m2.k)<_ 1.8

SHADING CO- EFFICIENT (SC) <0.3

FINSHING	
1	FULL EPOXY PAINT [white]
2	WOOD Aluminum
3	FULL EPOXY BLACK PAINT
4	

Savana
Engineering Consultancy & interior design

Client	NAYEF ABDULLA MOHAMMED KANAR ALAHMED		
Project	DOUBLE STORY VILLA		
Drg.Title	LIFT ELEVATION		
Area	AWAFI	Floortype	
Case ID.	2918676	Draw. Type.	ARCH
Sec No.	1	Com. No.	
Block No.		Plot No.	406132384
Bldg. No.	BLD-25-02935	Floor No.	
Date	2025	Sht. No.	A09
Scale	1/100	Job No.	

G.Manager	Architect	Designed By
ENG AYMEN	ENG IMEN	ENG AHMED

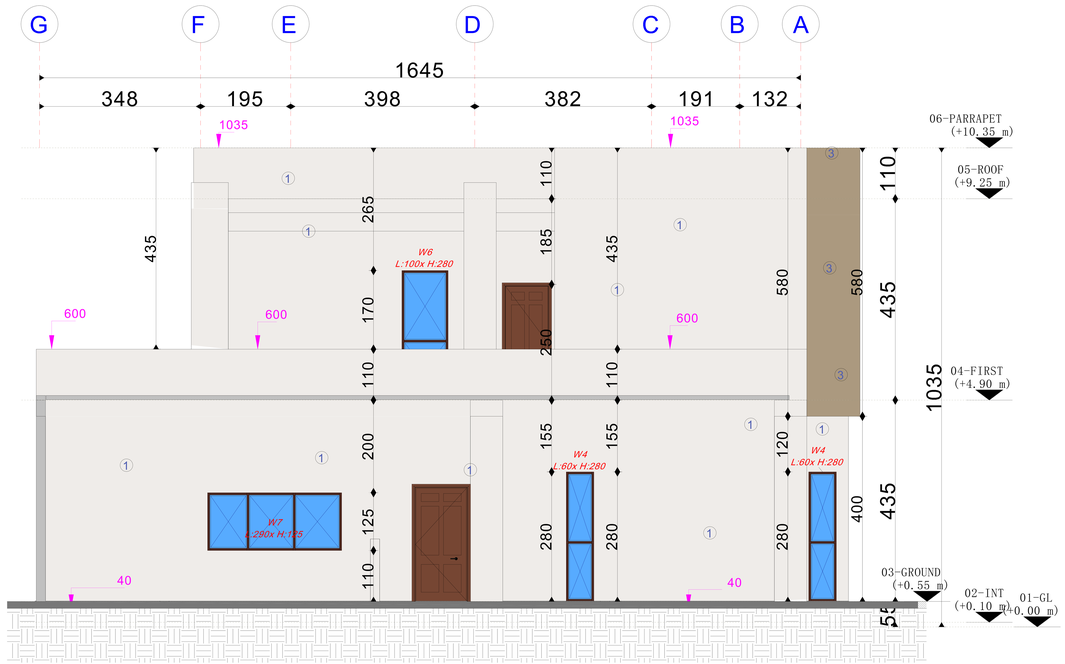

FINSHING	
1	FULL EPOXY PAINT [white]
2	WOOD Aluminum
3	FULL EPOXY BLACK PAINT
4	

Savana
Engineering Consultancy & interior design

Client	NAYEF ABDULLA MOHAMMED KANAR ALAHMED		
Project	DOUBLE STORY VILLA		
Drg.Title	REAR ELEVATION		
Area	AWAFI	Floortype	
Case ID.	2918676	Draw. Type.	ARCH
Sec No.	1	Com. No.	
Block No.		Plot No.	406132384
Bldg. No.	BLD-25-02935	Floor No.	
Date	2025	Sht. No.	A10
Scale	1/100	Job No.	

G.Manager	Architect	Designed By
ENG AYMEN	ENG IMEN	ENG AHMED

REAR ELEVATION

Govemment Of Ras Al Khaimah
R.A.K. Municipality
Buildings Administration

حكومة رأس الخيمة
دائرة البلدية
إدارة المباني

Approved On — اعتمد في

28 July 2025

Building Permit #:

Appoved By:

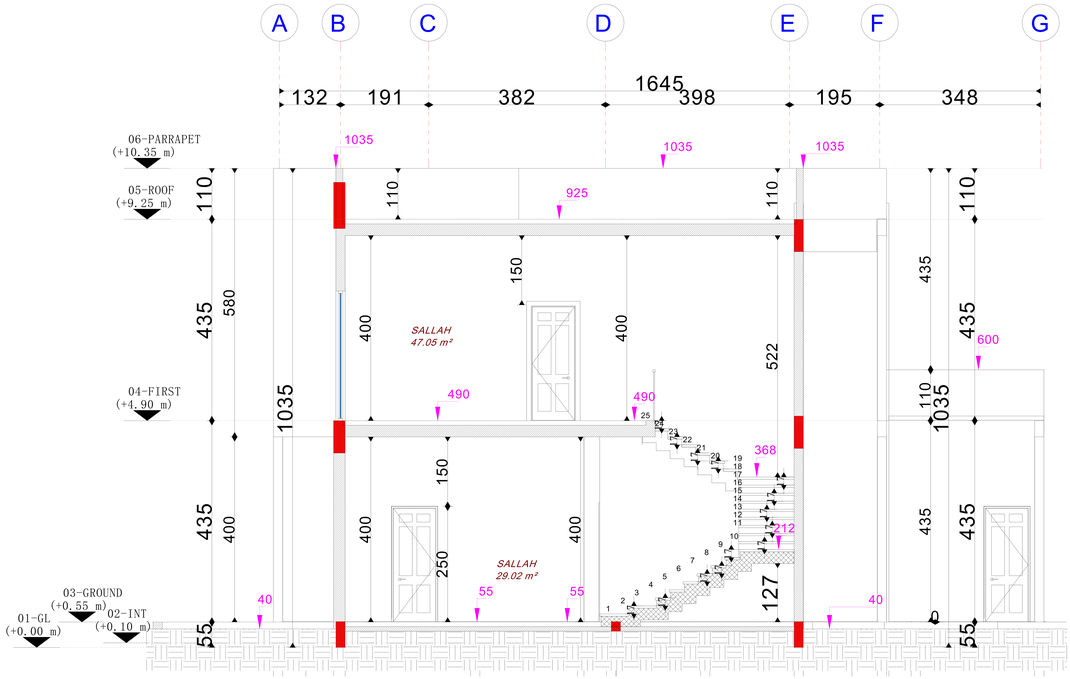

Govemment Of Ras Al Khaimah
R.A.K. Municipality
Buildings Administration

حكومة رأس الخيمة
دائرة البلدية
إدارة المباني

Approved On — اعتمد في

28 July 2025

Building Permit #:

Appoved By:

ALL GLASS MUST BE DOUBLE UNITES

U-value (w/m2.k)<_ 1.8

SHADING CO- EFFICIENT (SC) <0.3

FINSHING	
1	FULL EPOXY PAINT [white]
2	FULL EPOXY BLACK PAINT
3	WOOD Aluminum
4	

Savana
Engineering Consultancy & interior design

Client	NAYEF ABDULLA MOHAMMED KANAR ALAHMED		
Project	DOUBLE STORY VILLA		
Drg.Title	SECTION A-A		
Area	AWAFI	Floortype	
Case ID.	2918676	Draw. Type.	ARCH
Sec No.	1	Com. No.	
Block No.		Plot No.	406132384
Bldg. No.	BLD-25-02935	Floor No.	
Date	2025	Sht. No.	A11
Scale	1/100	Job No.	

G.Manager	Architect	Designed By
ENG AYMEN	ENG IMEN	ENG AHMED

SECTION A-A

SECTION B-B

Govemment Of Ras Al Khaimah
R.A.K. Municipality
Buildings Administration

حكومة رأس الخيمة
دائرة البلدية
إدارة المباني

Approved On — اعتمد في

28 July 2025

Building Permit #:

Appoved By:

ALL GLASS MUST BE DOUBLE UNITES

GLASS SPECIFICATION:-

U-value (w/m2.k)<_ 1.8

SHADING CO- EFFICIENT (SC) <0.3

FINSHING	
1	FULL EPOXY PAINT [white]
2	FULL EPOXY BLACK PAINT
3	WOOD Aluminum
4	

Savana
Engineering Consultancy & interior design

Client	NAYEF ABDULLA MOHAMMED KANAR ALAHMED		
Project	DOUBLE STORY VILLA		
Drg.Title	SECTION B-B		
Area	AWAFI	Floortype	
Case ID.	2918676	Draw. Type.	ARCH
Sec No.	1	Com. No.	
Block No.		Plot No.	406132384
Bldg. No.	BLD-25-02935	Floor No.	
Date	2025	Sht. No.	A12
Scale	1/100	Job No.	

G.Manager	Architect	Designed By
ENG AYMEN	ENG IMEN	ENG AHMED

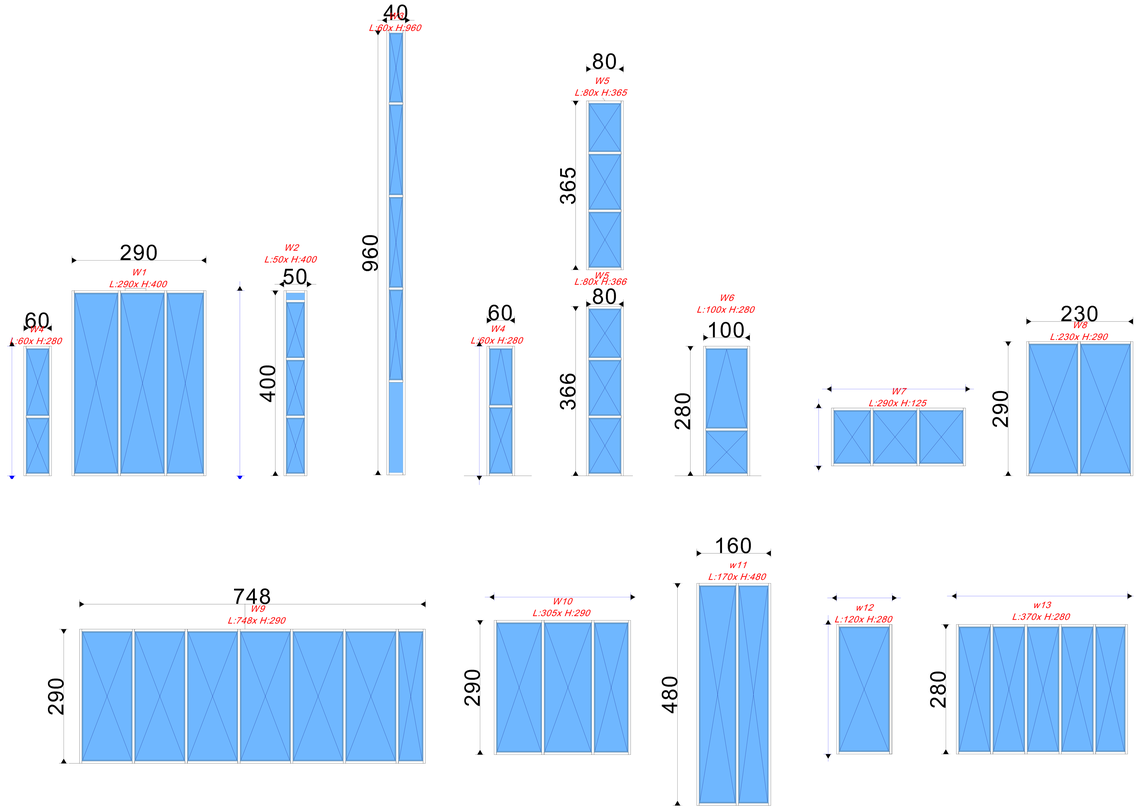

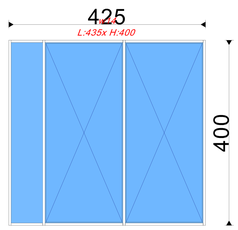

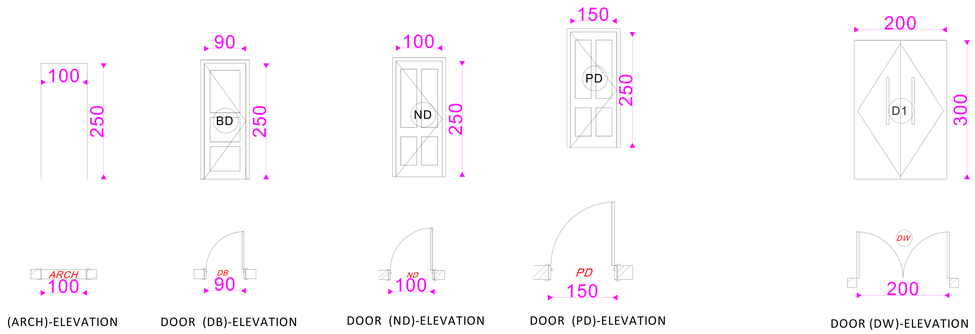

Govemment Of Ras Al Khaimah
R.A.K. Municipality
Buildings Administration

حكومة رأس الخيمة
دائرة البلدية
إدارة المباني

Approved On — **اعتمد في**

28 July 2025

Building Permit #:

Appoved By:

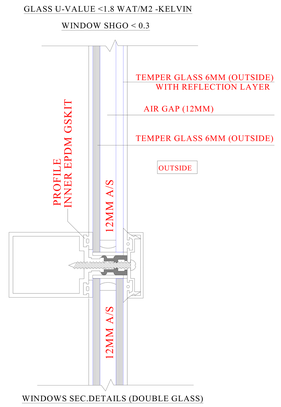

ALL GLASS MUST BE DOUBLE UNITES

GLASS SPECIFICATION:-

U-value (w/m2.k)<_ 1.8

SHADING CO- EFFICIENT (SC) <0.3

Savana
Engineering Consultancy & interior design

Client	NAYEF ABDULLA MOHAMMED KANAR ALAHMED		
Project	DOUBLE STORY VILLA		
Drg.Title	Opening Details		
Area	AWAFI	Floortype	
Case ID.	2918676	Draw. Type.	ARCH
Sec No.	1	Com. No.	
Block No.		Plot No.	406132384
Bldg. No.	BLD-25-02935	Floor No.	
Date	2025	Sht. No.	A13
Scale	1/100	Job No.	

G.Manager	Architect	Designed By
ENG AYMEN	ENG IMEN	ENG AHMED

OPENNING DETAILS

Govemment Of Ras Al Khaimah
R.A.K. Municipality
Buildings Administration

حكومة رأس الخيمة
دائرة البلدية
إدارة المباني

Approved On — اعتمد في

28 July 2025

Building Permit #:

Appoved By:

Savana
Engineering Consultancy & interior design

Client	NAYEF ABDULLA MOHAMMED KANAR ALAHMED		
Project	DOUBLE STORY VILLA		
Drg.Title	PERSPECTIVE		
Area	AWAFI	Floortype	
Case ID.	2918676	Draw. Type.	ARCH
Sec No.	2	Com. No.	
Block No.		Plot No.	406132384
Bldg. No.	BLD-25-02935	Floor No.	
Date	2025	Sht. No.	A14
Scale	1/100	Job No.	

G.Manager	Architect	Designed By
ENG AYMEN	ENG IMEN	ENG AHMED

PERSPECTIVE

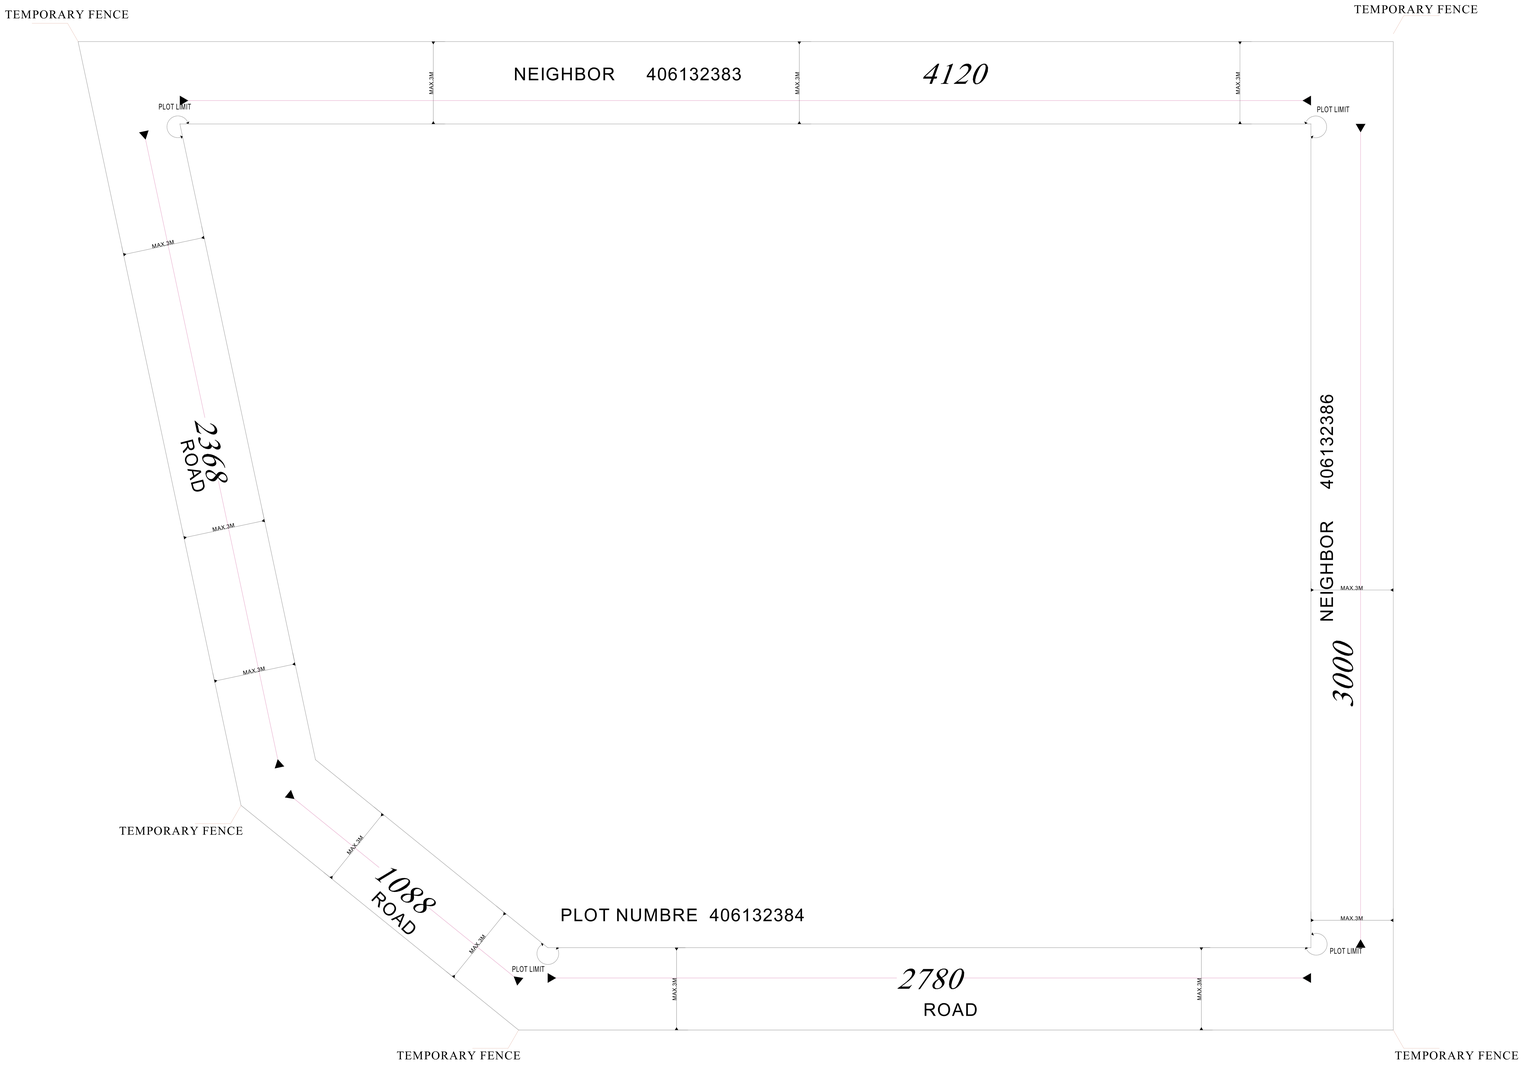

GENERALE SITE TEMPORARY FENCE

Govemment Of Ras Al Khaimah
R.A.K. Municipality
Buildings Administration

حكومة رأس الخيمة
دائرة البلدية
إدارة المباني

Approved On — اعتمد في

28 July 2025

Building Permit #:

Appoved By:

Savana
Engineering Consultancy & interior design

Client	NAYEF ABDULLA MOHAMMED KANAR ALAHMED		
Project	DOUBLE STORY VILLA		
Drg.Title	GENERALE SITE TEMPORARY FENCE		
Area	AWAFI	Floortype	
Case ID.	2918676	Draw. Type.	ARCH
Sec No.	2	Com. No.	
Block No.		Plot No.	406132384
Bldg. No.	BLD-25-02935	Floor No.	
Date	2025	Sht. No.	A18
Scale	1/100	Job No.	

G.Manager	Architect	Designed By
ENG AYMEN	ENG IMEN	ENG AHMED

Type	SCHEDULE OF FINISHINGS
1	LIGHT IVORY

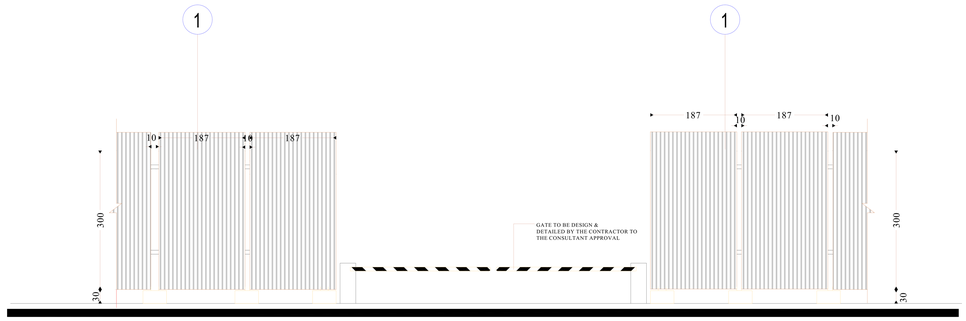

ALUMINIUM TEMPORARY FENCE

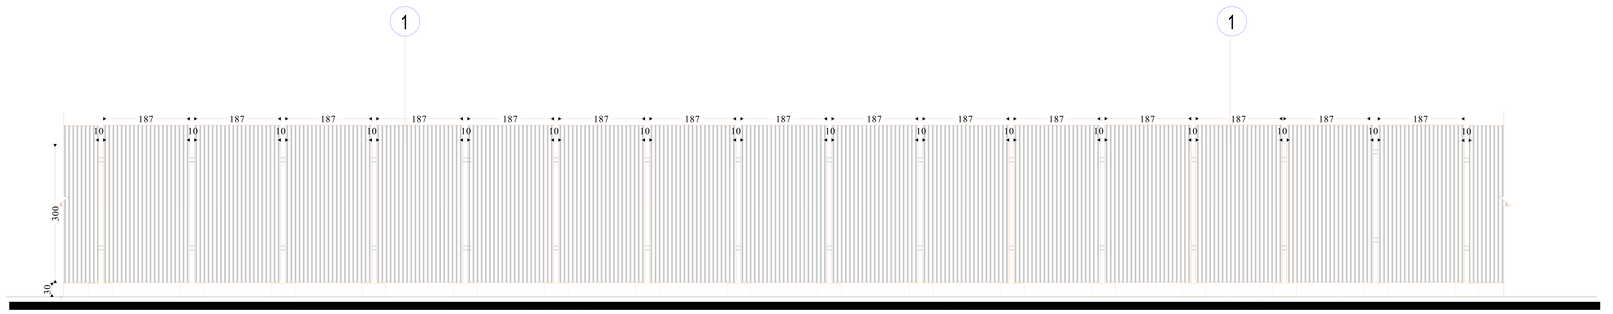

HOARDING ELEVATION

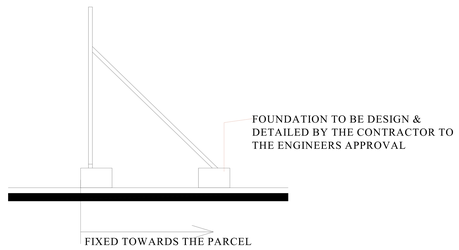

HOARDING SIDE ELEVATION

ALLUMINIUM FENCE

Govemment Of Ras Al Khaimah
R.A.K. Municipality
Buildings Administration

حكومة رأس الخيمة
دائرة البلدية
إدارة المباني

Approved On — اعتمد في

28 July 2025

Building Permit #:

Appoved By:

Savana
Engineering Consultancy & interior design

Client	NAYEF ABDULLA MOHAMMED KANAR ALAHMED		
Project	DOUBLE STORY VILLA		
Drg.Title	ALLUMINIUM FENCE		
Area	AWAFI	Floortype	
Case ID.	2918676	Draw. Type.	ARCH
Sec No.	2	Com. No.	
Block No.		Plot No.	406132384
Bldg. No.	BLD-25-02935	Floor No.	
Date	2025	Sht. No.	A19
Scale	1/100	Job No.	

G.Manager	Architect	Designed By
ENG AYMEN	ENG IMEN	ENG AHMED

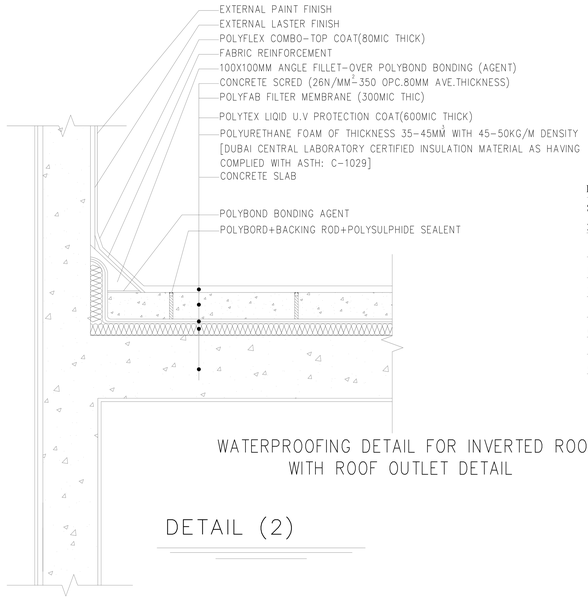

WATERPROOFING DETAIL FOR INVERTED ROOF
WITH ROOF OUTLET DETAIL

DETAIL (2)

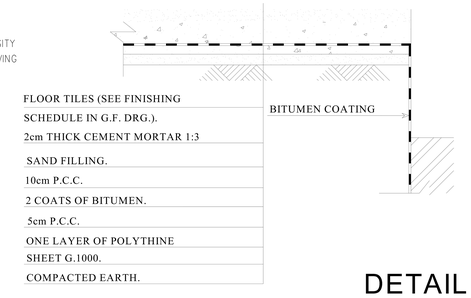

DETAIL (4)

ENTRANCE STEPS DETAIL

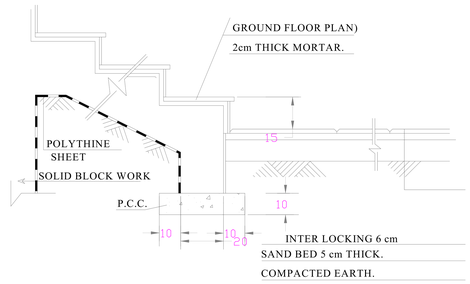

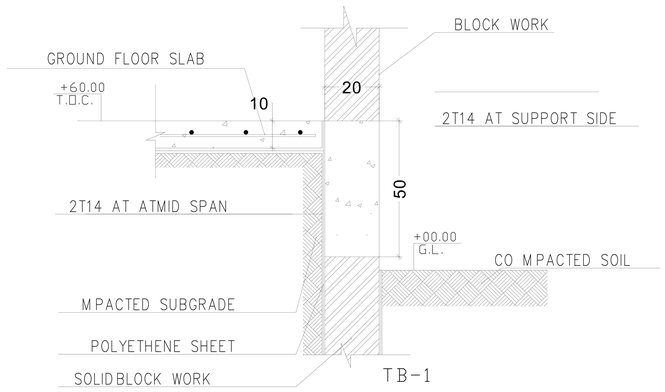

DETAIL (3)

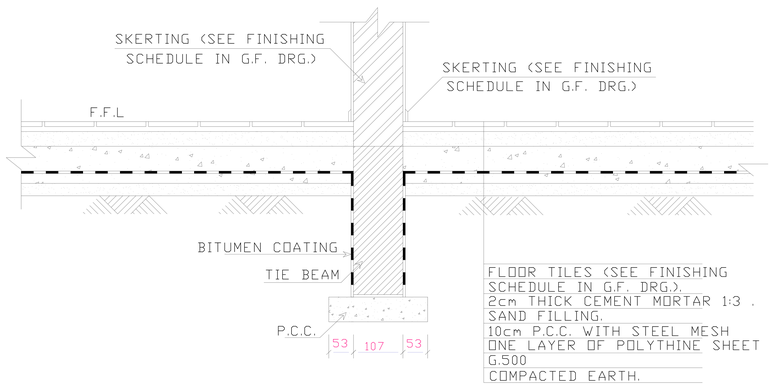

DETAIL (1)

GENERALE DETAILS

Govemment Of Ras Al Khaimah
R.A.K. Municipality
Buildings Administration

حكومة رأس الخيمة
دائرة البلدية
إدارة المباني

Approved On — اعتمد في

28 July 2025

Building Permit #:

Appoved By:

Savana
Engineering Consultancy & interior design

Client	NAYEF ABDULLA MOHAMMED KANAR ALAHMED		
Project	DOUBLE STORY VILLA		
Drg.Title	GENERALE DETAILS		
Area	AWAFI	Floortype	
Case ID.	2918676	Draw. Type.	ARCH
Sec No.	2	Com. No.	
Block No.		Plot No.	406132384
Bldg. No.	BLD-25-02935	Floor No.	
Date	2025	Sht. No.	A20
Scale	1/100	Job No.	

G.Manager	Architect	Designed By
ENG AYMEN	ENG IMEN	ENG AHMED

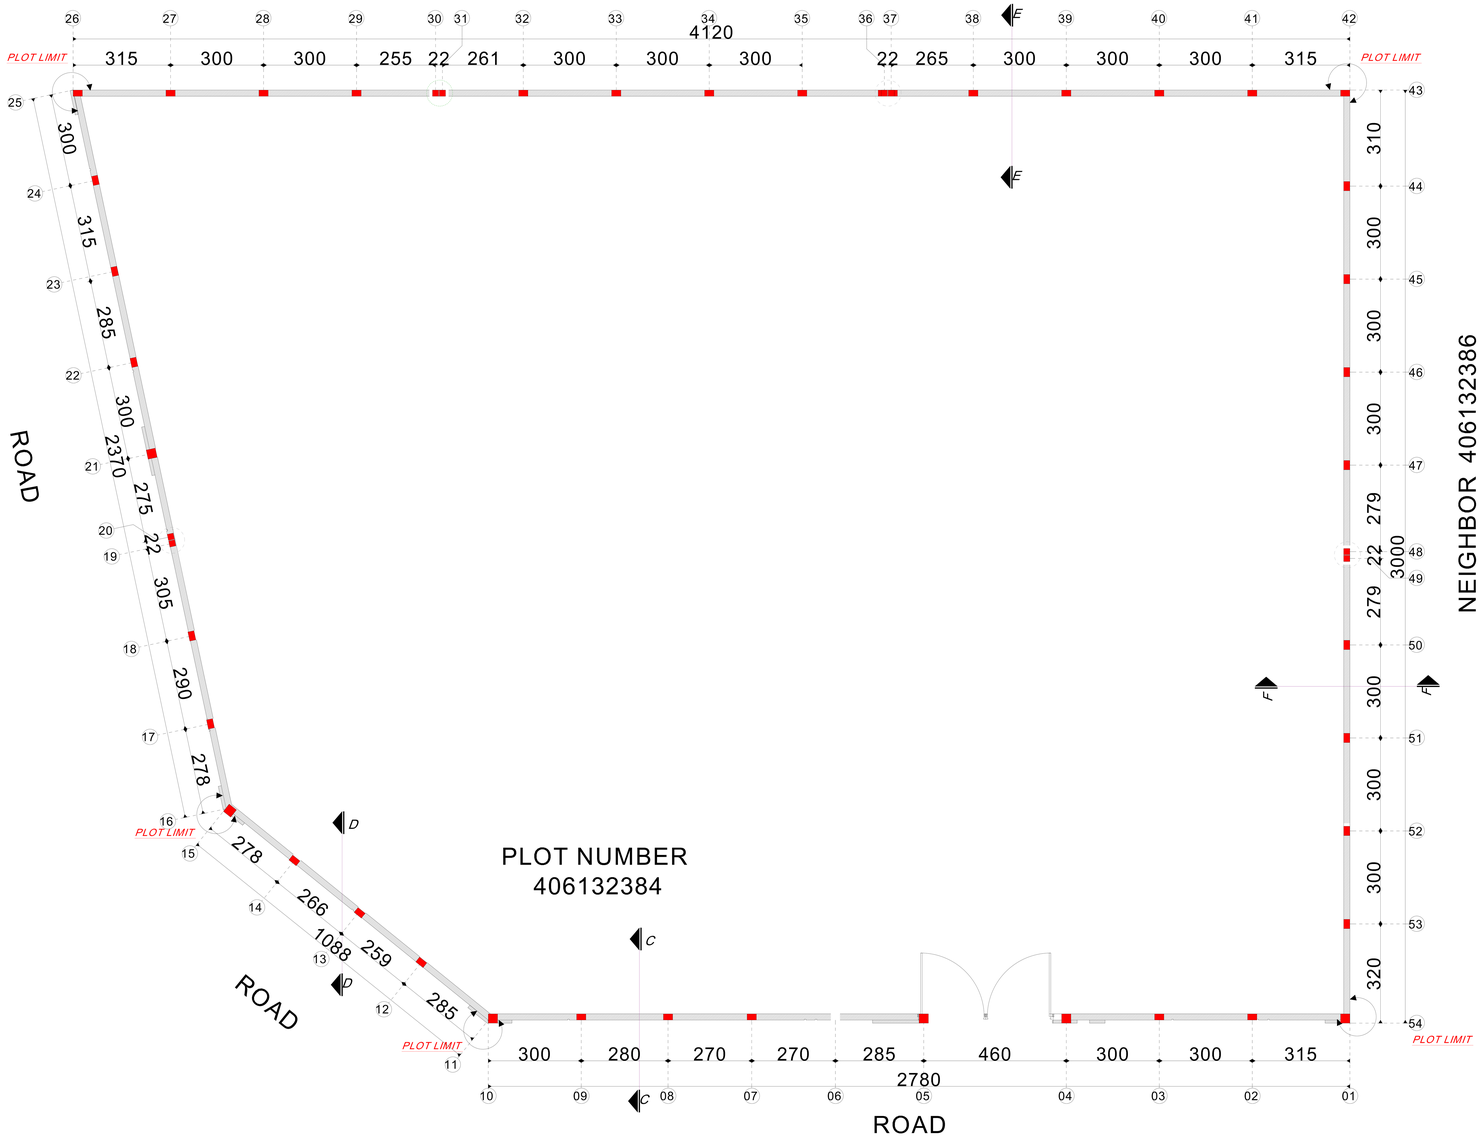

B.WALL SITE PLAN

Govemment Of Ras Al Khaimah
R.A.K. Municipality
Buildings Administration

حكومة رأس الخيمة
دائرة البلدية
إدارة المباني

Approved On — اعتمد في

28 July 2025

Building Permit #:

Appoved By:

Savana
Engineering Consultancy & interior design

Client	NAYEF ABDULLA MOHAMMED KANAR ALAHMED		
Project	DOUBLE STORY VILLA		
Drg.Title	BOUNDARY WALL LAYOUT PLAN		
Area	AWAFI	Floortype	
Case ID.	2918676	Draw. Type.	ARCH
Sec No.	2	Com. No.	
Block No.		Plot No.	406132384
Bldg. No.	FNC-25-001523	Floor No.	
Date	2025	Sht. No.	A15
Scale	1/100	Job No.	

G.Manager	Architect	Designed By
ENG AYMEN	ENG IMEN	ENG AHMED

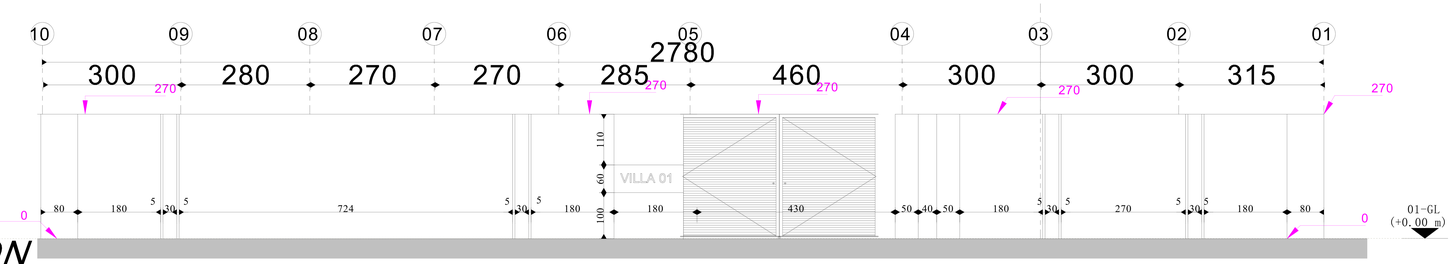

FRONT ELEVATION

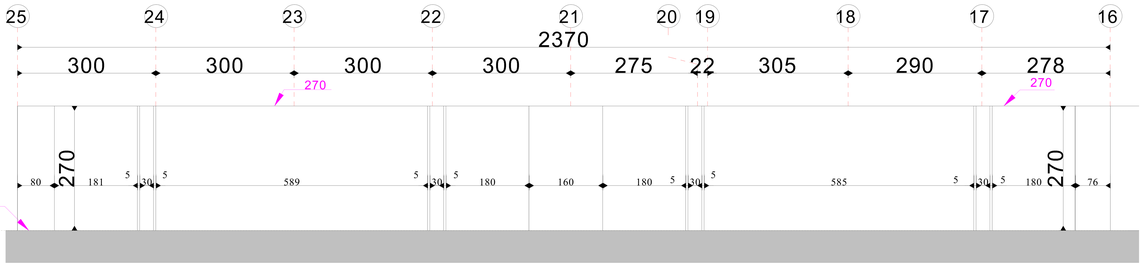

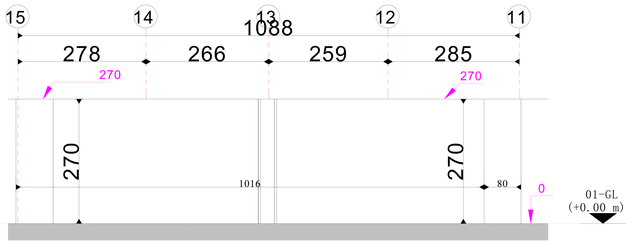

LEFT ELEVATION

REAR ELEVATION

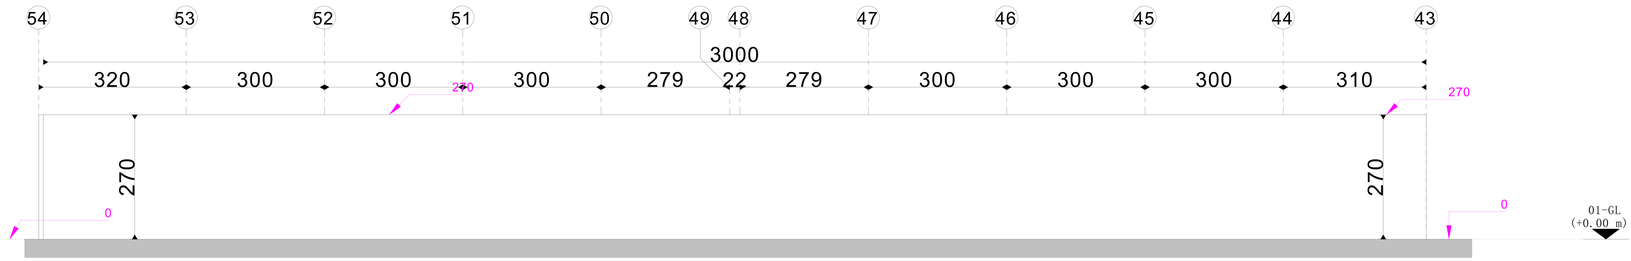

RIGHT ELEVATION

B.WALL ELEVATION

Govvernment Of Ras Al Khaimah
R.A.K. Municipality
Buildings Administration

حكومة رأس الخيمة
دائرة البلدية
إدارة المباني

Approved On — اعتمد في

28 July 2025

Building Permit #:

Appoved By:

Savana
Engineering Consultancy & interior design

Client	NAYEF ABDULLA MOHAMMED KANAR ALAHMED		
Project	DOUBLE STORY VILLA		
Drg.Title	Proposed Boundary Wall Elevations		
Area	AWAFI	Floortype	
Case ID.	2918676	Draw. Type.	ARCH
Sec No.	2	Com. No.	
Block No.		Plot No.	406132384
Bldg. No.	FNC-25-001523	Floor No.	
Date	2025	Sht. No.	A16
Scale	1/100	Job No.	

G.Manager	Architect	Designed By
ENG AYMEN	ENG IMEN	ENG AHMED

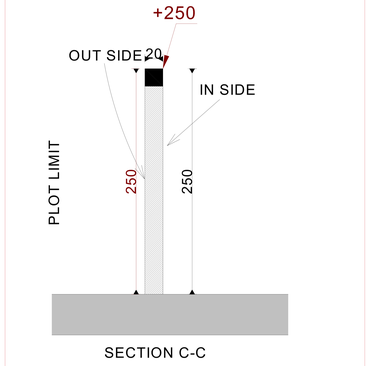

SECTION C-C

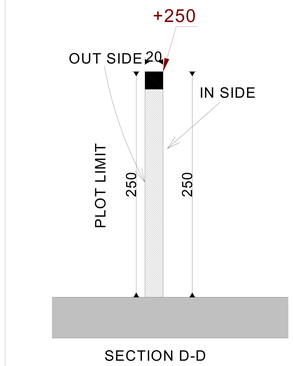

SECTION D-D

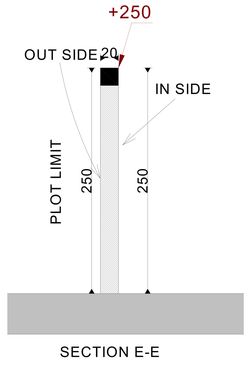

SECTION E-E

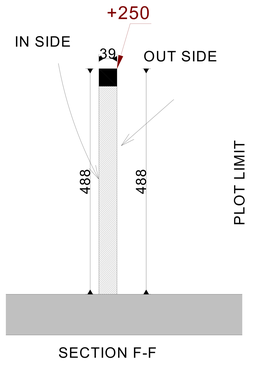

SECTION F-F

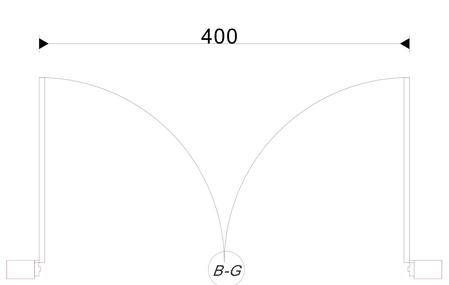

DOOR (BG)-ELEVATION

SCALE 1:50

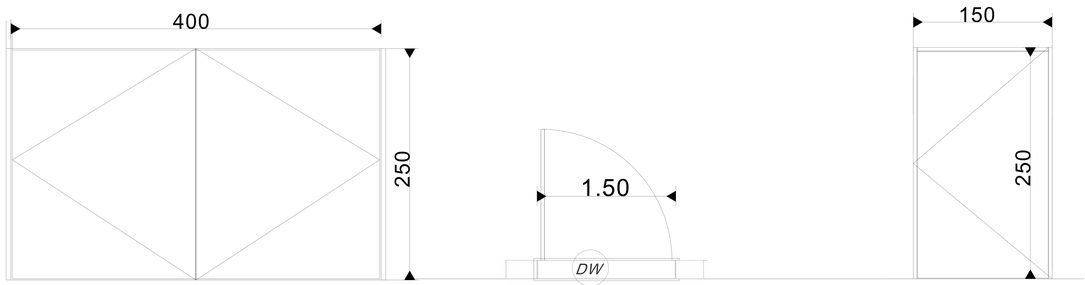

DOOR (DB)-ELEVATION

SCALE 1:50

Govemment Of Ras Al Khaimah
R.A.K. Municipality
Buildings Administration

حكومة رأس الخيمة
دائرة البلدية
إدارة المباني

Approved On — اعتمد في

28 July 2025

Building Permit #:

Appoved By:

Savana
Engineering Consultancy & interior design

Client	NAYEF ABDULLA MOHAMMED KANAR ALAHMED		
Project	DOUBLE STORY VILLA		
Drg.Title	Boundary Wall DETAILS		
Area	AWAFI	Floortype	
Case ID.	2918676	Draw. Type.	ARCH
Sec No.	2	Com. No.	
Block No.		Plot No.	406132384
Bldg. No.	FNC-25-001523	Floor No.	
Date	2025	Sht. No.	A17
Scale	1/100	Job No.	

G.Manager	Architect	Designed By
ENG AYMEN	ENG IMEN	ENG AHMED

B.WALL SECTION

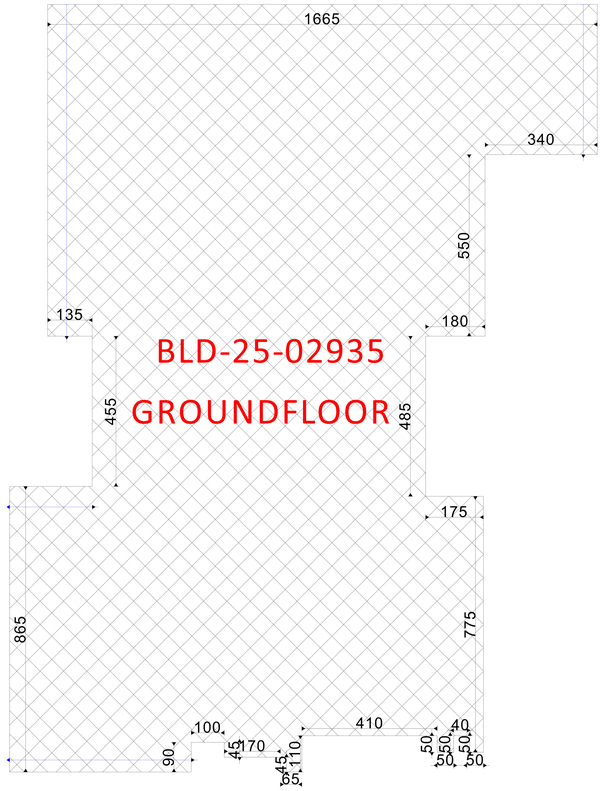

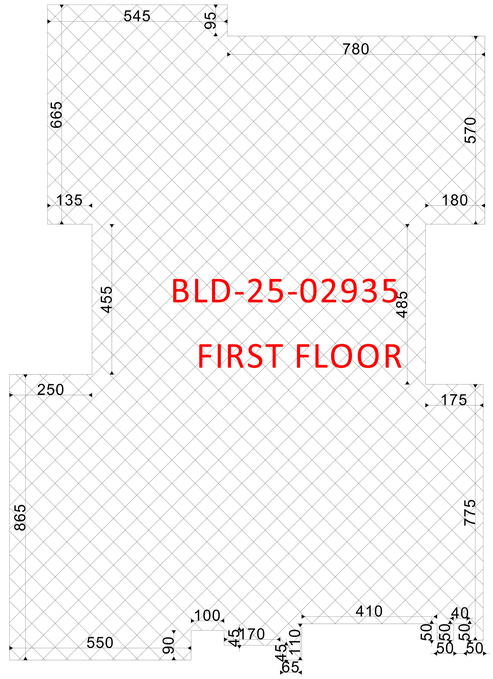

Govemment Of Ras Al Khaimah
R.A.K. Municipality
Buildings Administration

حكومة رأس الخيمة
دائرة البلدية
إدارة المباني

Approved On — اعتمد في

28 July 2025

Building Permit #:

Appoved By:

Area Statement	
Building Number	BLD-25-02935
Ground Floor Area	310.975m²
First Floor Area	243.045m²
Total Building Area	554.02m²
PLOT AREA ACCORDING TO KRUKI	1116.12m²
BUILD UP RATIO	27.86%

Savana
Engineering Consultancy & interior design

Client	NAYEF ABDULLA MOHAMMED KANAR ALAHMED		
Project	DOUBLE STORY VILLA		
Drg.Title	AreaStatement		
Area	AWAFI	Floortype	
Case ID.	2918676	Draw. Type.	ARCH
Sec No.	1	Com. No.	
Block No.		Plot No.	406132384
Bldg. No.	BLD-25-02935	Floor No.	
Date	2025	Sht. No.	A-01
Scale	1/100	Job No.	

G.Manager	Architect	Designed By
ENG AYMEN	ENG IMEN	ENG AHMED

AREA STATMENTENT

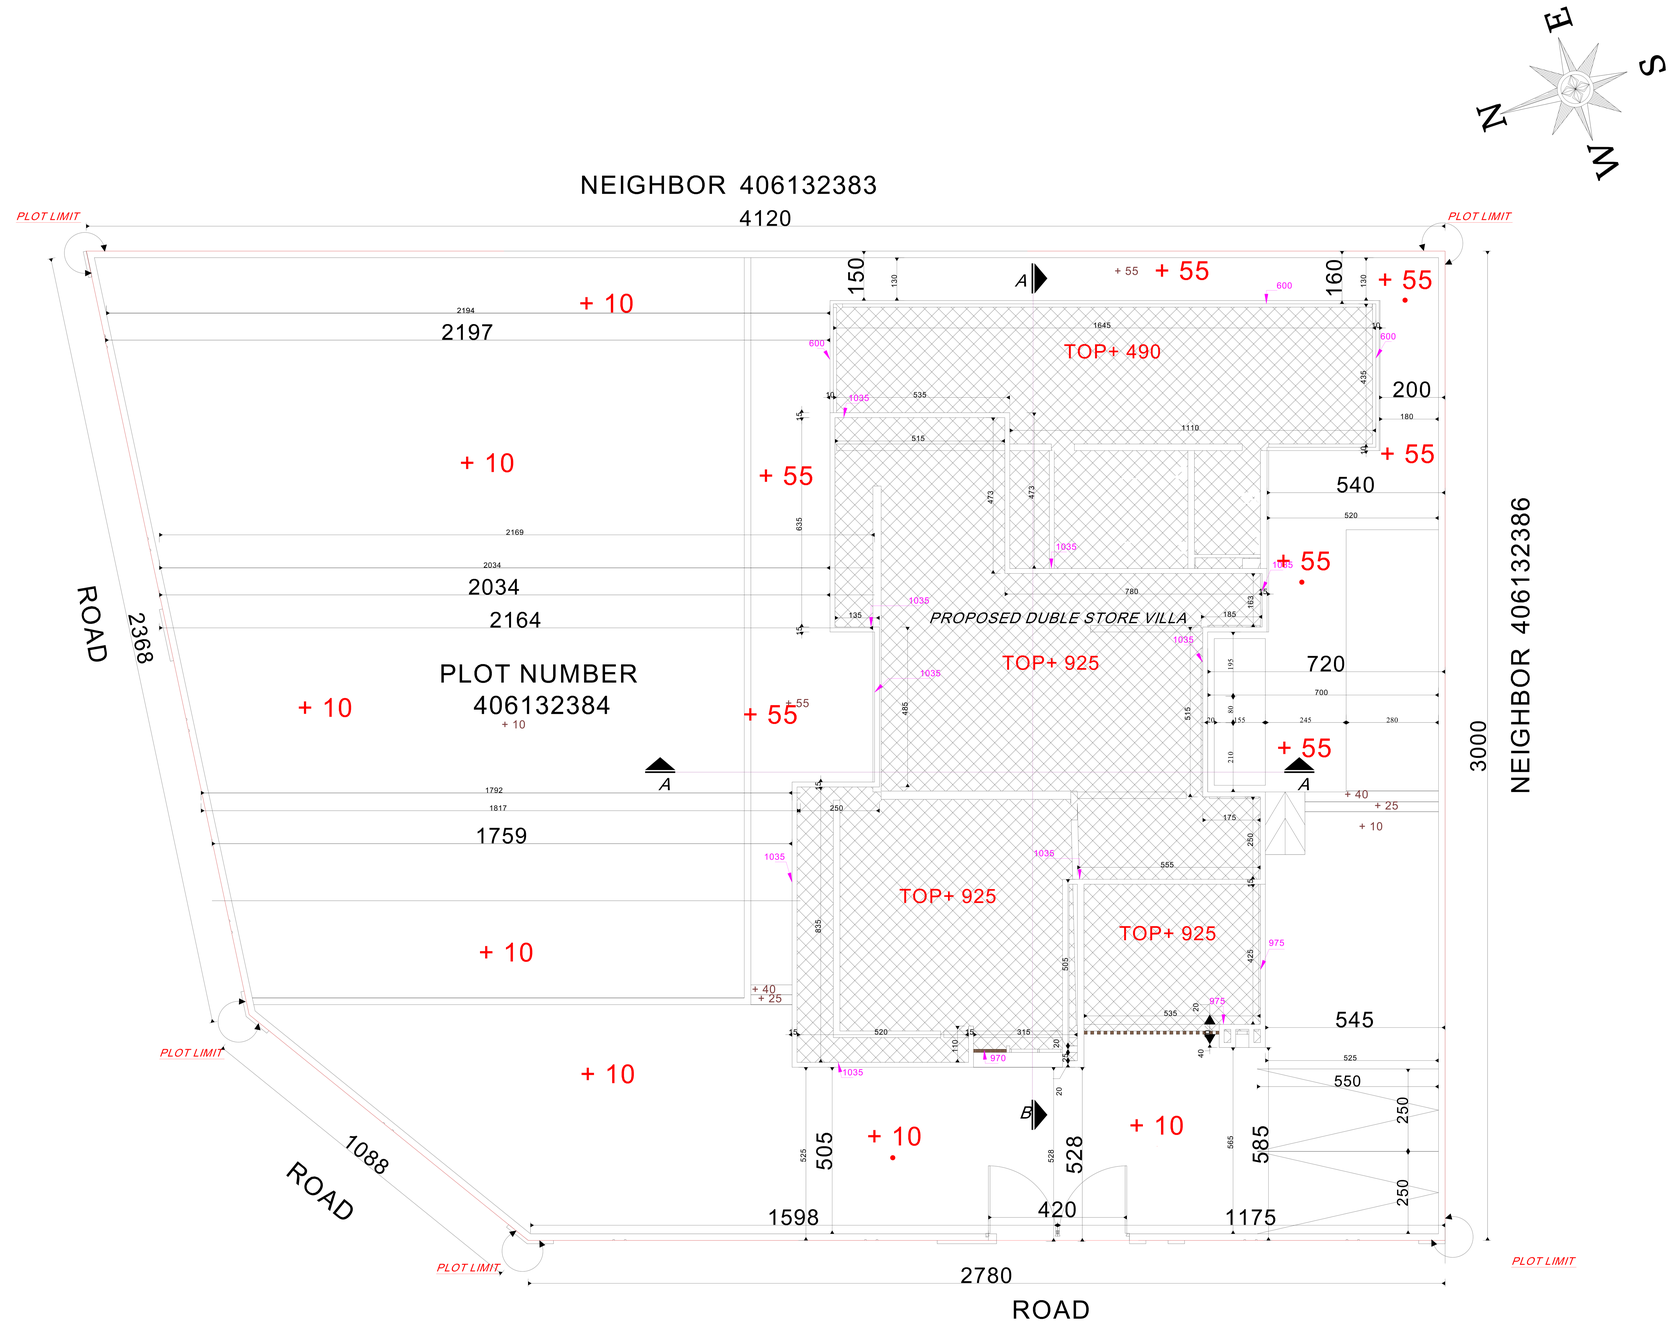

Government Of Ras Al Khaimah
R.A.K. Municipality
Buildings Administration

حكومة رأس الخيمة
دائرة البلدية
إدارة المباني

Approved On — اعتمد في

28 July 2025

Building Permit #:

Appoved By:

Note :-

* Rcc Lintels Must Be Made On Top Of All Doors , Arches And Windows All Of Them Are At Least 0.20 m Thick.
* All Blocks Adjacent To All Doors , Arches And Windows Must Be A Solid Block .

Savana
Engineering Consultancy & Interior design

Client	NAYEF ABDULLA MOHAMMED KANAR ALAHMED		
Project	DOUBLE STORY VILLA		
Drg.Title	Site Development Layout Plan		
Area	AWAFI	Floortype	
Case ID.	2918676	Draw. Type.	ARCH
Sec No.	1	Com. No.	
Block No.		Plot No.	406132384
Bldg. No.	BLD-25-02935	Floor No.	
Date	2025	Sht. No.	A02
Scale	1/100	Job No.	

G.Manager	Architect	Designed By
ENG AYMEN	ENG IMEN	ENG AHMED

SITE DEVELOPMENT LAYOUT PLAN

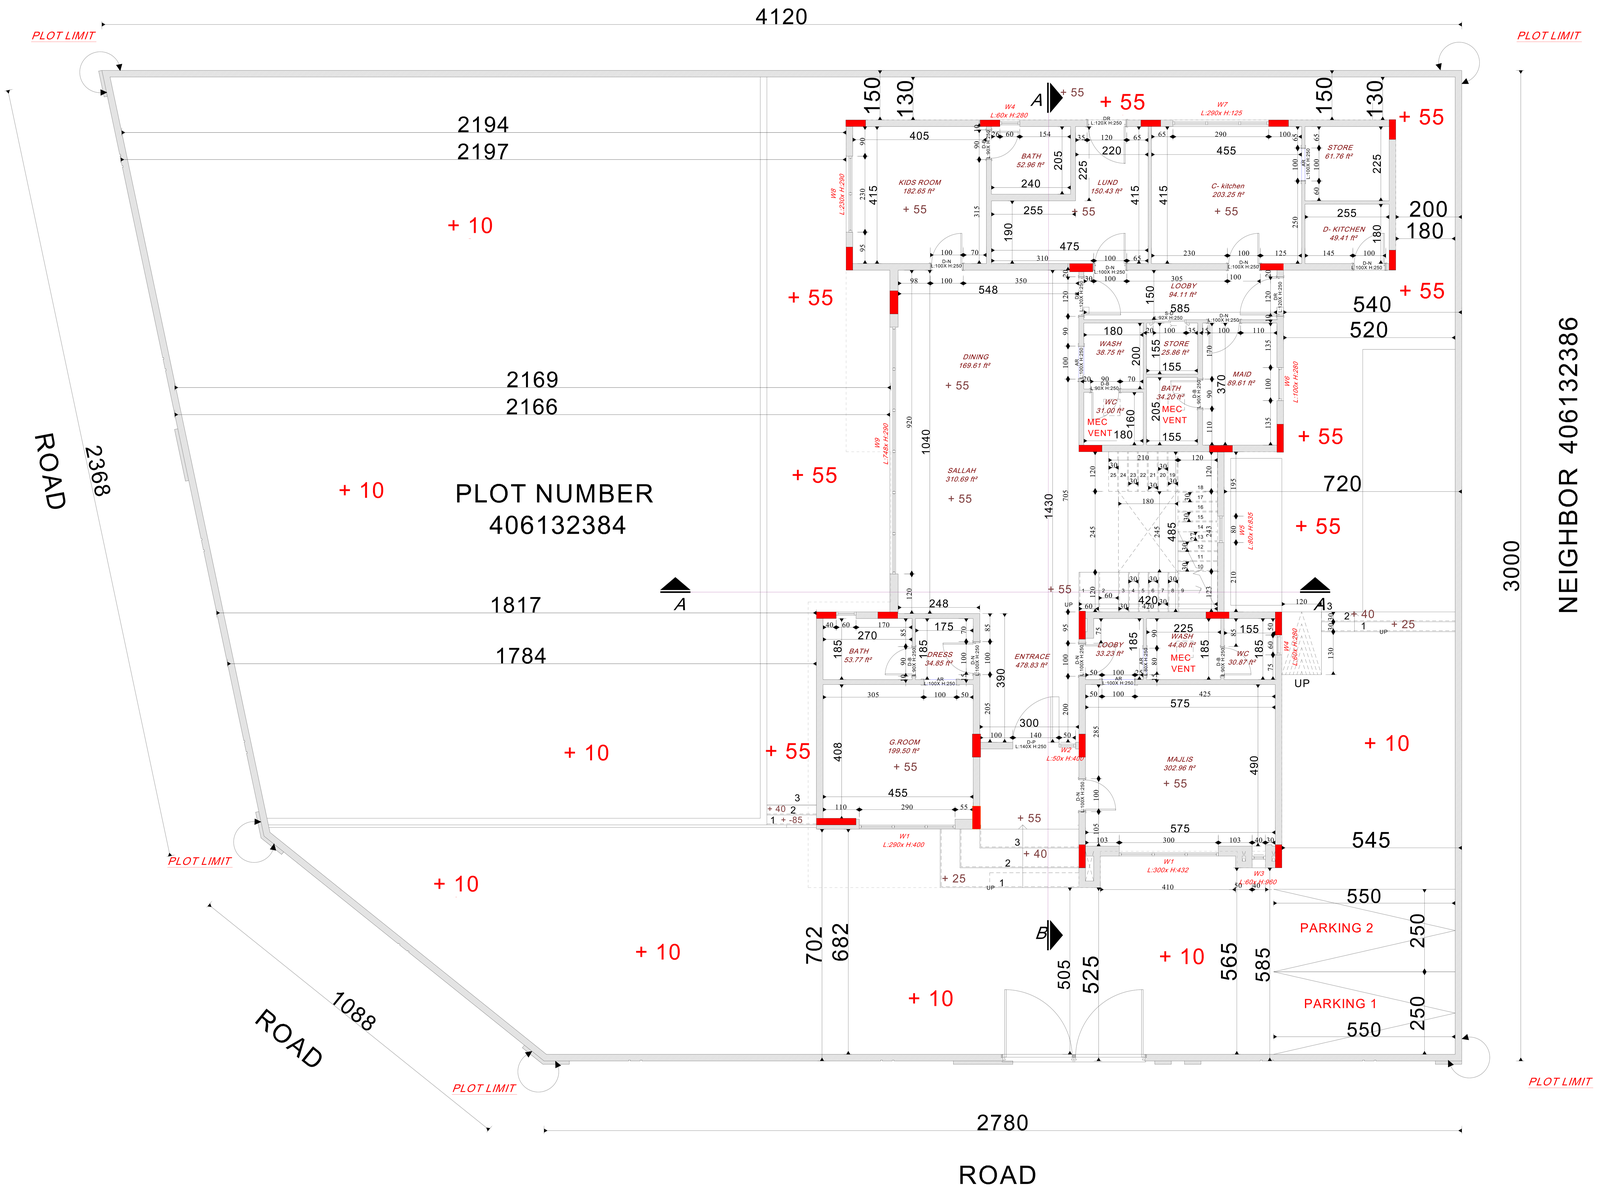

Govvernment Of Ras Al Khaimah
R.A.K. Municipality
Buildings Administration

حكومة رأس الخيمة
دائرة البلدية
إدارة المباني

Approved On — اعتمد في

28 July 2025

Building Permit #:

Approved By:

Savana
Engineering Consultancy & interior design

Client	NAYEF ABDULLA MOHAMMED KANAR ALAHMED		
Project	DOUBLE STORY VILLA		
Drg.Title	SITE SETTING PLAN		
Area	AWAFI	Floortype	
Case ID.	2918676	Draw. Type.	ARCH
Sec No.	1	Com. No.	
Block No.		Plot No.	406132384
Bldg. No.	BLD-25-02935	Floor No.	
Date	2025	Sht. No.	A03
Scale	1/100	Job No.	

G.Manager	Architect	Designed By
ENG AYMEN	ENG IMEN	ENG AHMED

SITE SETTING PLAN