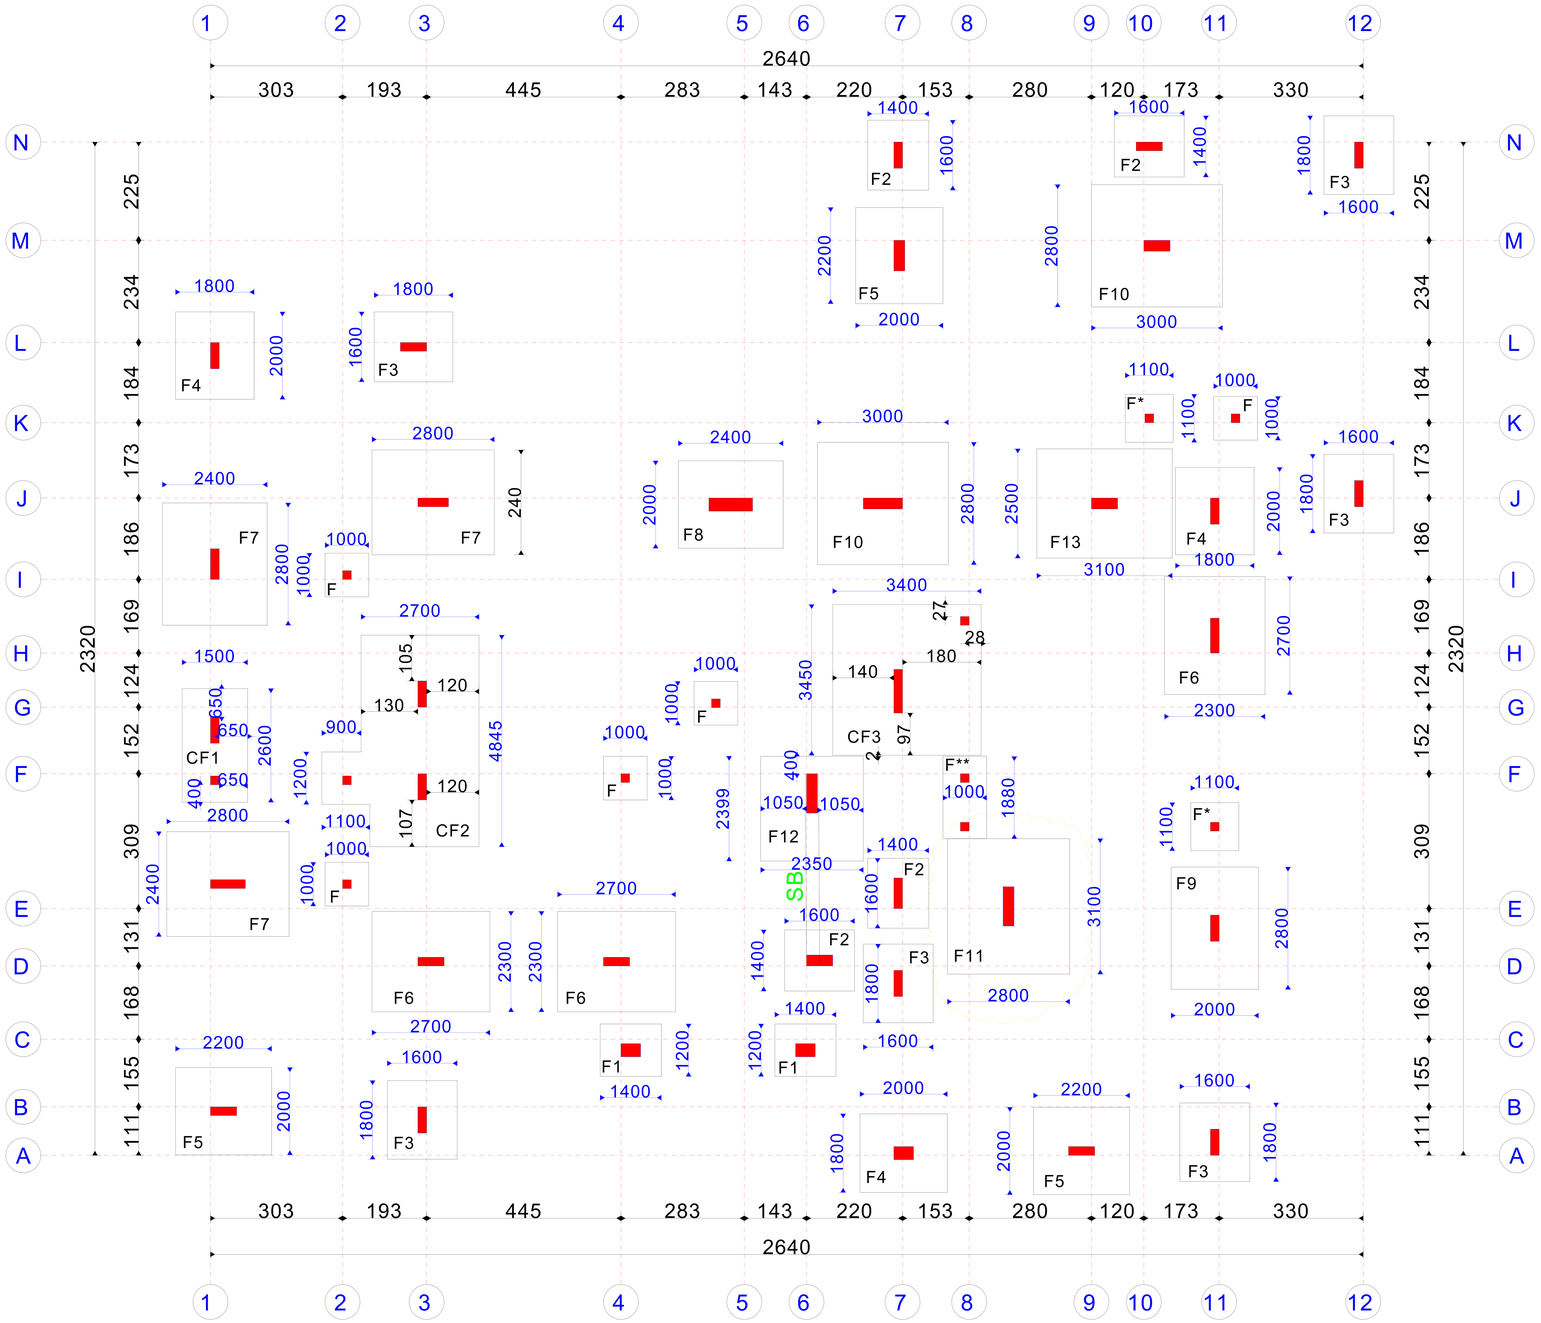

Govemment Of Ras Al Khaimah
R.A.K. Municipality
Buildings Administration

حكومة رأس الخيمة
دائـرة البلـدية
إدارة المباني

Approved On — اعتمد في

01 July 2025

Building Permit #: PRMT-25-0001719

Appoved By:

STRUCTURAL NOTES	CONCRETE COVERS :
ACI 318-11	Foundations cover = 75mm
F'C/FCU = 28/35 N/mm2	Columns cover = 40mm
FY = 460N/mm2	Walls cover = 30mm
FYt = 420N/mm2	Beams cover = 40mm
	Slabs & Stairs cover = 25mm

Rooms	Space	Number
Residential		
Commercial		
Industrial		
Goverment		
Resident.-Comm.		
Total		

Savana
Engineering Consultancy & Interior design

Client	EASA MOHAMMED ALI ALNUAIMI		
Project	DOUBLE STORY VILLA		
Drg.Title	FOUNDATION LAYOUT		
Area	AWAFI	Floortype	
Case ID.	2920970	Draw. Type.	STRC
Sec No.	1	Com. No.	
Block No.		Plot No.	406131530
Bldg. No.	BLD-25-00631	Floor No.	
Date	JUNE 2025	Sht. No.	S02
Scale	1/100	Job No.	

G.Manager	Architect	Designed By
ENG AYMEN	ENG IMEN	ENG IMEN

FONDATION LAYOUT

TYPE	SIZE			REINFORCEMENT DETAILS				REMARKS.
				BOTTOM MESH		TOP MESH		
	WIDTH (mm)	LENGTH (mm)	DEPTH (mm)	SHORT BAR	LONG BAR	SHORT BAR	LONG BAR	
F	1000	1000	350	T12-200	T12-200	4T12	4T12	
F*	1100	1100	350	T12-200	T12-200	4T12	4T12	
F*	1000	1880	350	T12-150	T12-150	T12-150	T12-150	
F1	1200	1400	400	T12-150	T12-150	4T12	4T12	
F2	1400	1600	400	T12-150	T12-150	4T12	4T12	
F3	1600	1800	400	T12-150	T12-150	4T12	4T12	
F4	1800	2000	400	T14-150	T14-150	4T12	4T12	
F5	2000	2200	400	T14-150	T14-150	4T12	4T12	
F6	2300	2700	400	T14-100	T14-100	4T12	4T12	
F7	2400	2800	400	T14-100	T14-100	4T12	4T12	
F8	2000	2400	400	T12-100	T12-100	4T12	4T12	
F9	2000	2800	400	T14-100	T14-100	4T12	4T12	
F10	2800	3000	450	T14-100	T14-100	4T12	4T12	
F11	2800	3100	450	T16-100	T16-100	T14-200	T14-200	
F12	2350	2400	400	T12-150	T12-150	T12-150	T12-150	
F13	2500	3100	400	T14-100	T14-100	T14-200	T14-200	
CF1	1500	2600	400	T12-150	T12-150	T12-150	T12-150	
CF2	AS PLAN		400	T14-100	T14-100	T12-100	T12-100	
CF3	3400	3450	450	T16-100	T16-100	T14-200	T14-200	

TYPE	BEAM SIZE	BOTTOM REINFORCEMENT		TOP REINFORCEMENT			SIDE BARS O.E.F (F) EACH SIDE	STIRRUPS		NO OF LEGS
	MM XMM	STRAIGHT (A)	EXTRA @ MID SPAN(B)	STRAIGHT (C)	EXTRA @ CONT. SUPPORT (D)	EXTRA @ DISCONT. SUPPORT (E)		AT SUPPORT	AT MIDSPAN	
SB	300 X 900	3T20	----	3T20+3T20	----	----	3T12	T10-100	T10-150	2

SCHEDUEL FONDATION

Govemment Of Ras Al Khaimah
R.A.K. Municipality
Buildings Administration

حكومة رأس الخيمة
دائرة البلدية
إدارة المباني

Approved On — اعتمد في

01 July 2025

Building Permit #: PRMT-25-0001719

Appoved By:

Savana
Engineering Consultancy & interior design

Client	EASA MOHAMMED ALI ALNUAIMI		
Project	DOUBLE STORY VILLA		
Drg.Title	FOUNDATION SCHEDULE		
Area	AWAFI	Floortype	
Case ID.	2920970	Draw. Type.	STRC
Sec No.	1	Com. No.	
Block No.		Plot No.	406131530
Bldg. No.	BLD-25-00631	Floor No.	
Date	JUNE 2025	Sht. No.	S03
Scale	1/100	Job No.	

G.Manager	Architect	Designed By
ENG AYMEN	ENG IMEN	ENG IMEN

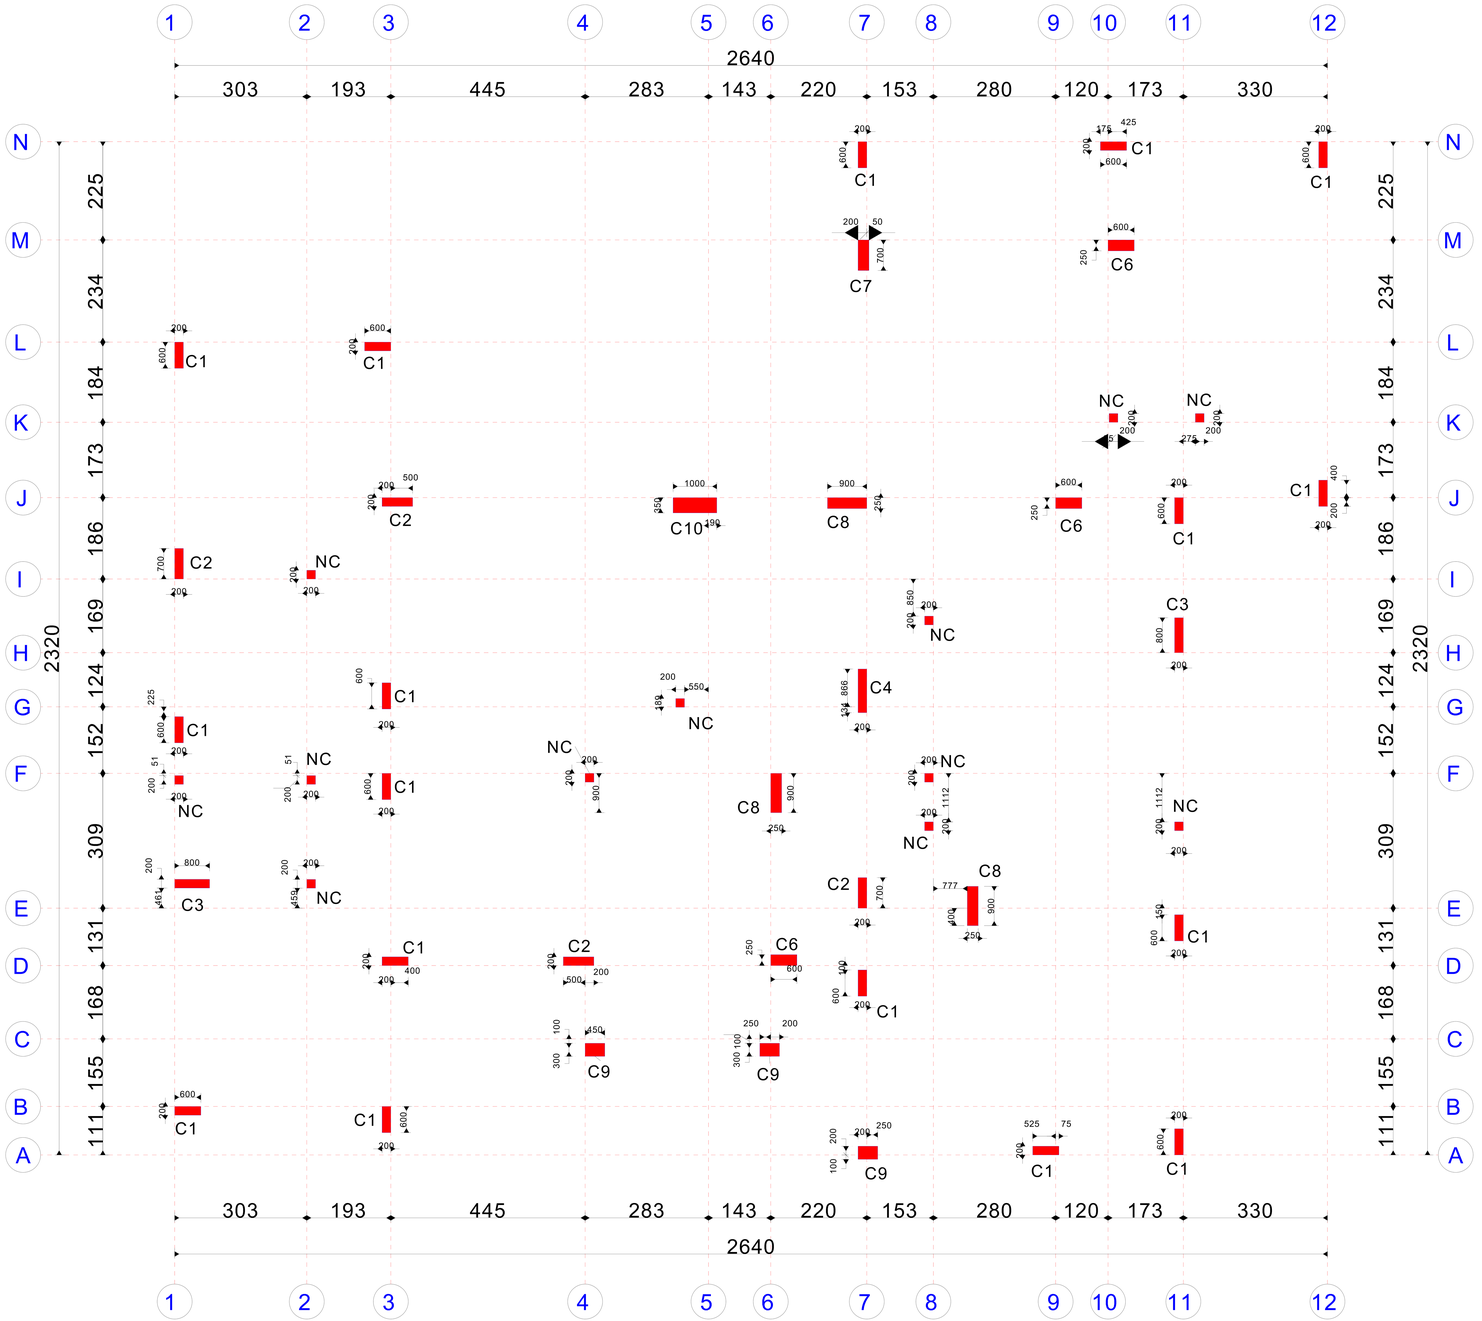

SCHEDULE OF COLUMNS

C1	600 / 200	Main Bar : 8T16 Links : (1T8-150)+(1T8-150) EXTERNAL INTERNAL
C2	700 / 200	Main Bar : 10T16 Links : (1T10-150)+(2T8-150) EXTERNAL INTERNAL
C3	800 / 200	Main Bar : 12T16 Links : (1T10-150)+(1T8-150) EXTERNAL INTERNAL
C4	1000 / 200	Main Bar : 16T18 Links : (1T10-150)+(2T10-150) EXTERNAL INTERNAL
C6	600 / 250	Main Bar : 10T16 Links : (1T10-150)+(1T8-150) EXTERNAL INTERNAL
C7	700 / 250	Main Bar : 10T18 Links : (1T10-150)+(2T8-150) EXTERNAL INTERNAL
C8	900 / 250	Main Bar : 16T16 Links : (1T10-150)+(2T10-150) EXTERNAL INTERNAL
C9	450 / 300	Main Bar : 10T16 Links : (1T10-150)+(2T8-150) EXTERNAL INTERNAL
C10	1000 / 350	Main Bar : 18T18 Links : (1T10-150)+(2T10-150) EXTERNAL INTERNAL
NC	200 / 200	UP TO GROUND SSL ONLY Main Bar : 4T14 Links : (1T8-150) EXTERNAL

Government Of Ras Al Khaimah
R.A.K. Municipality
Buildings Administration

حكومة رأس الخيمة
دائرة البلدية
إدارة المباني

Approved On — اعتمد في

01 July 2025

Building Permit #: PRMT-25-0001719

Approved By:

STRUCTURAL NOTES

ACI 318-11

F'C/FCU = 28/35 N/mm2

FY = 460N/mm2

FYt = 420N/mm2

CONCRETE COVERS :

Foundations cover = 75mm

Columns cover = 40mm

Walls cover = 30mm

Beams cover = 40mm

Slabs & Stairs cover = 25mm

LEGEND:

1) COLUMN / WALL TO BE CONTINUED

2) COLUMN / WALL TO BE TERMINATED

Savana
Engineering Consultancy & interior design

Client	EASA MOHAMMED ALI ALNUAIMI		
Project	DOUBLE STORY VILLA		
Drg.Title	FOUNDATION AND GROUND FLOOR COLUMN LAYOUT		
Area	AWAFI	Floortype	
Case ID.	2920970	Draw. Type.	STRC
Sec No.	1	Com. No.	
Block No.		Plot No.	406131530
Bldg. No.	BLD-25-00631	Floor No.	
Date	JUNE2025	Sht. No.	S10
Scale	1/100	Job No.	

G.Manager	Architect	Designed By
ENG AYMEN	ENG IMEN	ENG IMEN

FOUNDATION AND GROUND FLOOR COLUMN LAYOUT