SCHEDULE OF FOOTINGS

TYPE	SIZE			REINFORCEMENT DETAILS				REMARKS.
	WIDTH (MM)	LENGTH (MM)	DEPTH (MM)	BOTTOM MESH		TOP MESH		
				SHORT BAR	LONG BAR	SHORT BAR	LONG BAR	
FNC	1100	1700	350	T12-150	T12-150	4T12	2T12	
F1	1200	1500	400	T12-150	T12-150	4T12	2T12	
F2	1400	1700	400	T12-150	T12-150	4T12	2T12	
F3	1800	2100	400	T12-150	T12-150	4T12	2T12	
F4	2400	2700	450	T12-100	T12-100	4T12	2T12	
F5	2800	3100	450	T16-150	T16-150	4T12	2T12	
F6	3000	3500	450	T16-150	T16-150	4T12	2T12	
F7	3500	3800	450	T16-150	T16-150	4T12	2T12	
F8	2500	3400	450	T14-150	T14-150	4T12	2T12	
F9	AS PER LAYOUT		400	T14-150	T14-150	T12-150	T12-150	
F10	AS PER LAYOUT		500	T16-150	T16-150	T12-150	T12-150	
F11	2700	3500	450	T14-150	T14-150	4T12	2T12	
CF1	1500	2400	400	T12-150	T12-150	T12-150	T12-150	
CF2	1700	3500	400	T12-150	T12-150	T12-150	T12-150	
CF3	2300	3150	450	T12-150	T12-150	T12-150	T12-150	
CF4	2300	3500	450	T14-150	T14-150	T12-150	T12-150	
CF5	2700	2900	450	T14-150	T14-150	T12-150	T12-150	
CF6	2900	3900	400	T14-150	T14-150	T12-150	T12-150	
CF7	3000	4700	500	T12-100	T12-100	T12-100	T12-100	
CF8	AS PER LAYOUT		450	T14-150	T14-150	T12-150	T12-150	

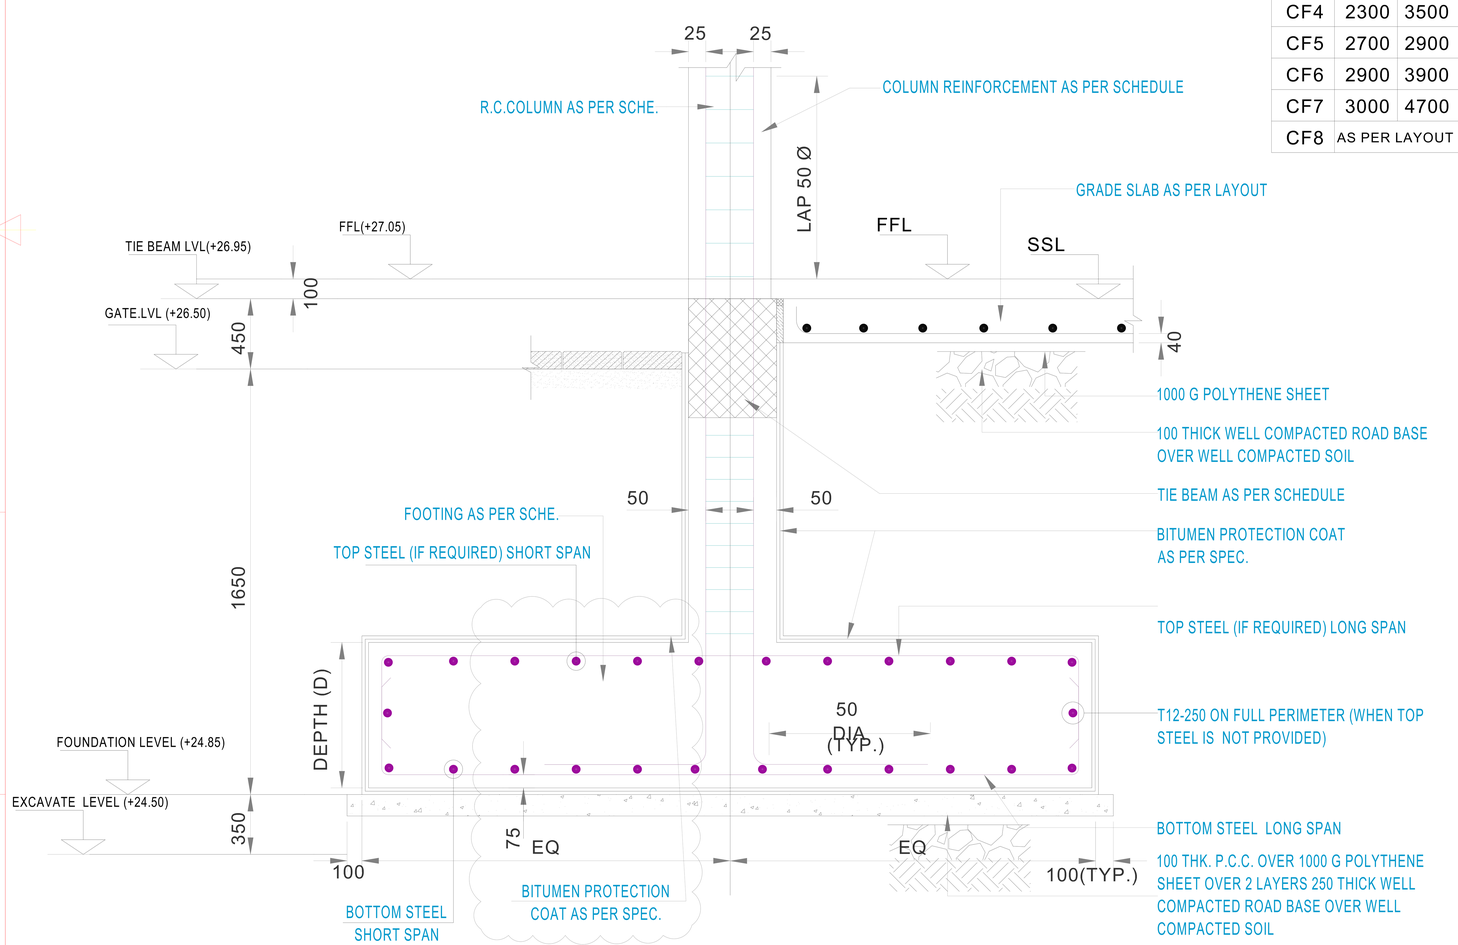

(TYPICAL SECTION FOR FOOTING)

SCHEDUEL FONDATION

Govemment Of Ras Al Khaimah
R.A.K. Municipality
Buildings Administration

حكومة رأس الخيمة
دائرة البلدية
إدارة المباني

Approved On — اعتمد في

09 June 2025

Building Permit #: PRMT-25-0001928

Appoved By:

Savana
Engineering Consultancy & interior design

Client	AHMED HASAN HAMAD TARYAM ALZAABI		
Project	DOUBLE STOREY VILLA		
Drg.Title	FOUNDATION SCHEDULE		
Area	ALRIFAA	Floortype	
Case ID.	2902259	Draw. Type.	STRC
Sec No.	1	Com. No.	
Block No.		Plot No.	603100061
Bldg. No.	BLD-25-00764	Floor No.	
Date	MAY2025	Sht. No.	S03
Scale	1/100	Job No.	

G.Manager	Architect	Designed By
ENG AYMEN	ENG IMEN	ENG IMEN