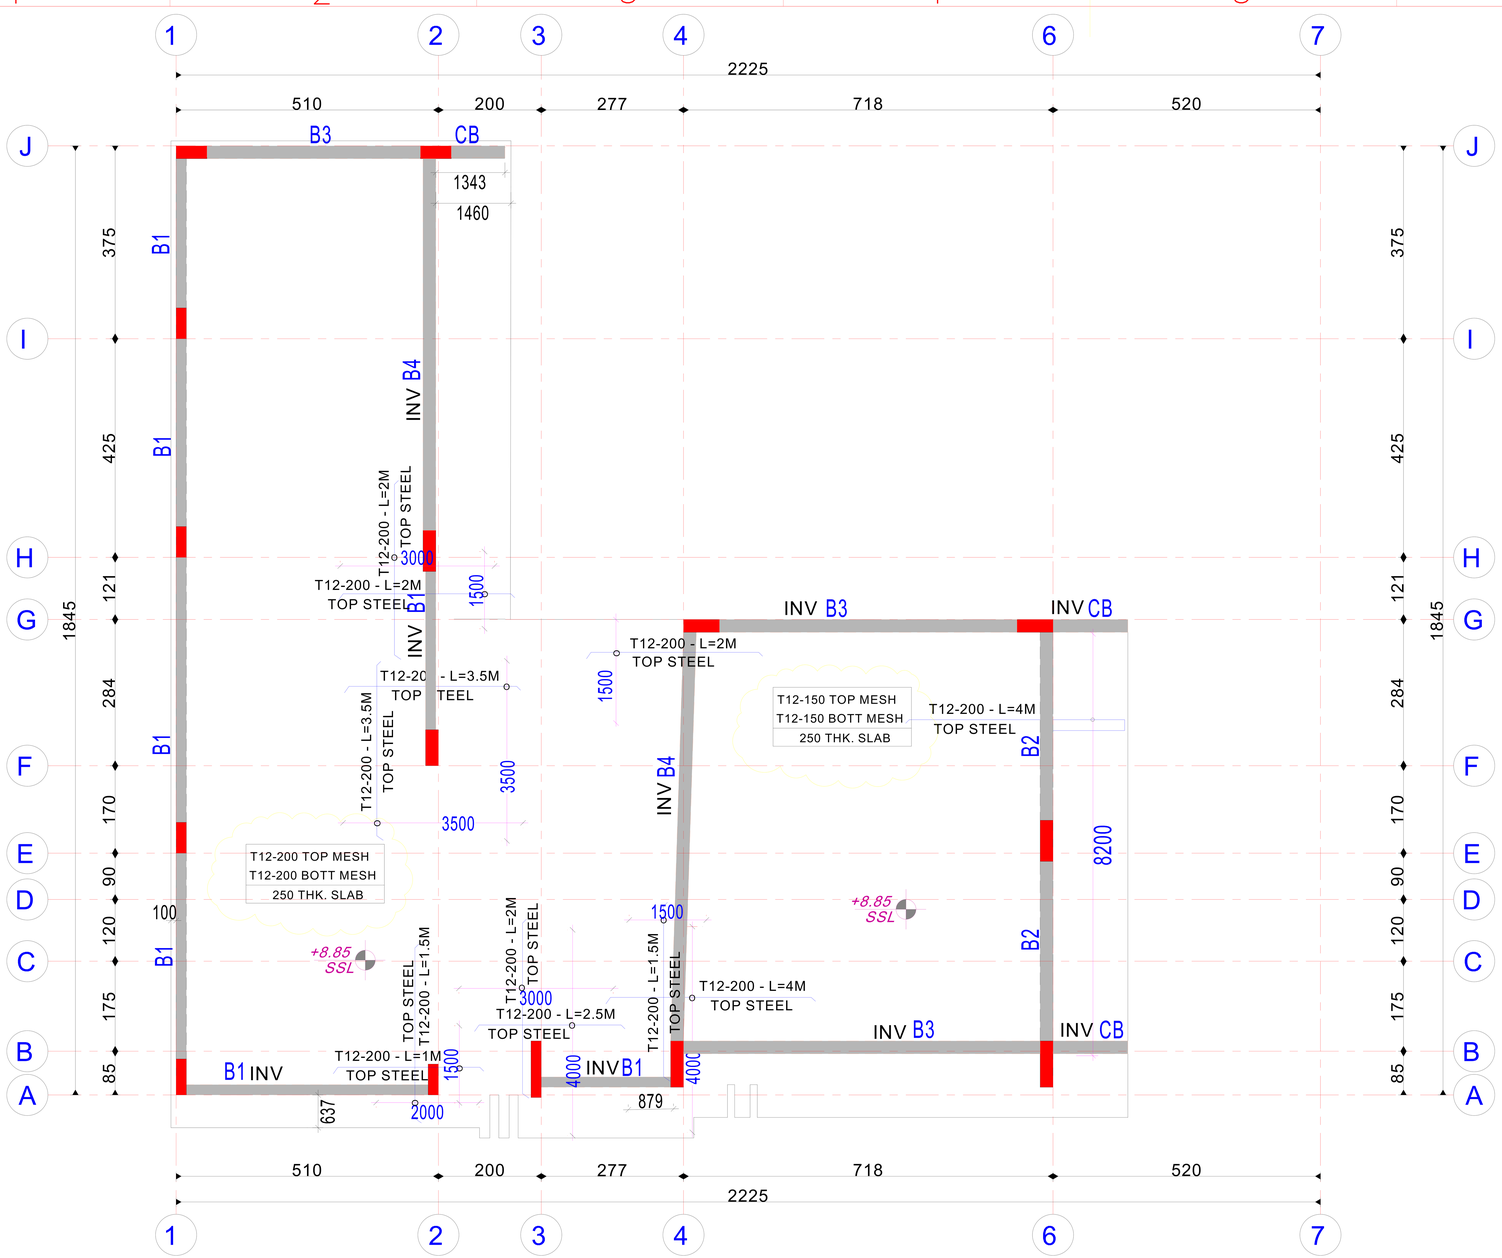

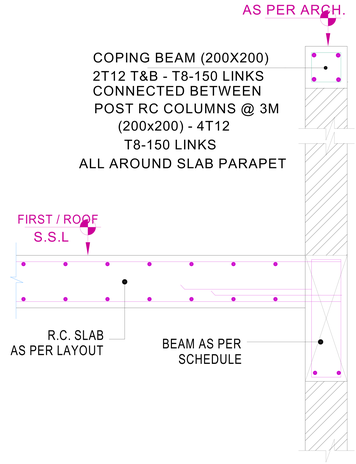

TYPICAL SECTION FOR PARAPET

Govemment Of Ras Al Khaimah
R.A.K. Municipality
Buildings Administration

حكومة رأس الخيمة
دائرة البلدية
إدارة المباني

Approved On — اعتمد في

10 June 2025

Building Permit #: PRMT-24-0004844

Approved By:

STRUCTURAL NOTES	CONCRETE COVERS :
ACI 318-11	Foundations cover = 75mm
F'C/FCU = 28/35 N/mm2	Columns cover = 40mm
FY = 460N/mm2	Walls cover = 30mm
FYt = 420N/mm2	Beams cover = 40mm
	Slabs & Stairs cover = 25mm

SCHEDULE OF FIRST BEAMS

TYPE	BEAM SIZE MM XMM	BOTTOM REINFORCEMENT STRAIGHT (A)	BOTTOM REINFORCEMENT EXTRA @ MID SPAN(B)	TOP REINFORCEMENT STRAIGHT (C)	TOP REINFORCEMENT EXTRA @ CONT. SUPPORT (D)	TOP REINFORCEMENT EXTRA @ DISCONT. SUPPORT (E)	SIDE BARS O.E.F (F) EACH SIDE	STIRRUPS AT SUPPORT OUTER (G1)	STIRRUPS AT SUPPORT INNER (G2)	STIRRUPS AT MIDSPAN OUTER (H1)	STIRRUPS AT MIDSPAN INNER (H2)	NO OF LEGS	REMARKS
B1	200 X 700	2T16	1T16	2T16	1T16	1T16	1T12	T10-150	--------	T10-200	--------	2	
B2	250X 800	3T18	2T16	2T16	2T16	2T16	2T12	T10-150	--------	T10-200	--------	2	
B3	250 X 900	3T16	3T16	3T16	2T16	2T16	3T12	T10-100	--------	T10-200	--------	2	
B4	250 X 1200	3T18	3T18	3T18	3T16	3T16	4T12	T10-100	--------	T10-200	--------	2	
CB	250 X 900	3T16	---------	3T16+2T16			3T12	T10-100	--------	T10-200	--------	2	

Savana
Engineering Consultancy & Interior Design

Client	KHALED ALI SAEED BEN SHUOOM AL SHEHHI		
Project	DOUBLE STORY VILAA		
Drg.Title	FIRST FLOOR SLAB-BEAMS		
Area	ARIFAA	Floortype	
Case ID.	2900429	Draw. Type.	STRC
Sec No.	1	Com. No.	
Block No.		Plot No.	406131922
Bldg. No.	BLD-24-04245	Floor No.	
Date	3/JUNE/2025	Sht. No.	S06
Scale	1/100	Job No.	

G.Manager	Architect	Designed By
ENG AYMEN	ENG IMEN	ENG.IBRAHIM

FIRST FLOOR SLAB-BEAMS