ROOF FLOOR
BLD-26-00570

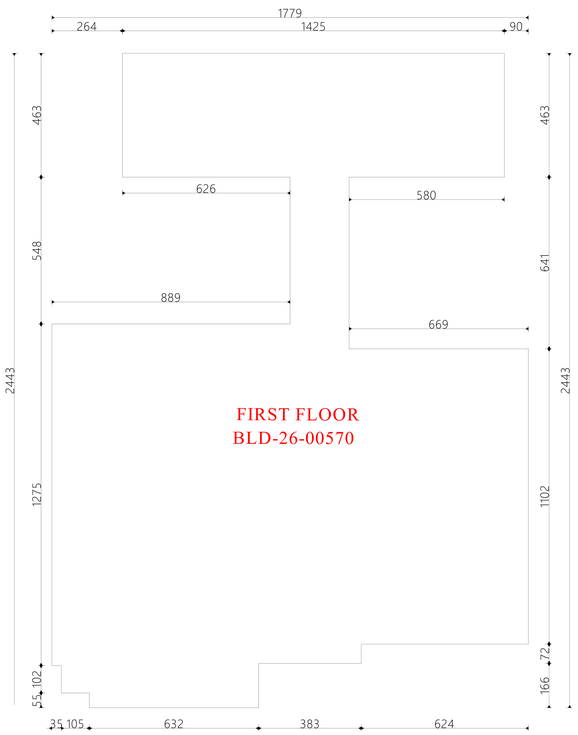

FIRST FLOOR
BLD-26-00570

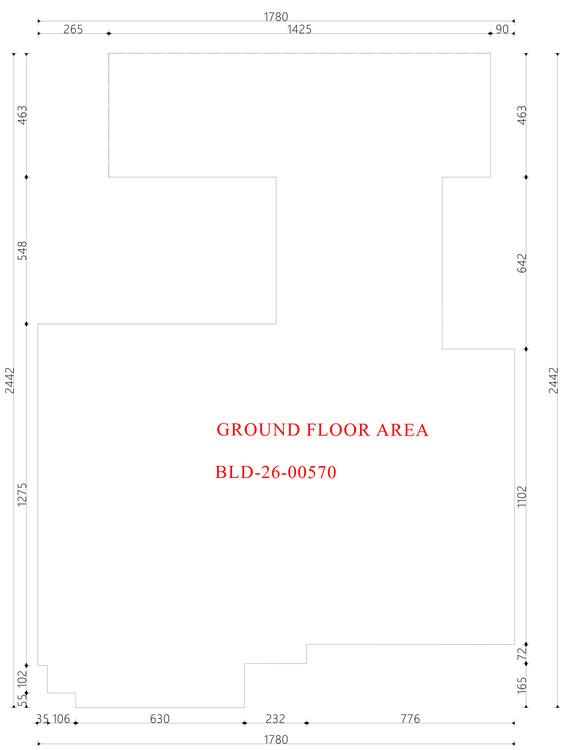

GROUND FLOOR AREA

BLD-26-00570

AREA STATMENTENT

Govemment Of Ras Al Khaimah
R.A.K. Municipality
Buildings Administration

حكومة رأس الخيمة
دائرة البلدية
إدارة المباني

Approved On — **اعتمد في**

20 January 2026

Building Permit #: PRMT-26-0000880

Appoved By:

Area Statement	
Building Number	BLD-26-00570
Ground Floor Area	328.93m²
First Floor Area	304.29m²
ROOF Floor Area	5.20m²
Total Building Area	638.42m²
PLOT AREA ACCORDING TO KRUKI	982.37m²
BUILD UP RATIO	33.45%

Savana
Engineering Consultancy & interior design

Client	MAYED MEERZA BASHEER MOHMMED + ROOF		
Project	DOUBLE STORY VILLA		
Drg.Title	AreaStatement		
Area	AWAFI	Floortype	
Case ID.	3136005	Draw. Type.	ARCH
Sec No.	1	Com. No.	
Block No.		Plot No.	406132098
Bldg. No.	BLD-26-00570	Floor No.	
Date	2026	Sht. No.	A-01
Scale	1/100	Job No.	

G.Manager	Architect	Designed By
ENG AYMEN	ENG IMEN	ENG OMAR

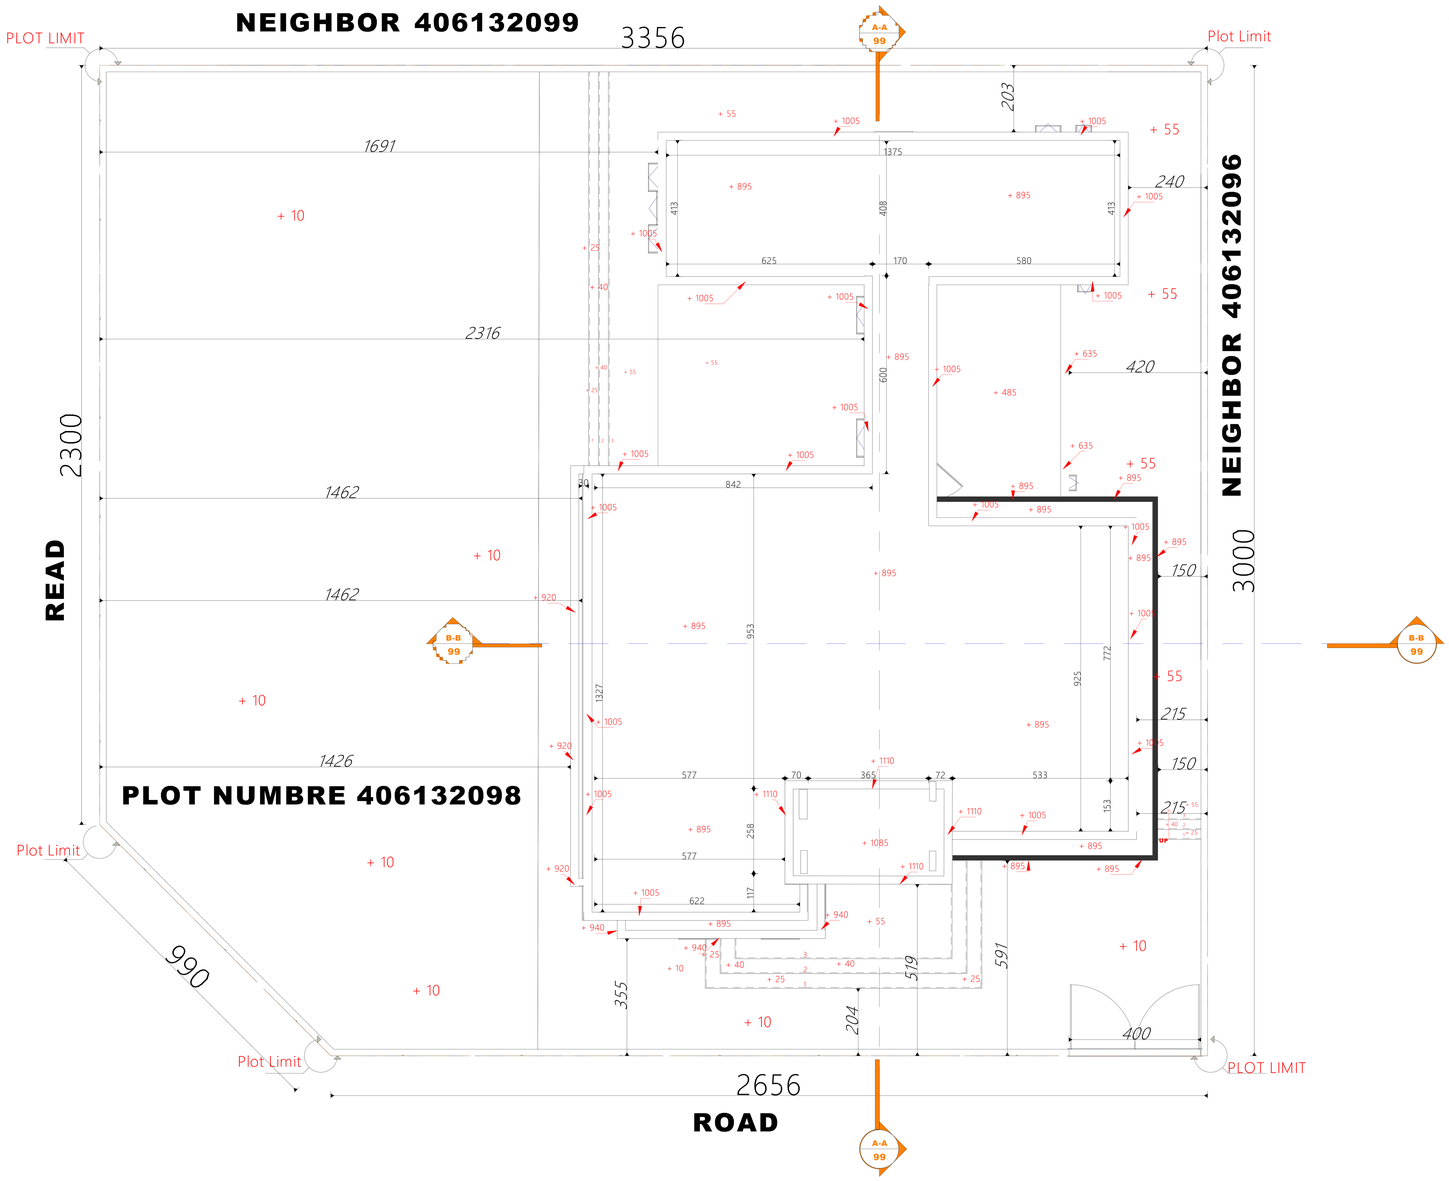

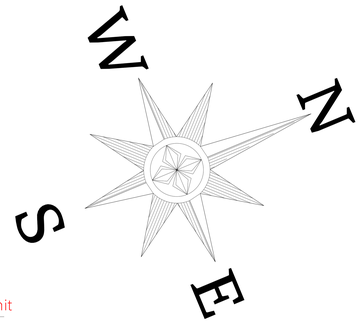

Govemment Of Ras Al Khaimah
R.A.K. Municipality
Buildings Administration

حكومة رأس الخيمة
دائرة البلدية
إدارة المباني

Approved On — اعتمد في

14 January 2026

Building Permit #: PRMT-26-0000880

Appoved By:

Note :-

* Rcc Lintels Must Be Made On Top Of All Doors , Arches And Windows All Of Them Are At Least 0.20 m Thick.
* All Blocks Adjacent To All Doors , Arches And Windows Must Be A Solid Block .

Savana
Engineering Consultancy & interior design

Client	MAYED MEERZA BASHEER MOHMMED + ROOF		
Project	DOUBLE STORY VILLA		
Drg.Title	Site Development Layout Plan		
Area	AWAFI	Floortype	
Case ID.	3136005	Draw. Type.	ARCH
Sec No.	1	Com. No.	
Block No.		Plot No.	406132098
Bldg. No.	BLD-26-00570	Floor No.	
Date	2026	Sht. No.	A02
Scale	1/100	Job No.	

G.Manager	Architect	Designed By
ENG AYMEN	ENG IMEN	ENG OMAR

SITE DEVELOPMENT LAYOUT PLAN

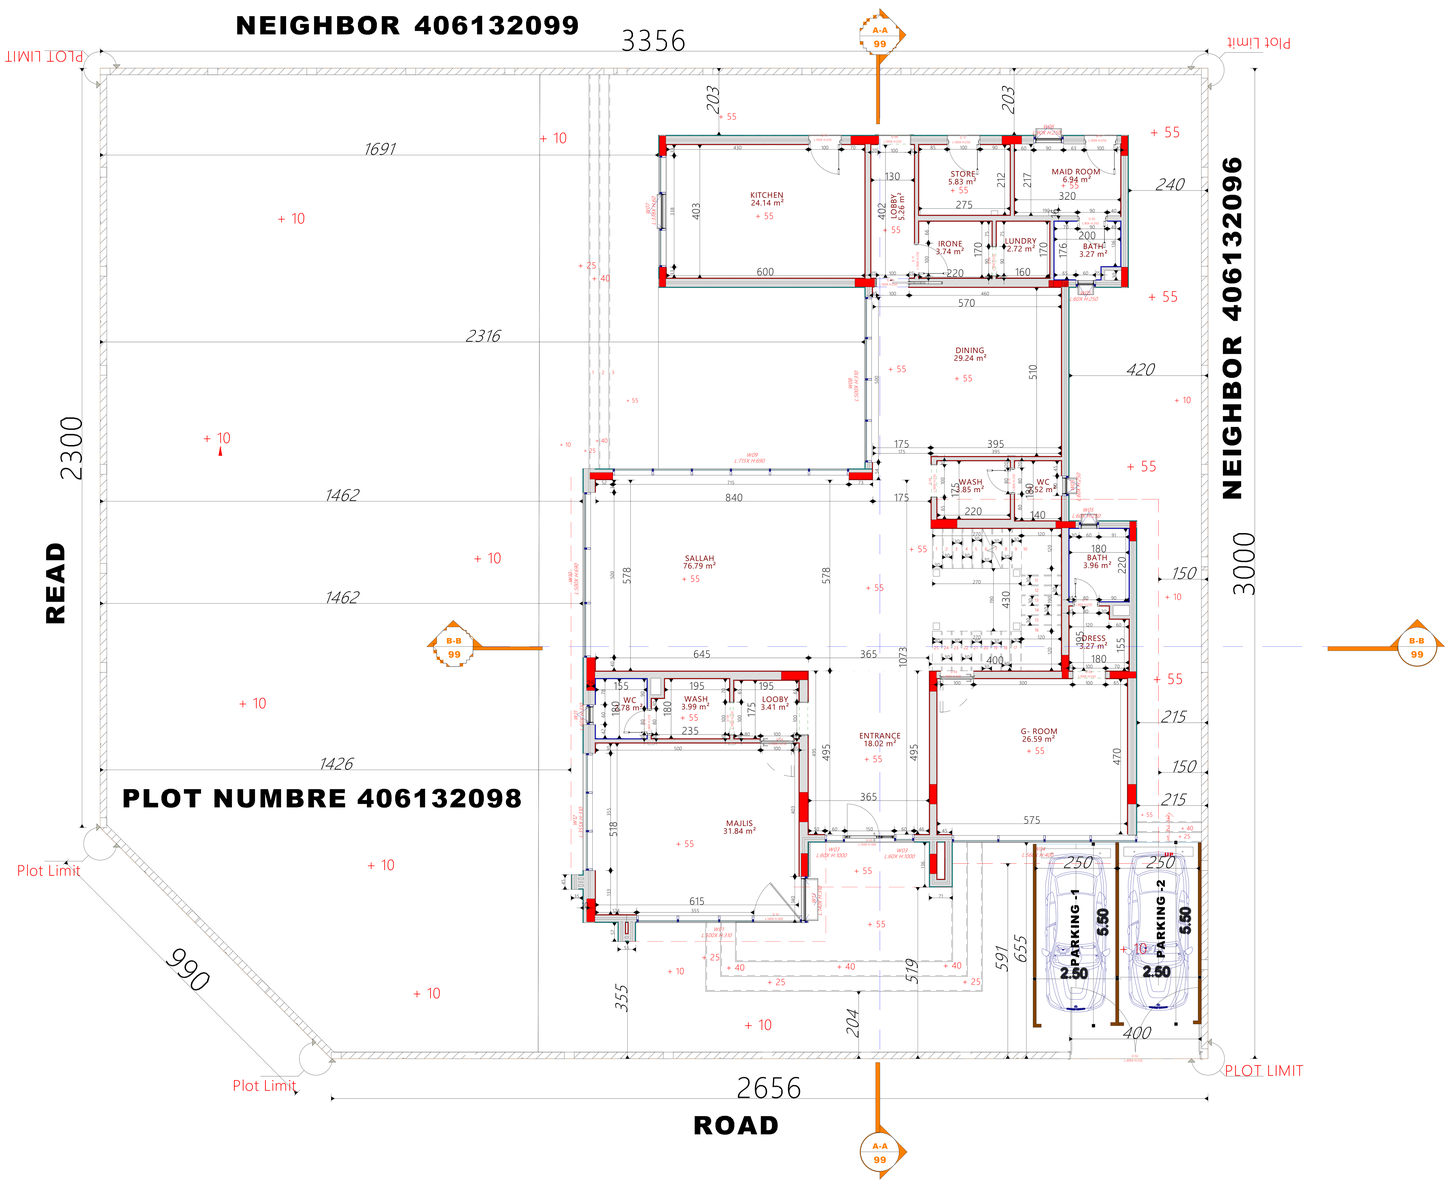

Govement Of Ras Al Khaimah
R.A.K. Municipality
Buildings Administration

حكومة رأس الخيمة
دائرة البلدية
إدارة المباني

Approved On — اعتمد في

28 January 2026

Building Permit #: PRMT-26-0000880

Appoved By:

Savana
Engineering Consultancy & interior design

Client	MAYED MEERZA BASHEER MOHMMED + ROOF		
Project	DOUBLE STORY VILLA		
Drg.Title	SITE SETTING PLAN		
Area	AWAFI	Floortype	
Case ID.	3136005	Draw. Type.	ARCH
Sec No.	1	Com. No.	
Block No.		Plot No.	406132098
Bldg. No.	BLD-26-00570	Floor No.	
Date	2026	Sht. No.	A03
Scale	1/100	Job No.	

G.Manager	Architect	Designed By
ENG AYMEN	ENG IMEN	ENG OMAR

SITE SETTING PLAN

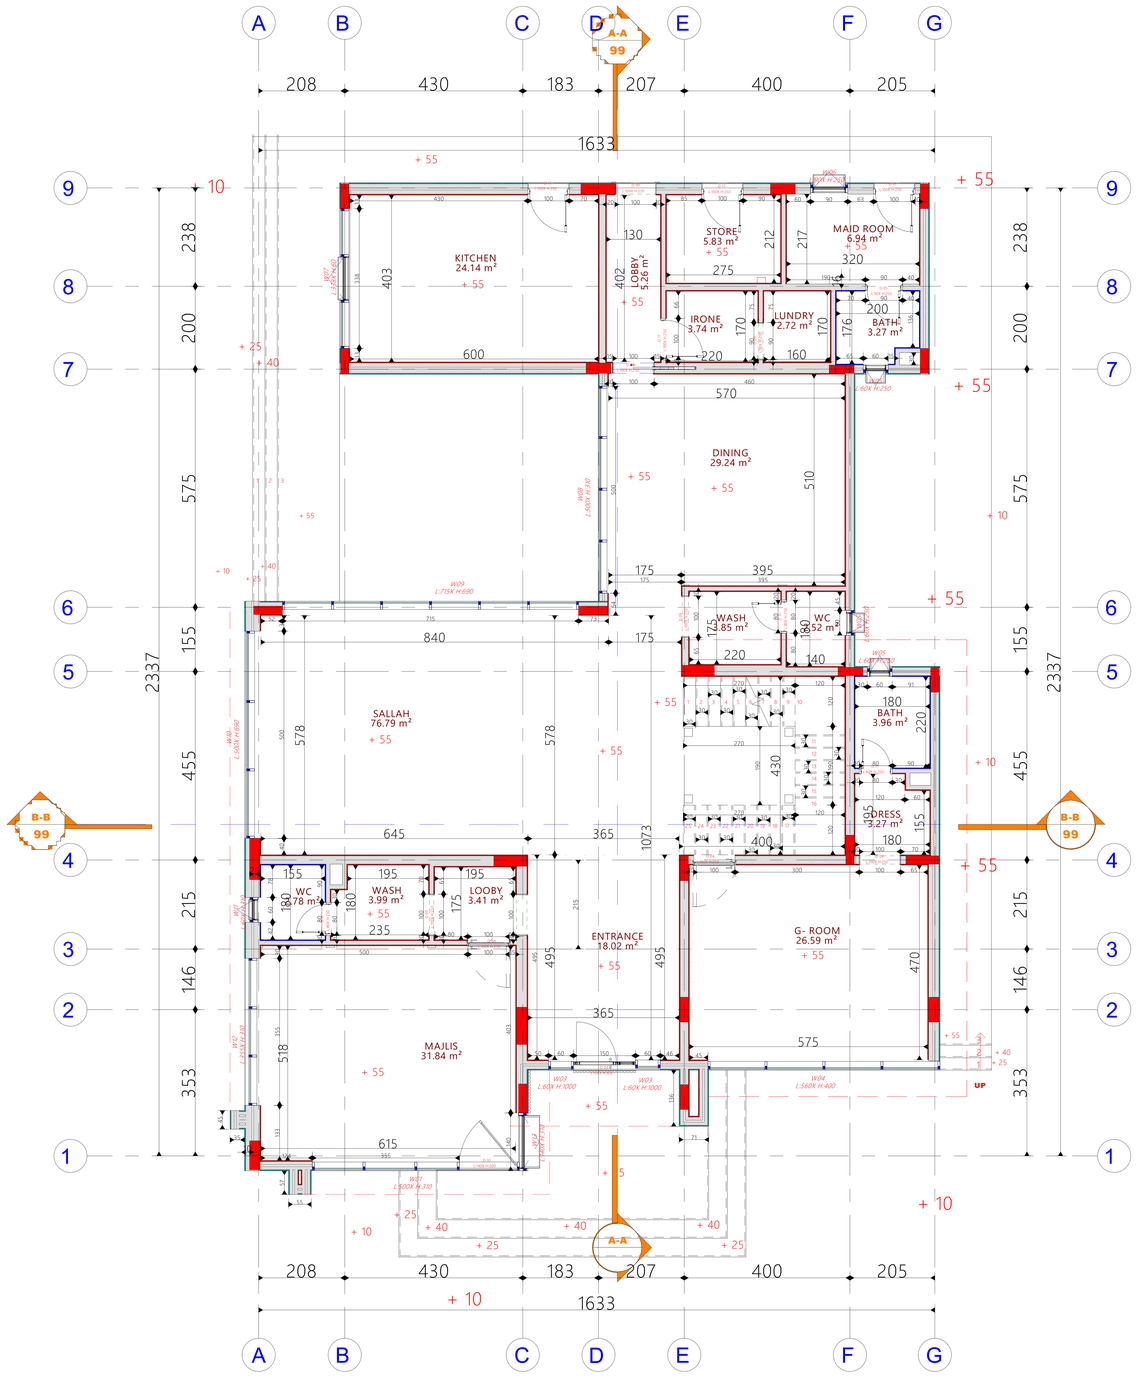

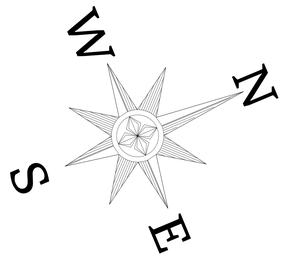

FINISHING FOR VERANDAH	FINISHING FOR DRESSING AREA	FINISHING FOR BATH,WC & WASH
FLOORING		
F3 Marble Tiles	F2 Ceramic Tiles (Non Slippery)	F1 Ceramic glazed tiles
WALLS		
W3 Epoxy paint.	W2 Ceramic tiles up to ceiling	W1 Acrylic emulsion paint
SKIRTING		
S2 Marble tiles 10cm hight	S1 Ceramic Tiles 10cm hight	
CEILING		
C3 Epoxy paint.	C2 Oil Paint.	C1 Acrylic emulsion paint

Govemment Of Ras Al Khaimah
R.A.K. Municipality
Buildings Administration

حكومة رأس الخيمة
دائـرة البلـدية
إدارة المباني

Approved On — اعتمد في

14 January 2026

Building Permit #: PRMT-26-0000880

Appoved By:

Note :-

* Rcc Lintels Must Be Made On Top Of All Doors , Arches And Windows All Of Them Are At Least 0.20 m Thick.
* All Blocks Adjacent To All Doors , Arches And Windows Must Be A Solid Block .

Rooms	Space	Number
Residential	328.93	
Commercial		
Industrial		
Goverment		
Resident.-Comm.		
Total		

Savana
Engineering Consultancy & interior design

Client	MAYED MEERZA BASHEER MOHMMED + ROOF		
Project	DOUBLE STORY VILLA		
Drg.Title	GROUND FLOOR PLAN		
Area	AWAFI	Floortype	G
Case ID.	3136005	Draw. Type.	ARCH
Sec No.	1	Com. No.	
Block No.		Plot No.	406132098
Bldg. No.	BLD-26-00570	Floor No.	01
Date	2026	Sht. No.	A04
Scale	1/100	Job No.	

G.Manager	Architect	Designed By
ENG AYMEN	ENG IMEN	ENG OMAR

GROUND FLOOR PLAN

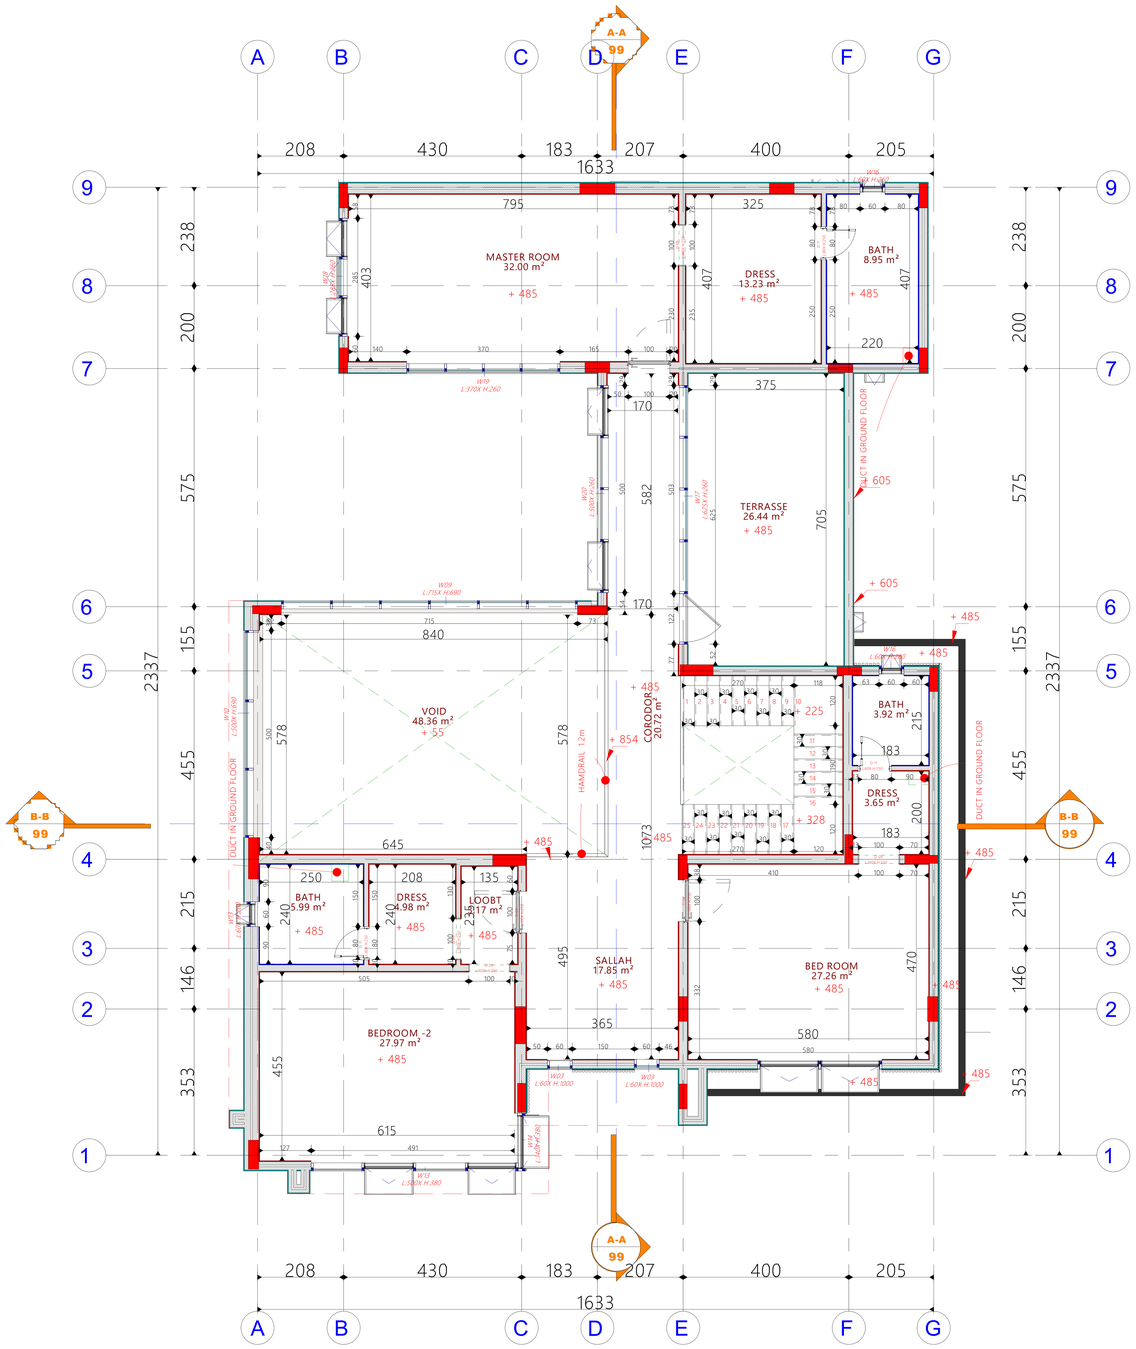

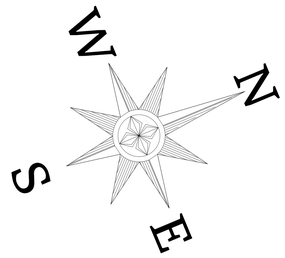

Govemment Of Ras Al Khaimah
R.A.K. Municipality
Buildings Administration

حكومة رأس الخيمة
دائـرة البلـدية
إدارة المباني

Approved On — اعتمد في

14 January 2026

Building Permit #: PRMT-26-0000880

Appoved By:

Note :-

* Rcc Lintels Must Be Made On Top Of All Doors , Arches And Windows All Of Them Are At Least 0.20 m Thick.
* All Blocks Adjacent To All Doors , Arches And Windows Must Be A Solid Block .

Rooms	Space	Number
Residential	304.29	
Commercial		
Industrial		
Goverment		
Resident.-Comm.		
Total		

Savana
Engineering Consultancy & interior design

Client	MAYED MEERZA BASHEER MOHMMED + ROOF		
Project	DOUBLE STORY VILLA		
Drg.Title	FIRST FLOOR PLAN		
Area	AWAFI	Floortype	F
Case ID.	3136005	Draw. Type.	ARCH
Sec No.	1	Com. No.	
Block No.		Plot No.	406132098
Bldg. No.	BLD-26-00570	Floor No.	01
Date	2026	Sht. No.	A05
Scale	1/100	Job No.	

G.Manager	Architect	Designed By
ENG AYMEN	ENG IMEN	ENG OMAR

FIRST FLOOR PLAN

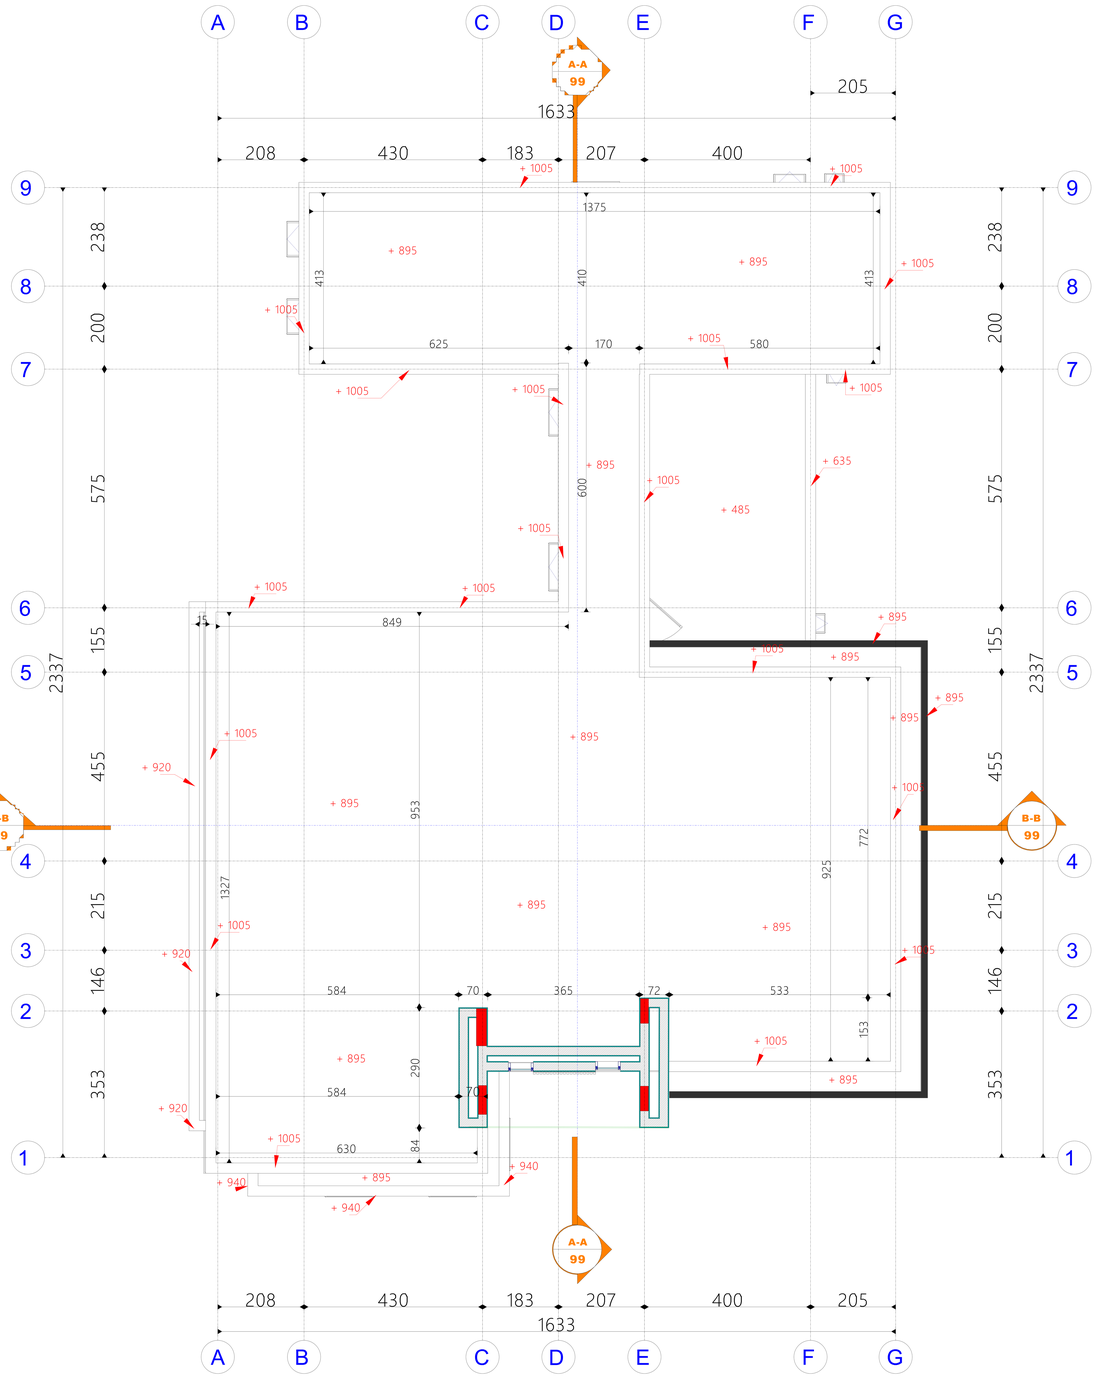

N

S

E

FINISHING FOR VERANDAH	FINISHING FOR DRESSING AREA	FINISHING FOR BATH,WC & WASH	
F3 Marble Tiles	F2 Ceramic Tiles (Non Slippery)	F1 Ceramic glazed tiles	FLOORING
W3 Epoxy paint.	W2 Ceramic tiles up to ceiling	W1 Acrylic emulsion paint	WALLS
	S2 Marble tiles 10cm hight	S1 Ceramic Tiles 10cm hight	SKIRTING
C3 Epoxy paint.	C2 Oil Paint.	C1 Acrylic emulsion paint	CEILING

Govemment Of Ras Al Khaimah
R.A.K. Municipality
Buildings Administration

حكومة رأس الخيمة
دائرة البلدية
إدارة المباني

Approved On — اعتمد في

14 January 2026

Building Permit #: PRMT-26-0000880

Appoved By:

Rooms	Space	Number
Residential	5.20	
Commercial		
Industrial		
Goverment		
Resident.-Comm.		
Total		

Savana
Engineering Consultancy & interior design

Client	MAYED MEERZA BASHEER MOHMMED + ROOF		
Project	DOUBLE STORY VILLA		
Drg.Title	ROOF PLAN		
Area	AWAFI	Floortype	R
Case ID.	3136005	Draw. Type.	ARCH
Sec No.	1	Com. No.	
Block No.		Plot No.	406132098
Bldg. No.	BLD-26-00570	Floor No.	01
Date	2026	Sht. No.	A06
Scale	1/100	Job No.	

G.Manager	Architect	Designed By
ENG AYMEN	ENG IMEN	ENG OMAR

ROOF FLOOR PLAN

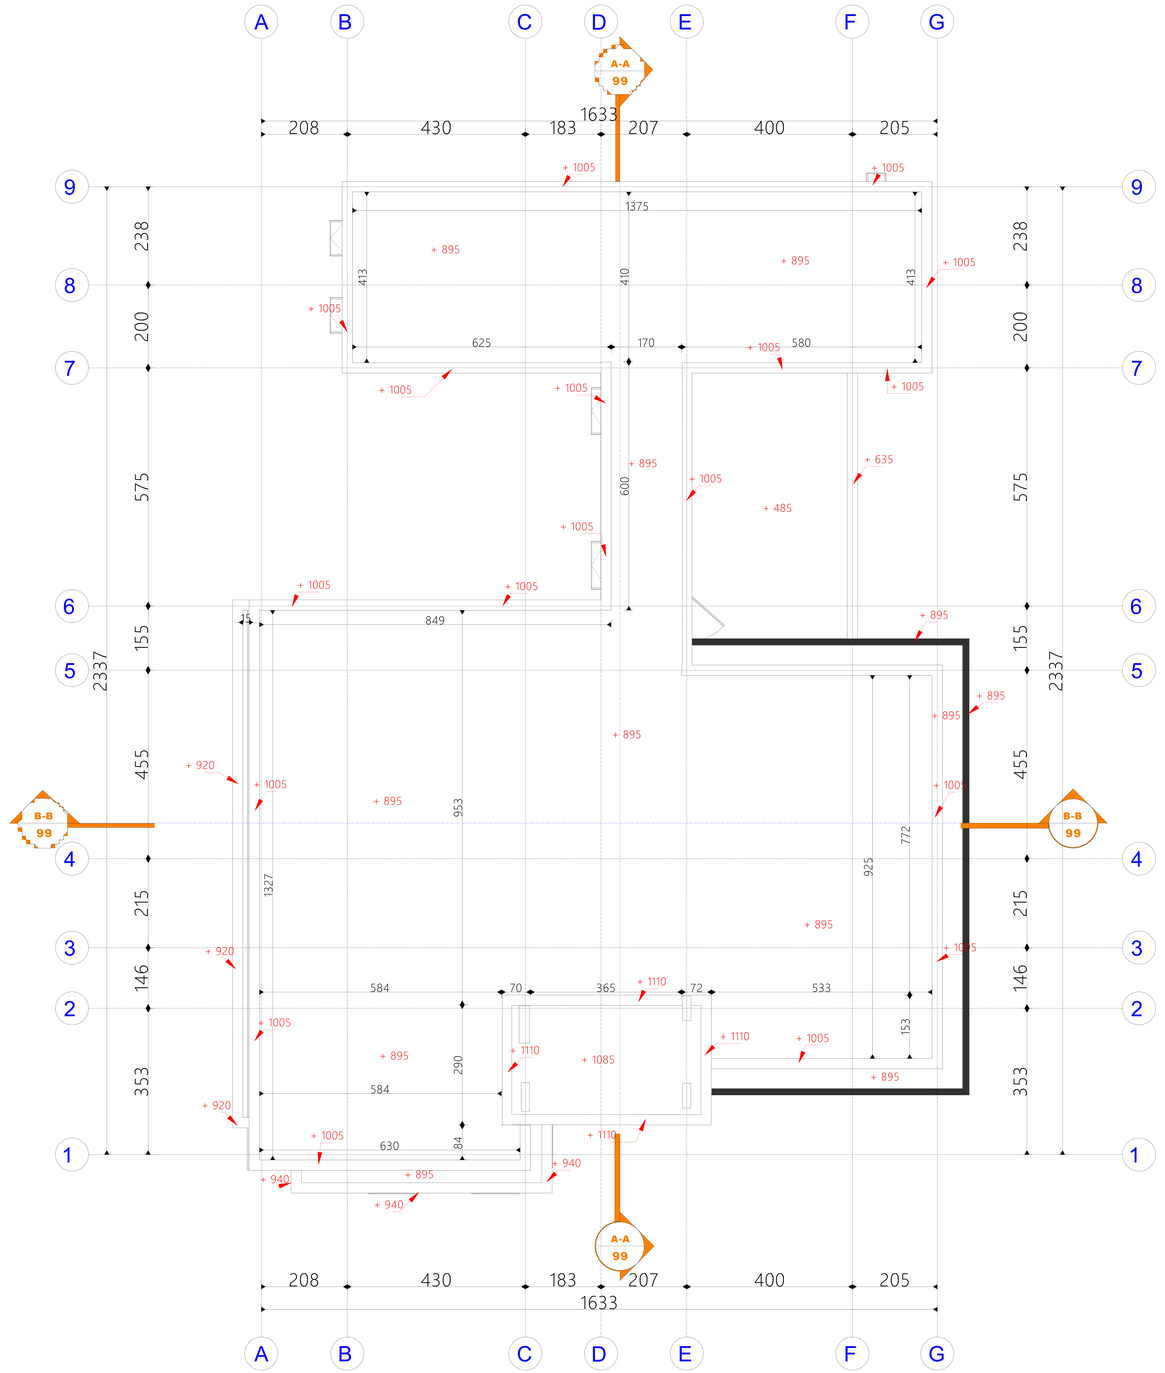

N

S

E

W

FINISHING FOR VERANDAH	FINISHING FOR DRESSING AREA	FINISHING FOR BATH,WC & WASH
C3 F3 W3 S2	C1 F1 W1 S1	C2 F2 W2 S2

FLOORING	F3 Marble Tiles	F2 Ceramic Tiles (Non Slippery)
		F1 Ceramic glazed tiles
WALLS	W3 Epoxy paint.	W2 Ceramic tiles up to ceiling
		W1 Acrylic emulsion paint
SKIRTING	S2 Marble tiles 10cm hight	S1 Ceramic Tiles 10cm hight
CEILING	C3 Epoxy paint.	C2 Oil Paint.
		C1 Acrylic emulsion paint

Govemment Of Ras Al Khaimah
R.A.K. Municipality
Buildings Administration

حكومة رأس الخيمة
دائرة البلدية
إدارة المباني

Approved On — اعتمد في

14 January 2026

Building Permit #: PRMT-26-0000880

Approved By:

Savana
Engineering Consultancy & interior design

Client	MAYED MEERZA BASHEER MOHMMED + ROOF		
Project	DOUBLE STORY VILLA		
Drg.Title	TOP ROOF PLAN		
Area	AWAFI	Floortype	
Case ID.	3136005	Draw. Type.	ARCH
Sec No.	1	Com. No.	
Block No.		Plot No.	406132098
Bldg. No.	BLD-26-00570	Floor No.	
Date	2026	Sht. No.	A06A
Scale	1/100	Job No.	

G.Manager	Architect	Designed By
ENG AYMEN	ENG IMEN	ENG OMAR

TOP ROOF FLOOR PLAN

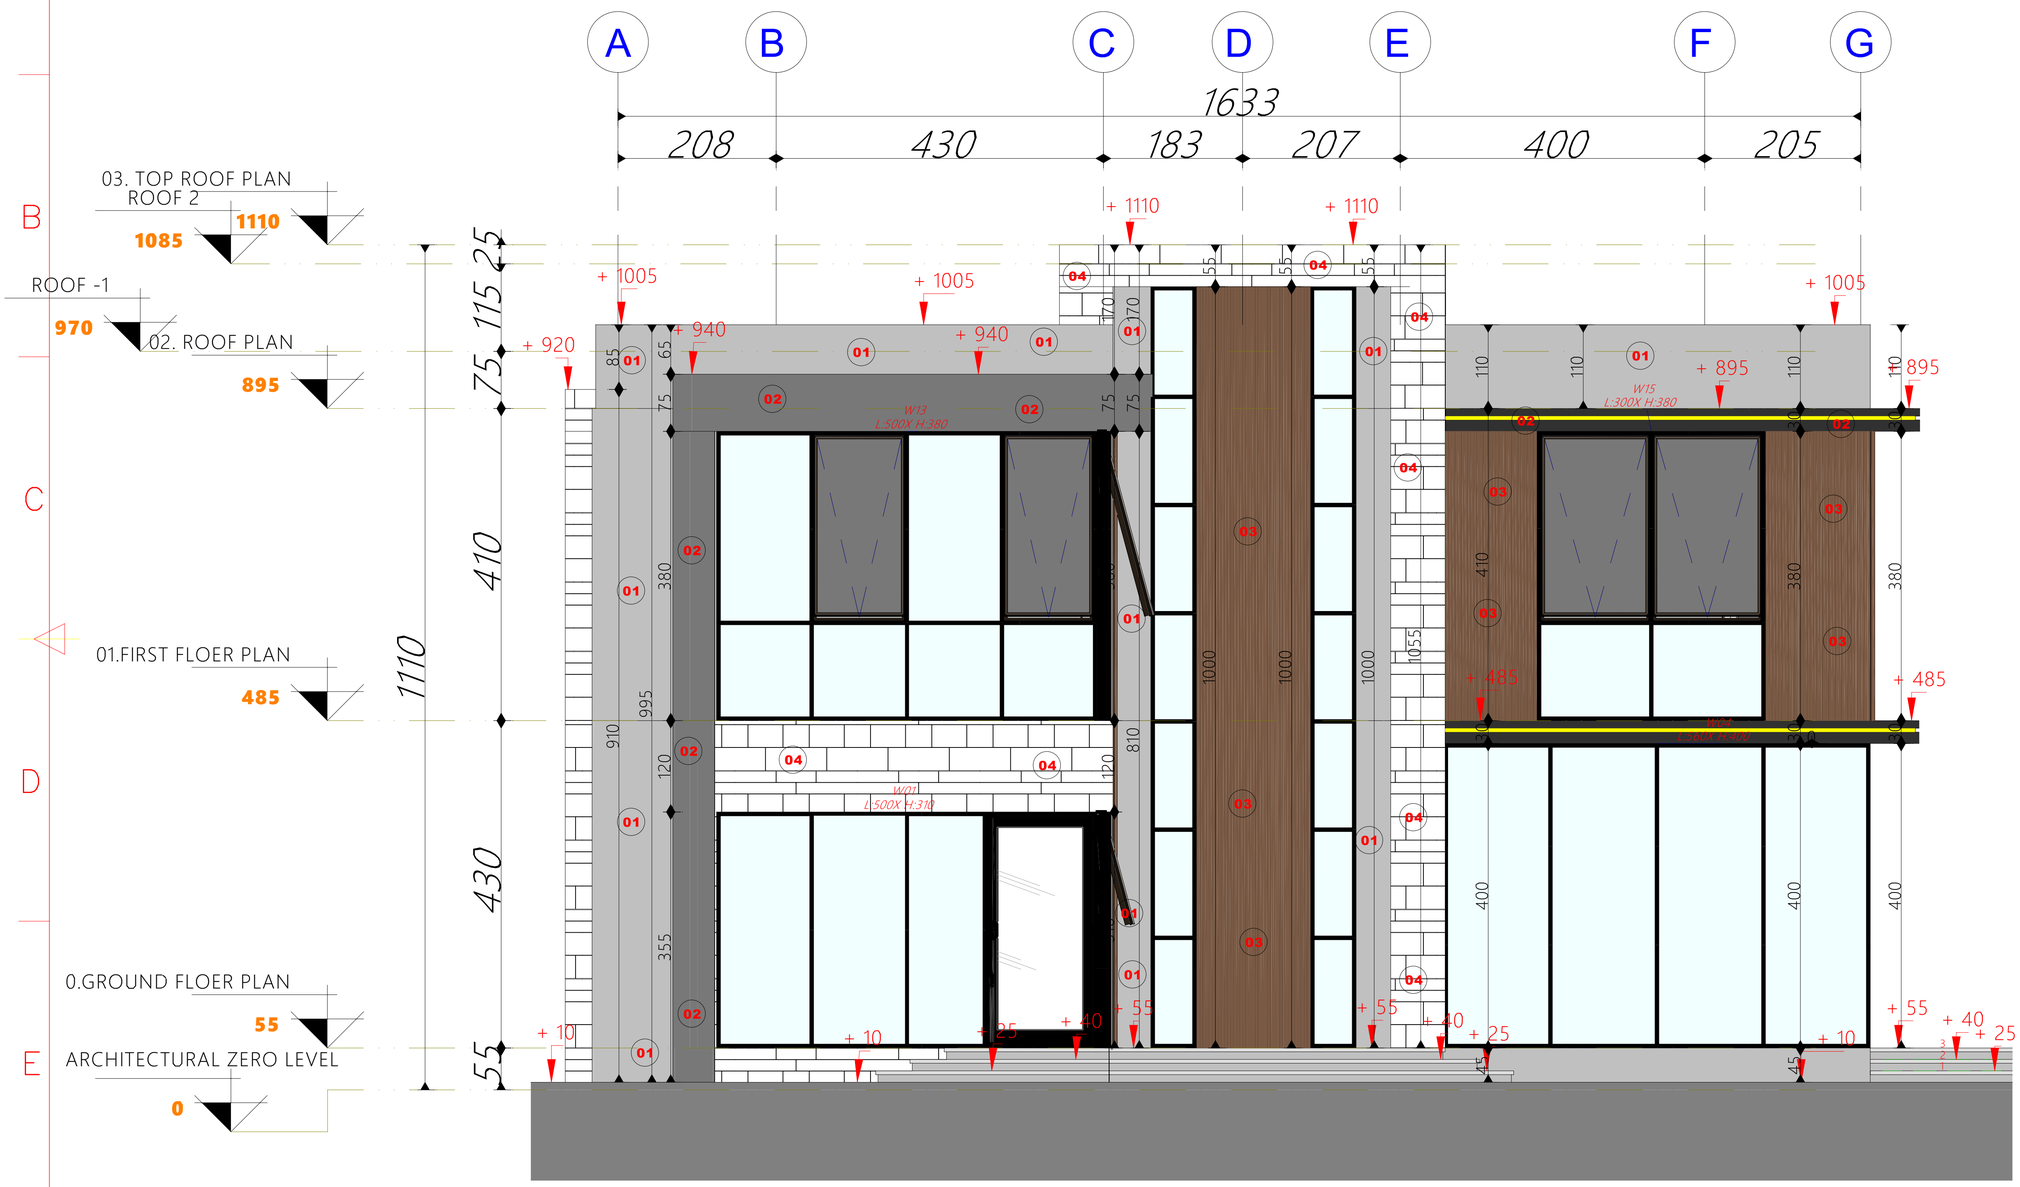

FRONT ELEVATION

Govemment Of Ras Al Khaimah
R.A.K. Municipality
Buildings Administration

حكومة رأس الخيمة
دائرة البلدية
إدارة المباني

Approved On — اعتمد في

14 January 2026

Building Permit #: PRMT-26-0000880

Appoved By:

FINSHING	
1	FULL EPOXY PAINT [white]
2	WOOD Aluminum
3	FULL EPOXY BLACK PAINT
4	

Savana
Engineering Consultancy & interior design

Client	MAYED MEERZA BASHEER MOHMMED + ROOF		
Project	DOUBLE STORY VILLA		
Drg.Title	FRONT ELEVATION		
Area	AWAFI	Floortype	
Case ID.	3136005	Draw. Type.	ARCH
Sec No.	1	Com. No.	
Block No.		Plot No.	406132098
Bldg. No.	BLD-26-00570	Floor No.	
Date	2026	Sht. No.	A07
Scale	1/100	Job No.	

G.Manager	Architect	Designed By
ENG AYMEN	ENG IMEN	ENG OMAR

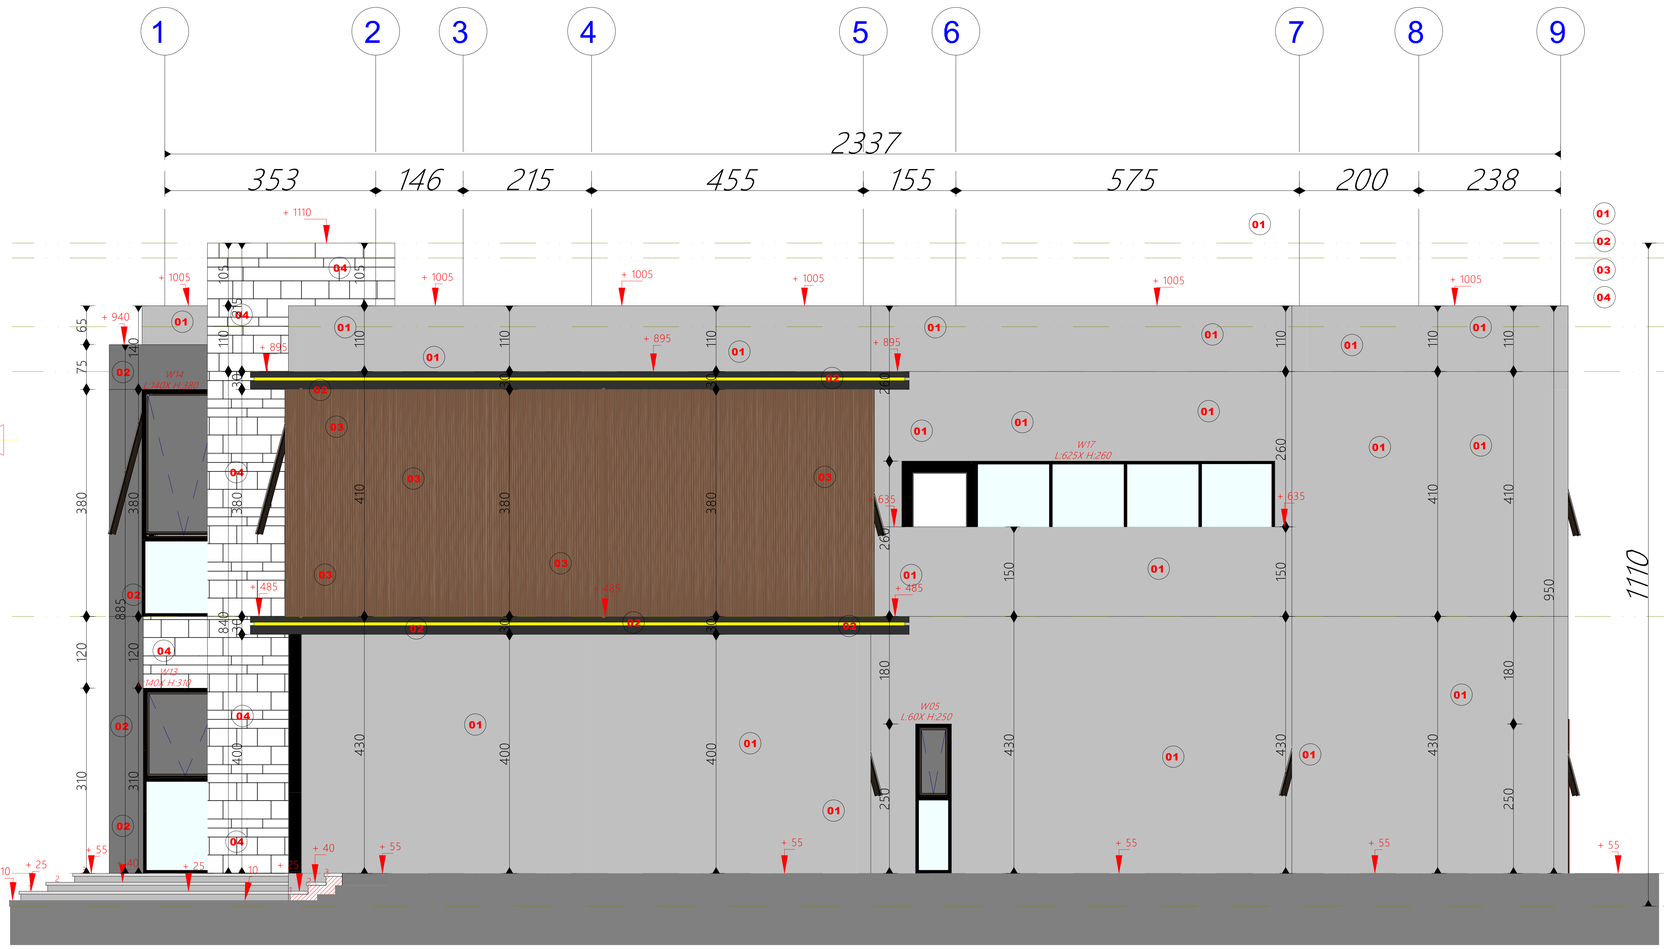

Govemment Of Ras Al Khaimah
R.A.K. Municipality
Buildings Administration

حكومة رأس الخيمة
دائرة البلدية
إدارة المباني

Approved On — اعتمد في

14 January 2026

Building Permit #: PRMT-26-0000880

Appoved By:

FINSHING	
1	FULL EPOXY PAINT [white]
2	WOOD Aluminum
3	FULL EPOXY BLACK PAINT
4	

Savana
Engineering Consultancy & interior design

Client	MAYED MEERZA BASHEER MOHMMED + ROOF		
Project	DOUBLE STORY VILLA		
Drg.Title	RIGHT ELEVATION		
Area	AWAFI	Floortype	
Case ID.	3136005	Draw. Type.	ARCH
Sec No.	1	Com. No.	
Block No.		Plot No.	406132098
Bldg. No.	BLD-26-00570	Floor No.	
Date	2026	Sht. No.	A08
Scale	1/100	Job No.	

G.Manager	Architect	Designed By
ENG AYMEN	ENG IMEN	ENG OMAR

RIGHT ELEVATION

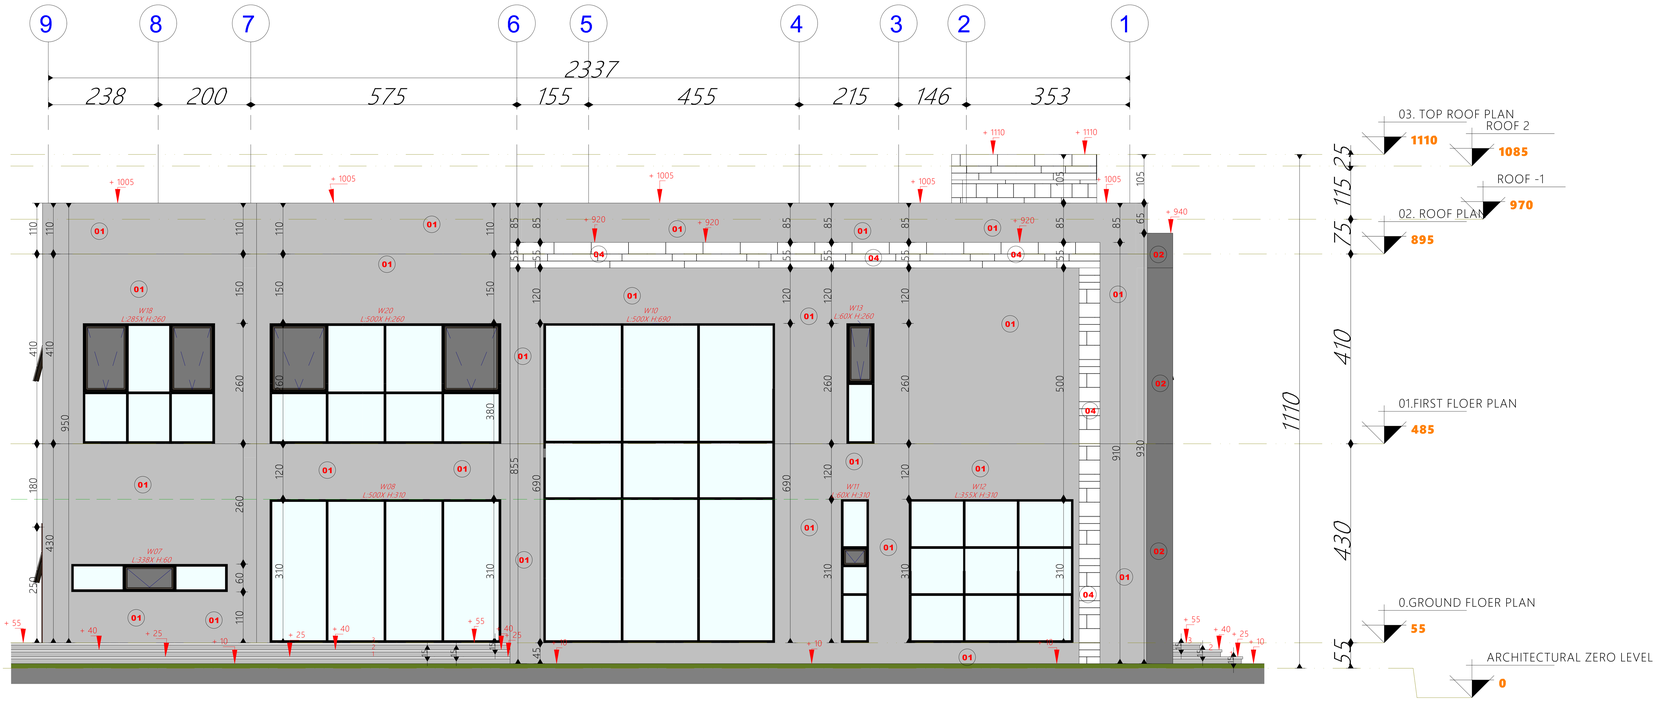

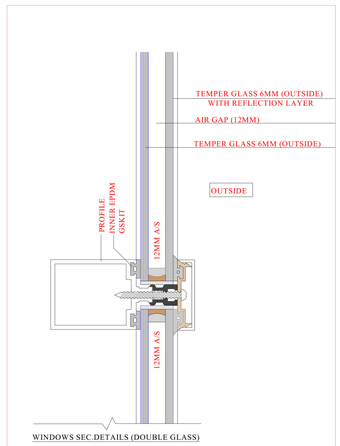

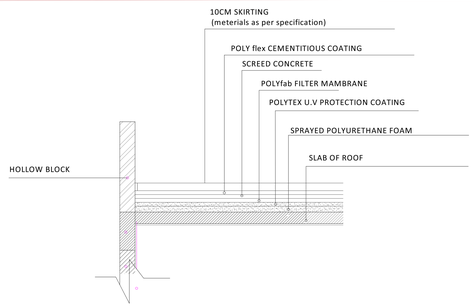

DETAIL FOR COMBO SYSTEM
U-VALUE <0.3 W/M2 K

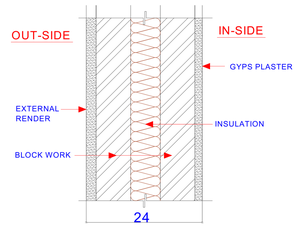

As per E. Walls Predefined Section:	W - 1 - A
DETAIL "W1"	TYPICAL FOR EXTERNAL WALL USING INSULATED CONC. BLOCK (200 mm) U-VALUE < 0.5 W/M2 K

LEFT ELEVATION

Govemment Of Ras Al Khaimah
R.A.K. Municipality
Buildings Administration

حكومة رأس الخيمة
دائرة البلدية
إدارة المباني

Approved On — اعتمد في

14 January 2026

Building Permit #: PRMT-26-0000880

Appoved By:

* Rcc Lintels Must Be Made On Top Of All Doors , Arches And Windows All Of Them Are At Least 0.20 m Thick.
* All Blocks Adjacent To All Doors , Arches And Windows Must Be A Solid Block .

U VALUE AND SHGC

ALL GLASS MUST BE DOUBLE UNITES

GLASS SPECIFICATION:-

U-value (w/m2.k)<_ 1.8

SHADING CO- EFFICIENT (SC) <0.3

FINSHING	
1	FULL EPOXY PAINT [white]
2	WOOD Aluminum
3	FULL EPOXY BLACK PAINT
4	

Savana
Engineering Consultancy & interior design

Client	MAYED MEERZA BASHEER MOHMMED + ROOF		
Project	DOUBLE STORY VILLA		
Drg.Title	LIFT ELEVATION		
Area	AWAFI	Floortype	
Case ID.	3136005	Draw. Type.	ARCH
Sec No.	1	Com. No.	
Block No.		Plot No.	406132098
Bldg. No.	BLD-26-00570	Floor No.	
Date	2026	Sht. No.	A09
Scale	1/100	Job No.	

G.Manager	Architect	Designed By
ENG AYMEN	ENG IMEN	ENG OMAR

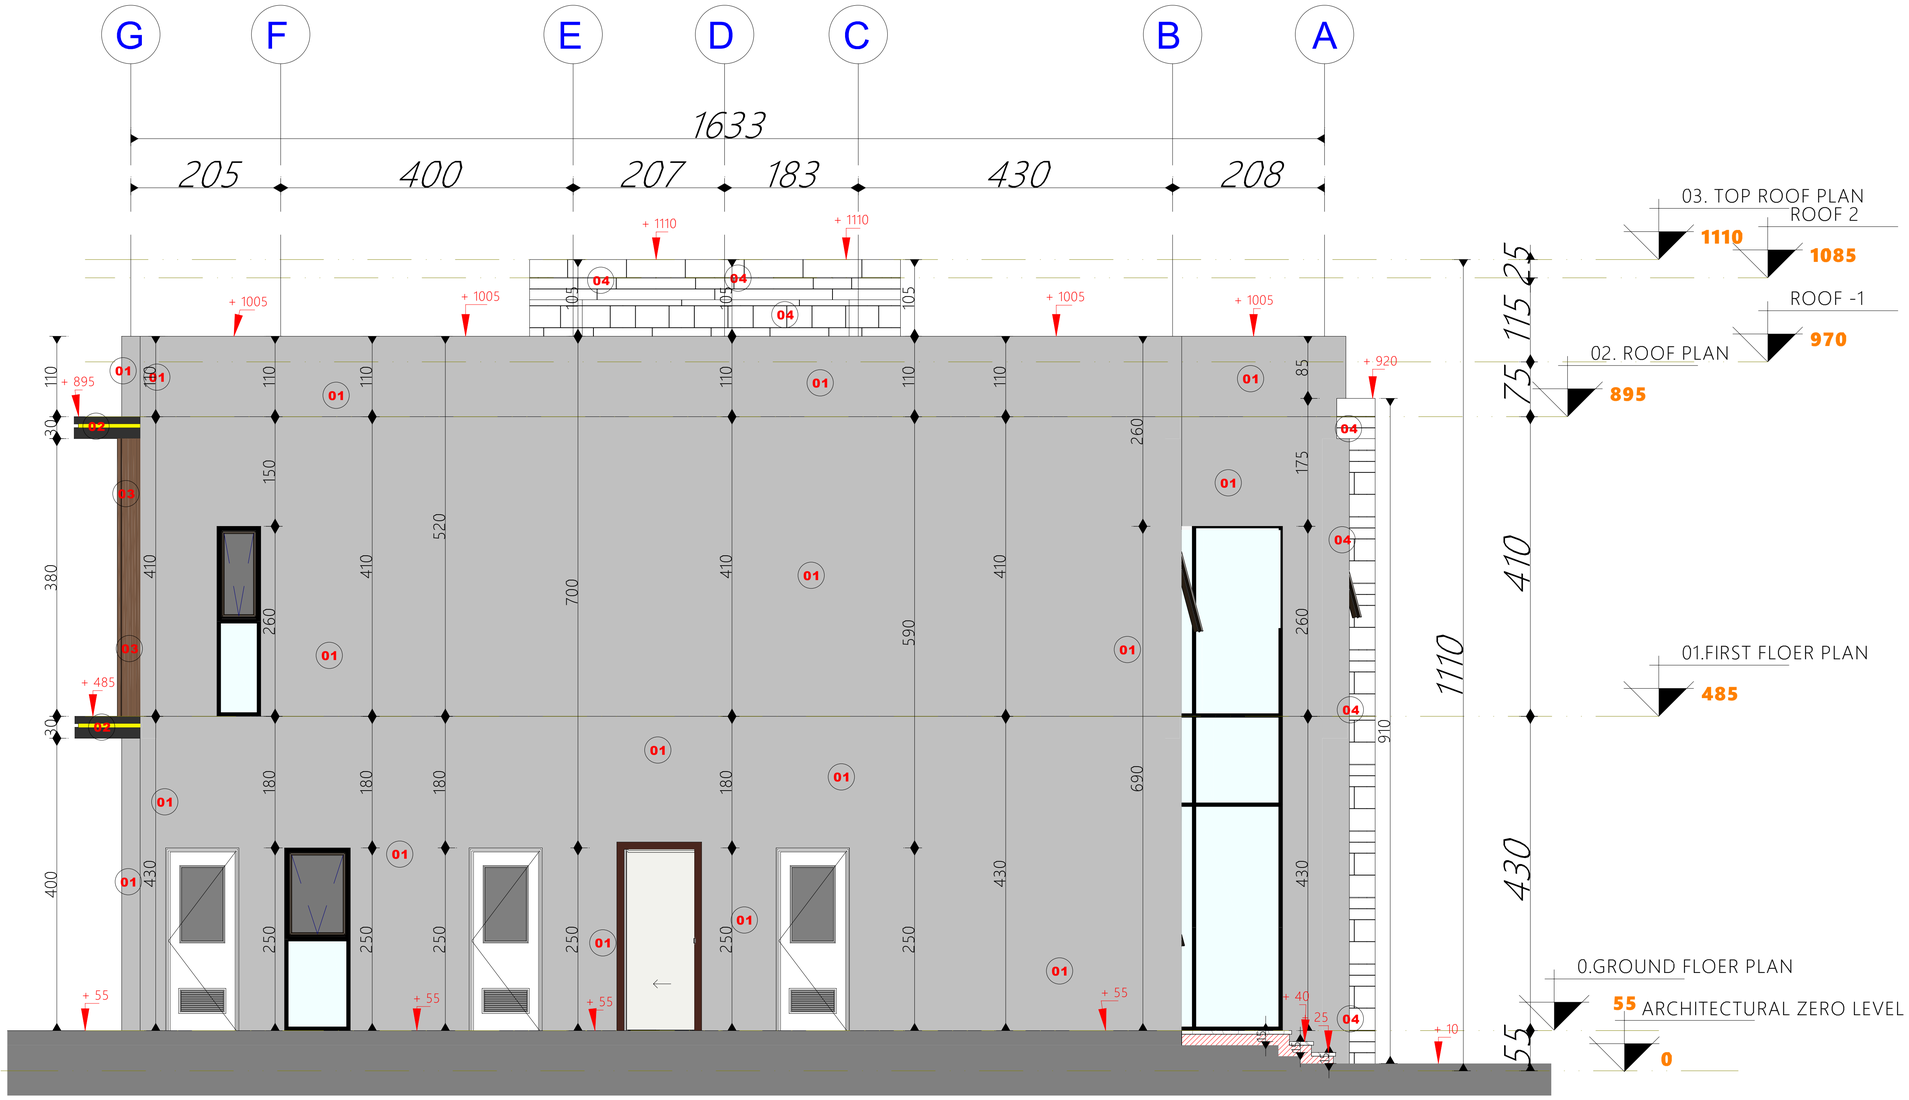

REAR ELEVATION

Govemment Of Ras Al Khaimah
R.A.K. Municipality
Buildings Administration

حكومة رأس الخيمة
دائرة البلدية
إدارة المباني

Approved On
اعتمد في

14 January 2026

Building Permit #: PRMT-26-0000880

Appoved By:

FINSHING	
1	FULL EPOXY PAINT [white]
2	WOOD Aluminum
3	FULL EPOXY BLACK PAINT
4	

Savana
Engineering Consultancy & interior design

Client	MAYED MEERZA BASHEER MOHMMED + ROOF		
Project	DOUBLE STORY VILLA		
Drg.Title	REAR ELEVATION		
Area	AWAFI	Floortype	
Case ID.	3136005	Draw. Type.	ARCH
Sec No.	1	Com. No.	
Block No.		Plot No.	406132098
Bldg. No.	BLD-26-00570	Floor No.	
Date	2026	Sht. No.	A10
Scale	1/100	Job No.	

G.Manager	Architect	Designed By
ENG AYMEN	ENG IMEN	ENG OMAR

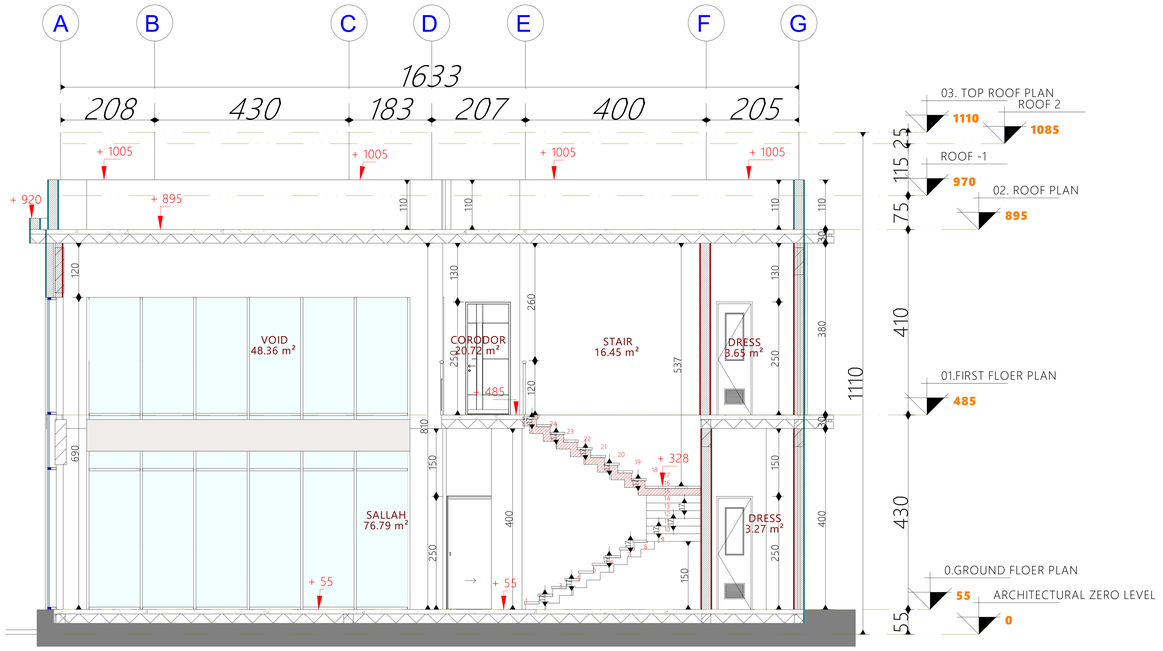

SECTION A-A

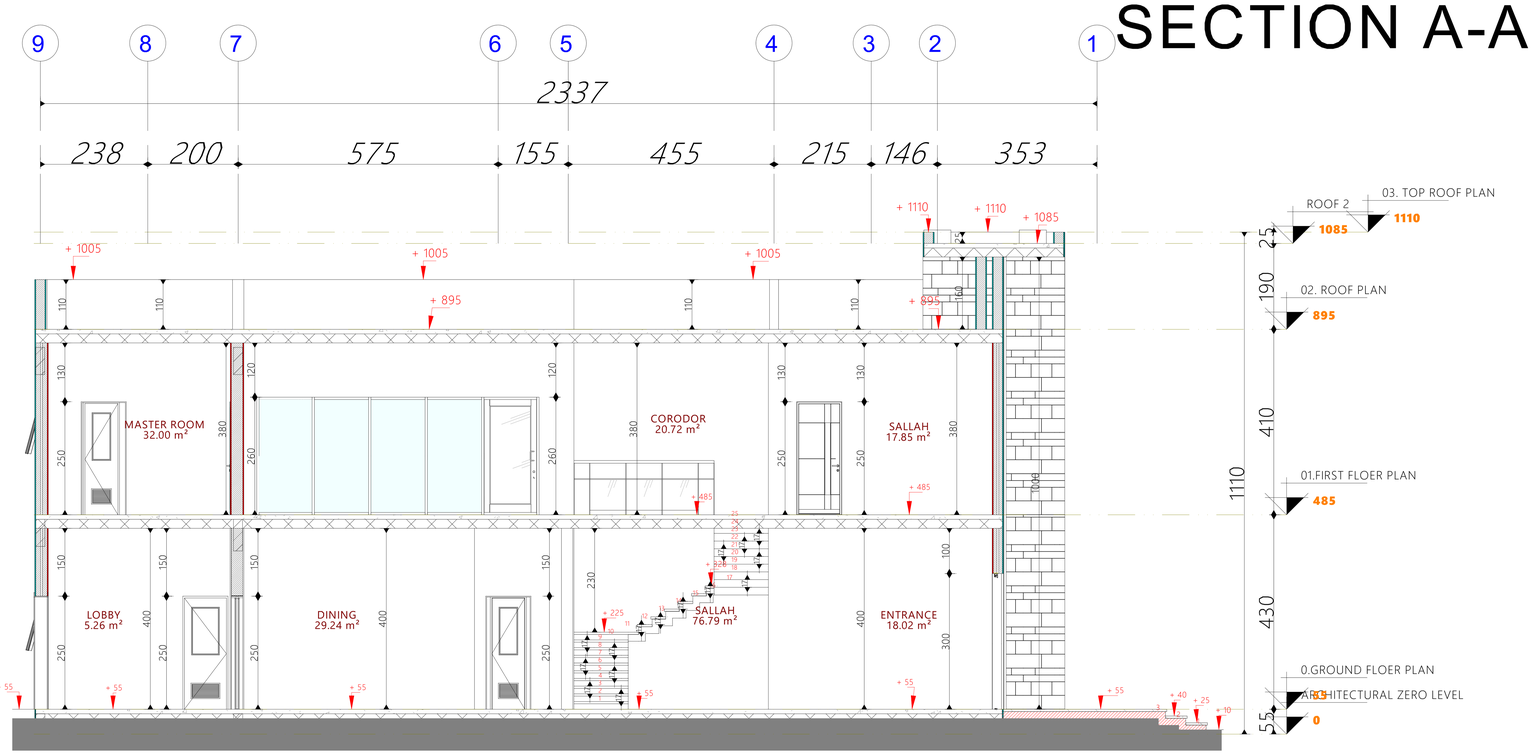

SECTION B-B

Govemment Of Ras Al Khaimah
R.A.K. Municipality
Buildings Administration

حكومة رأس الخيمة
دائرة البلدية
إدارة المباني

Approved On — اعتمد في

14 January 2026

Building Permit #: PRMT-26-0000880

Appoved By:

ALL GLASS MUST BE DOUBLE UNITES

GLASS SPECIFICATION:-

U-value (w/m2.k)<_ 1.8

SHADING CO- EFFICIENT (SC) <0.3

FINSHING	
1	FULL EPOXY PAINT [white]
2	FULL EPOXY BLACK PAINT
3	WOOD Aluminum
4	

Savana
Engineering Consultancy & interior design

Client	MAYED MEERZA BASHEER MOHMMED + ROOF		
Project	DOUBLE STORY VILLA		
Drg.Title	SECTION		
Area	AWAFI	Floortype	
Case ID.	3136005	Draw. Type.	ARCH
Sec No.	1	Com. No.	
Block No.		Plot No.	406132098
Bldg. No.	BLD-26-00570	Floor No.	
Date	2026	Sht. No.	A12
Scale	1/100	Job No.	

G.Manager	Architect	Designed By
ENG AYMEN	ENG IMEN	ENG OMAR

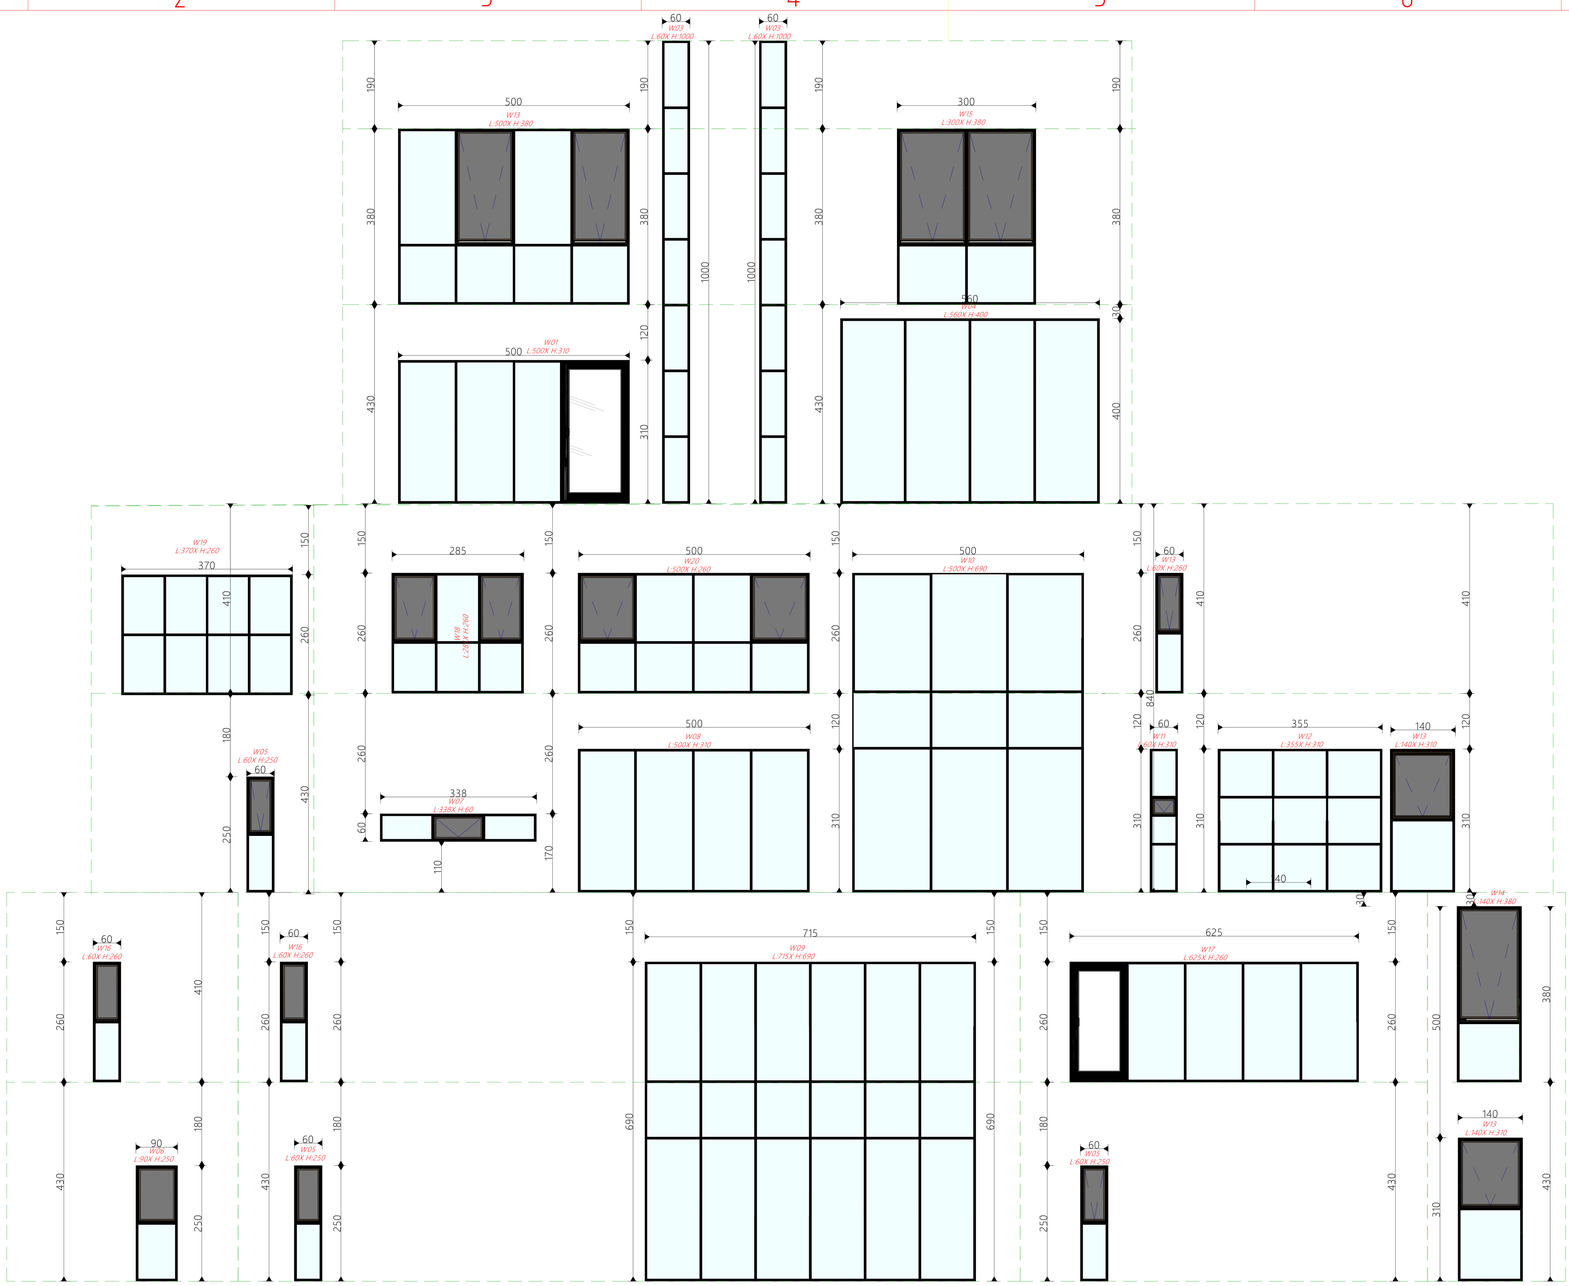

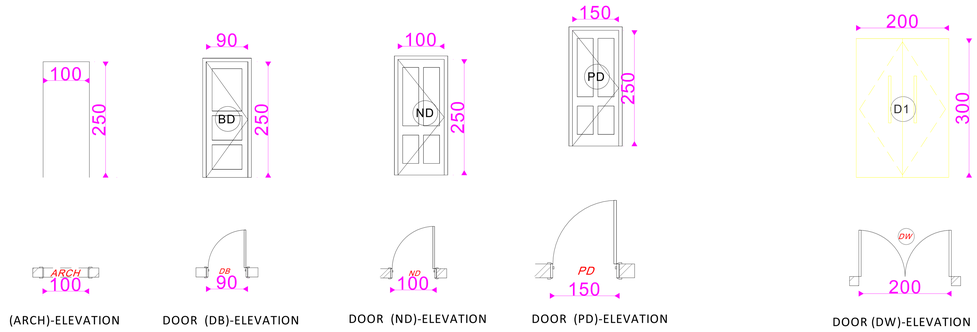

(ARCH)-ELEVATION

DOOR (DB)-ELEVATION

DOOR (ND)-ELEVATION

DOOR (PD)-ELEVATION

DOOR (DW)-ELEVATION

OPENNING DETAILS

Govemment Of Ras Al Khaimah
R.A.K. Municipality
Buildings Administration

حكومة رأس الخيمة
دائرة البلدية
إدارة المباني

Approved On — **اعتمد في**

14 January 2026

Building Permit #: PRMT-26-0000880

Appoved By:

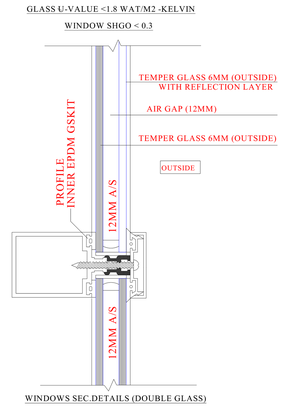

WINDOWS SEC.DETAILS (DOUBLE GLASS)

ALL GLASS MUST BE DOUBLE UNITES

GLASS SPECIFICATION:-

U-value (w/m2.k)<_ 1.8

SHADING CO- EFFICIENT (SC) <0.3

Savana
Engineering Consultancy & interior design

Client	MAYED MEERZA BASHEER MOHMMED + ROOF		
Project	DOUBLE STORY VILLA		
Drg.Title	Opening Details		
Area	AWAFI	Floortype	
Case ID.	3136005	Draw. Type.	ARCH
Sec No.	1	Com. No.	
Block No.		Plot No.	406132098
Bldg. No.	BLD-26-00570	Floor No.	
Date	2026	Sht. No.	A13
Scale	1/100	Job No.	

G.Manager	Architect	Designed By
ENG AYMEN	ENG IMEN	ENG OMAR

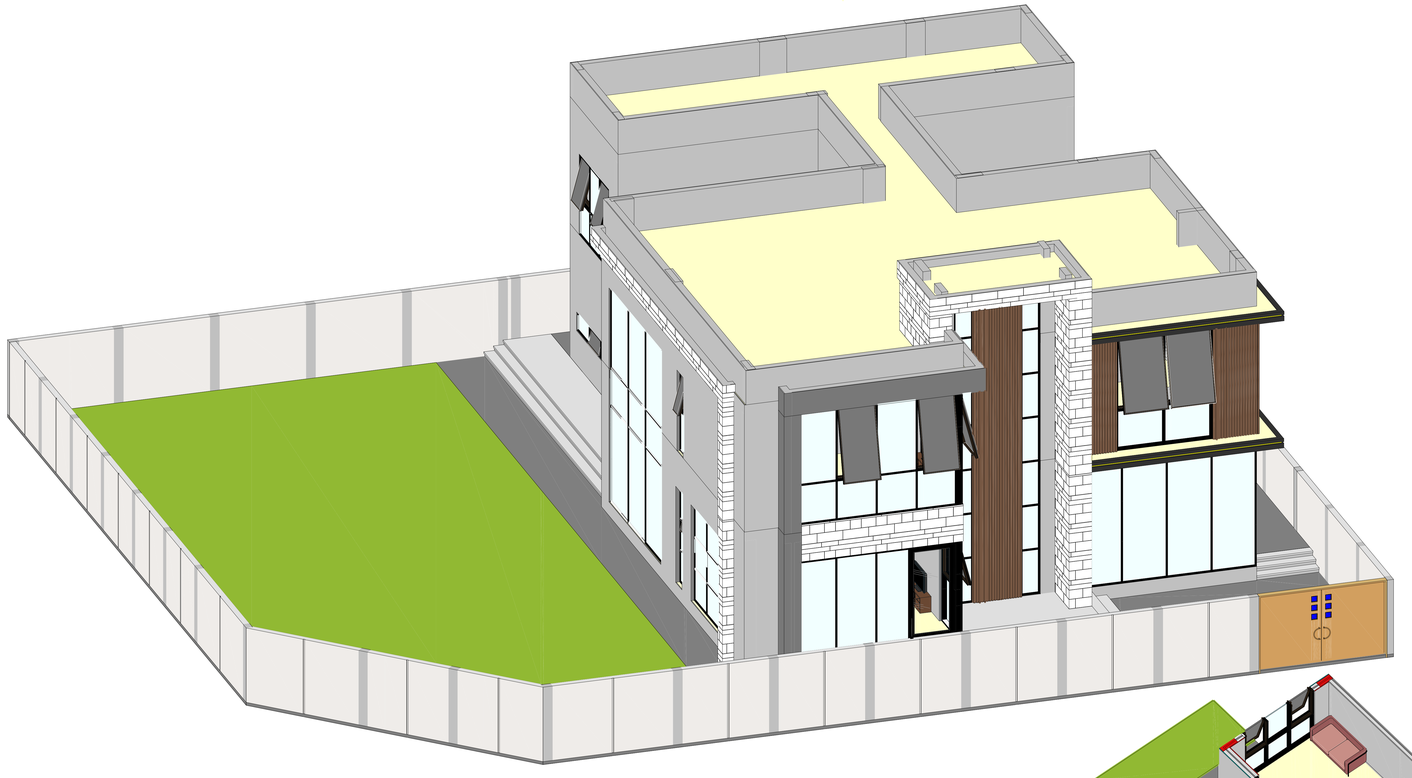

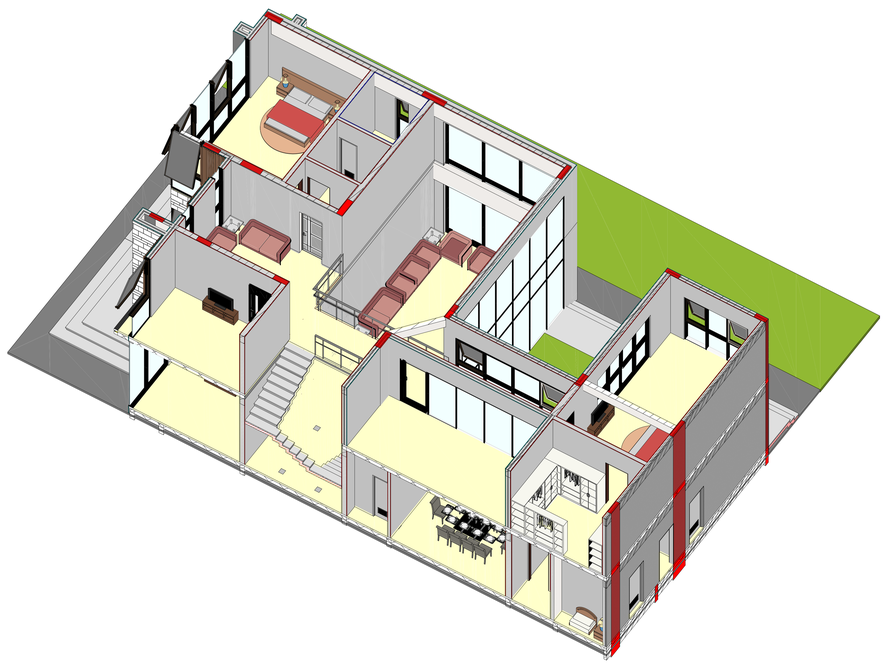

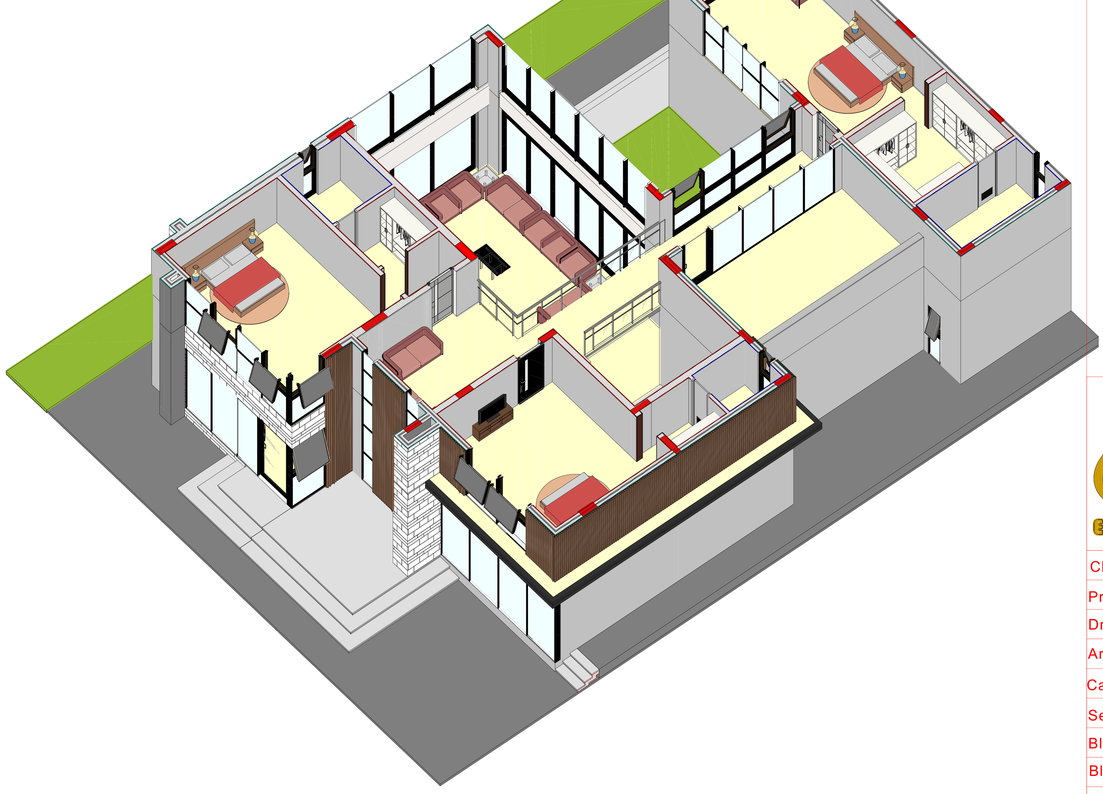

Govemment Of Ras Al Khaimah
R.A.K. Municipality
Buildings Administration

حكومة رأس الخيمة
دائرة البلدية
إدارة المباني

Approved On — اعتمد في

14 January 2026

Building Permit #: PRMT-26-0000880

Appoved By:

Savana
Engineering Consultancy & interior design

Client	MAYED MEERZA BASHEER MOHMMED + ROOF		
Project	DOUBLE STORY VILLA		
Drg.Title	PERSPECTIVE		
Area	AWAFI	Floortype	
Case ID.	3136005	Draw. Type.	ARCH
Sec No.	2	Com. No.	
Block No.		Plot No.	406132098
Bldg. No.	BLD-26-00570	Floor No.	
Date	2026	Sht. No.	A14
Scale	1/100	Job No.	

G.Manager	Architect	Designed By
ENG AYMEN	ENG IMEN	ENG OMAR

PERSPECTIVE

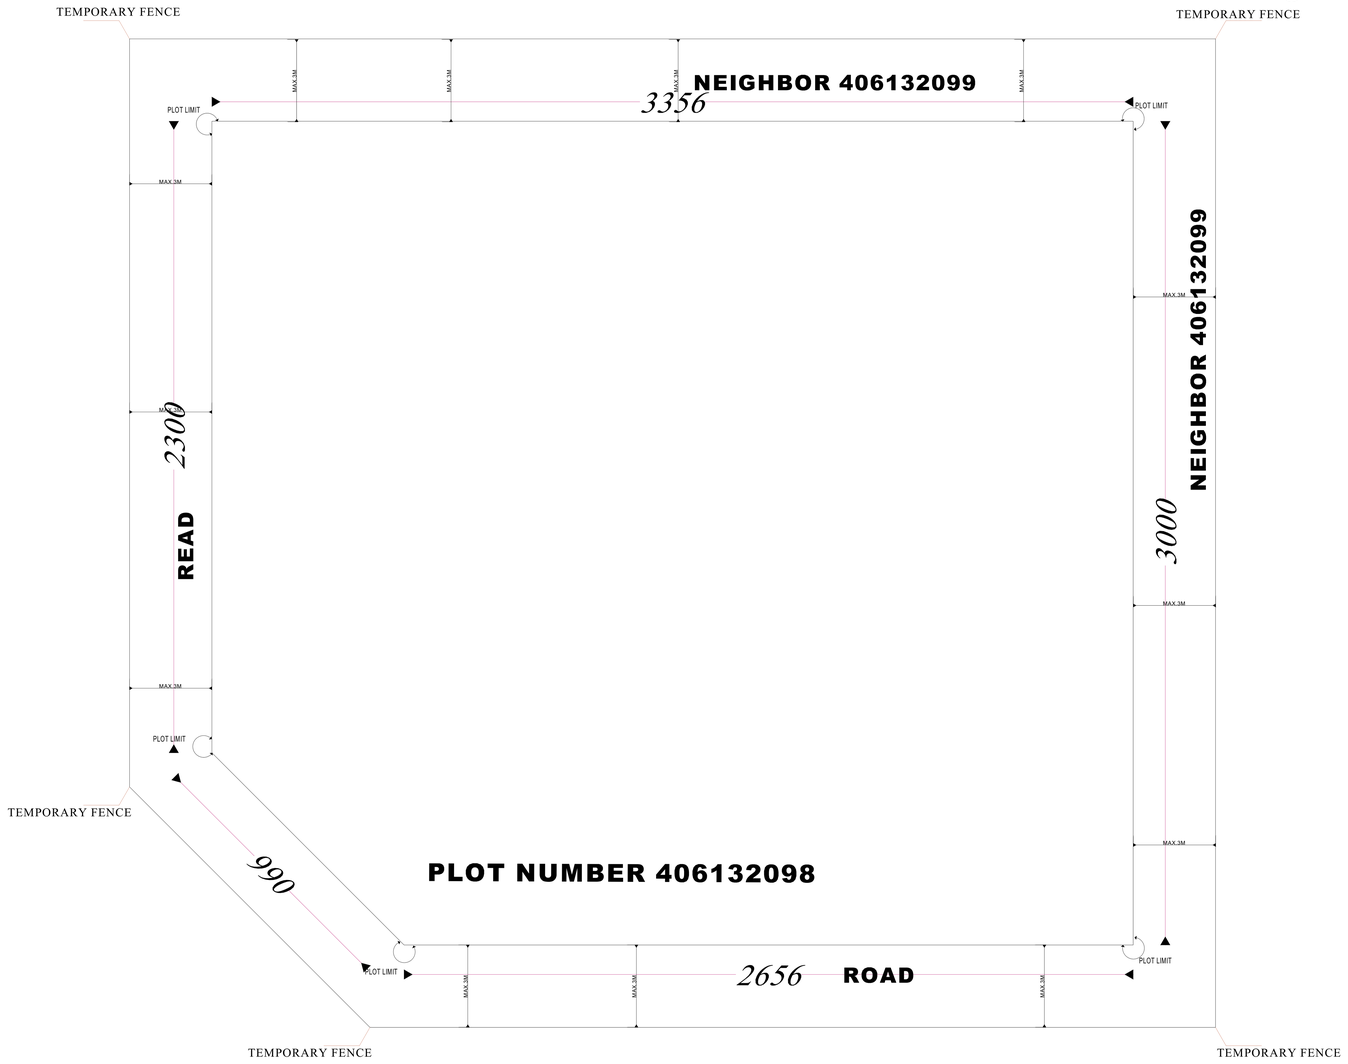

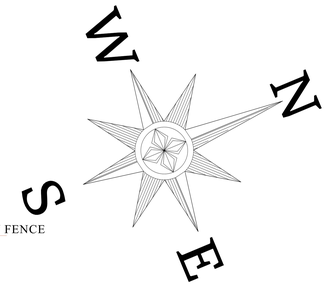

Govemment Of Ras Al Khaimah
R.A.K. Municipality
Buildings Administration

حكومة رأس الخيمة
دائرة البلدية
إدارة المباني

Approved On — اعتمد في

14 January 2026

Building Permit #: PRMT-26-0000880

Appoved By:

Savana
Engineering Consultancy & interior design

Client	MAYED MEERZA BASHEER MOHMMED + ROOF		
Project	DOUBLE STORY VILLA		
Drg.Title	GENERALE SITE TEMPORARY FENCE		
Area	AWAFI	Floortype	
Case ID.	3136005	Draw. Type.	ARCH
Sec No.	2	Com. No.	
Block No.		Plot No.	406132098
Bldg. No.	BLD-26-00570	Floor No.	
Date	2026	Sht. No.	A18
Scale	1/100	Job No.	

G.Manager	Architect	Designed By
ENG AYMEN	ENG IMEN	ENG OMAR

GENERALE SITE TEMPORARY FENCE

Type	SCHEDULE OF FINISHINGS
1	LIGHT IVORY

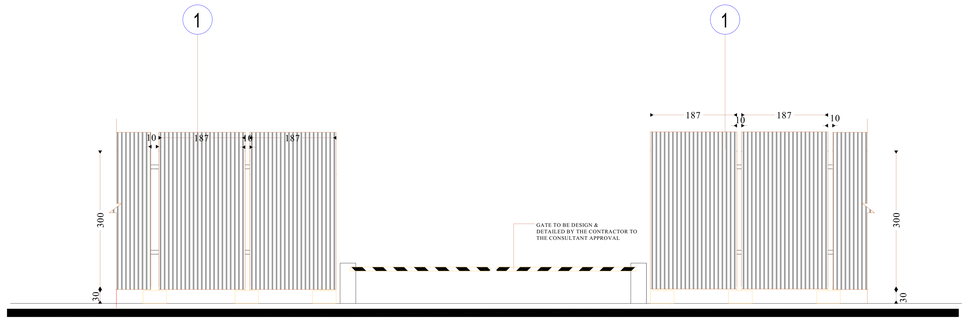

ALUMINIUM TEMPORARY FENCE

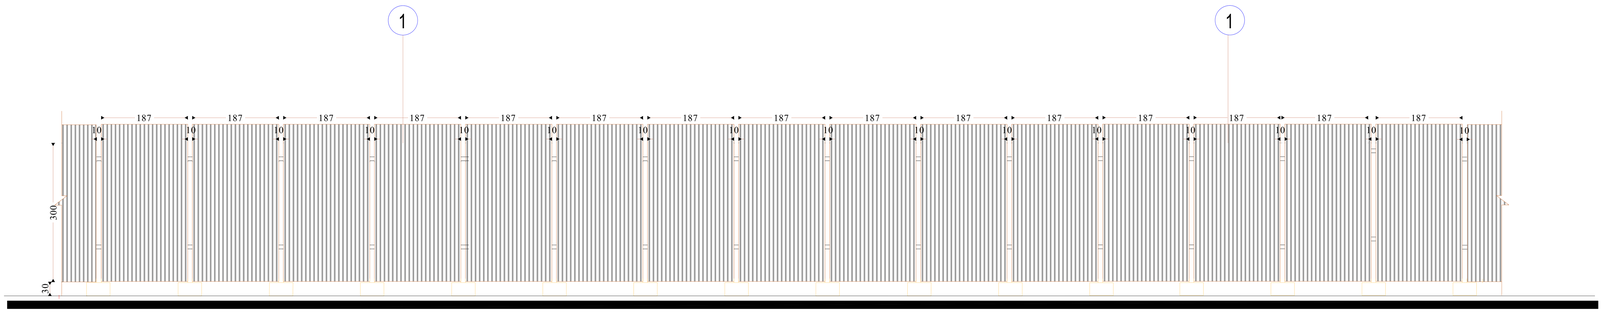

HOARDING ELEVATION

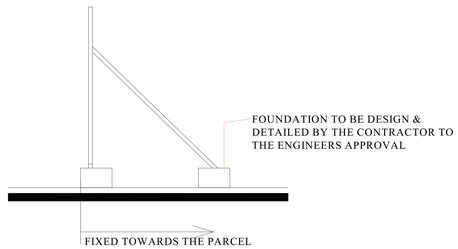

HOARDING SIDE ELEVATION

ALLUMINIUM FENCE

Govemment Of Ras Al Khaimah
R.A.K. Municipality
Buildings Administration

حكومة رأس الخيمة
دائرة البلدية
إدارة المباني

Approved On — اعتمد في

14 January 2026

Building Permit #: PRMT-26-0000880

Appoved By:

Savana
Engineering Consultancy & interior design

Client	MAYED MEERZA BASHEER MOHMMED + ROOF		
Project	DOUBLE STORY VILLA		
Drg.Title	ALLUMINIUM FENCE		
Area	AWAFI	Floortype	
Case ID.	3136005	Draw. Type.	ARCH
Sec No.	2	Com. No.	
Block No.		Plot No.	406132098
Bldg. No.	BLD-26-00570	Floor No.	
Date	2026	Sht. No.	A19
Scale	1/100	Job No.	

G.Manager	Architect	Designed By
ENG AYMEN	ENG IMEN	ENG OMAR

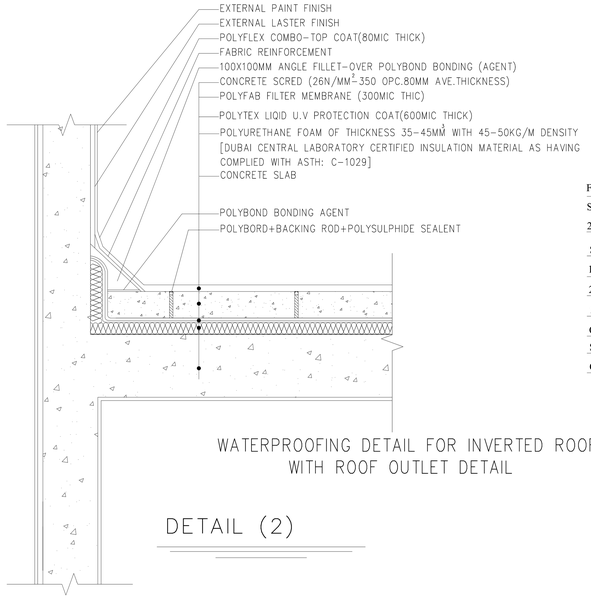

WATERPROOFING DETAIL FOR INVERTED ROOF
WITH ROOF OUTLET DETAIL

DETAIL (2)

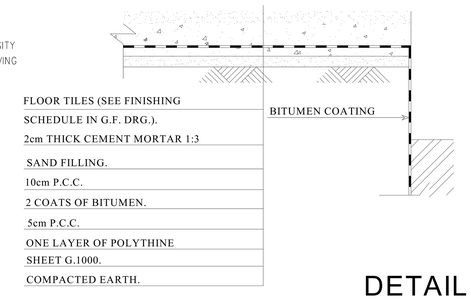

DETAIL (4)

ENTRANCE STEPS DETAIL

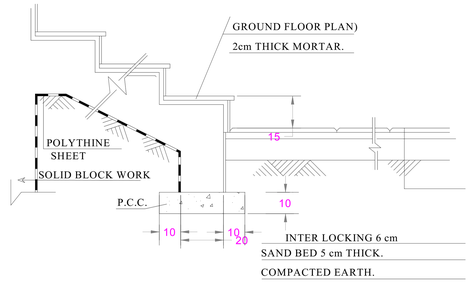

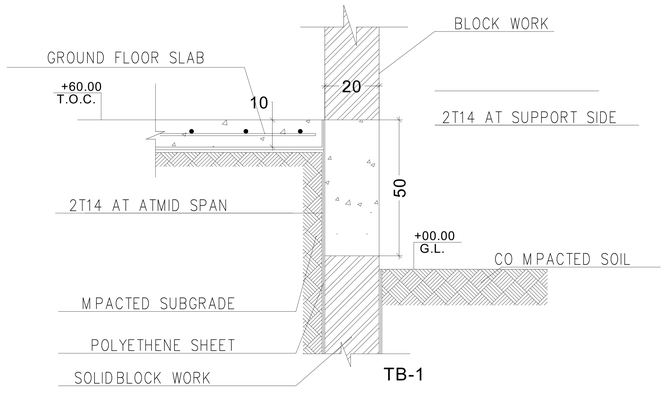

DETAIL (3)

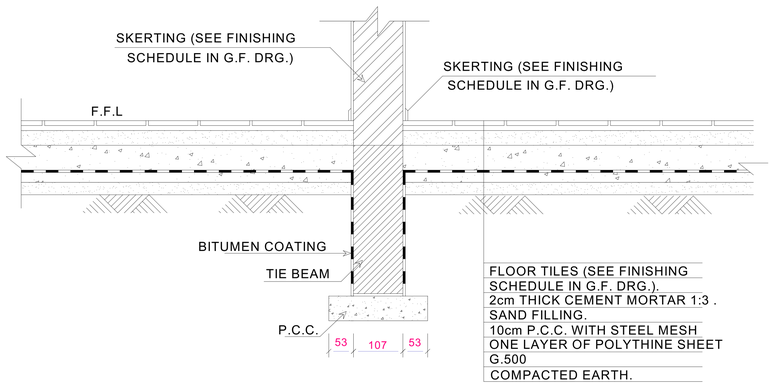

DETAIL (1)

GENERALE DETAILS

Govemment Of Ras Al Khaimah
R.A.K. Municipality
Buildings Administration

حكومة رأس الخيمة
دائرة البلدية
إدارة المباني

Approved On — اعتمد في

14 January 2026

Building Permit #: PRMT-26-0000880

Appoved By:

Savana
Engineering Consultancy & interior design

Client	MAYED MEERZA BASHEER MOHMMED + ROOF		
Project	DOUBLE STORY VILLA		
Drg.Title	GENERALE DETAILS		
Area	AWAFI	Floortype	
Case ID.	3136005	Draw. Type.	ARCH
Sec No.	2	Com. No.	
Block No.		Plot No.	406132098
Bldg. No.	BLD-26-00570	Floor No.	
Date	2026	Sht. No.	A20
Scale	1/100	Job No.	

G.Manager	Architect	Designed By
ENG AYMEN	ENG IMEN	ENG OMAR

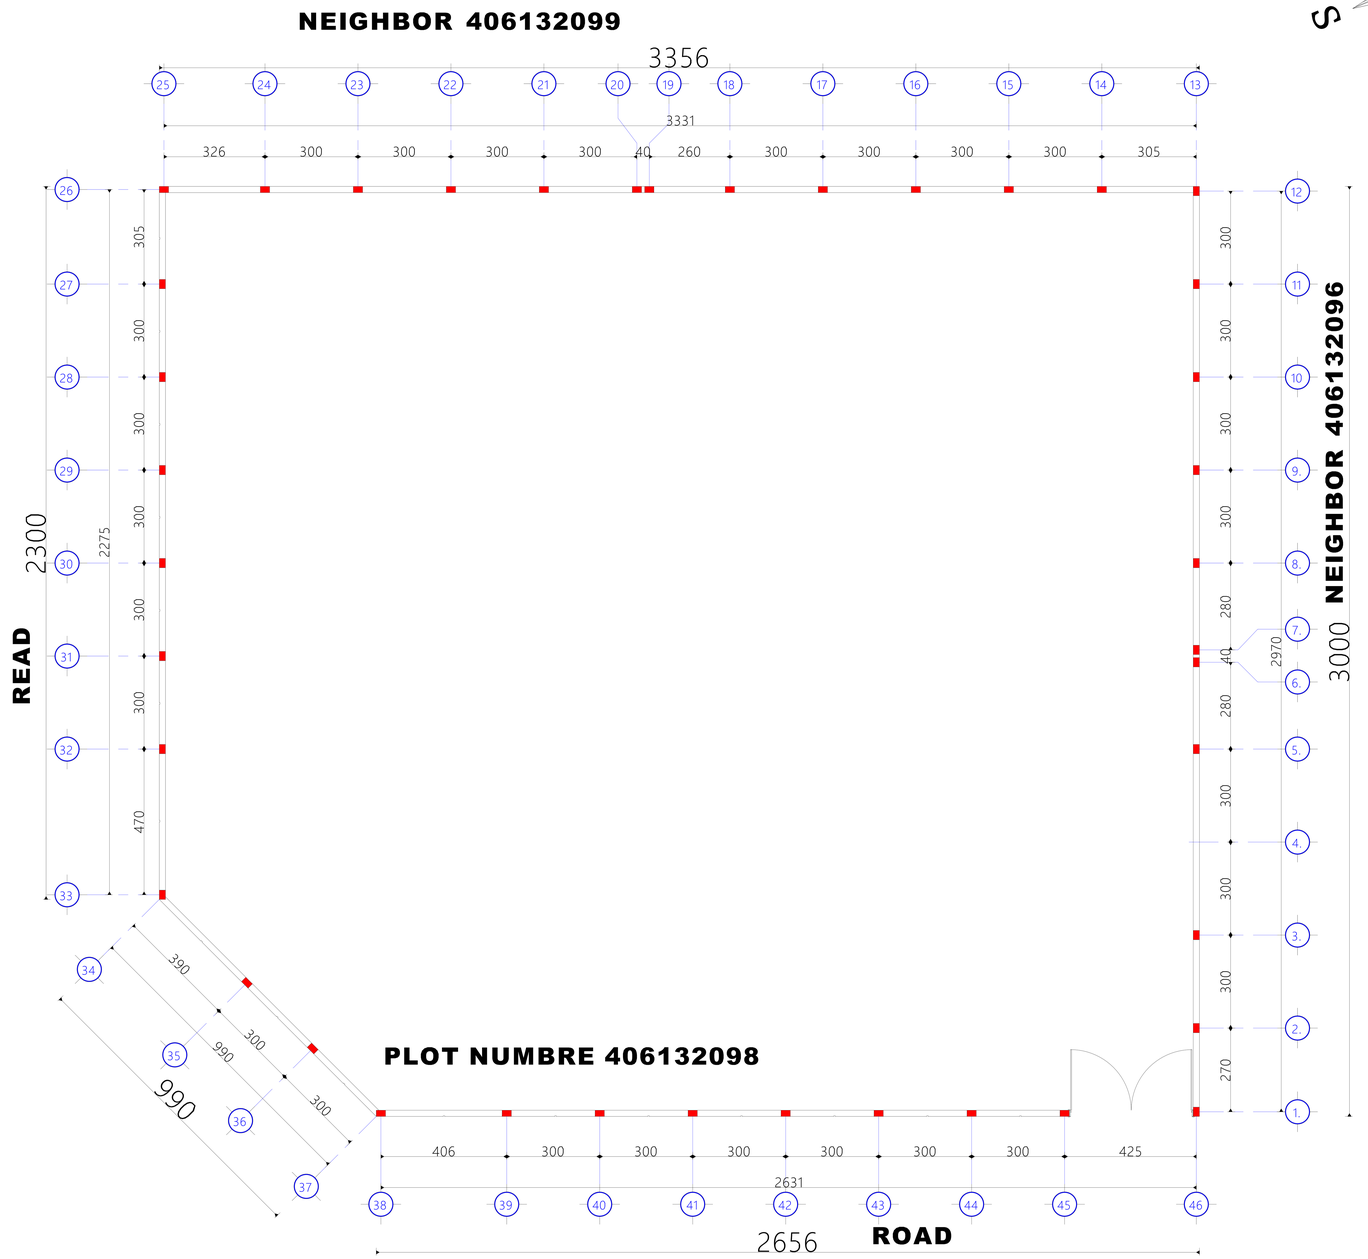

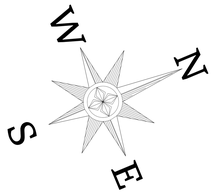

Govemment Of Ras Al Khaimah
R.A.K. Municipality
Buildings Administration

حكومة رأس الخيمة
دائرة البلدية
إدارة المباني

Approved On — اعتمد في

14 January 2026

Building Permit #: PRMT-26-0000880

Appoved By:

Savana
Engineering Consultancy & interior design

Client	MAYED MEERZA BASHEER MOHMMED + ROOF		
Project	DOUBLE STORY VILLA		
Drg.Title	BOUNDARY WALL LAYOUT PLAN		
Area	AWAFI	Floortype	
Case ID.	3136005	Draw. Type.	ARCH
Sec No.	2	Com. No.	
Block No.		Plot No.	406132098
Bldg. No.	FNC-26-000125	Floor No.	
Date	2025	Sht. No.	A15
Scale	1/100	Job No.	

G.Manager	Architect	Designed By
ENG AYMEN	ENG IMEN	ENG OMAR

B.WALL SITE PLAN

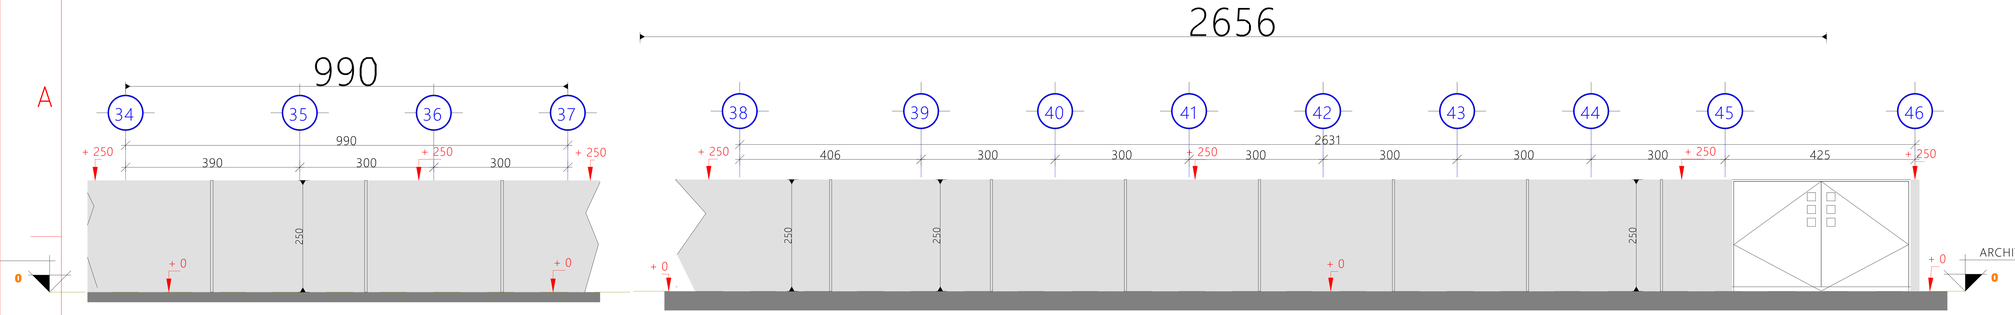

FRONT ELEVATION

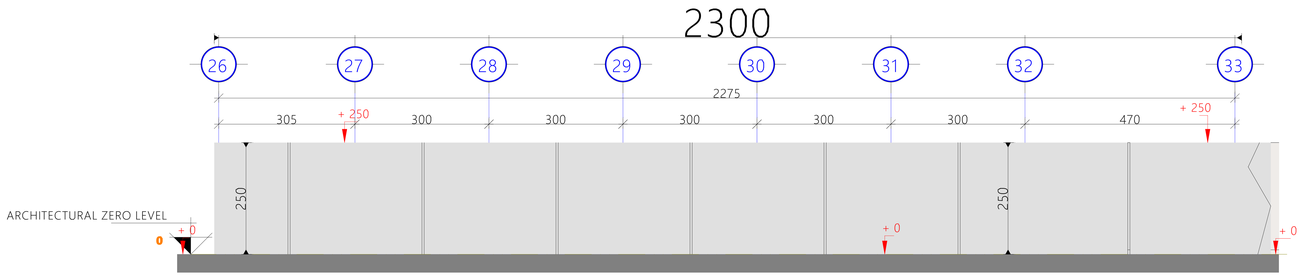

LEFT ELEVATION

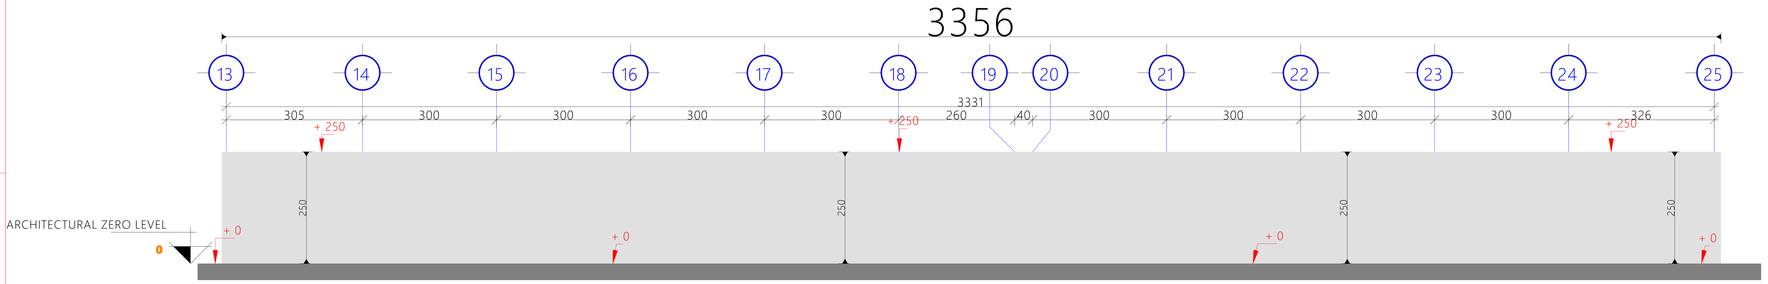

RIGHT ELEVATION

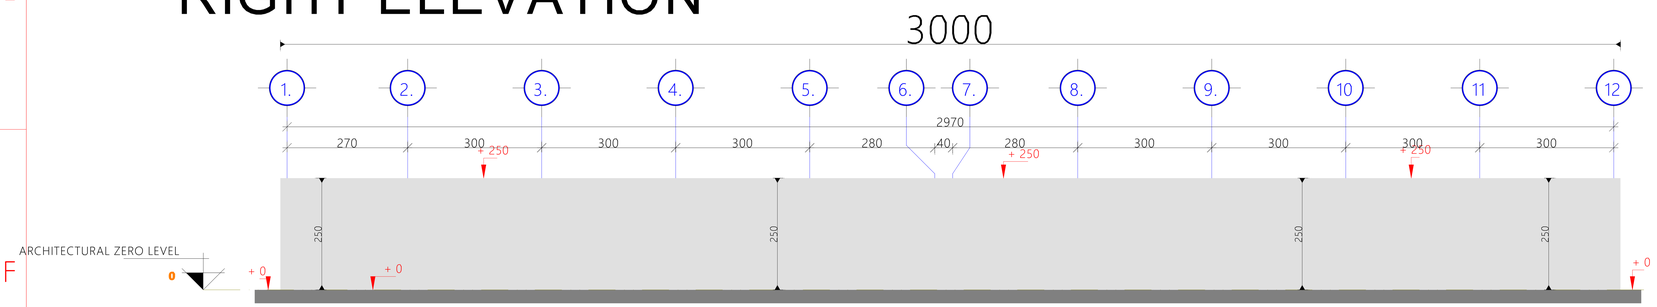

REAR ELEVATION

Govemment Of Ras Al Khaimah
R.A.K. Municipality
Buildings Administration

حكومة رأس الخيمة
دائرة البلدية
إدارة المباني

Approved On — اعتمد في

14 January 2026

Building Permit #: PRMT-26-0000880

Appoved By:

Savana
Engineering Consultancy & interior design

Client	MAYED MEERZA BASHEER MOHMMED + ROOF		
Project	DOUBLE STORY VILLA		
Drg.Title	Proposed Boundary Wall Elevations		
Area	AWAFI	Floortype	
Case ID.	3136005	Draw. Type.	ARCH
Sec No.	2	Com. No.	
Block No.		Plot No.	406132098
Bldg. No.	FNC-26-000125	Floor No.	
Date	2025	Sht. No.	A16
Scale	1/100	Job No.	

G.Manager	Architect	Designed By
ENG AYMEN	ENG IMEN	ENG OMAR

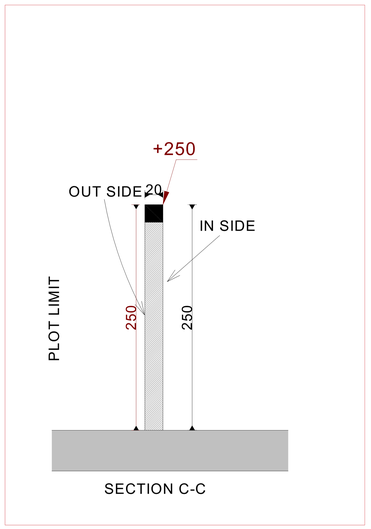

SECTION C-C

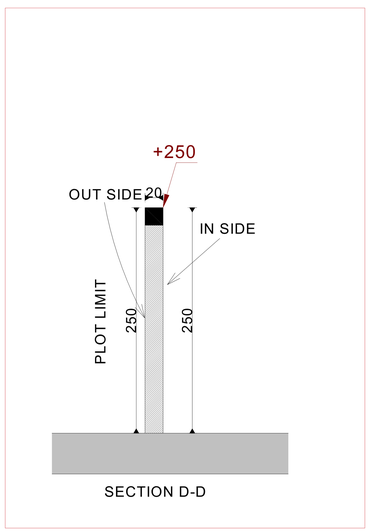

SECTION D-D

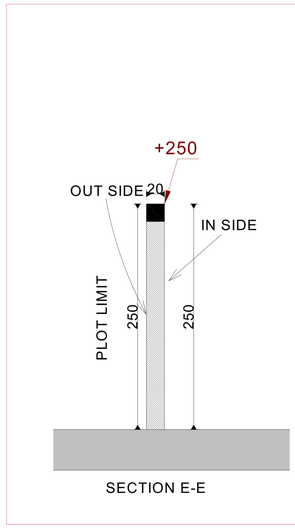

SECTION E-E

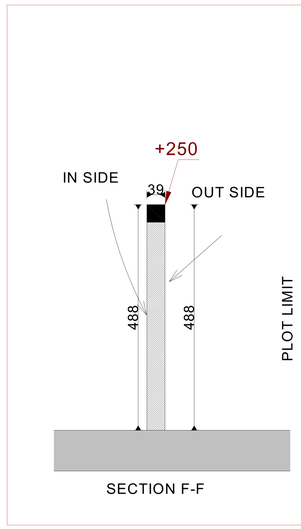

SECTION F-F

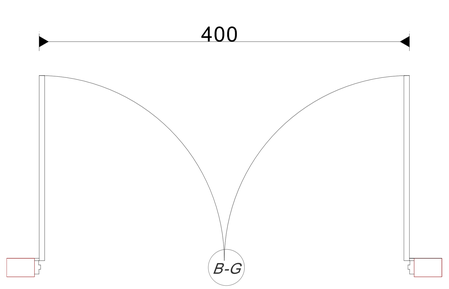

DOOR (BG)-ELEVATION

SCALE 1:50

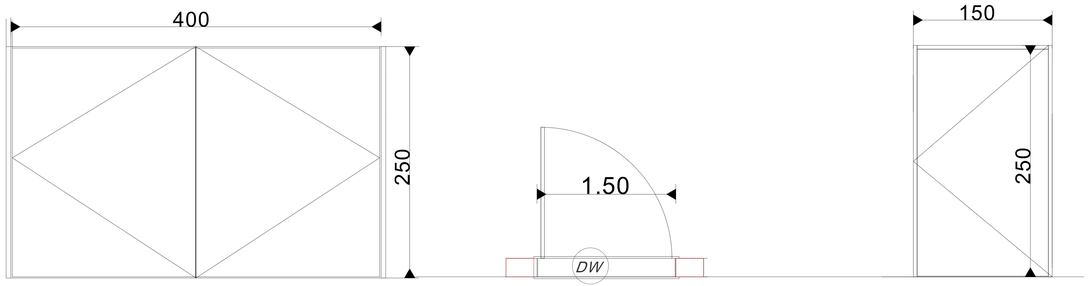

DOOR (DB)-ELEVATION

SCALE 1:50

B.WALL SECTION

Govemment Of Ras Al Khaimah
R.A.K. Municipality
Buildings Administration

حكومة رأس الخيمة
دائرة البلدية
إدارة المباني

Approved On — اعتمد في

14 January 2026

Building Permit #: PRMT-26-0000880

Appoved By:

Savana
Engineering Consultancy & interior design

Client	MAYED MEERZA BASHEER MOHMMED + ROOF		
Project	DOUBLE STORY VILLA		
Drg.Title	Boundary Wall DETAILS		
Area	AWAFI	Floortype	
Case ID.	3136005	Draw. Type.	ARCH
Sec No.	2	Com. No.	
Block No.		Plot No.	406132098
Bldg. No.	FNC-26-000125	Floor No.	
Date	2025	Sht. No.	A17
Scale	1/100	Job No.	

G.Manager	Architect	Designed By
ENG AYMEN	ENG IMEN	ENG OMAR