	BATH TUB
	SHOWER TRAY
	WASH BASIN
	SINK
	EUROPEAN W C
	ARABIC W C
	BEDET
FT	FLOOR TRAP
GT	GULLY TRAP
MH	MANHOLE
ST	SEPTIC TANK
	BATH TUB - CORNER TYPE

DRAINAGE PIPE SIZE SCHEDULE:

SR.NO	LOCATION	PIPES SIZE (Ø-inch)
01	MAINHOLE TO MANHOLE	6
02	WC TO MAINHOLE	4
03	GULLY TRAP TO MAINHOLE	4
04	FLOOR TRAP TO GULLY TRAP	3
05	MAINHOLE VENT	3
06	LAST MAINHOLE&SEPTIC TANK VENT	3
07	WASH BASIN TO FLOOR TRAP	2
08	KITCHEN SINK TO FLOOR TRAP	2
09	OTHERS REFER TO DRAWINGS	

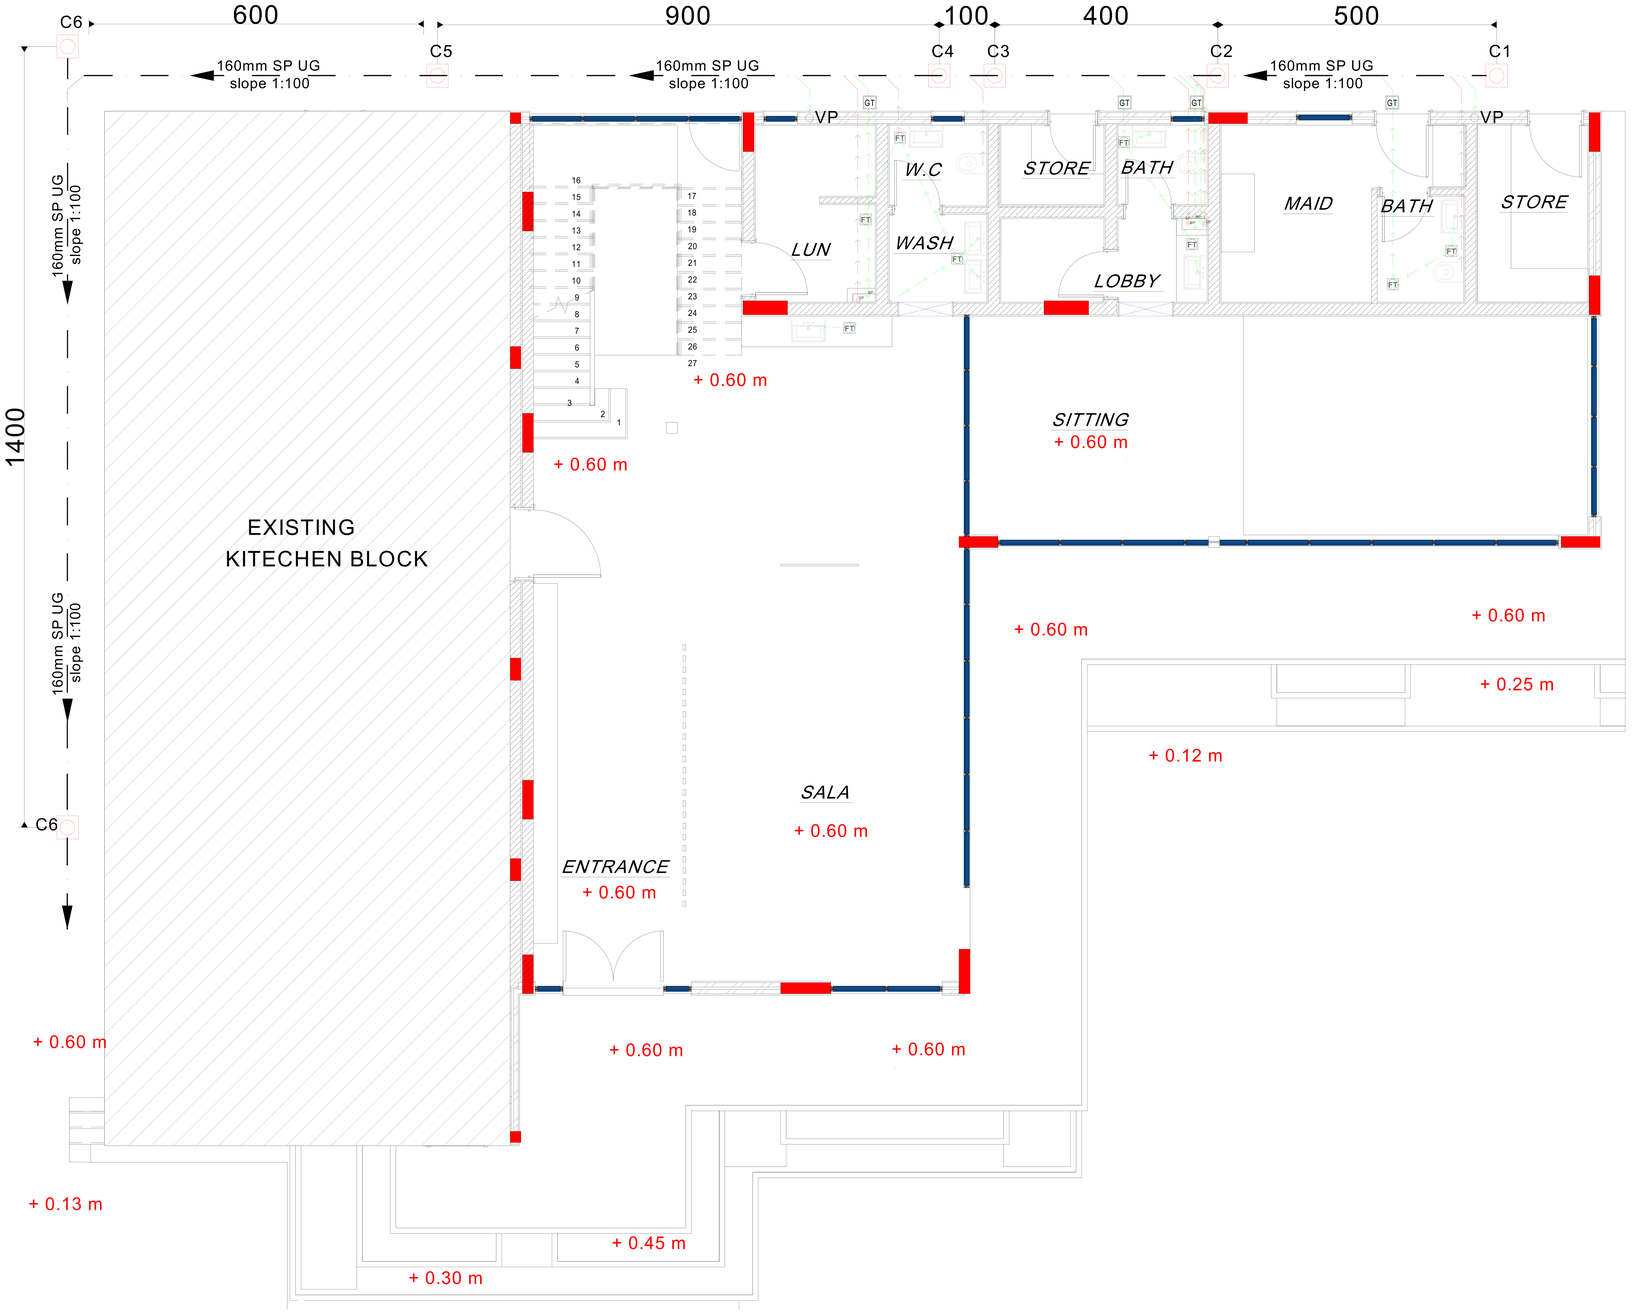

Government of Ras Al Khaimah
WASTEWATER AGENCY
حكومة رأس الخيمة
مؤسسة الصرف الصحي

26 June 2024

APPROVED

PRMT-24-0003939

Signed .....

Savana
Engineering Consultancy & interior design

Client	SAID AHMED MOHAMMED ALMANSOURI		
Project	DOUBLE STOREY VILLA		
Drg.Title	GROUND Floor Drainage Layout Plan		
Area	ALRIFAA	Floortype	G
Case ID.	2542576	Draw. Type.	DRNG
Sec No.	2	Com. No.	
Block No.		Plot No.	607011962
Bldg. No.	BLD-24-03157	Floor No.	01
Date	JUN2024	Sht. No.	D02
Scale	1:100	Job No.	

G.Manager	Architect	Drawn by
ENG.AYMEN	ENG.IMEN	M.IMEN

4
D-03

GROUND Floor Drainage Layout Plan

SCALE 1:100

	BATH TUB
	SHOWER TRAY
	WASH BASIN
	SINK
	EUROPEAN W C
	ARABIC W C
	BEDET
FT	FLOOR TRAP
GT	GULLY TRAP
MH	MANHOLE
ST	SEPTIC TANK
	BATH TUB - CORNER TYPE

DRAINAGE PIPE SIZE SCHEDULE:

SR.NO	LOCATION	PIPES SIZE (Ø-inch)
01	MAINHOLE TO MANHOLE	6
02	WC TO MAINHOLE	4
03	GULLY TRAP TO MAINHOLE	4
04	FLOOR TRAP TO GULLY TRAP	3
05	MAINHOLE VENT	3
06	LAST MAINHOLE&SEPTIC TANK VENT	3
07	WASH BASIN TO FLOOR TRAP	2
08	KITCHEN SINK TO FLOOR TRAP	2
09	OTHERS REFER TO DRAWINGS	

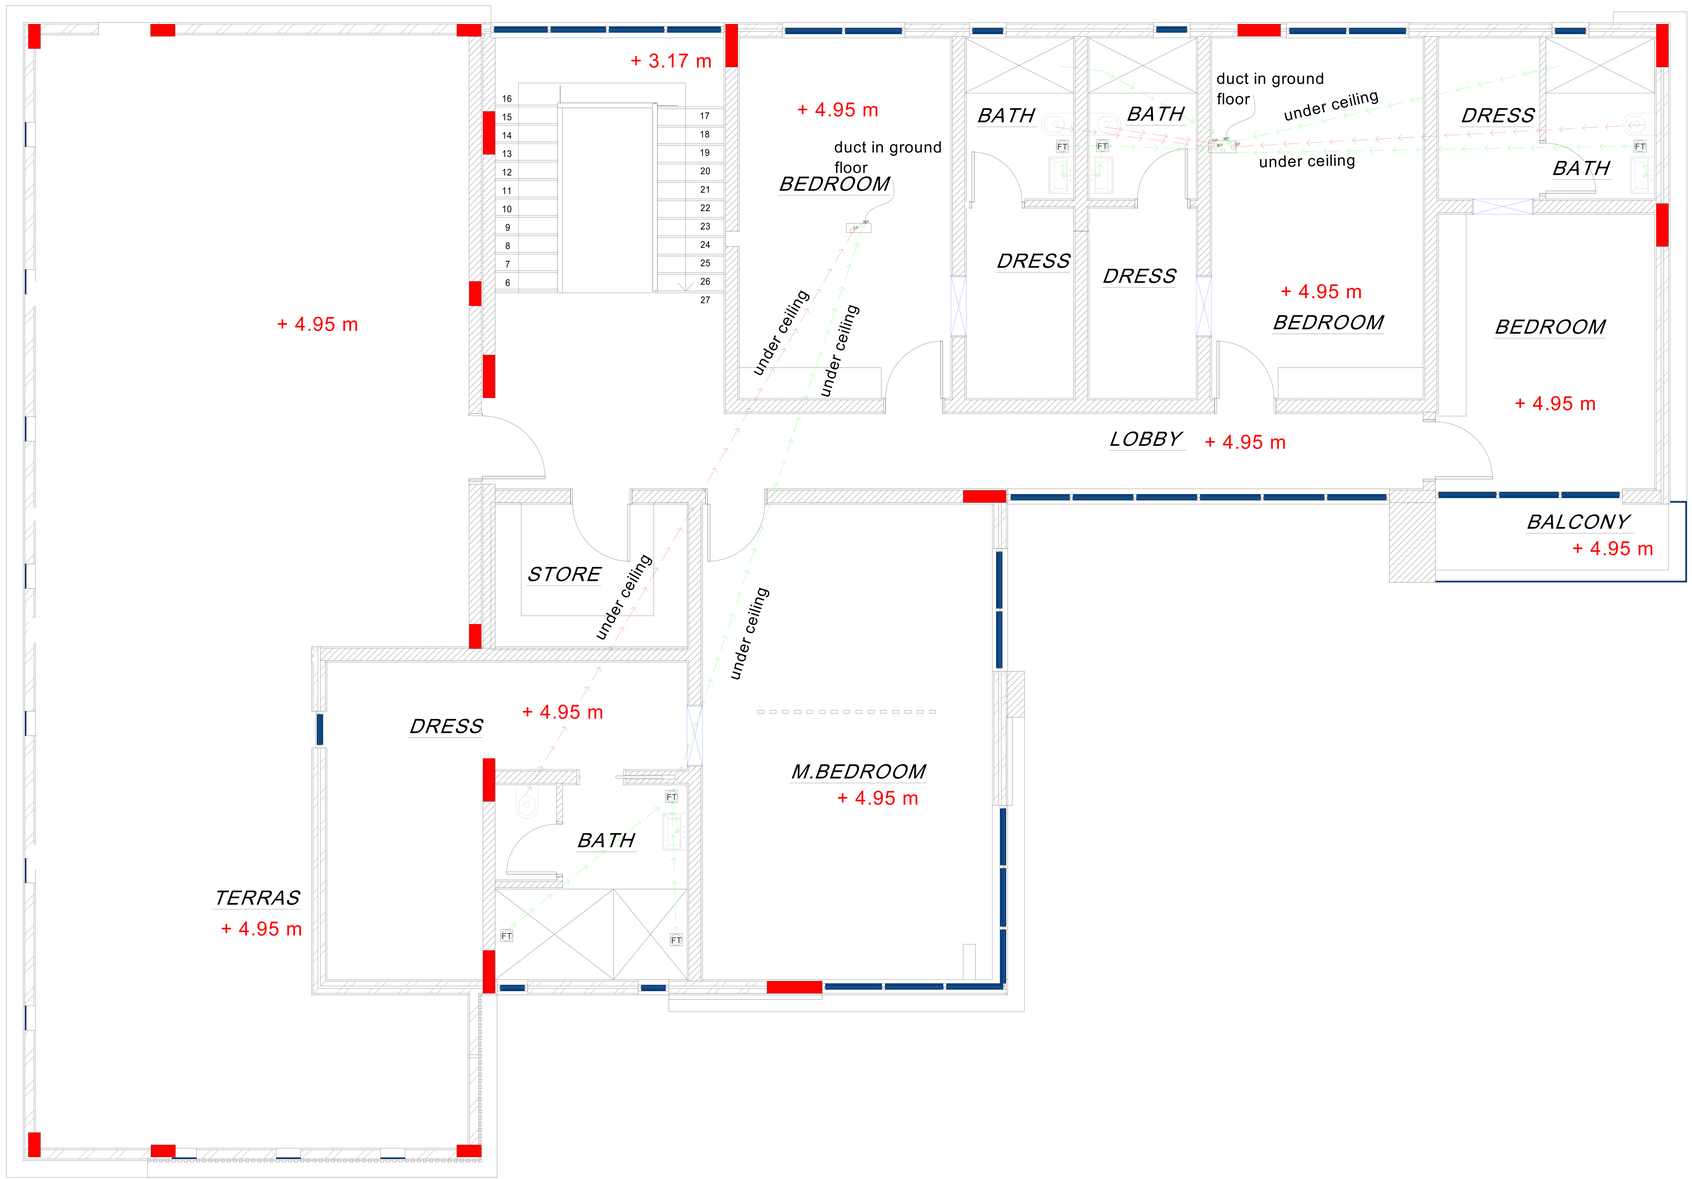

Government of Ras Al Khaimah
WASTEWATER AGENCY
حكومة رأس الخيمة
مؤسسة الصرف الصحي

26 June 2024

APPROVED

PRMT-24-0003939

Signed .....

Savana
Engineering Consultancy & interior design

Client	SAID AHMED MOHAMMED ALMANSOURI		
Project	DOUBLE STOREY VILLA		
Drg.Title	FIRST Floor Drainage Layout Plan		
Area	ALRIFAA	Floortype	F
Case ID.	2542576	Draw. Type.	DRNG
Sec No.	2	Com. No.	
Block No.		Plot No.	607011962
Bldg. No.	BLD-24-03157	Floor No.	01
Date	JUN2024	Sht. No.	D03
Scale	1:100	Job No.	

G.Manager	Architect	Drawn by
ENG.AYMEN	ENG.IMEN	M.IMEN

4
D-04

FIRST Floor Drainage Layout Plan

SCALE 1:100

	BATH TUB
	SHOWER TRAY
	WASH BASIN
	SINK
	EUROPEAN W C
	ARABIC W C
	BEDET
FT	FLOOR TRAP
GT	GULLY TRAP
MH	MANHOLE
ST	SEPTIC TANK
	BATH TUB - CORNER TYPE

DRAINAGE PIPE SIZE SCHEDULE:

SR.NO	LOCATION	PIPES SIZE (Ø-inch)
01	MAINHOLE TO MANHOLE	6
02	WC TO MAINHOLE	4
03	GULLY TRAP TO MAINHOLE	4
04	FLOOR TRAP TO GULLY TRAP	3
05	MAINHOLE VENT	3
06	LAST MAINHOLE&SEPTIC TANK VENT	3
07	WASH BASIN TO FLOOR TRAP	2
08	KITCHEN SINK TO FLOOR TRAP	2
09	OTHERS REFER TO DRAWINGS	

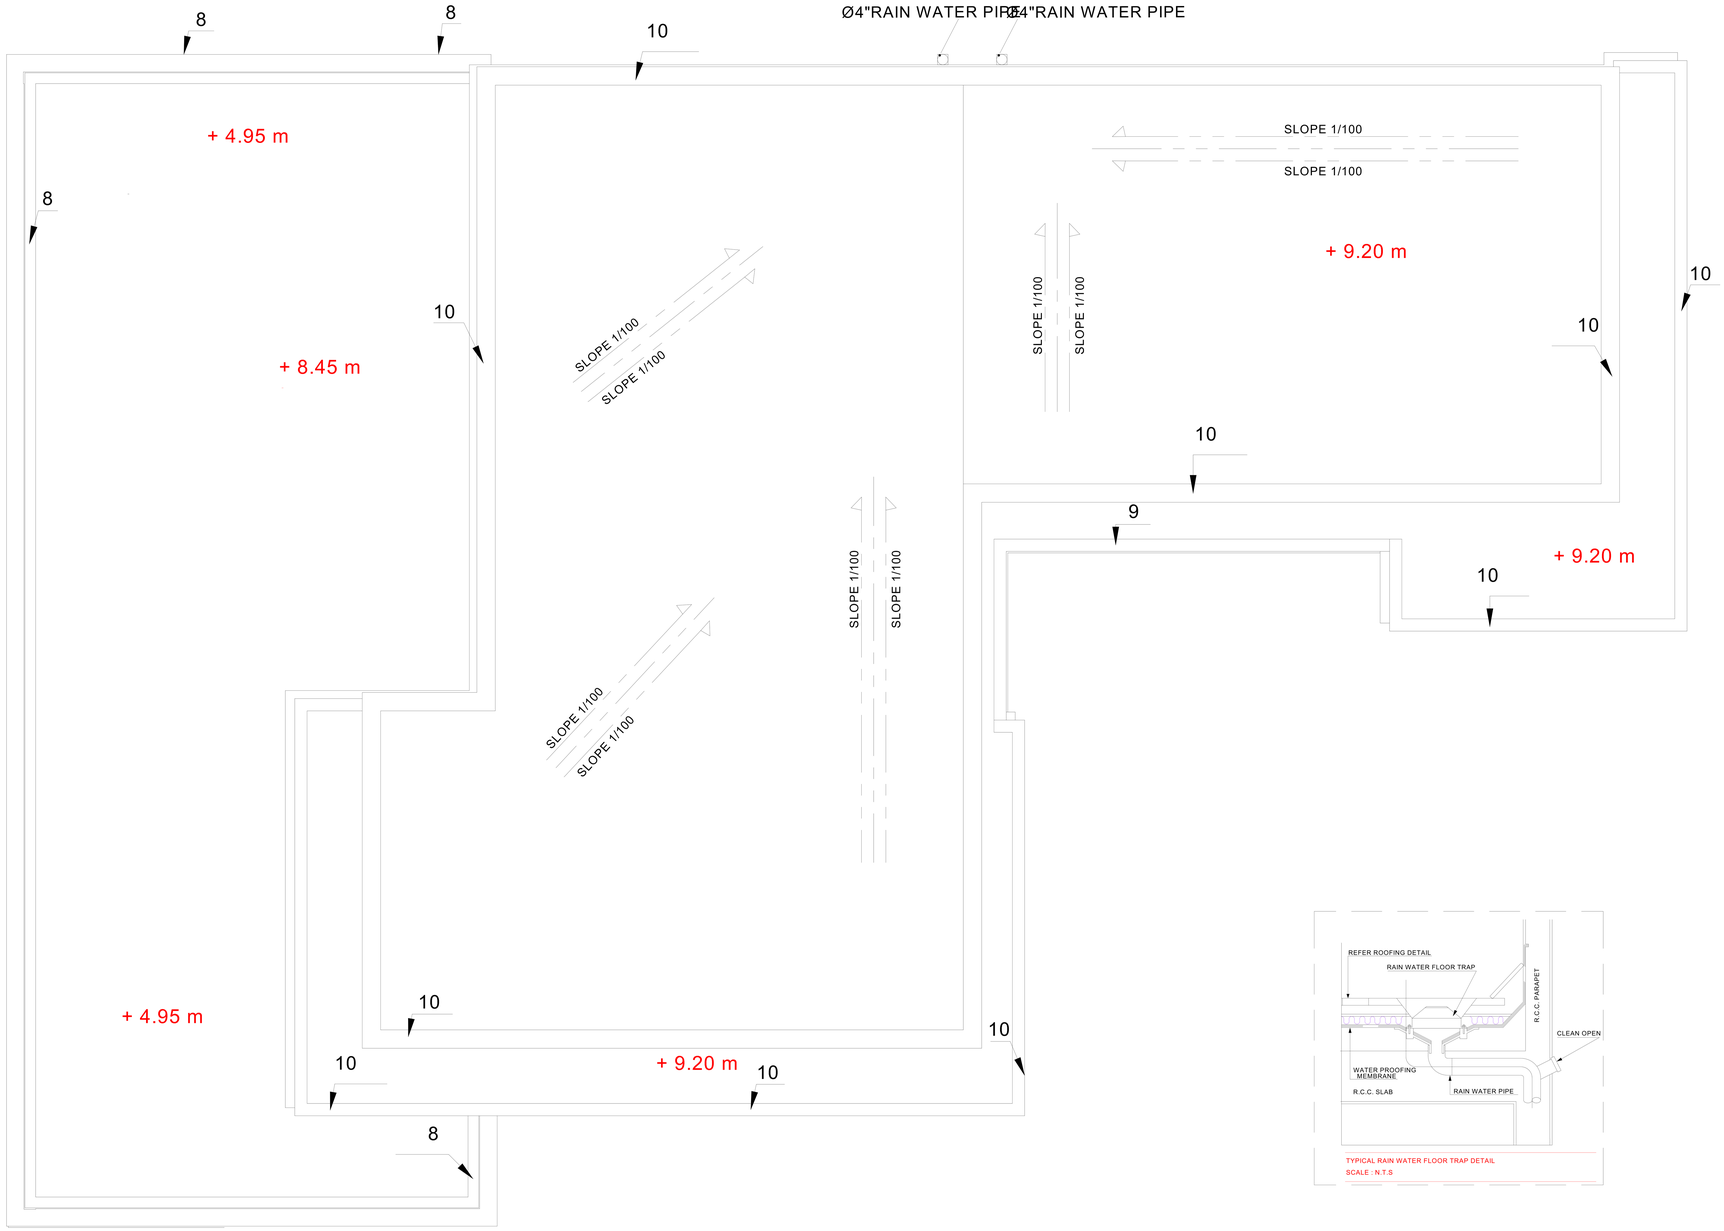

TYPICAL RAIN WATER FLOOR TRAP DETAIL
SCALE : N.T.S

Government of Ras Al Khaimah
WASTEWATER AGENCY
حكومة رأس الخيمة
مؤسسة الصرف الصحي
26 June 2024
APPROVED
PRMT-24-0003939
Signed

Savana
Engineering Consultancy & interior design

Client	SAID AHMED MOHAMMED ALMANSOURI		
Project	DOUBLE STOREY VILLA		
Drg.Title	ROOF Floor Drainage Layout Plan		
Area	ALRIFAA	Floortype	
Case ID.	2542576	Draw. Type.	DRNG
Sec No.	2	Com. No.	
Block No.		Plot No.	607011962
Bldg. No.	BLD-24-03157	Floor No.	
Date	JUN2024	Sht. No.	D04
Scale	1:100	Job No.	

G.Manager	Architect	Drawn by
ENG.AYMEN	ENG.IMEN	M.IMEN

4
D-05

ROOF Floor Drainage Layout Plan

SCALE 1:100

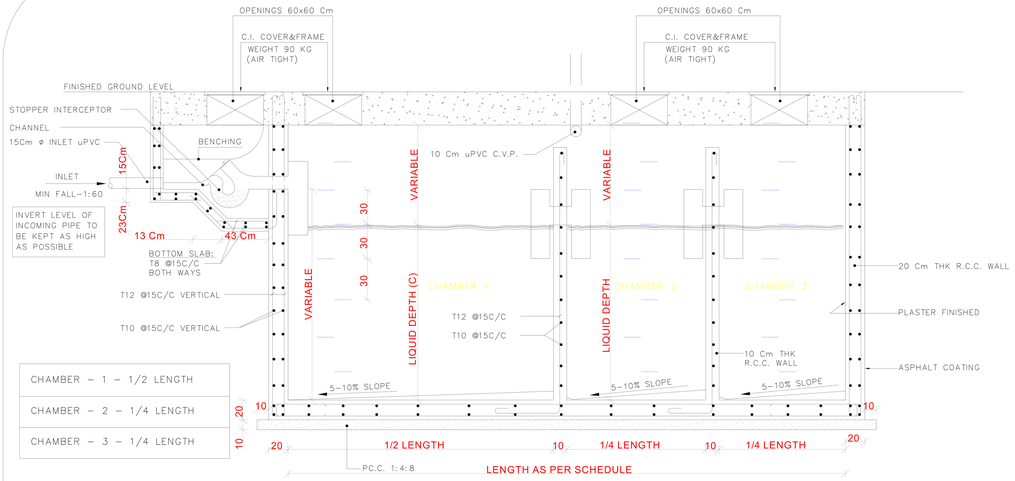

SECTION A-A

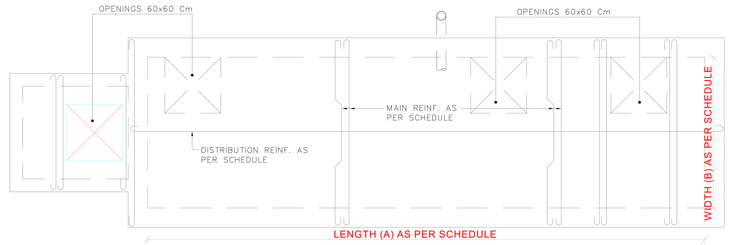

REINFORCEMENT DETAIL OF TOP SLAB

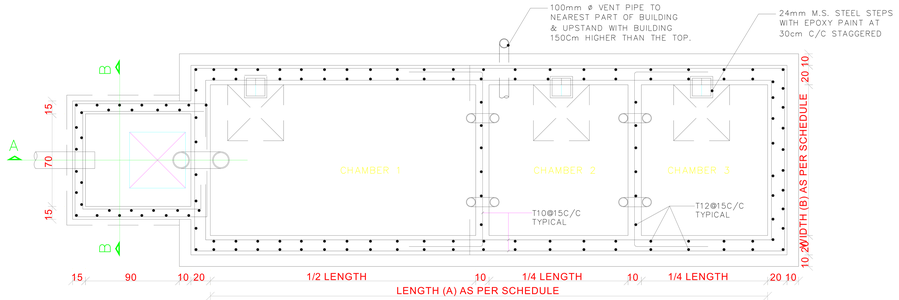

SEPTIC TANK PLAN

SCHEDULE OF STANDARD R.C.C SEPTIC TANK

TYPE	No. OF USERS	CAPACITY OF THE TANK BY FORMULA (cu.m.)	CAPACITY OF THE TANK BY DIMENSION (cu.m.)	SEPTIC TANK SIZE (A) LENGTH	(B) WIDTH	(C) LIQ. DEPTH	SEPTIC TANK TOP SLAB REINF. THICKNESS	MAIN.REINF.	DIST. BARS
1.	1 TO 10	3.80 cum	3.83 cum	2.90 m	1.10 m	1.20 m	12 cm	T10/15cm	T10/20cm
2.	11 TO 20	5.60 cum	5.62 cum	3.60 m	1.20 m	1.30 m	12 cm	T10/15cm	T10/20cm
3.	21 TO 30	7.40 cum	7.46 cum	4.10 m	1.30 m	1.40 m	15 cm	T12/15cm	T10/20cm
4.	31 TO 40	9.20 cum	9.21 cum	4.70 m	1.40 m	1.40 m	15 cm	T12/15cm	T10/20cm
5.	41 TO 50	11.00 cum	11.25 cum	5.00 m	1.50 m	1.50 m	15 cm	T12/15cm	T10/20cm
6.	51 TO 60	12.80 cum	12.84 cum	5.35 m	1.60 m	1.50 m	15 cm	T12/15cm	T10/20cm
7.	61 TO 70	14.60 cum	14.65 cum	5.55 m	1.65 m	1.60 m	15 cm	T12/15cm	T10/20cm
8.	71 TO 80	16.40 cum	16.47 cum	5.70 m	1.70 m	1.70 m	15 cm	T12/15cm	T10/20cm
9.	81 TO 90	18.20 cum	18.05 cum	5.90 m	1.80 m	1.70 m	15 cm	T12/15cm	T10/20cm
10.	91 TO 100	20.00 cum	20.02 cum	6.20 m	1.90 m	1.70 m	15 cm	T12/15cm	T10/20cm
11.	101 TO 120	23.60 cum	23.76 cum	6.60 m	2.00 m	1.80 m	20 cm	T14/15cm	T10/20cm
12.	121 TO 150	29.00 cum	28.91 cum	7.30 m	2.20 m	1.80 m	20 cm	T14/15cm	T10/20cm
13.	151 TO 175	33.50 cum	33.21 cum	7.60 m	2.30 m	1.90 m	20 cm	T14/15cm	T10/20cm
14.	176 TO 200	38.00 cum	38.00 cum	7.60 m	2.50 m	2.00 m	20 cm	T14/15cm	T10/20cm
15.	275 TO 300	56.00 cum	56.00 cum	10.0 m	2.80 m	2.00 m	20 cm	T14/15cm	T10/20cm

REINFORCEMENT OF WALLS		REINFORCEMENT OF FLOOR	
THICKNESS	: 20 cm	THICKNESS	: 20 cm
VERTICAL BARS	: T12/15cm C/C BOTH SIDES	MAIN REINF.	: T12/15cm C/C TOP & BOTTOM.
HORIZONTAL BARS	: T10/15cm C/C BOTH SIDES	DIST. REINF	: T10/15cm C/C TOP & BOTTOM.

Government of Ras Al Khaimah
WASTEWATER AGENCY
حكومة رأس الخيمة
مؤسسة الصرف الصحي
26 June 2024
APPROVED
PRMT-24-0003939
Signed

Savana
Engineering Consultancy & Interior Design

Client	SAID AHMED MOHAMMED ALMANSOURI		
Project	DOUBLE STOREY VILLA		
Drg.Title	Septic Tank Details		
Area	ALRIFAA	Floortype	
Case ID.	2542576	Draw. Type.	DRNG
Sec No.	2	Com. No.	
Block No.		Plot No.	607011962
Bldg. No.	BLD-24-03157	Floor No.	
Date	JUN2024	Sht. No.	D05
Scale	1:100	Job No.	

G.Manager	Architect	Drawn by
ENG.AYMEN	ENG.IMEN	M.IMEN

4
D-07
Septic Tank Details
SCALE 1:100

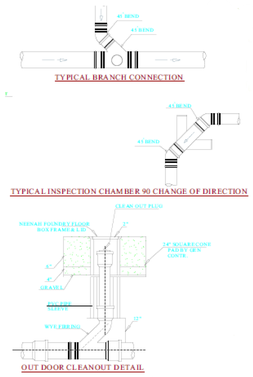

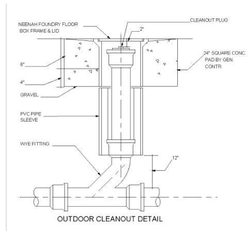

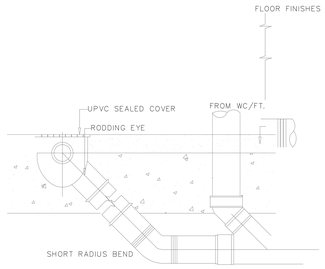

FLOOR CLEAN OUT (FCO)
NEAR WC CONNECTION

DRAINAGE MANHOLE SCHEDULE

MANHOLE REFERENCE	DIST BETWEEN CLEAN OUT (M)	COVER LEVEL (CM)	INVERT LEVEL (CM)	CLEAN OUT DEPTH (CM)
C.1		+60	+5	55
C.2	5m	+60	+0	60
C.3	4m	+60	-4	64
C.4	1m	+60	-5	65
C.5	9m	+60	-14	74
C.6	6m	+60	-20	80
C.7	14m	+60	-34	94
M.H2	13m	+10	-97	107
M.H1	2m	+10	-95	105
F.I.C	3m	+10	-100	X=384624.9022 Y=2840197.9068 DEPTH=110

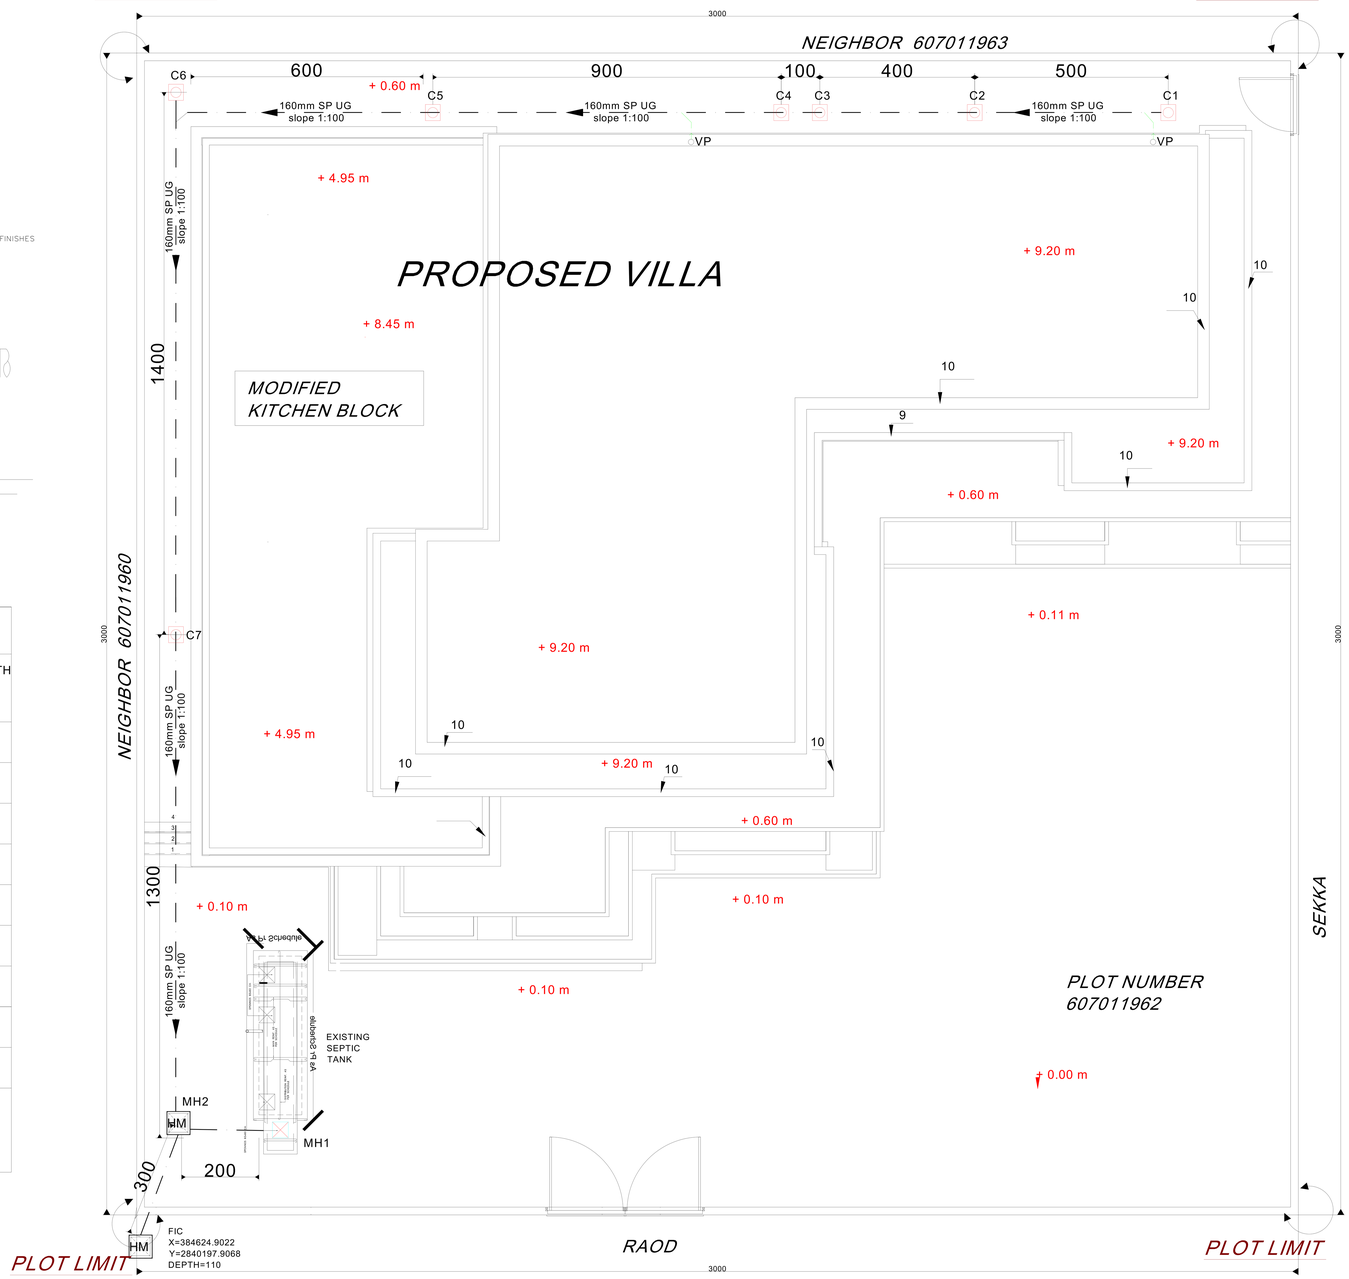

Government of Ras Al Khaimah
WASTEWATER AGENCY
حكومة رأس الخيمة
مؤسسة الصرف الصحي
APPROVED
08 July 2024
PRMT-24-0003939
Signed

Savana
Engineering Consultancy & interior design

Client	SAID AHMED MOHAMMED ALMANSOURI		
Project	DOUBLE STOREY VILLA		
Drg.Title	Site Development Drainage Layout Plan		
Area	ALRIFAA	Floortype	
Case ID.	2542576	Draw. Type.	DRNG
Sec No.	2	Com. No.	
Block No.		Plot No.	607011962
Bldg. No.	BLD-24-03157	Floor No.	
Date	JUN2024	Sht. No.	D01
Scale	1:100	Job No.	

G.Manager	Architect	Drawn by
ENG.AYMEN	ENG.IMEN	M.IMEN

4
D-01
Site Development Drainage Layout Plan
SCALE 1:100