



**بلدية رأس الخيمة  
إدارة التخطيط والمصاحبة**


**Ras Al Khaimah Municipality  
Town Planning and Survey  
Administration**

بلدية رأس الخيمة  
Ras Al Khaimah Municipality

المالك : سعيد احمد محمد حسن المنصوري

| الاشترارات التخطيطية |       |                   |        | مواصفات القسيمة                        |   |                                            |                  |
|----------------------|-------|-------------------|--------|----------------------------------------|---|--------------------------------------------|------------------|
| منسوب الرصيف         |       | عدد الطوابق       |        | نسبة البناء                            |   | الرقم المميز : 607011962                   |                  |
|                      |       | <u>الإرتدادات</u> |        | اسم المنطقة : الرفاعة                  |   | استخدام الارض : سكني                       |                  |
| الغرب                | الشرق | الجنوب            | الشمال | 9687.51                                | = | 900 متر مربع                               | المساحة الكلية   |
|                      |       |                   |        | قدم مربع                               | = | متر مربع                                   | المساحة المتأثرة |
|                      |       | <u>البروزات</u>   |        | 9687.51                                |   | =                                          | 900 متر مربع     |
| الغرب                | الشرق | الجنوب            | الشمال | قدم مربع                               | = |                                            | المساحة المتبقية |
|                      |       |                   |        | تاريخ الانتهاء : 07/05/2026            |   | رقم الكروكي : 199784                       |                  |
|                      |       |                   |        | نوع المنحة : برنامج الشيخ زايد للإسكان |   | تاريخ الاصدار : 07/05/2025                 |                  |
|                      |       |                   |        |                                        |   | الرقم المرجعي / رقم الرسالة : 2023/120/120 |                  |

ملاحظات: تم التحويل من منحة عادية إلى منحة برنامج الشيخ زايد للإسكان بموجب الرسالة الصادرة بتاريخ 2023/11/24

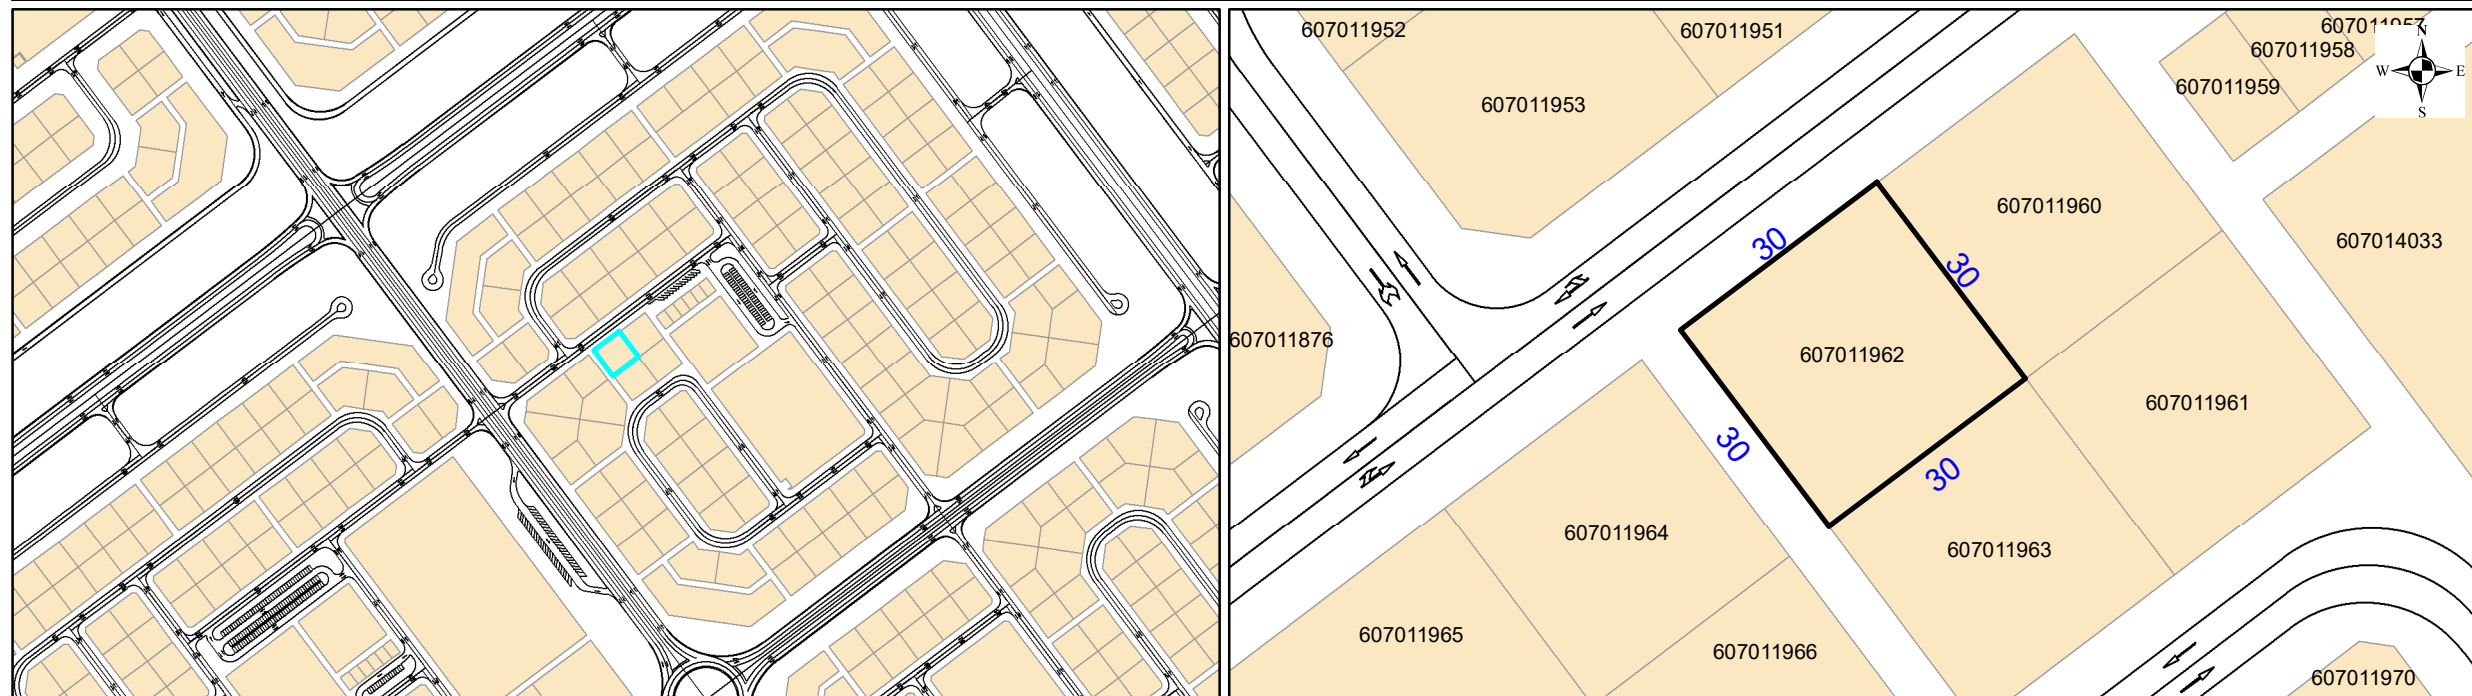

## الرؤية

بلدية رائدة لإمارة صحية وسعيدة ومستدامة

## الرسالة

الابتكار في تقديم خدمات بلدية متميزة تضمن الاستدامة في  
التطوير العمراني والصحة العامة من خلال التوظيف الأمثل للموارد لتحقيق السعادة لكافة شرائح المجتمع



اعتماد مدير  
ادارة التخطيط والمساحة

ممنوع البيع نهائيا بأمر من سمو الحاكم المؤرخ في 2001/01/31  
القسيمة مقبدة