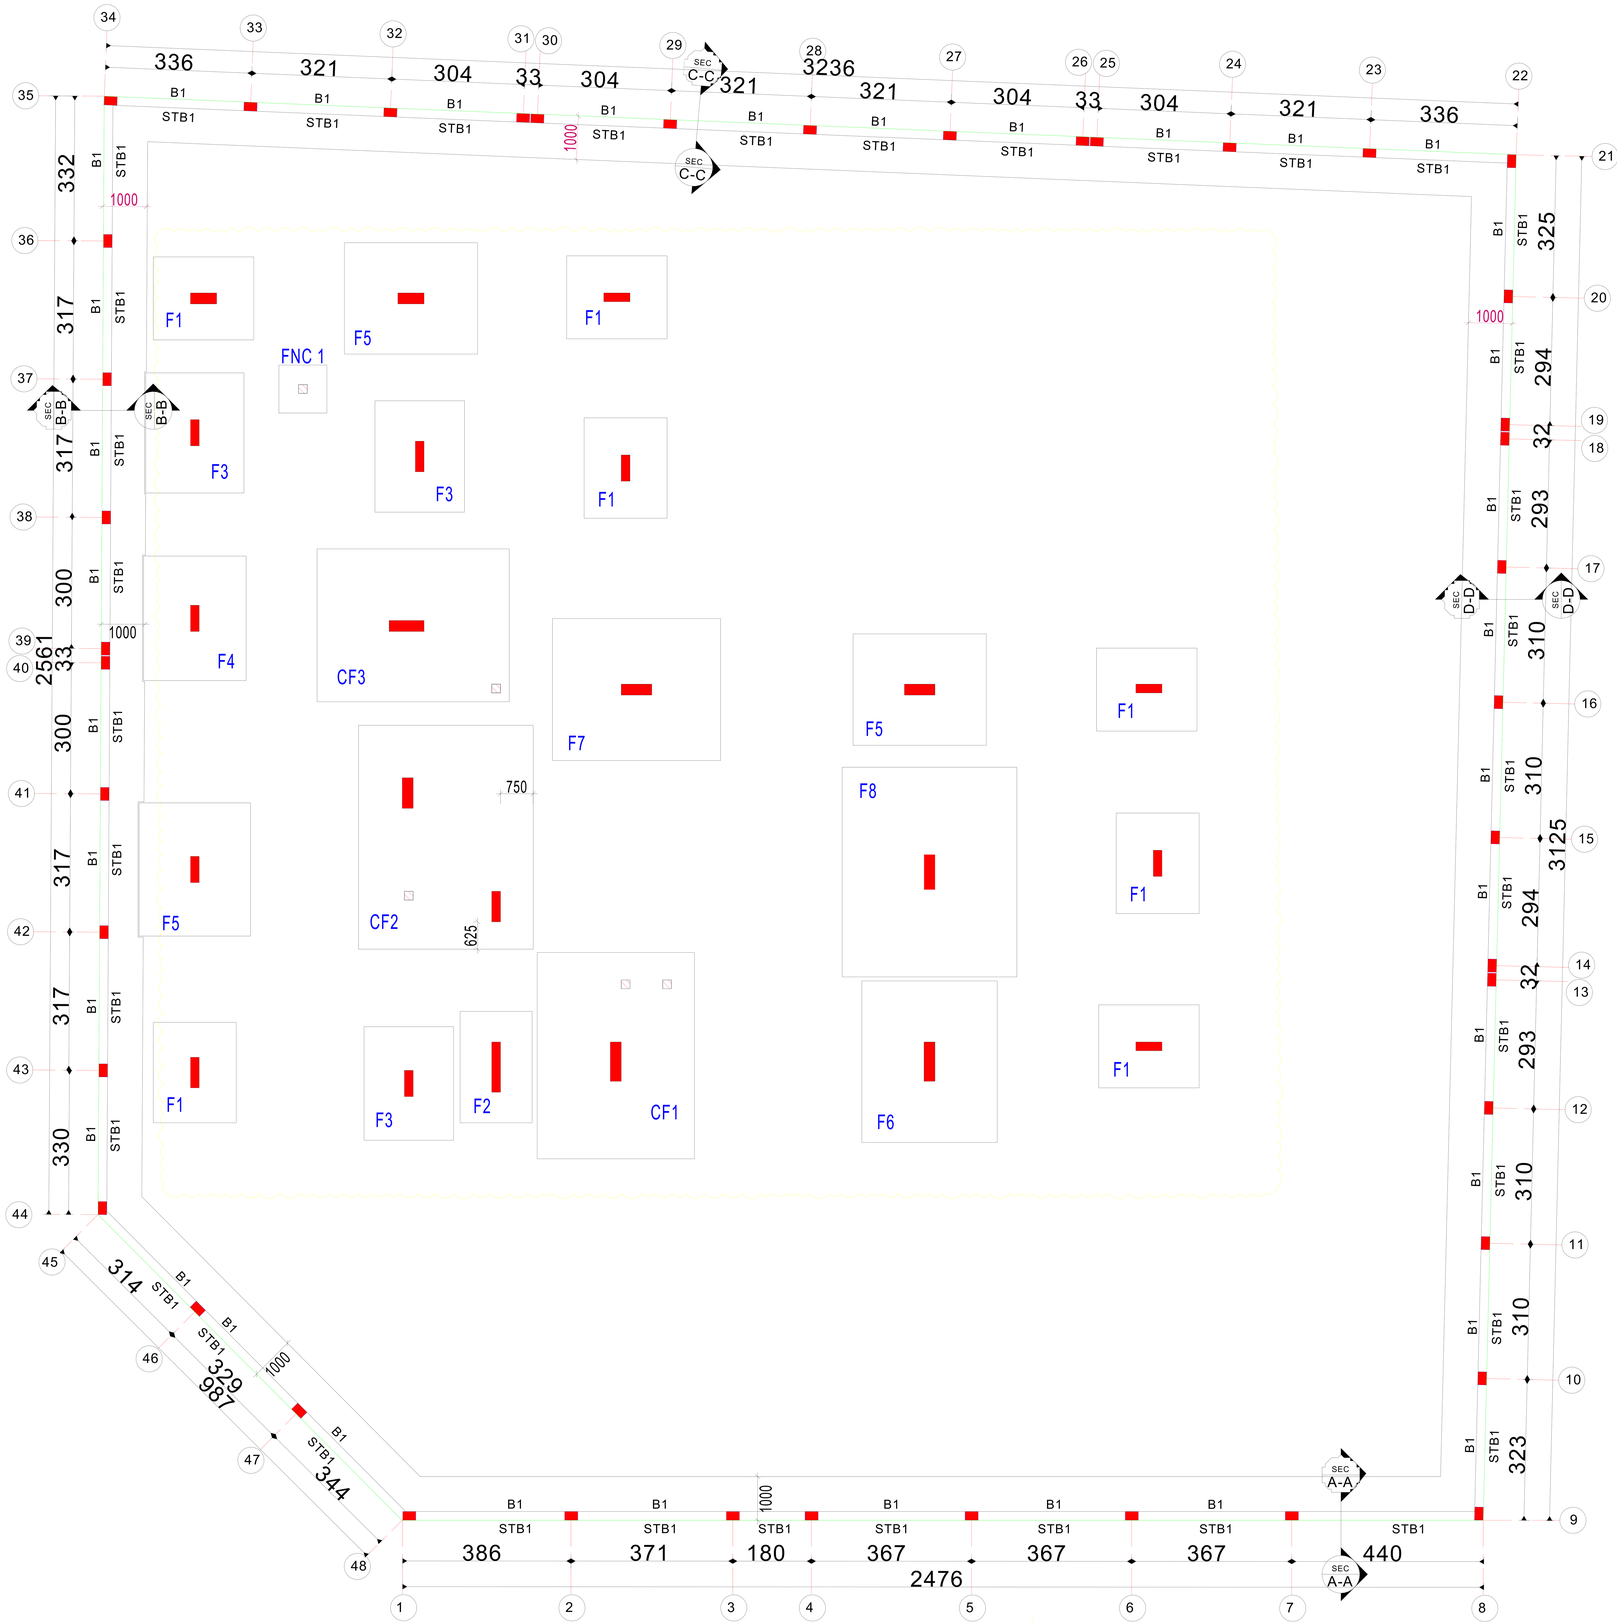

Govement Of Ras Al Khaimah
R.A.K. Municipality
Buildings Administration

حكومة رأس الخيمة
دائرة البلدية
إدارة المباني

Approved On — اعتمد في

09 December 2024

Building Permit #: PRMT-24-0004326

Appoved By:

Savana
Engineering Consultancy & interior design

Client	KHALED ALI SAEED BEN SHUOOM AL SHEHHI		
Project	DOUBLE STORY VILAA		
Drg.Title	COMPOUND WALL LAYOUT		
Area	AWAFI	Floortype	
Case ID.	2712017	Draw. Type.	STRC
Sec No.	1	Com. No.	
Block No.		Plot No.	406131922
Bldg. No.	FNC-24-002142	Floor No.	
Date	DEC- 2024	Sht. No.	S12
Scale	1/100	Job No.	

G.Manager	Architect	Designed By
ENG AYMEN	ENG IMEN	ENG IMEN