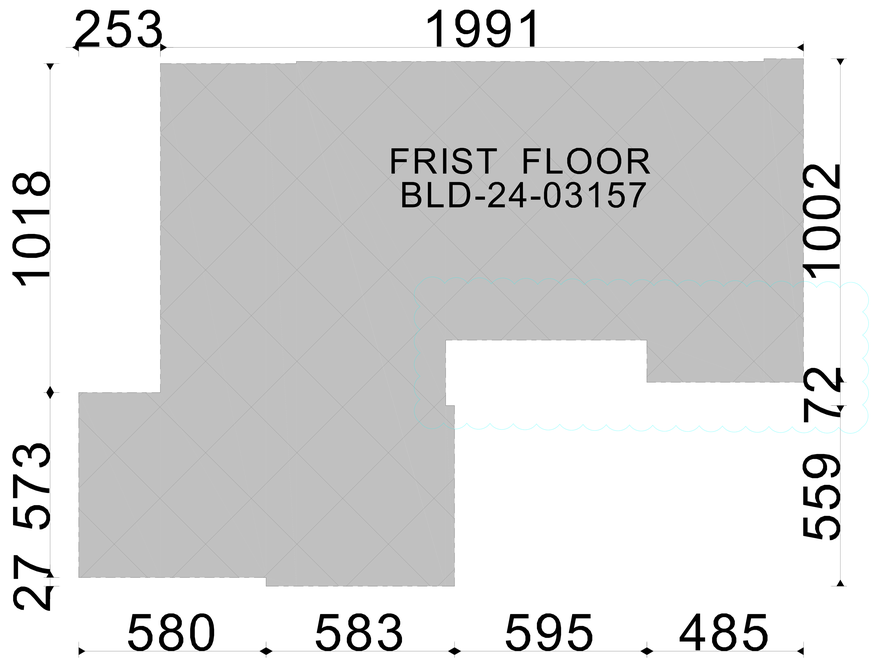

AREA STATMENTENT

Govemment Of Ras Al Khaimah
R.A.K. Municipality
Buildings Administration

حكومة رأس الخيمة
دائرة البلدية
إدارة المباني

Approved On — اعتمد في

12 November 2024

Building Permit #: PRMT-24-0005227

Appoved By:

Area Statement	
Building Number	BLD-24-03157
Ground Floor Villa Area	383.3 m²
First Floor Villa Area	263.4m²
Total Building Area	646.7m²
PLOT AREA ACCORDING TO KRUKI	900m²
BUILD UP RATIO	42.55 %

Savana
Engineering Consultancy & interior design

Client	SAEED AHMED MOHAMMED HASAN ALMANSORI		
Project	DOUBLE STORY VILAA		
Drg.Title	AreaStatement		
Area	ARIFAA	Floortype	
Case ID.	2673356	Draw. Type.	ARCH
Sec No.	1	Com. No.	
Block No.		Plot No.	607011962
Bldg. No.	BLD-24-03157	Floor No.	
Date	OCT-2024	Sht. No.	A-01
Scale	1/100	Job No.	

G.Manager	Architect	Designed By
ENG AYMEN	ENG IMEN	ENG IMEN

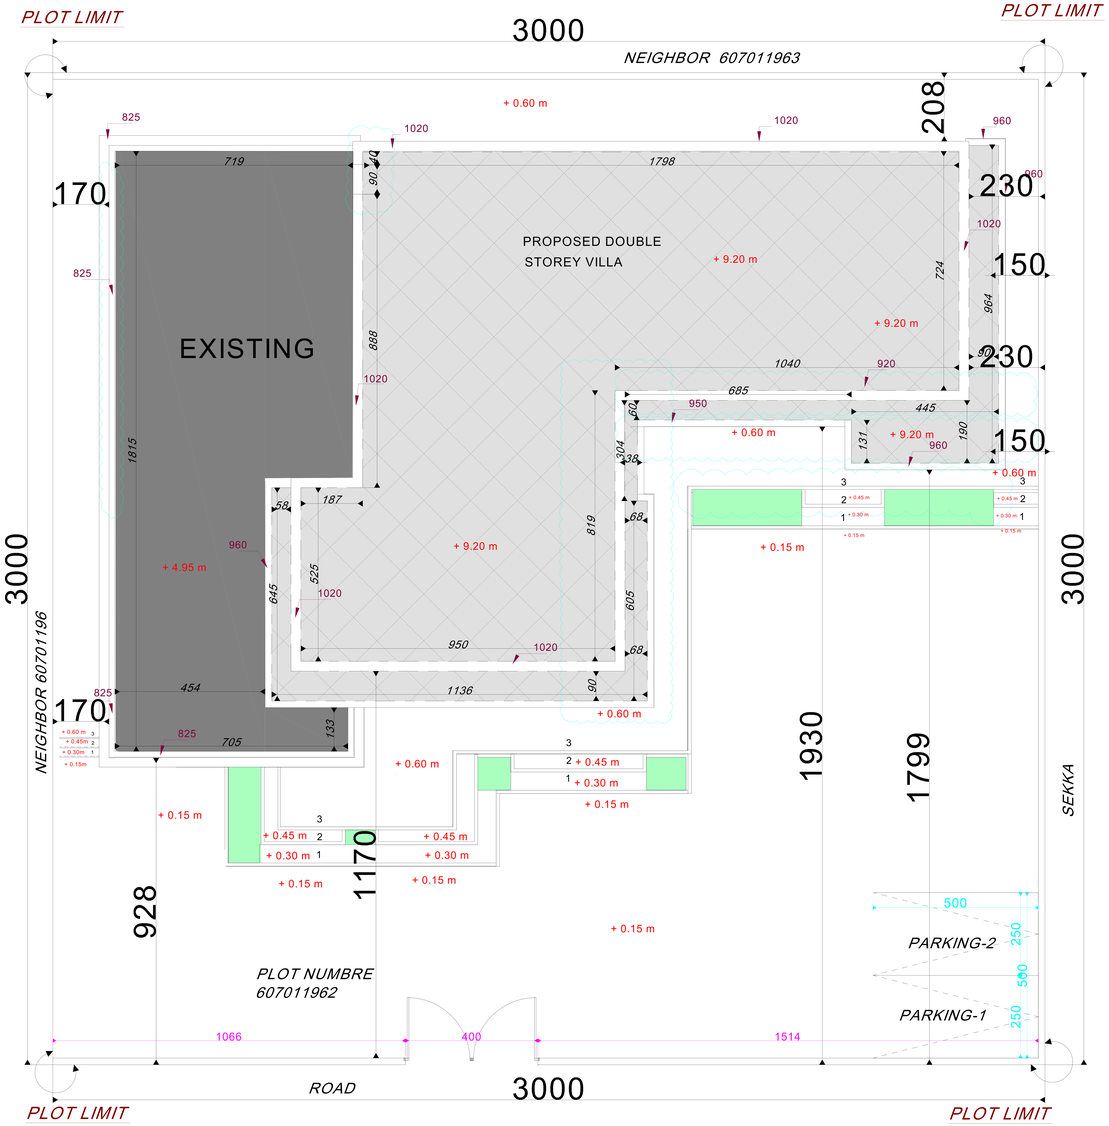

Govemment Of Ras Al Khaimah
R.A.K. Municipality
Buildings Administration

حكومة رأس الخيمة
دائرة البلدية
إدارة المباني

Approved On — اعتمد في

12 November 2024

Building Permit #: PRMT-24-0005227

Appoved By:

Client	SAEED AHMED MOHAMMED HASAN ALMANSORI		
Project	DOUBLE STORY VILAA		
Drg.Title	Site Development Layout Plan		
Area	ARIFAA	Floortype	
Case ID.	2673356	Draw. Type.	ARCH
Sec No.	1	Com. No.	
Block No.		Plot No.	607011962
Bldg. No.	BLD-24-03157	Floor No.	
Date	OCT-2024	Sht. No.	A02
Scale	1/100	Job No.	

G.Manager	Architect	Designed By
ENG AYMEN	ENG IMEN	ENG IMEN

SITE DEVELOPMENT LAYOUT PLAN

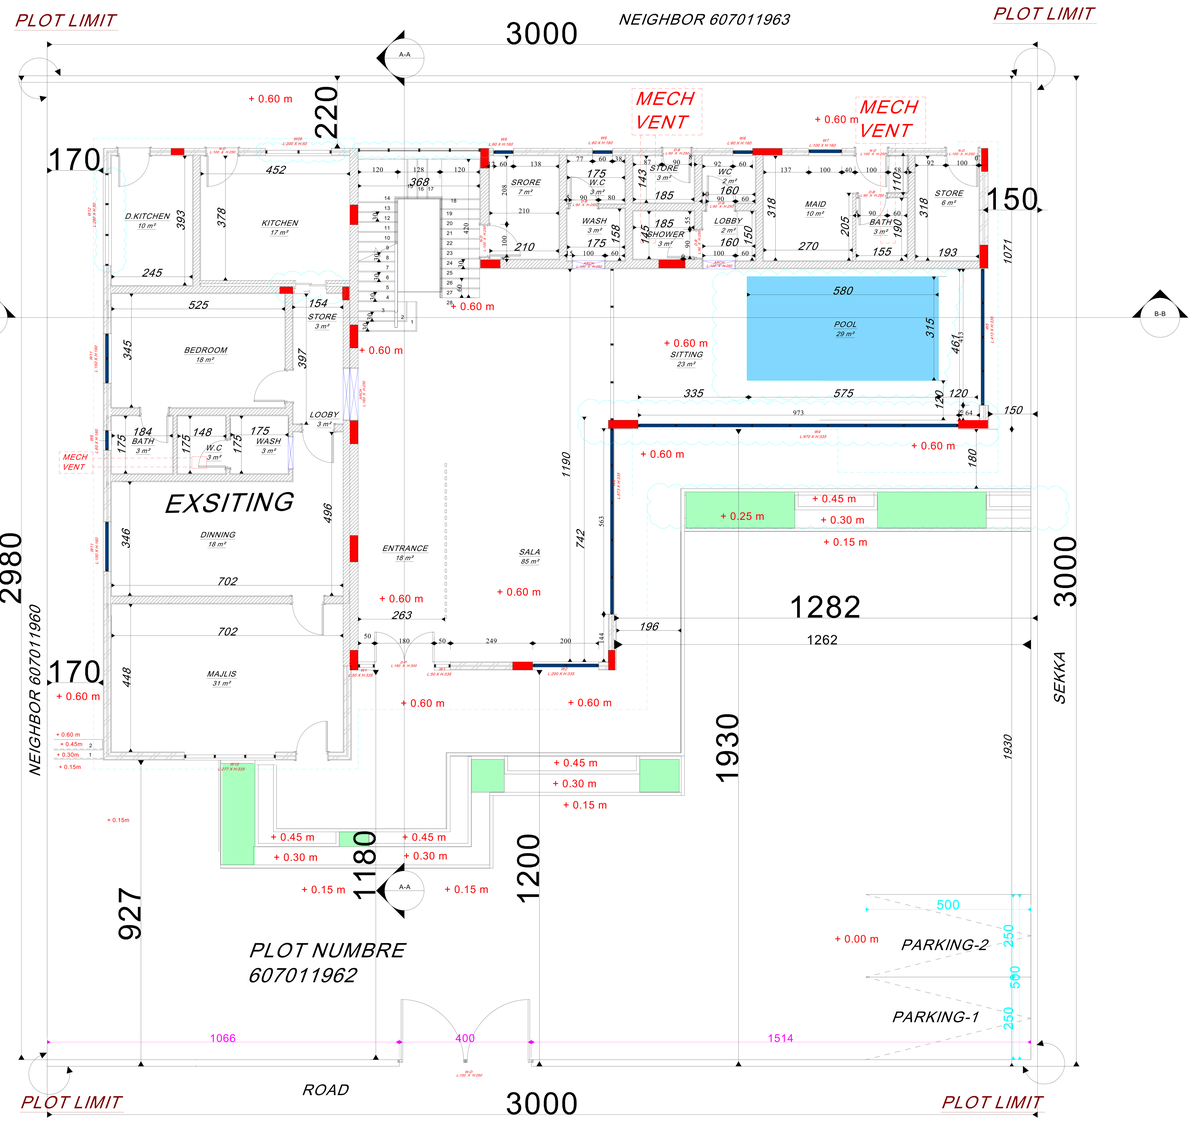

Govement Of Ras Al Khaimah
R.A.K. Municipality
Buildings Administration

حكومة رأس الخيمة
دائرة البلدية
إدارة المباني

Approved On — اعتمد في

12 November 2024

Building Permit #: PRMT-24-0005227

Appoved By:

Savana
Engineering Consultancy & Interior design

Client	SAEED AHMED MOHAMMED HASAN ALMANSORI		
Project	DOUBLE STORY VILAA		
Drg.Title	SITE SETTING PLAN		
Area	ARIFAA	Floortype	
Case ID.	2673356	Draw. Type.	ARCH
Sec No.	1	Com. No.	
Block No.		Plot No.	607011962
Bldg. No.	BLD-24-03157	Floor No.	
Date	OCT-2024	Sht. No.	A03
Scale	1/100	Job No.	

G.Manager	Architect	Designed By
ENG AYMEN	ENG IMEN	ENG IMEN

SITE SETTING PLAN

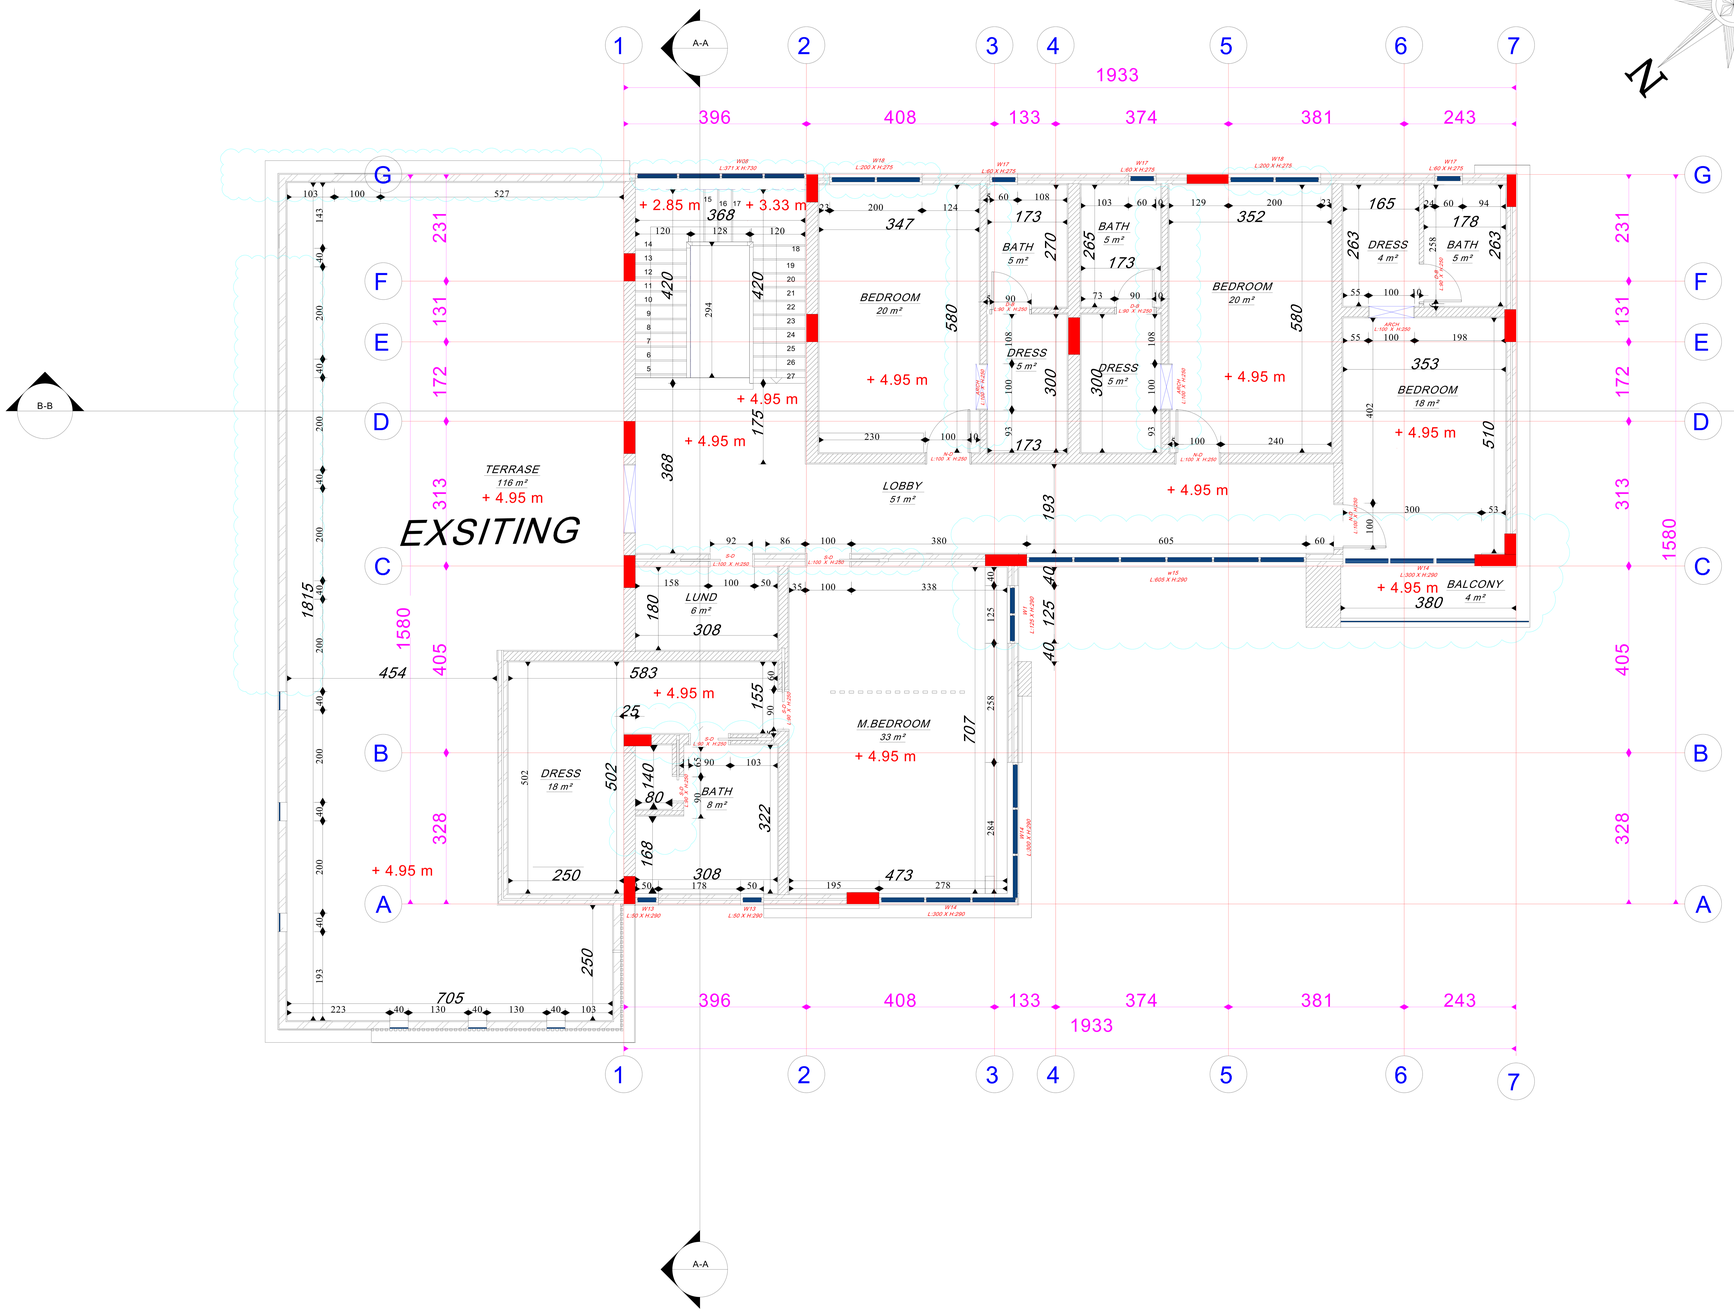

Govvernment Of Ras Al Khaimah
R.A.K. Municipality
Buildings Administration

حكومة رأس الخيمة
دائرة البلدية
إدارة المباني

Approved On — اعتمد في

12 November 2024

Building Permit #: PRMT-24-0005227

Appoved By:

FINISHING FOR VERANDAH	FINISHING FOR DRESSING AREA	FINISHING FOR BATH,WC & WASH	
FLOORING	F1 Ceramic glazed tiles	F2 Ceramic Tiles (Non Slippery)	F3 Marble Tiles
WALLS	W1 Acrylic emulsion paint	W2 Ceramic tiles up to ceiling	W3 Epoxy paint.
SKIRTING	S1 Ceramic Tiles. 10cm hight	S2 Marble tiles 10cm hight	
CEILING	C1 Acrylic emulsion paint	C2 Oil Paint.	C3 Epoxy paint.

Note :-

* Rcc Lintels Must Be Made On Top Of All Doors , Arches And Windows All Of Them Are At Least 0.20 m Thick.
* All Blocks Adjacent To All Doors , Arches And Windows Must Be A Solid Block .

Rooms	Space	Number
Residential	263.4	
Commercial		
Industrial		
Goverment		
Resident.-Comm.		
Total		

Savana
Engineering Consultancy & interior design

Client	SAEED AHMED MOHAMMED HASAN ALMANSORI		
Project	DOUBLE STORY VILAA		
Drg.Title	FIRST FLOOR PLAN		
Area	ARIFAA	Floortype	F
Case ID.	2673356	Draw. Type.	ARCH
Sec No.	1	Com. No.	
Block No.		Plot No.	607011962
Bldg. No.	BLD-24-03157	Floor No.	01
Date	OCT-2024	Sht. No.	A05
Scale	1/100	Job No.	

G.Manager	Architect	Designed By
ENG AYMEN	ENG IMEN	ENG IMEN

FIRST FLOOR PLAN

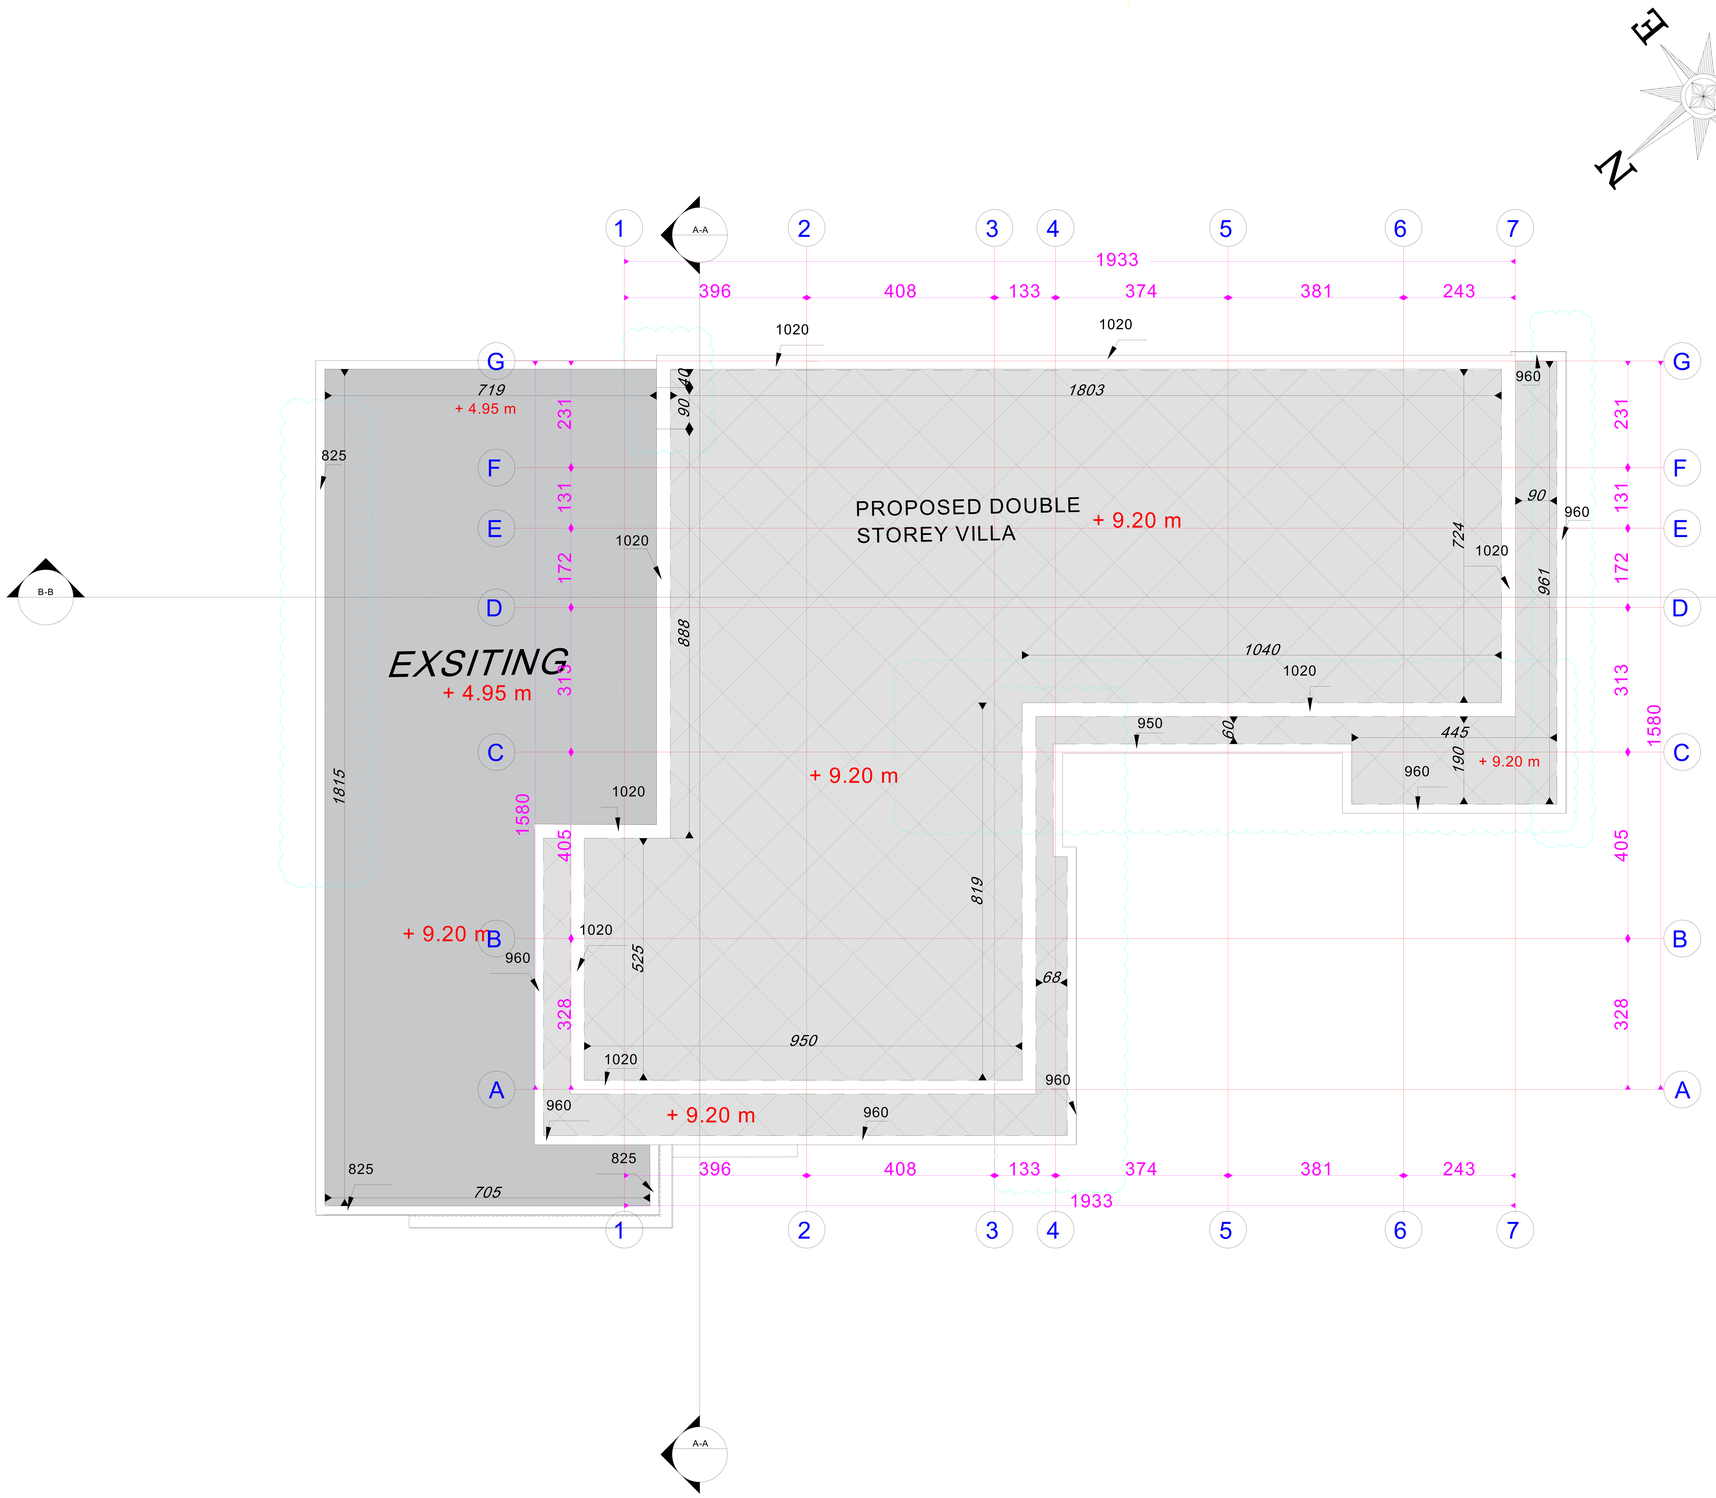

FINISHING FOR VERANDAH		FINISHING FOR BATH,WC & WASH AREA	
		C3 S2 F3 W3	C2 S1 F2 W2
FLOORING			
F3	Marble Tiles	F1	Ceramic glazed tiles
		F2	Ceramic Tiles (Non Slippery)
WALLS			
W3	Epoxy paint.	W1	Acrylic emulsion paint
		W2	Ceramic tiles up to ceiling
SKIRTING			
		S2	Marble tiles 10cm hight
		S1	Ceramic Tiles. 10cm hight
CEILING			
C3	Epoxy paint.	C2	Oil Paint.
		C1	Acrylic emulsion paint

Govemment Of Ras Al Khaimah
R.A.K. Municipality
Buildings Administration

حكومة رأس الخيمة
دائرة البلدية
إدارة المباني

Approved On — اعتمد في

12 November 2024

Building Permit #: PRMT-24-0005227

Appoved By:

Savana
Engineering Consultancy & interior design

Client	SAEED AHMED MOHAMMED HASAN ALMANSORI		
Project	DOUBLE STORY VILAA		
Drg.Title	TOP ROOF PLAN		
Area	ARIFAA	Floortype	
Case ID.	2673356	Draw. Type.	ARCH
Sec No.	1	Com. No.	
Block No.		Plot No.	607011962
Bldg. No.	BLD-24-03157	Floor No.	
Date	OCT-2024	Sht. No.	A06A
Scale	1/100	Job No.	

G.Manager	Architect	Designed By
ENG AYMEN	ENG IMEN	ENG IMEN

TOP ROOF FLOOR PLAN

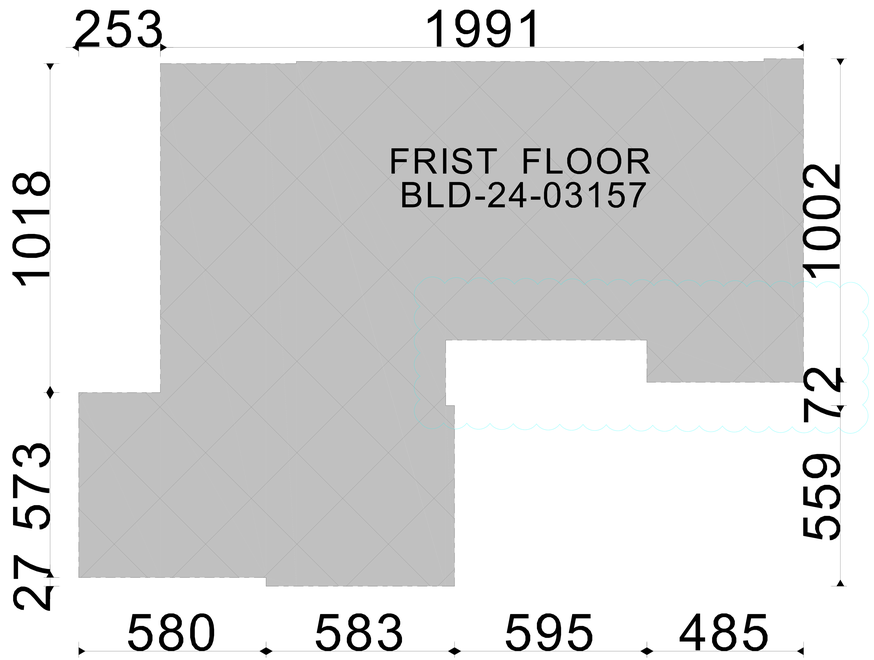

AREA STATMENTENT

Govemment Of Ras Al Khaimah
R.A.K. Municipality
Buildings Administration

حكومة رأس الخيمة
دائرة البلدية
إدارة المباني

Approved On — اعتمد في

12 November 2024

Building Permit #: PRMT-24-0005227

Appoved By:

Area Statement	
Building Number	BLD-24-03157
Ground Floor Villa Area	383.3 m²
First Floor Villa Area	263.4m²
Total Building Area	646.7m²
PLOT AREA ACCORDING TO KRUKI	900m²
BUILD UP RATIO	42.55 %

Savana
Engineering Consultancy & interior design

Client	SAEED AHMED MOHAMMED HASAN ALMANSORI		
Project	DOUBLE STORY VILAA		
Drg.Title	AreaStatement		
Area	ARIFAA	Floortype	
Case ID.	2673356	Draw. Type.	ARCH
Sec No.	1	Com. No.	
Block No.		Plot No.	607011962
Bldg. No.	BLD-24-03157	Floor No.	
Date	OCT-2024	Sht. No.	A-01
Scale	1/100	Job No.	

G.Manager	Architect	Designed By
ENG AYMEN	ENG IMEN	ENG IMEN

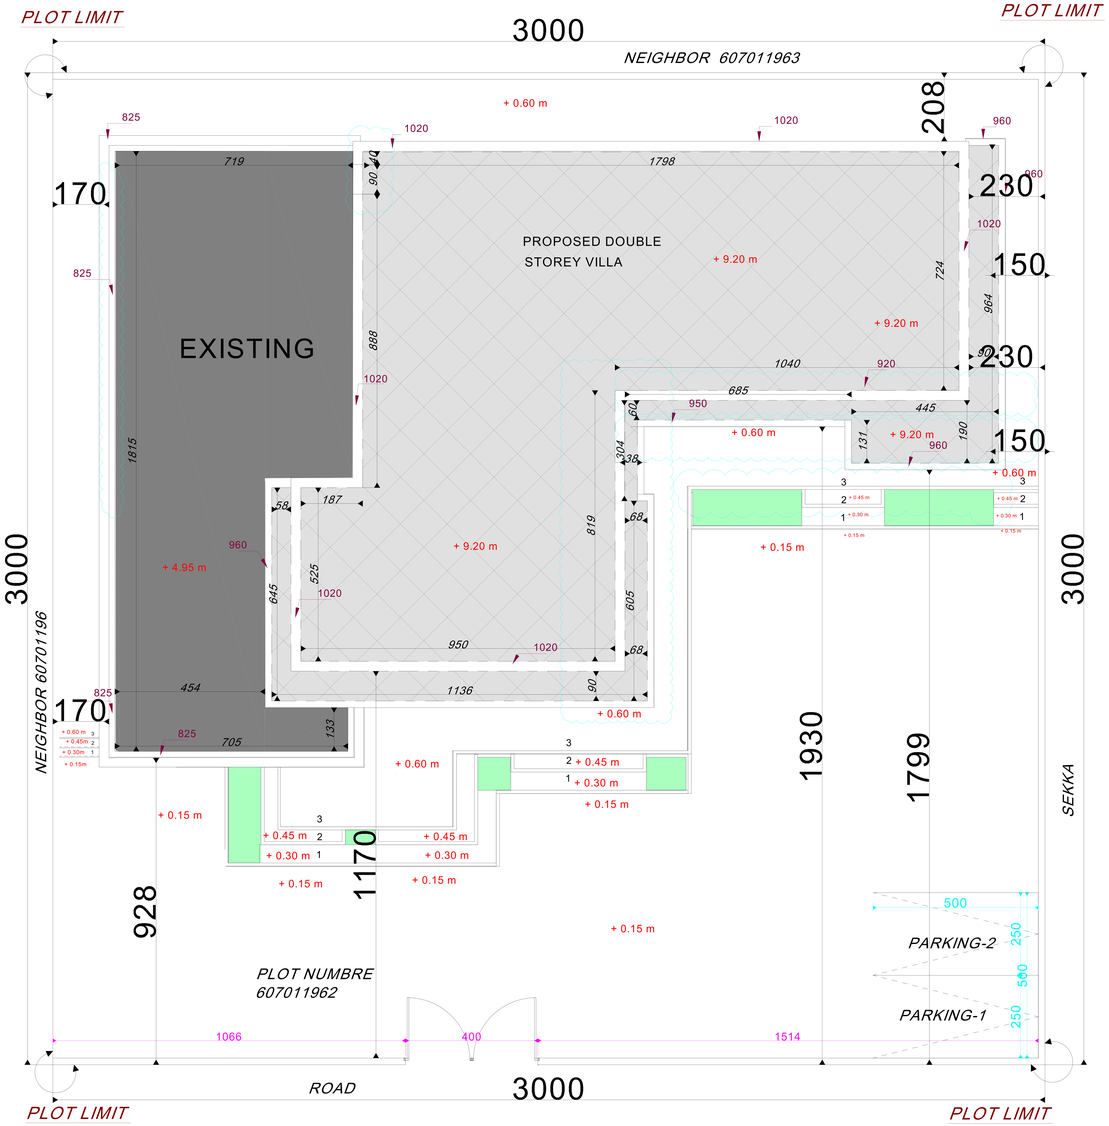

Govemment Of Ras Al Khaimah
R.A.K. Municipality
Buildings Administration

حكومة رأس الخيمة
دائرة البلدية
إدارة المباني

Approved On — اعتمد في

12 November 2024

Building Permit #: PRMT-24-0005227

Appoved By:

Client	SAEED AHMED MOHAMMED HASAN ALMANSORI		
Project	DOUBLE STORY VILAA		
Drg.Title	Site Development Layout Plan		
Area	ARIFAA	Floortype	
Case ID.	2673356	Draw. Type.	ARCH
Sec No.	1	Com. No.	
Block No.		Plot No.	607011962
Bldg. No.	BLD-24-03157	Floor No.	
Date	OCT-2024	Sht. No.	A02
Scale	1/100	Job No.	

G.Manager	Architect	Designed By
ENG AYMEN	ENG IMEN	ENG IMEN

SITE DEVELOPMENT LAYOUT PLAN

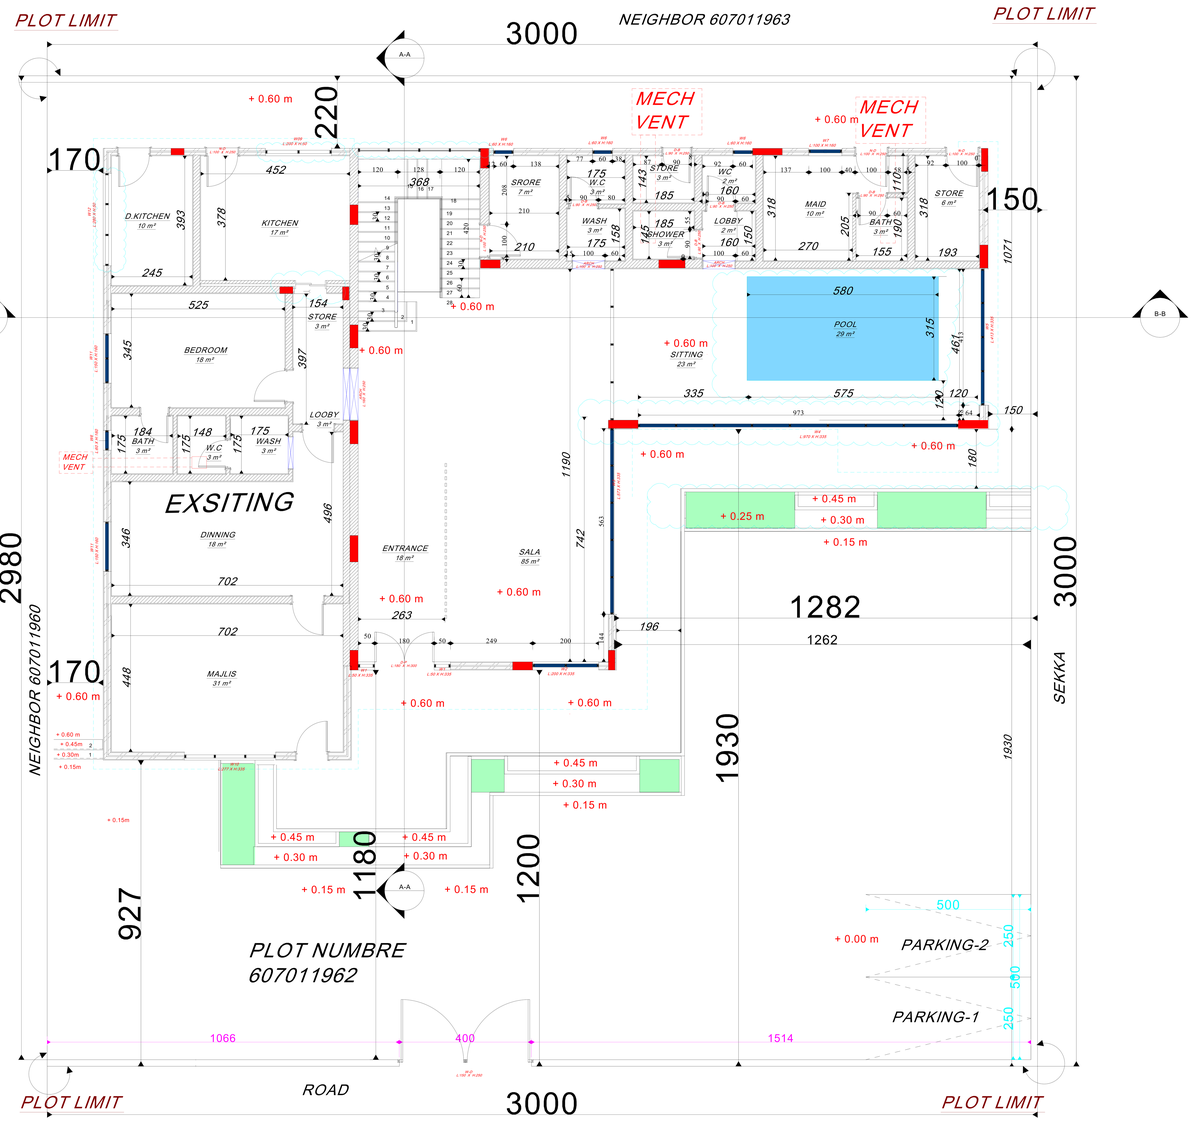

Govement Of Ras Al Khaimah
R.A.K. Municipality
Buildings Administration

حكومة رأس الخيمة
دائرة البلدية
إدارة المباني

Approved On — اعتمد في

12 November 2024

Building Permit #: PRMT-24-0005227

Appoved By:

Savana
Engineering Consultancy & Interior design

Client	SAEED AHMED MOHAMMED HASAN ALMANSORI		
Project	DOUBLE STORY VILAA		
Drg.Title	SITE SETTING PLAN		
Area	ARIFAA	Floortype	
Case ID.	2673356	Draw. Type.	ARCH
Sec No.	1	Com. No.	
Block No.		Plot No.	607011962
Bldg. No.	BLD-24-03157	Floor No.	
Date	OCT-2024	Sht. No.	A03
Scale	1/100	Job No.	

G.Manager	Architect	Designed By
ENG AYMEN	ENG IMEN	ENG IMEN

SITE SETTING PLAN

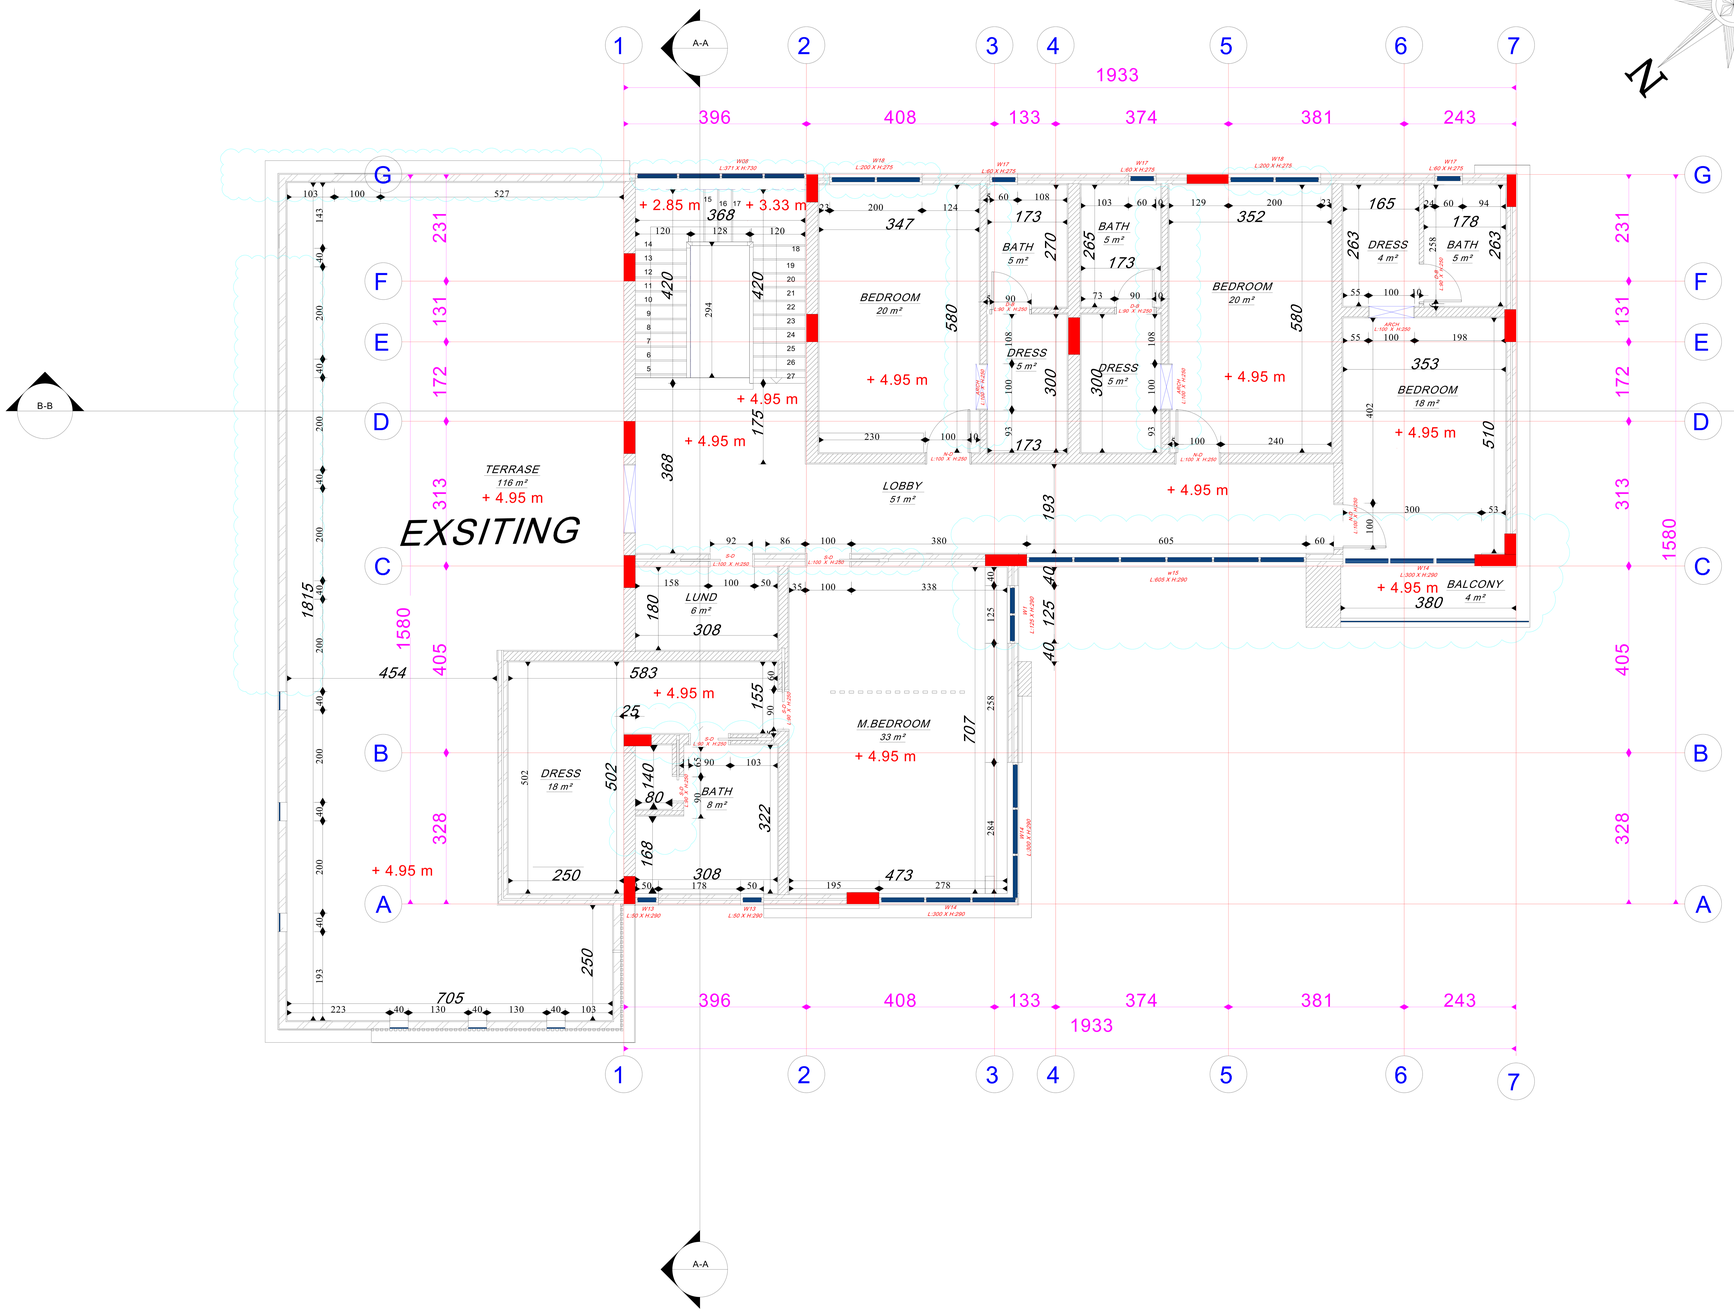

Govvernment Of Ras Al Khaimah
R.A.K. Municipality
Buildings Administration

حكومة رأس الخيمة
دائرة البلدية
إدارة المباني

Approved On — اعتمد في

12 November 2024

Building Permit #: PRMT-24-0005227

Appoved By:

FINISHING FOR VERANDAH	FINISHING FOR DRESSING AREA	FINISHING FOR BATH,WC & WASH	
FLOORING	F1 Ceramic glazed tiles	F2 Ceramic Tiles (Non Slippery)	F3 Marble Tiles
WALLS	W1 Acrylic emulsion paint	W2 Ceramic tiles up to ceiling	W3 Epoxy paint.
SKIRTING	S1 Ceramic Tiles. 10cm hight	S2 Marble tiles 10cm hight	
CEILING	C1 Acrylic emulsion paint	C2 Oil Paint.	C3 Epoxy paint.

Note :-

* Rcc Lintels Must Be Made On Top Of All Doors , Arches And Windows All Of Them Are At Least 0.20 m Thick.
* All Blocks Adjacent To All Doors , Arches And Windows Must Be A Solid Block .

Rooms	Space	Number
Residential	263.4	
Commercial		
Industrial		
Goverment		
Resident.-Comm.		
Total		

Savana
Engineering Consultancy & interior design

Client	SAEED AHMED MOHAMMED HASAN ALMANSORI		
Project	DOUBLE STORY VILAA		
Drg.Title	FIRST FLOOR PLAN		
Area	ARIFAA	Floortype	F
Case ID.	2673356	Draw. Type.	ARCH
Sec No.	1	Com. No.	
Block No.		Plot No.	607011962
Bldg. No.	BLD-24-03157	Floor No.	01
Date	OCT-2024	Sht. No.	A05
Scale	1/100	Job No.	

G.Manager	Architect	Designed By
ENG AYMEN	ENG IMEN	ENG IMEN

FIRST FLOOR PLAN

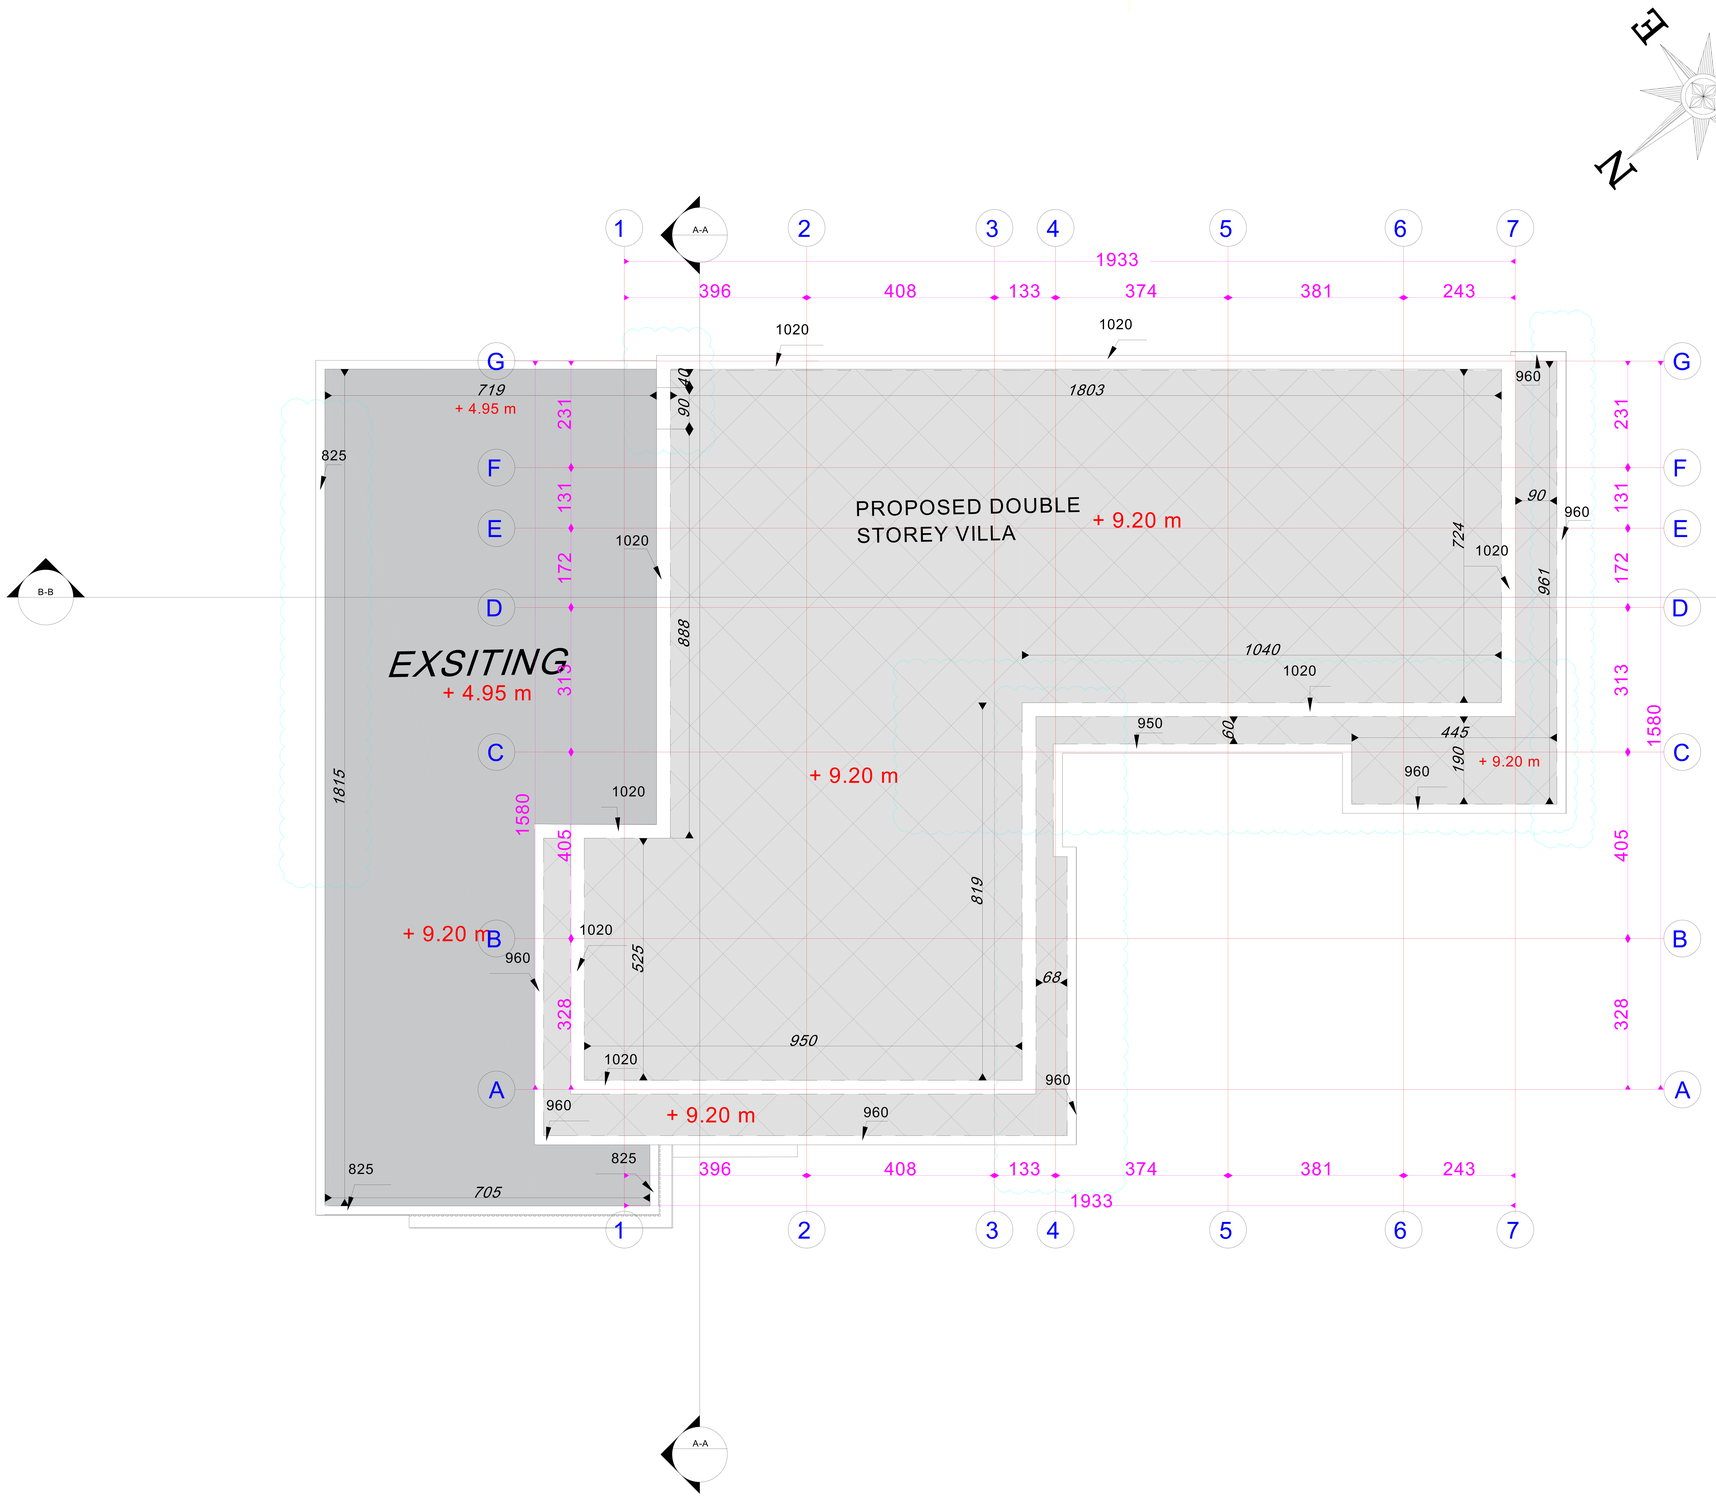

FINISHING FOR VERANDAH		FINISHING FOR BATH,WC & WASH AREA	
		C3 S2 F3 W3	C2 S1 F2 W2
FLOORING			
F3	Marble Tiles	F1	Ceramic glazed tiles
		F2	Ceramic Tiles (Non Slippery)
WALLS			
W3	Epoxy paint.	W1	Acrylic emulsion paint
		W2	Ceramic tiles up to ceiling
SKIRTING			
		S2	Marble tiles 10cm hight
		S1	Ceramic Tiles. 10cm hight
CEILING			
C3	Epoxy paint.	C2	Oil Paint.
		C1	Acrylic emulsion paint

Govemment Of Ras Al Khaimah
R.A.K. Municipality
Buildings Administration

حكومة رأس الخيمة
دائرة البلدية
إدارة المباني

Approved On — اعتمد في

12 November 2024

Building Permit #: PRMT-24-0005227

Appoved By:

Savana
Engineering Consultancy & interior design

Client	SAEED AHMED MOHAMMED HASAN ALMANSORI		
Project	DOUBLE STORY VILAA		
Drg.Title	TOP ROOF PLAN		
Area	ARIFAA	Floortype	
Case ID.	2673356	Draw. Type.	ARCH
Sec No.	1	Com. No.	
Block No.		Plot No.	607011962
Bldg. No.	BLD-24-03157	Floor No.	
Date	OCT-2024	Sht. No.	A06A
Scale	1/100	Job No.	

G.Manager	Architect	Designed By
ENG AYMEN	ENG IMEN	ENG IMEN

TOP ROOF FLOOR PLAN

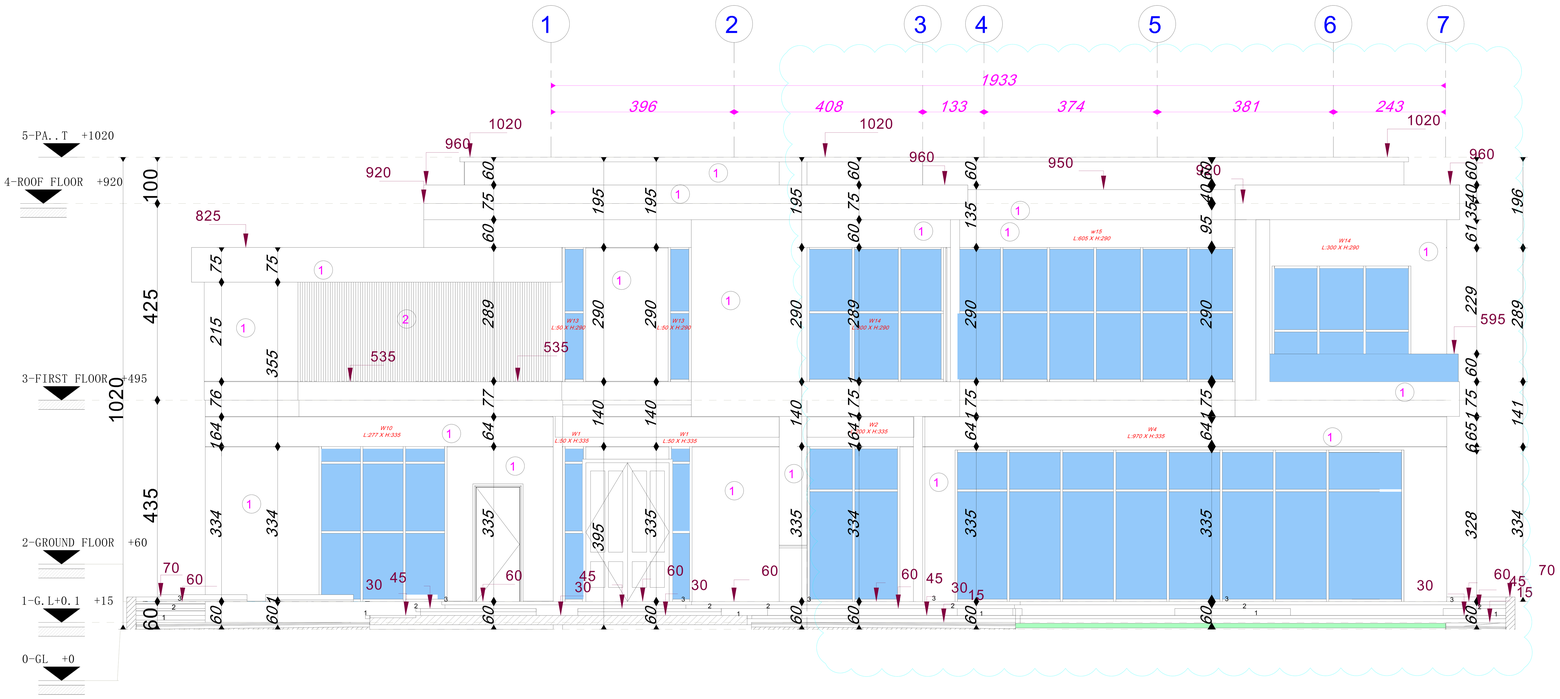

FRONT ELEVATION

Govemment Of Ras Al Khaimah
R.A.K. Municipality
Buildings Administration

حكومة رأس الخيمة
دائرة البلدية
إدارة المباني

Approved On — اعتمد في

12 November 2024

Building Permit #: PRMT-24-0005227

Appoved By:

FINSHING	
1	FULL EPOXY PAINT [white]
2	WOOD Aluminum
3	FULL EPOXY BLACK PAINT

Savana
Engineering Consultancy & interior design

Client	SAEED AHMED MOHAMMED HASAN ALMANSORI		
Project	DOUBLE STORY VILAA		
Drg.Title	FRONT ELEVATION		
Area	ARIFAA	Floortype	
Case ID.	2673356	Draw. Type.	ARCH
Sec No.	1	Com. No.	
Block No.		Plot No.	607011962
Bldg. No.	BLD-24-03157	Floor No.	
Date	OCT-2024	Sht. No.	A07
Scale	1/100	Job No.	

G.Manager	Architect	Designed By
ENG AYMEN	ENG IMEN	ENG IMEN

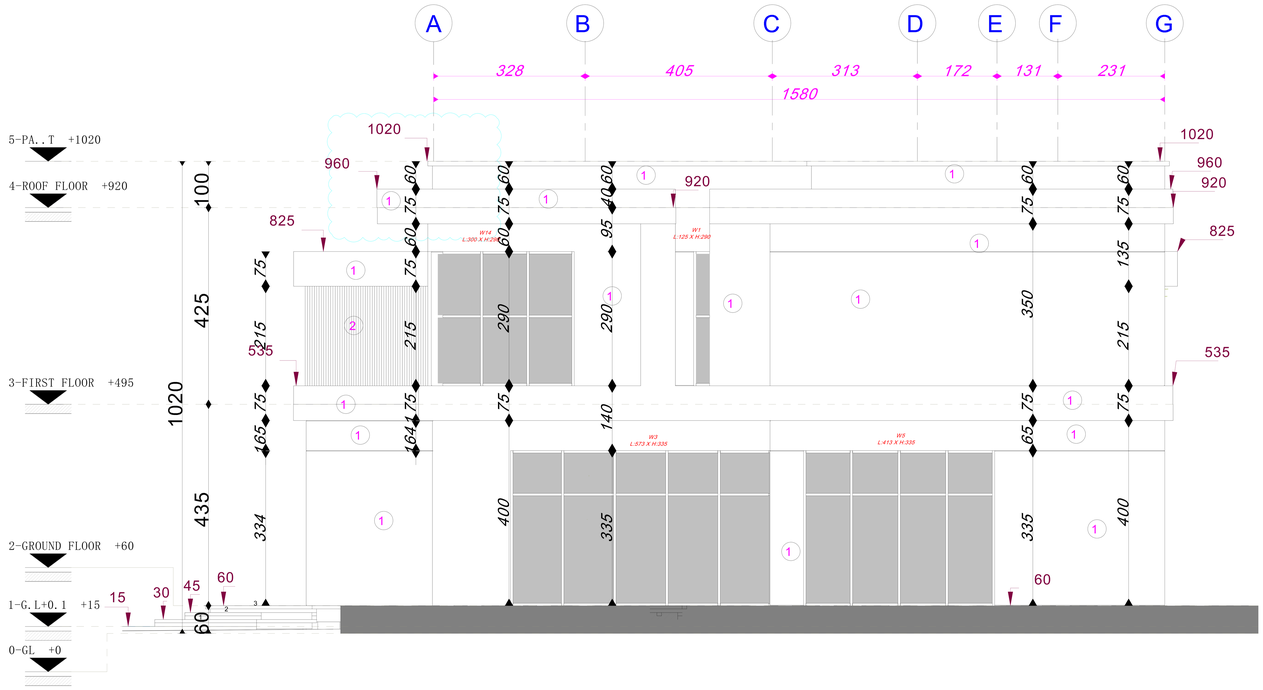

Govemment Of Ras Al Khaimah
R.A.K. Municipality
Buildings Administration

حكومة رأس الخيمة
دائرة البلدية
إدارة المباني

Approved On — اعتمد في

12 November 2024

Building Permit #: PRMT-24-0005227

Appoved By:

FINSHING	
1	FULL EPOXY PAINT [white]
2	FULL EPOXY BLACK PAINT
3	WOOD Aluminum

Savana
Engineering Consultancy & interior design

Client	SAEED AHMED MOHAMMED HASAN ALMANSORI		
Project	DOUBLE STORY VILAA		
Drg.Title	RIGHT ELEVATION		
Area	ARIFAA	Floortype	
Case ID.	2673356	Draw. Type.	ARCH
Sec No.	1	Com. No.	
Block No.		Plot No.	607011962
Bldg. No.	BLD-24-03157	Floor No.	
Date	OCT-2024	Sht. No.	A08
Scale	1/100	Job No.	

G.Manager	Architect	Designed By
ENG AYMEN	ENG IMEN	ENG IMEN

RIGHT ELEVATION

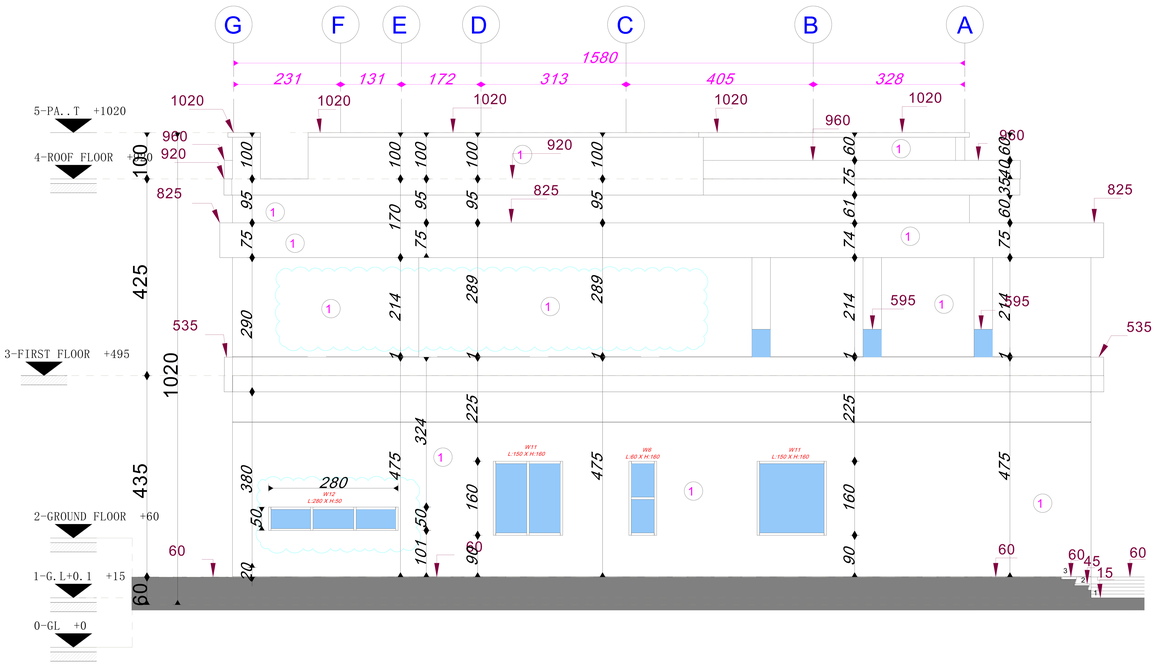

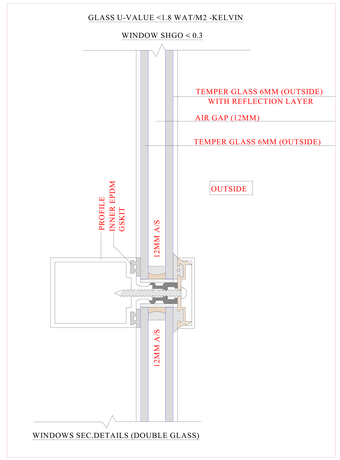

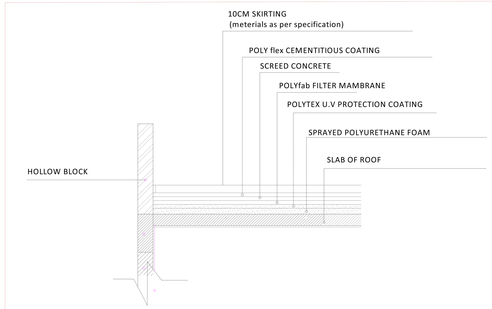

DETAIL FOR COMBO SYSTEM
U-VALUE <0.3 W/M2 K

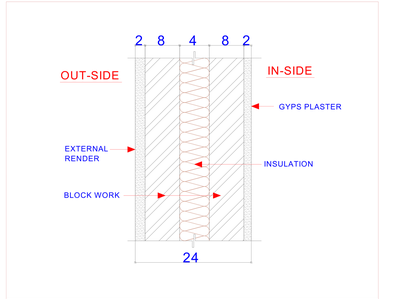

As per E. Walls Predefined Section: W - 1 - A

DETAIL 'W1'	TYPICAL FOR EXTERNAL WALL USING INSULATED CONC. BLOCK (200 mm) U-VALUE < 0.5 W/M2 K

LEFT ELEVATION

Govemment Of Ras Al Khaimah
R.A.K. Municipality
Buildings Administration

حكومة رأس الخيمة
دائرة البلدية
إدارة المباني

Approved On — اعتمد في

12 November 2024

Building Permit #: PRMT-24-0005227

Appoved By:

* Rcc Lintels Must Be Made On Top Of All Doors , Arches And Windows All Of Them Are At Least 0.20 m Thick.
* All Blocks Adjacent To All Doors , Arches And Windows Must Be A Solid Block .

U VALUE AND SHGC

ALL GLASS MUST BE DOUBLE UNITES

GLASS SPECIFICATION:-

U-value (w/m2.k)<_ 1.8

SHADING CO- EFFICIENT (SC) <0.3

FINSHING	
1	FULL EPOXY PAINT [white]
2	WOOD Aluminum
3	FULL EPOXY BLACK PAINT

Savana
Engineering Consultancy & interior design

Client	SAEED AHMED MOHAMMED HASAN ALMANSORI		
Project	DOUBLE STORY VILAA		
Drg.Title	LIFT ELEVATION		
Area	ARIFAA	Floortype	
Case ID.	2673356	Draw. Type.	ARCH
Sec No.	1	Com. No.	
Block No.		Plot No.	607011962
Bldg. No.	BLD-24-03157	Floor No.	
Date	OCT-2024	Sht. No.	A09
Scale	1/100	Job No.	

G.Manager	Architect	Designed By
ENG AYMEN	ENG IMEN	ENG IMEN

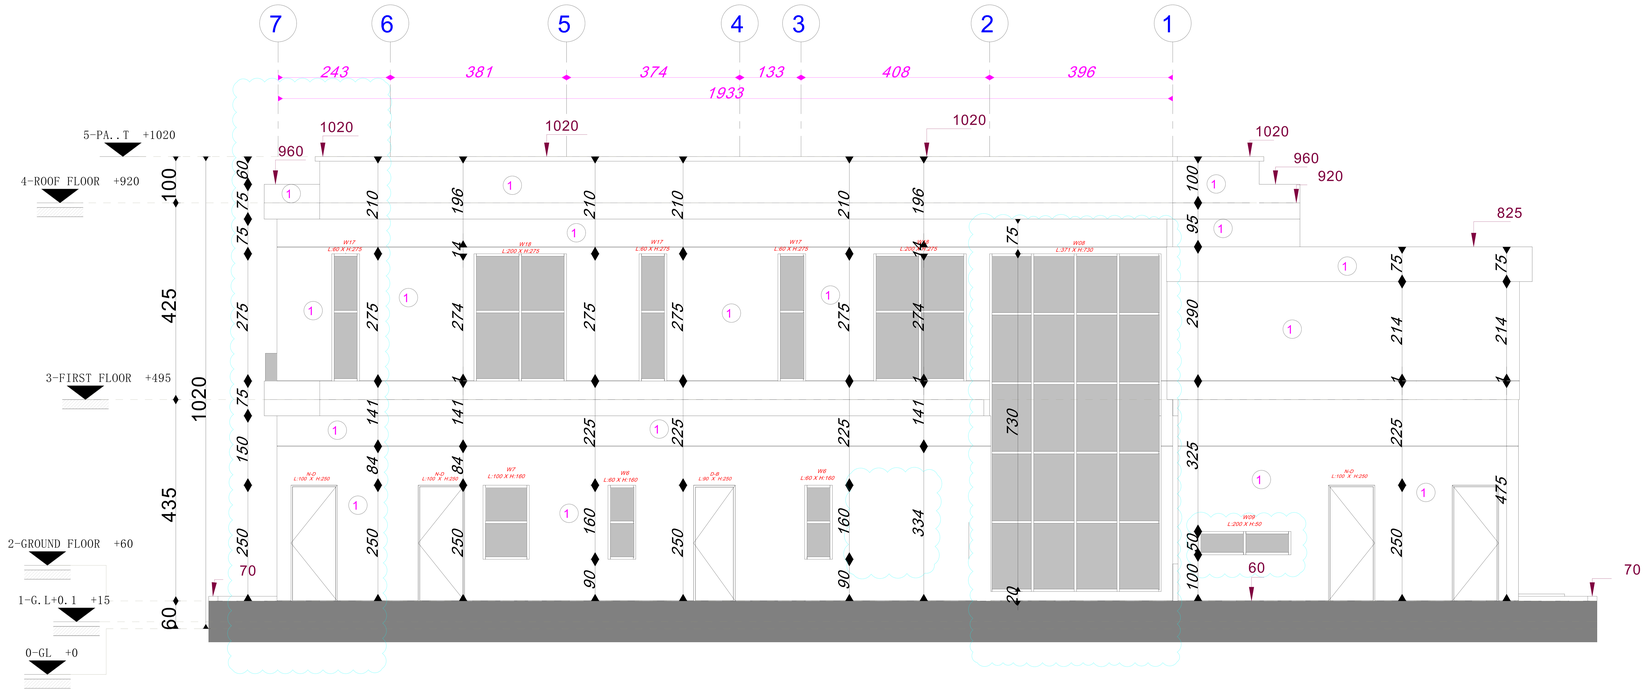

Govvernment Of Ras Al Khaimah
R.A.K. Municipality
Buildings Administration

حكومة رأس الخيمة
دائرة البلدية
إدارة المباني

Approved On — اعتمد في

12 November 2024

Building Permit #: PRMT-24-0005227

Appoved By:

FINSHING	
1	FULL EPOXY PAINT [white]
2	WOOD Aluminum
3	FULL EPOXY BLACK PAINT

Savana
Engineering Consultancy & interior design

Client	SAEED AHMED MOHAMMED HASAN ALMANSORI		
Project	DOUBLE STORY VILAA		
Drg.Title	REAR ELEVATION		
Area	ARIFAA	Floortype	
Case ID.	2673356	Draw. Type.	ARCH
Sec No.	1	Com. No.	
Block No.		Plot No.	607011962
Bldg. No.	BLD-24-03157	Floor No.	
Date	OCT-2024	Sht. No.	A10
Scale	1/100	Job No.	

G.Manager	Architect	Designed By
ENG AYMEN	ENG IMEN	ENG IMEN

REAR ELEVATION

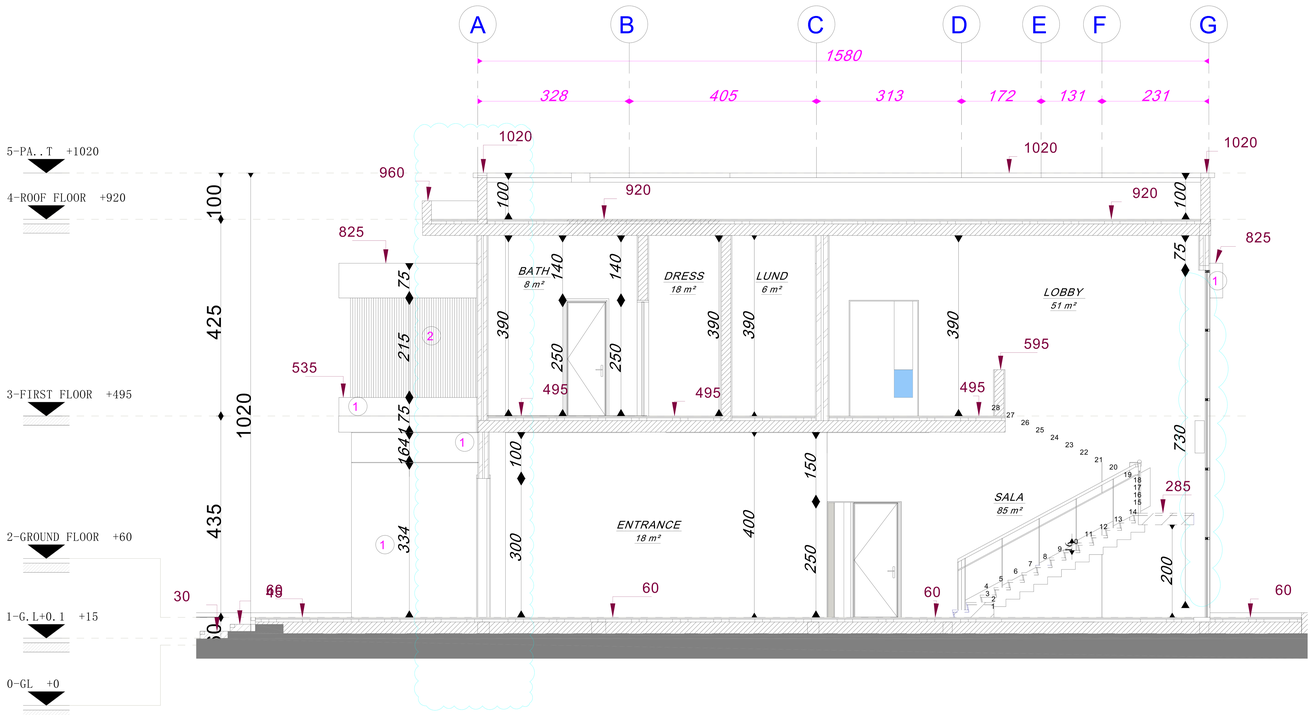

SECTION A-A

ALL GLASS MUST BE DOUBLE UNITES

U-value (w/m2.k)<_ 1.8

SHADING CO- EFFICIENT (SC) <0.3

FINSHING	
1	FULL EPOXY PAINT [white]
2	WOOD Aluminum
3	FULL EPOXY BLACK PAINT
4	

Savana
Engineering Consultancy & interior design

Client	SAEED AHMED MOHAMMED HASAN ALMANSORI		
Project	DOUBLE STORY VILAA		
Drg.Title	SECTION A-A		
Area	ARIFAA	Floortype	
Case ID.	2673356	Draw. Type.	ARCH
Sec No.	1	Com. No.	
Block No.		Plot No.	607011962
Bldg. No.	BLD-24-03157	Floor No.	
Date	OCT-2024	Sht. No.	A11
Scale	1/100	Job No.	

G.Manager	Architect	Designed By
ENG AYMEN	ENG IMEN	ENG IMEN

Govemment Of Ras Al Khaimah
R.A.K. Municipality
Buildings Administration

حكومة رأس الخيمة
دائرة البلدية
إدارة المباني

Approved On / اعتمد في

12 November 2024

Building Permit #: PRMT-24-0005227

Appoved By:

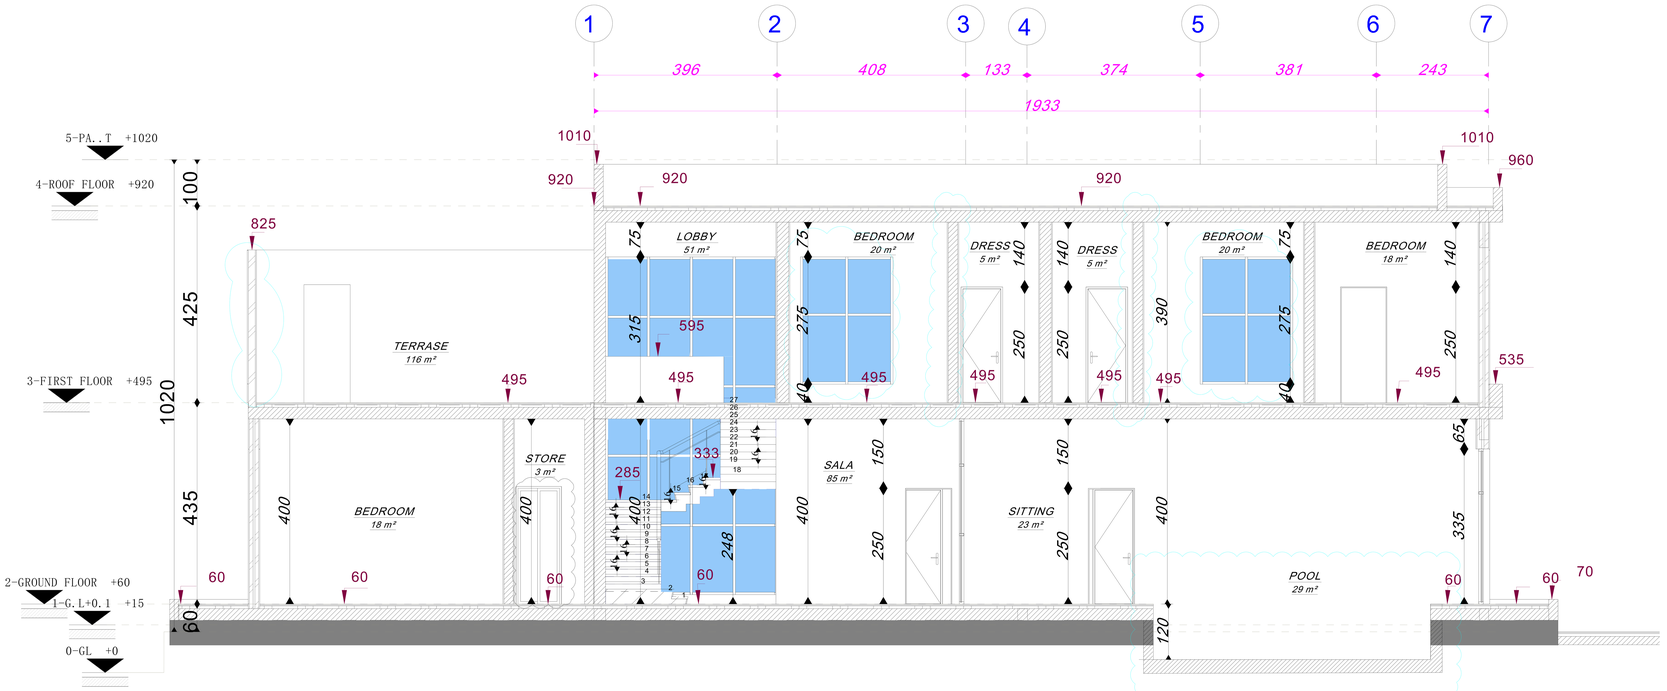

Govvernment Of Ras Al Khaimah
R.A.K. Municipality
Buildings Administration

حكومة رأس الخيمة
دائرة البلدية
إدارة المباني

Approved On — اعتمد في

12 November 2024

Building Permit #: PRMT-24-0005227

Appoved By:

ALL GLASS MUST BE DOUBLE UNITES

GLASS SPECIFICATION:-

U-value (w/m2.k)<_ 1.8

SHADING CO- EFFICIENT (SC) <0.3

FINSHING	
1	FULL EPOXY PAINT [white]
2	WOOD Aluminum
3	FULL EPOXY BLACK PAINT
4	

Savana
Engineering Consultancy & interior design

Client	SAEED AHMED MOHAMMED HASAN ALMANSORI		
Project	DOUBLE STORY VILAA		
Drg.Title	SECTION B-B		
Area	ARIFAA	Floortype	
Case ID.	2673356	Draw. Type.	ARCH
Sec No.	1	Com. No.	
Block No.		Plot No.	607011962
Bldg. No.	BLD-24-03157	Floor No.	
Date	OCT-2024	Sht. No.	A12
Scale	1/100	Job No.	

G.Manager	Architect	Designed By
ENG AYMEN	ENG IMEN	ENG IMEN

SECTION B-B

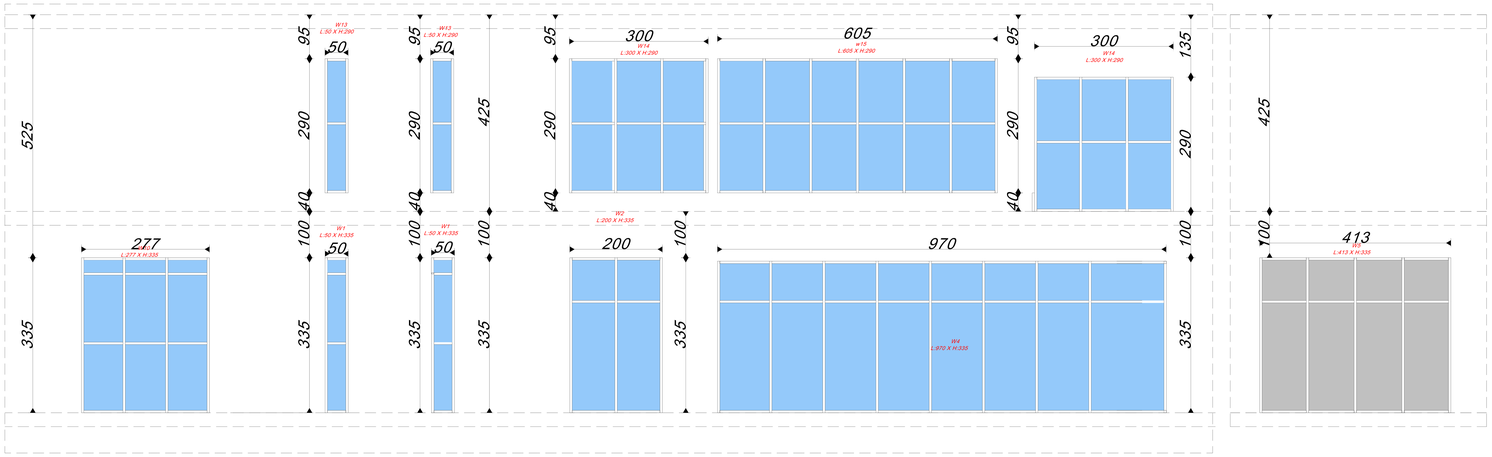

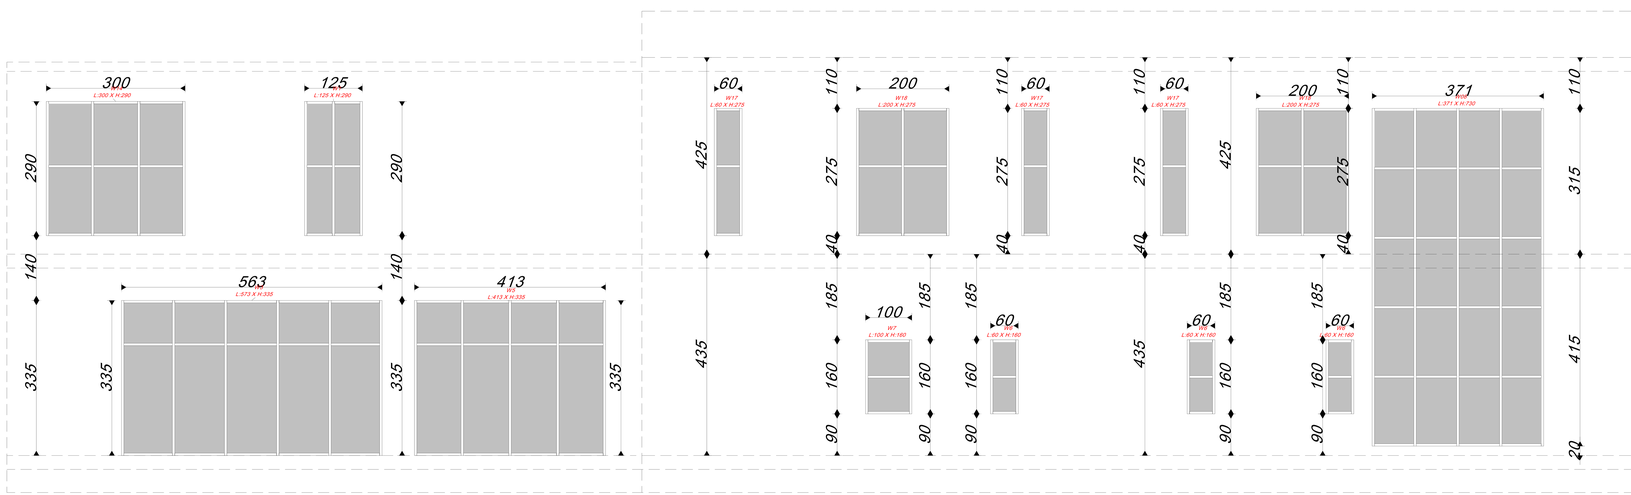

OPENNING DETAILS

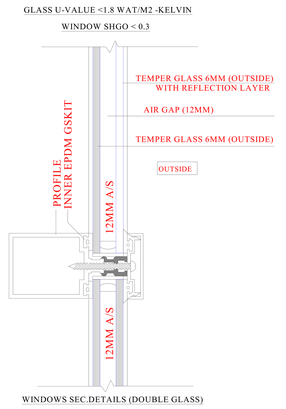

WINDOWS SEC.DETAILS (DOUBLE GLASS)

ALL GLASS MUST BE DOUBLE UNITES

GLASS SPECIFICATION:-

U-value (w/m2.k)<_ 1.8

SHADING CO- EFFICIENT (SC) <0.3

Savana
Engineering Consultancy & interior design

Govemment Of Ras Al Khaimah
R.A.K. Municipality
Buildings Administration

حكومة رأس الخيمة
دائرة البلدية
إدارة المباني

Approved On — اعتمد في

12 November 2024

Building Permit #: PRMT-24-0005227

Appoved By:

Client	SAEED AHMED MOHAMMED HASAN ALMANSORI		
Project	DOUBLE STORY VILAA		
Drg.Title	Opening Details		
Area	ARIFAA	Floortype	
Case ID.	2673356	Draw. Type.	ARCH
Sec No.	1	Com. No.	
Block No.		Plot No.	607011962
Bldg. No.	BLD-24-03157	Floor No.	
Date	OCT-2024	Sht. No.	A13
Scale	1/100	Job No.	

G.Manager	Architect	Designed By
ENG AYMEN	ENG IMEN	ENG IMEN

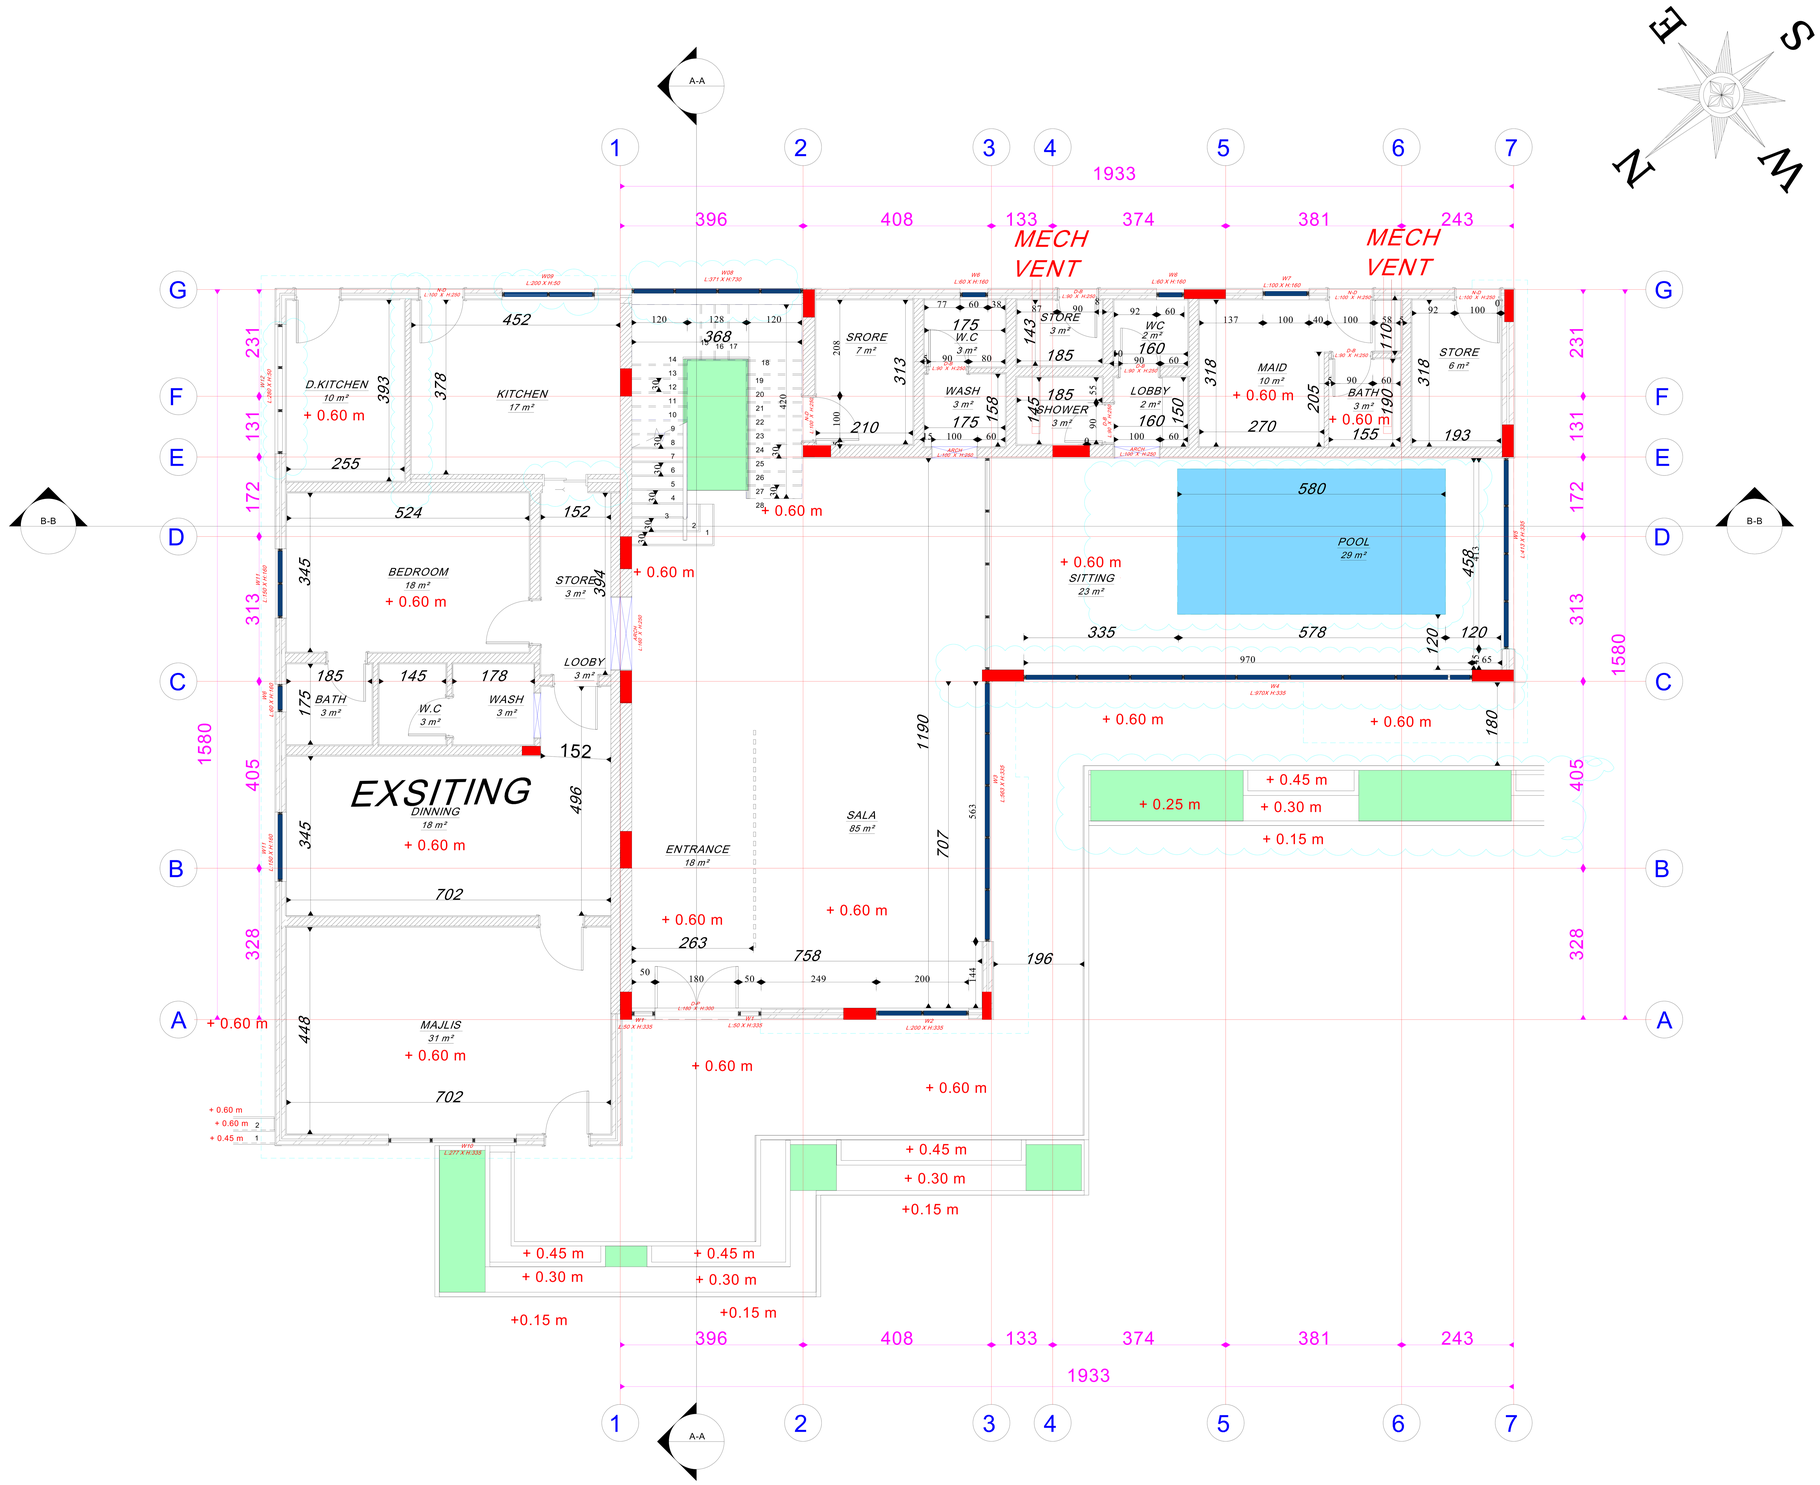

FINISHING FOR VERANDAH		FINISHING FOR DRESSING AREA		FINISHING FOR BATH,WC & WASH	
C3 / W3 / S2 / F3		C1 / W1 / S1 / F1		C2 / W2 / S2 / F2	

FLOORING	F1 Ceramic glazed tiles	
	F2 Ceramic Tiles (Non Slippery)	
	F3 Marble Tiles	
WALLS	W1 Acrylic emulsion paint	
	W2 Ceramic tiles up to ceiling	
	W3 Epoxy paint.	
SKIRTING	S1 Ceramic Tiles. 10cm hight	
	S2 Marble tiles 10cm hight	
CEILING	C1 Acrylic emulsion paint	
	C2 Oil Paint.	
	C3 Epoxy paint.	

Govemment Of Ras Al Khaimah
R.A.K. Municipality
Buildings Administration

حكومة رأس الخيمة
دائرة البلدية
إدارة المباني

Approved On — اعتمد في

21 November 2024

Building Permit #: PRMT-24-0005227

Approved By:

Note :-

* Rcc Lintels Must Be Made On Top Of All Doors , Arches And Windows All Of Them Are At Least 0.20 m Thick.
* All Blocks Adjacent To All Doors , Arches And Windows Must Be A Solid Block .

Rooms	Space	Number
Residential	383.3	
Commercial		
Industrial		
Goverment		
Resident.-Comm.		
Total		

Savana
Engineering Consultancy & interior design

Client	SAEED AHMED MOHAMMED HASAN ALMANSORI		
Project	DOUBLE STORY VILAA		
Drg.Title	GROUND FLOOR PLAN		
Area	ARIFAA	Floortype	G
Case ID.	2673356	Draw. Type.	ARCH
Sec No.	1	Com. No.	
Block No.		Plot No.	607011962
Bldg. No.	BLD-24-03157	Floor No.	01
Date	NOV-2024	Sht. No.	A04
Scale	1/100	Job No.	

G.Manager	Architect	Designed By
ENG AYMEN	ENG IMEN	ENG IMEN

GROUND FLOOR PLAN