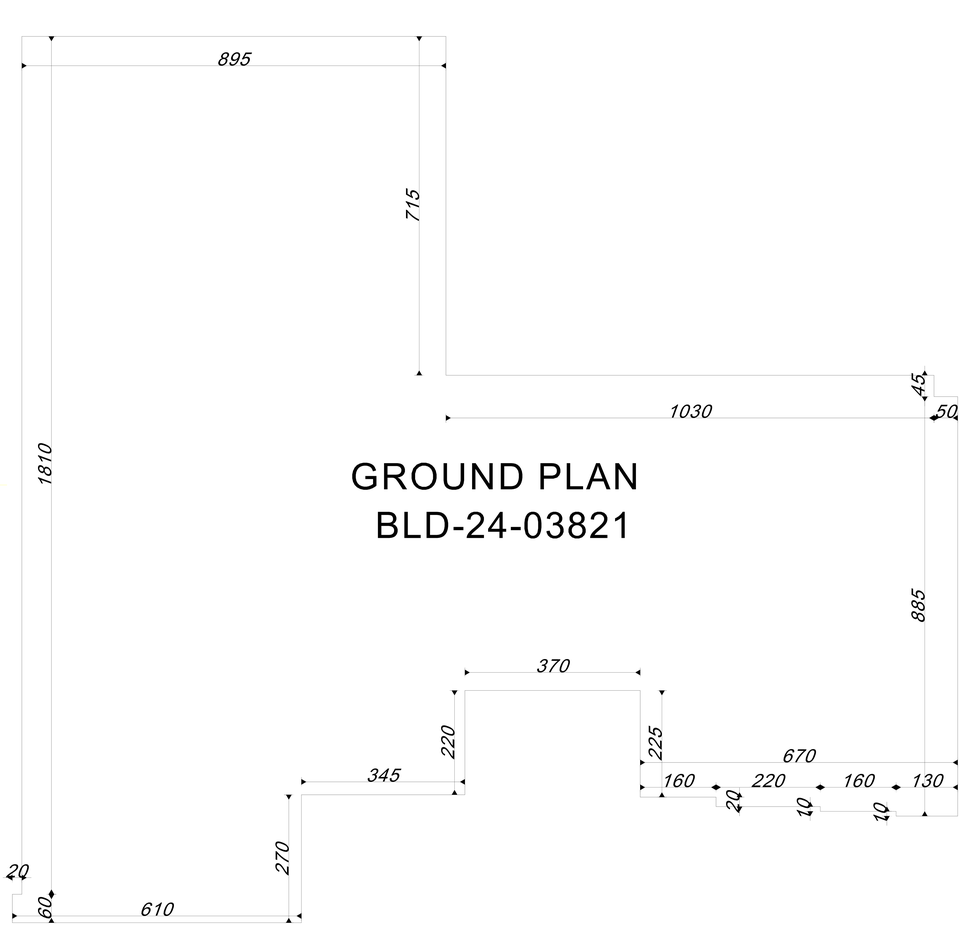

GROUND PLAN

BLD-24-03821

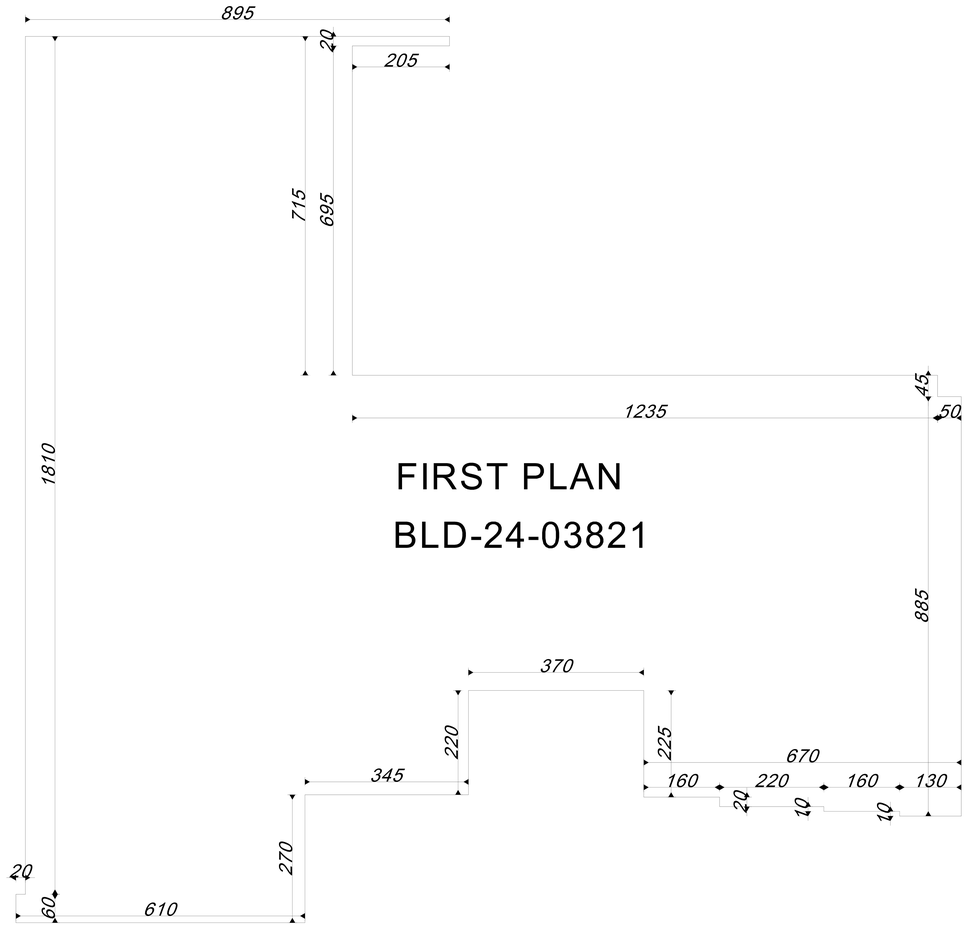

FIRST PLAN

BLD-24-03821

Area Statement

Building Number	BLD-24-03821
Ground Floor Area	248.240
First Floor Area	233.993
Total Building Area	482.233
PLOT AREA ACCORDING TO KRUKI	910m²
BUILD UP RATIO	27.28 %

Client	ISSA LYAS ISSA AL HOUSANI		
Project	Proposed Double Storey Villa		
Drg.Title	AreaStatement		
Area	AWAFI	Floortype	
Case ID.	2578043	Draw. Type.	ARCH
Sec No.	1	Com. No.	
Block No.		Plot No.	406131666
Bldg. No.	BLD-24-03821	Floor No.	
Date	JULY 2024	Sht. No.	A-01
Scale	1/100	Job No.	

G.Manager	Architect	Designed By
ENG AYMEN	ENG IMEN	ENG IMEN

AREA STATMENTENT

Govemment Of Ras Al Khaimah
R.A.K. Municipality
Buildings Administration

حكومة رأس الخيمة
دائرة البلدية
إدارة المباني

Approved On — اعتمد في

29 July 2024

Building Permit #: PRMT-24-0004328

Appoved By:

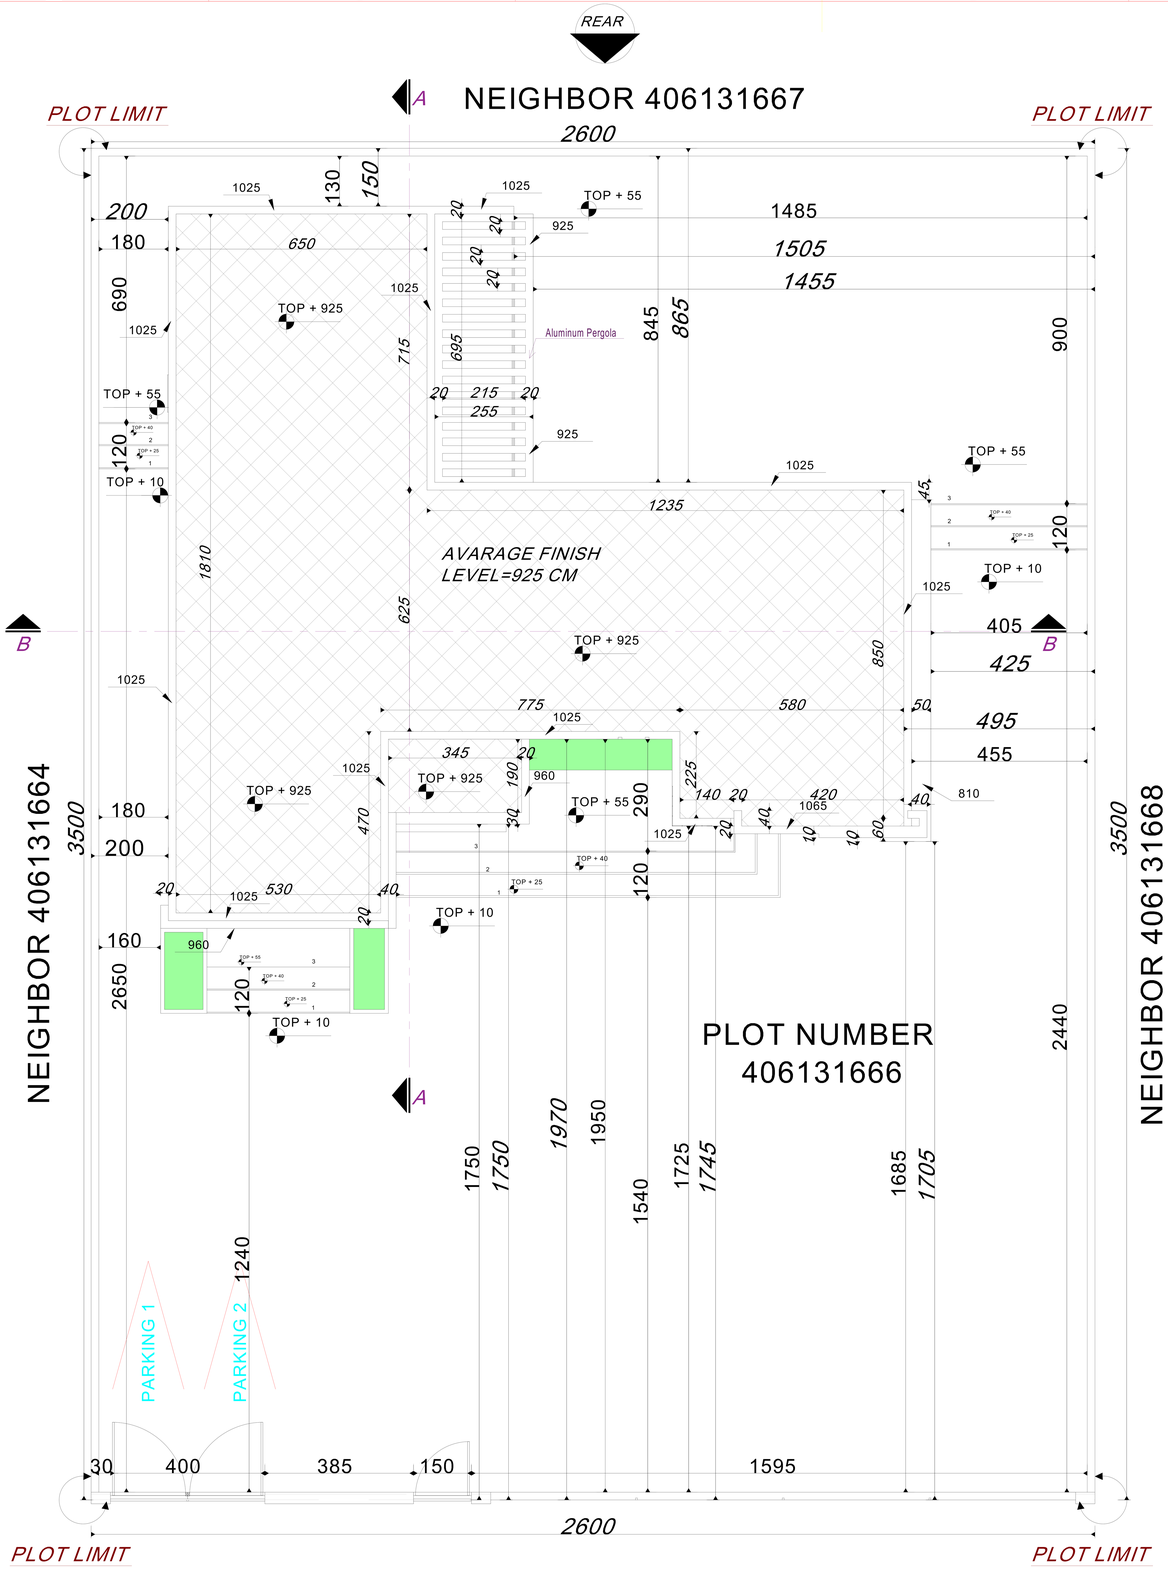

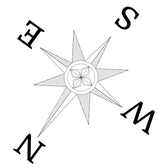

Govvernment Of Ras Al Khaimah
R.A.K. Municipality
Buildings Administration

حكومة رأس الخيمة
دائرة البلدية
إدارة المباني

Approved On — اعتمد في

30 July 2024

Building Permit #: PRMT-24-0004328

Appoved By:

Note :-

* Rcc Lintels Must Be Made On Top Of All Doors , Arches And Windows All Of Them Are At Least 0.20 m Thick.
* All Blocks Adjacent To All Doors , Arches And Windows Must Be A Solid Block .

Savana
Engineering Consultancy & interior design

Client	ISSA LYAS ISSA AL HOUSANI		
Project	Proposed Double Storey Villa		
Drg.Title	Site Development Layout Plan		
Area	AWAFI	Floortype	
Case ID.	2578043	Draw. Type.	ARCH
Sec No.	1	Com. No.	
Block No.		Plot No.	406131666
Bldg. No.	BLD-24-03821	Floor No.	
Date	JULY 2024	Sht. No.	A02
Scale	1/100	Job No.	

G.Manager	Architect	Designed By
ENG AYMEN	ENG IMEN	ENG IMEN

SITE DEVELOPMENT LAYOUT PLAN

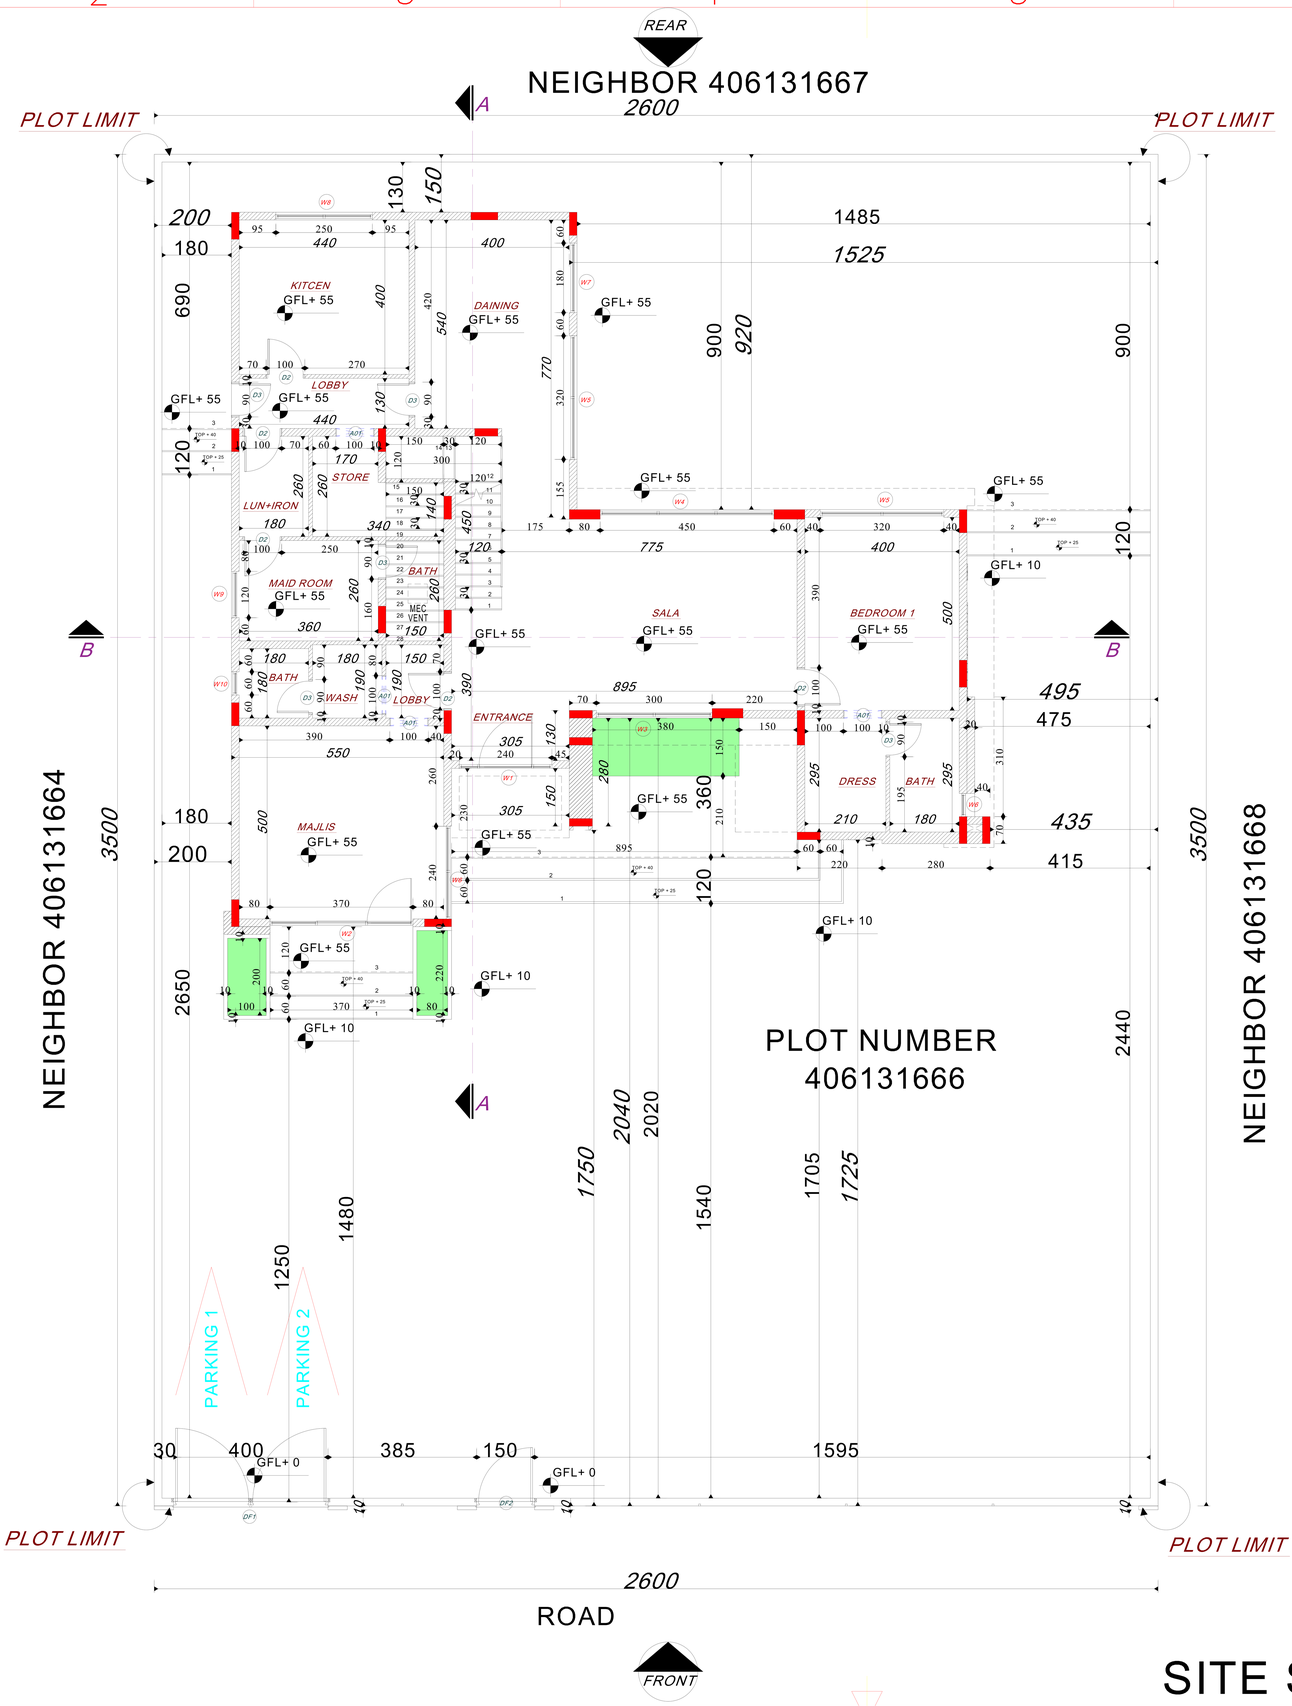

Govement Of Ras Al Khaimah
R.A.K. Municipality
Buildings Administration

حكومة رأس الخيمة
دائرة البلدية
إدارة المباني

Approved On — اعتمد في

30 July 2024

Building Permit #: PRMT-24-0004328

Appoved By:

Savana
Engineering Consultancy & interior design

Client	ISSA LYAS ISSA AL HOUSANI		
Project	Proposed Double Storey Villa		
Drg.Title	SITE SETTING PLAN		
Area	AWAFI	Floortype	
Case ID.	2578043	Draw. Type.	ARCH
Sec No.	1	Com. No.	
Block No.		Plot No.	406131666
Bldg. No.	BLD-24-03821	Floor No.	
Date	JULY 2024	Sht. No.	A03
Scale	1/100	Job No.	

G.Manager	Architect	Designed By
ENG AYMEN	ENG IMEN	ENG IMEN

SITE SETTING PLAN

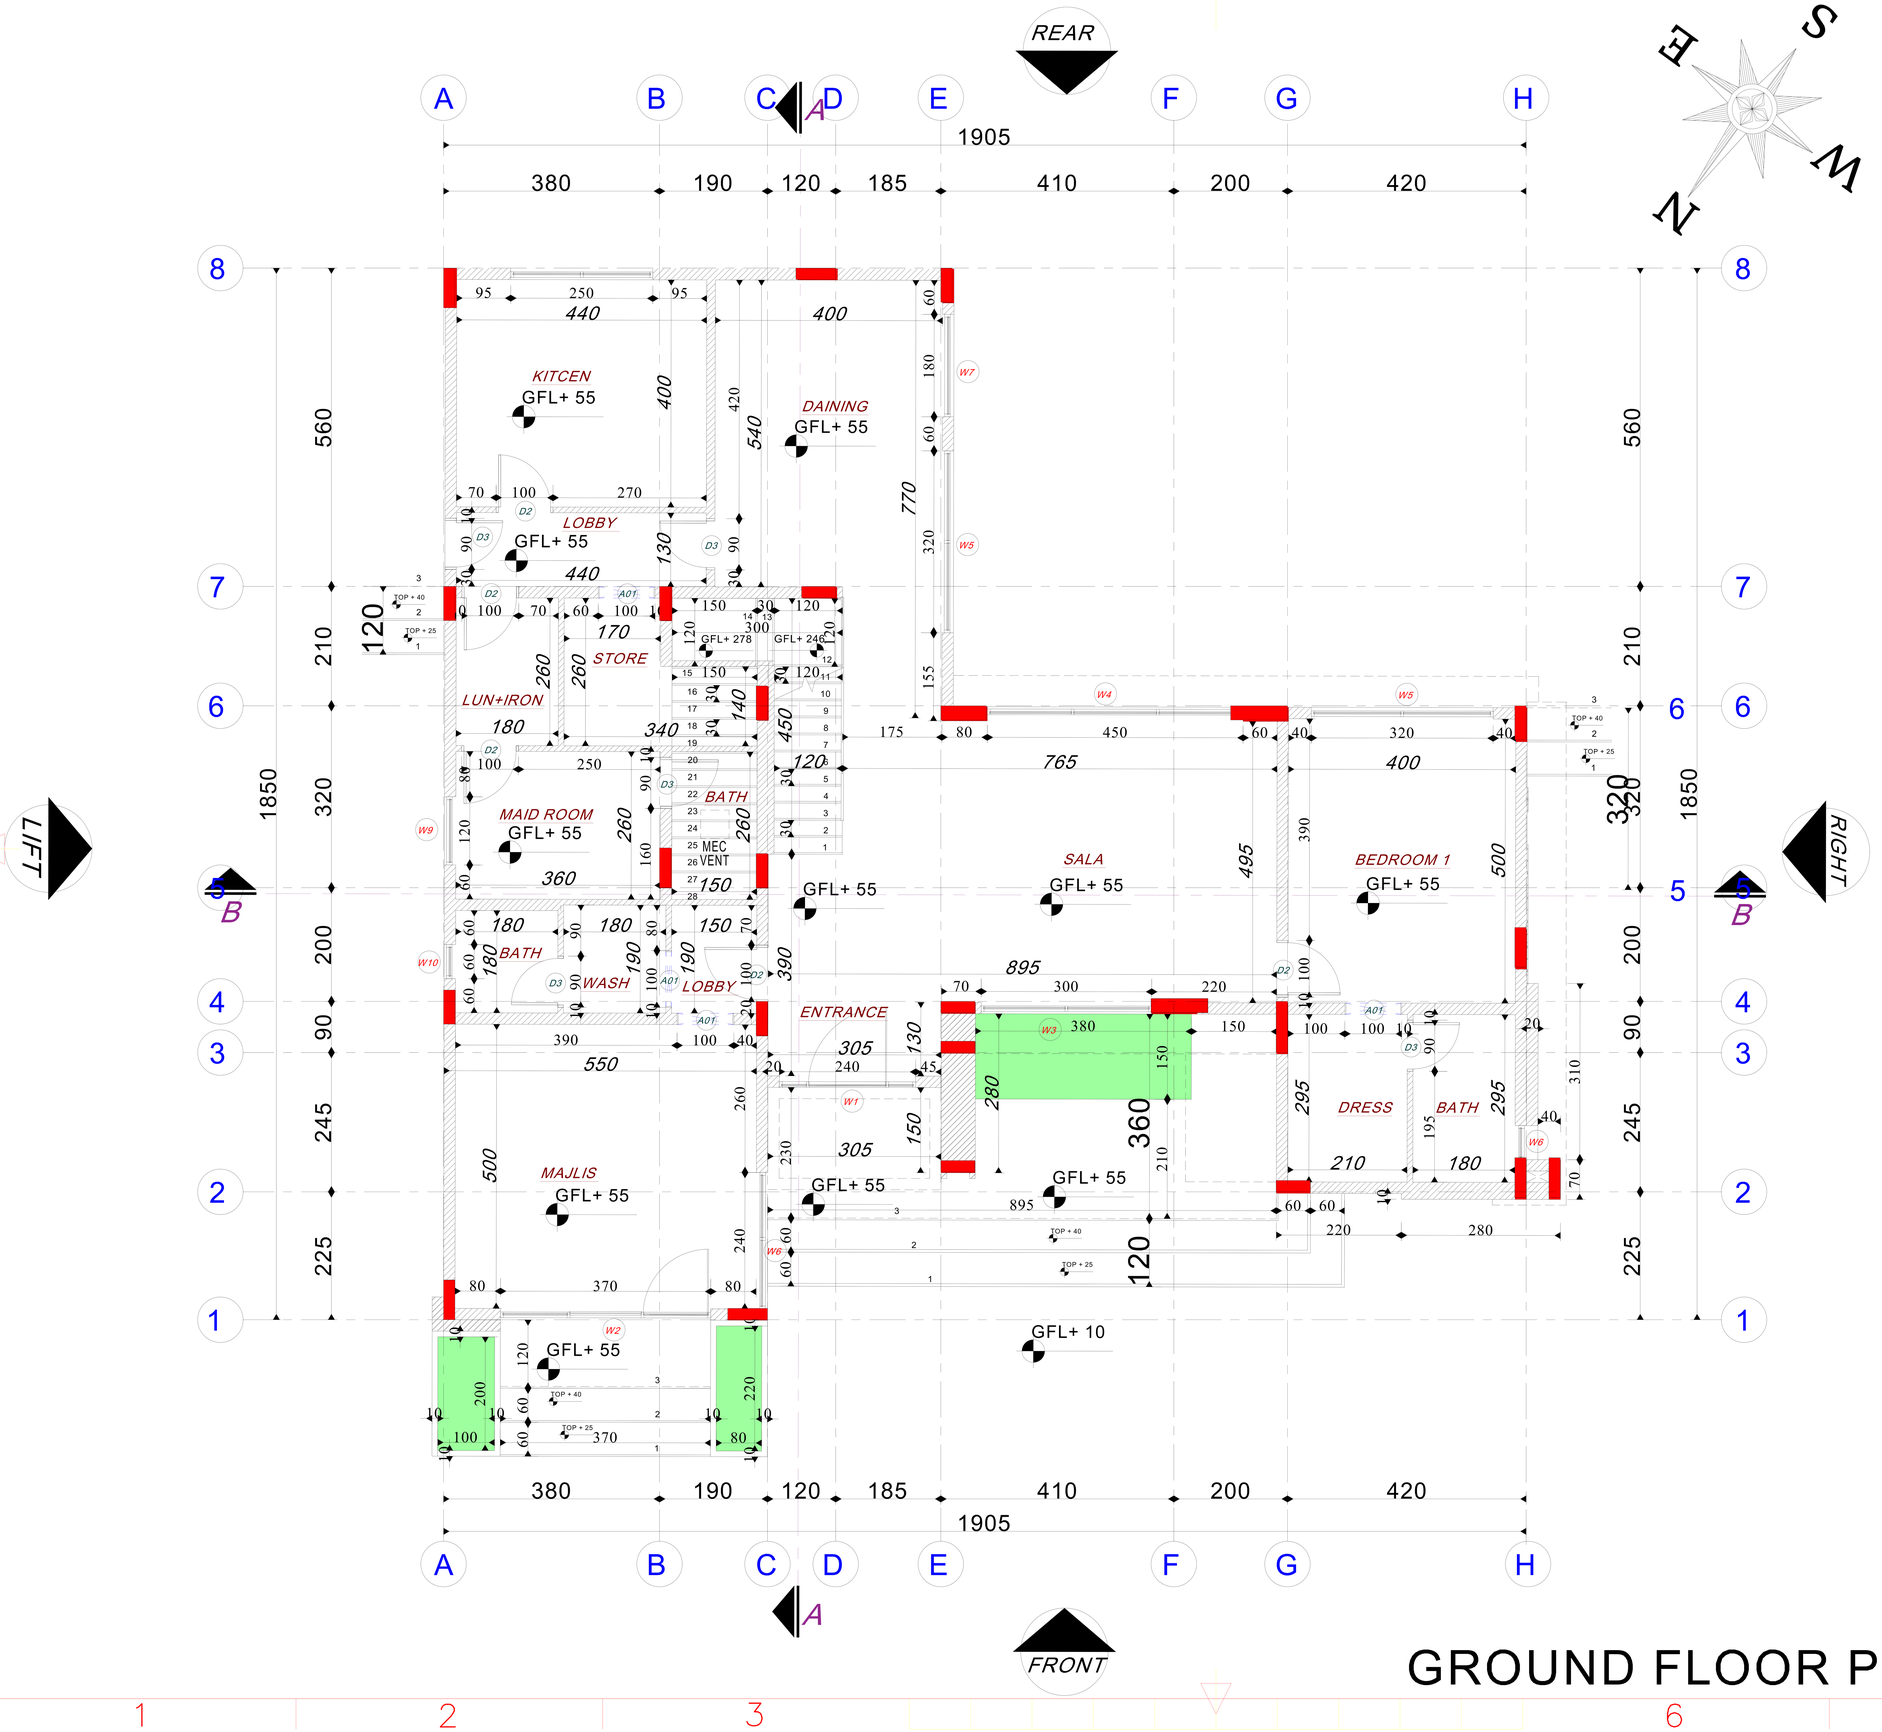

FINISHING FOR VERANDAH	FINISHING FOR DRESSING AREA	FINISHING FOR BATH,WC & WASH
FLOORING	F3 Marble Tiles	F2 Ceramic Tiles (Non Slippery)	F1 Ceramic glazed tiles
WALLS	W3 Epoxy paint.	W2 Ceramic tiles up to ceiling	W1 Acrylic emulsion paint
SKIRTING		S2 Marble tiles 10cm hight	S1 Ceramic Tiles. 10cm hight
CEILING	C3 Epoxy paint.	C2 Oil Paint.	C1 Acrylic emulsion paint

Govement Of Ras Al Khaimah
R.A.K. Municipality
Buildings Administration

حكومة رأس الخيمة
دائـرة البلـدية
إدارة المباني

Approved On — اعتمد في

28 August 2024

Building Permit #: PRMT-24-0004328

Appoved By:

Note :-

* Rcc Lintels Must Be Made On Top Of All Doors , Arches And Windows All Of Them Are At Least 0.20 m Thick.
* All Blocks Adjacent To All Doors , Arches And Windows Must Be A Solid Block .

Rooms	Space	Number
Residential	248.240	
Commercial		
Industrial		
Goverment		
Resident.-Comm.		
Total		

Savana
Engineering Consultancy & interior design

Client	ISSA LYAS ISSA AL HOUSANI		
Project	Proposed Double Storey Villa		
Drg.Title	GROUND FLOOR PLAN		
Area	AWAFI	Floortype	G
Case ID.	2578043	Draw. Type.	ARCH
Sec No.	1	Com. No.	
Block No.		Plot No.	406131666
Bldg. No.	BLD-24-03821	Floor No.	01
Date	JULY 2024	Sht. No.	A04
Scale	1/100	Job No.	

G.Manager	Architect	Designed By
ENG AYMEN	ENG IMEN	ENG IMEN

GROUND FLOOR PLAN

REAR

LIFT

RIGHT

FRONT

A

B

M. BED ROOM
FFL+ 500

BALCON
FFL+ 500

Aluminum Pergola

DRESS

BATH

SALA
FFL+ 500

BED ROOM 2
FFL+ 500

DRESS

BATH

BATH
FFL+ 500

BED ROOM 3
FFL+ 500

PANTRY

LOBBY
FFL+ 500

BED ROOM 4
FFL+ 500

Aluminum Pergola

1905

380 190 120 185 430 160 440

1850

560 210 320

1850

200 90 245 225

Government Of Ras Al Khaimah
R.A.K. Municipality
Buildings Administration

حكومة رأس الخيمة
دائرة البلدية
إدارة المباني

Approved On
اعتمد في

29 July 2024

Building Permit #:
PRMT-24-0004328

Approved By:

Note :-

* Rcc Lintels Must Be Made On Top Of All Doors , Arches And Windows All Of Them Are At Least 0.20 m Thick.
* All Blocks Adjacent To All Doors , Arches And Windows Must Be A Solid Block .

Rooms	Space	Number
Residential	233.993	
Commercial		
Industrial		
Goverment		
Resident.-Comm.		
Total		

Savana
Engineering Consultancy & Interior Design

Client	ISSA LYAS ISSA AL HOUSANI		
Project	Proposed Double Storey Villa		
Drg.Title	FIRST FLOOR PLAN		
Area	AWAFI	Floortype	F
Case ID.	2578043	Draw. Type.	ARCH
Sec No.	1	Com. No.	
Block No.		Plot No.	406131666
Bldg. No.	BLD-24-03821	Floor No.	01
Date	JULY 2024	Sht. No.	A05
Scale	1/100	Job No.	

G.Manager	Architect	Designed By
ENG AYMEN	ENG IMEN	ENG IMEN

FIRST FLOOR PLAN

REAR

LIFT

RIGHT

FRONT

A

B

M. BED ROOM
FFL+ 500

BALCON
FFL+ 500

Aluminum Pergola

DRESS

BATH

SALA
FFL+ 500

BED ROOM 2
FFL+ 500

DRESS

BATH

BATH
FFL+ 500

BED ROOM 3
FFL+ 500

PANTRY

LOBBY
FFL+ 500

BED ROOM 4
FFL+ 500

Aluminum Pergola

1905

380 190 120 185 430 160 440

1850

560 210 320

1850

200 90 245 225

Government Of Ras Al Khaimah
R.A.K. Municipality
Buildings Administration

حكومة رأس الخيمة
دائرة البلدية
إدارة المباني

Approved On
اعتمد في

29 July 2024

Building Permit #:
PRMT-24-0004328

Approved By:

Note :-

* Rcc Lintels Must Be Made On Top Of All Doors , Arches And Windows All Of Them Are At Least 0.20 m Thick.
* All Blocks Adjacent To All Doors , Arches And Windows Must Be A Solid Block .

Rooms	Space	Number
Residential	233.993	
Commercial		
Industrial		
Goverment		
Resident.-Comm.		
Total		

Savana
Engineering Consultancy & Interior Design

Client	ISSA LYAS ISSA AL HOUSANI		
Project	Proposed Double Storey Villa		
Drg.Title	FIRST FLOOR PLAN		
Area	AWAFI	Floortype	F
Case ID.	2578043	Draw. Type.	ARCH
Sec No.	1	Com. No.	
Block No.		Plot No.	406131666
Bldg. No.	BLD-24-03821	Floor No.	01
Date	JULY 2024	Sht. No.	A05
Scale	1/100	Job No.	

G.Manager	Architect	Designed By
ENG AYMEN	ENG IMEN	ENG IMEN

FIRST FLOOR PLAN

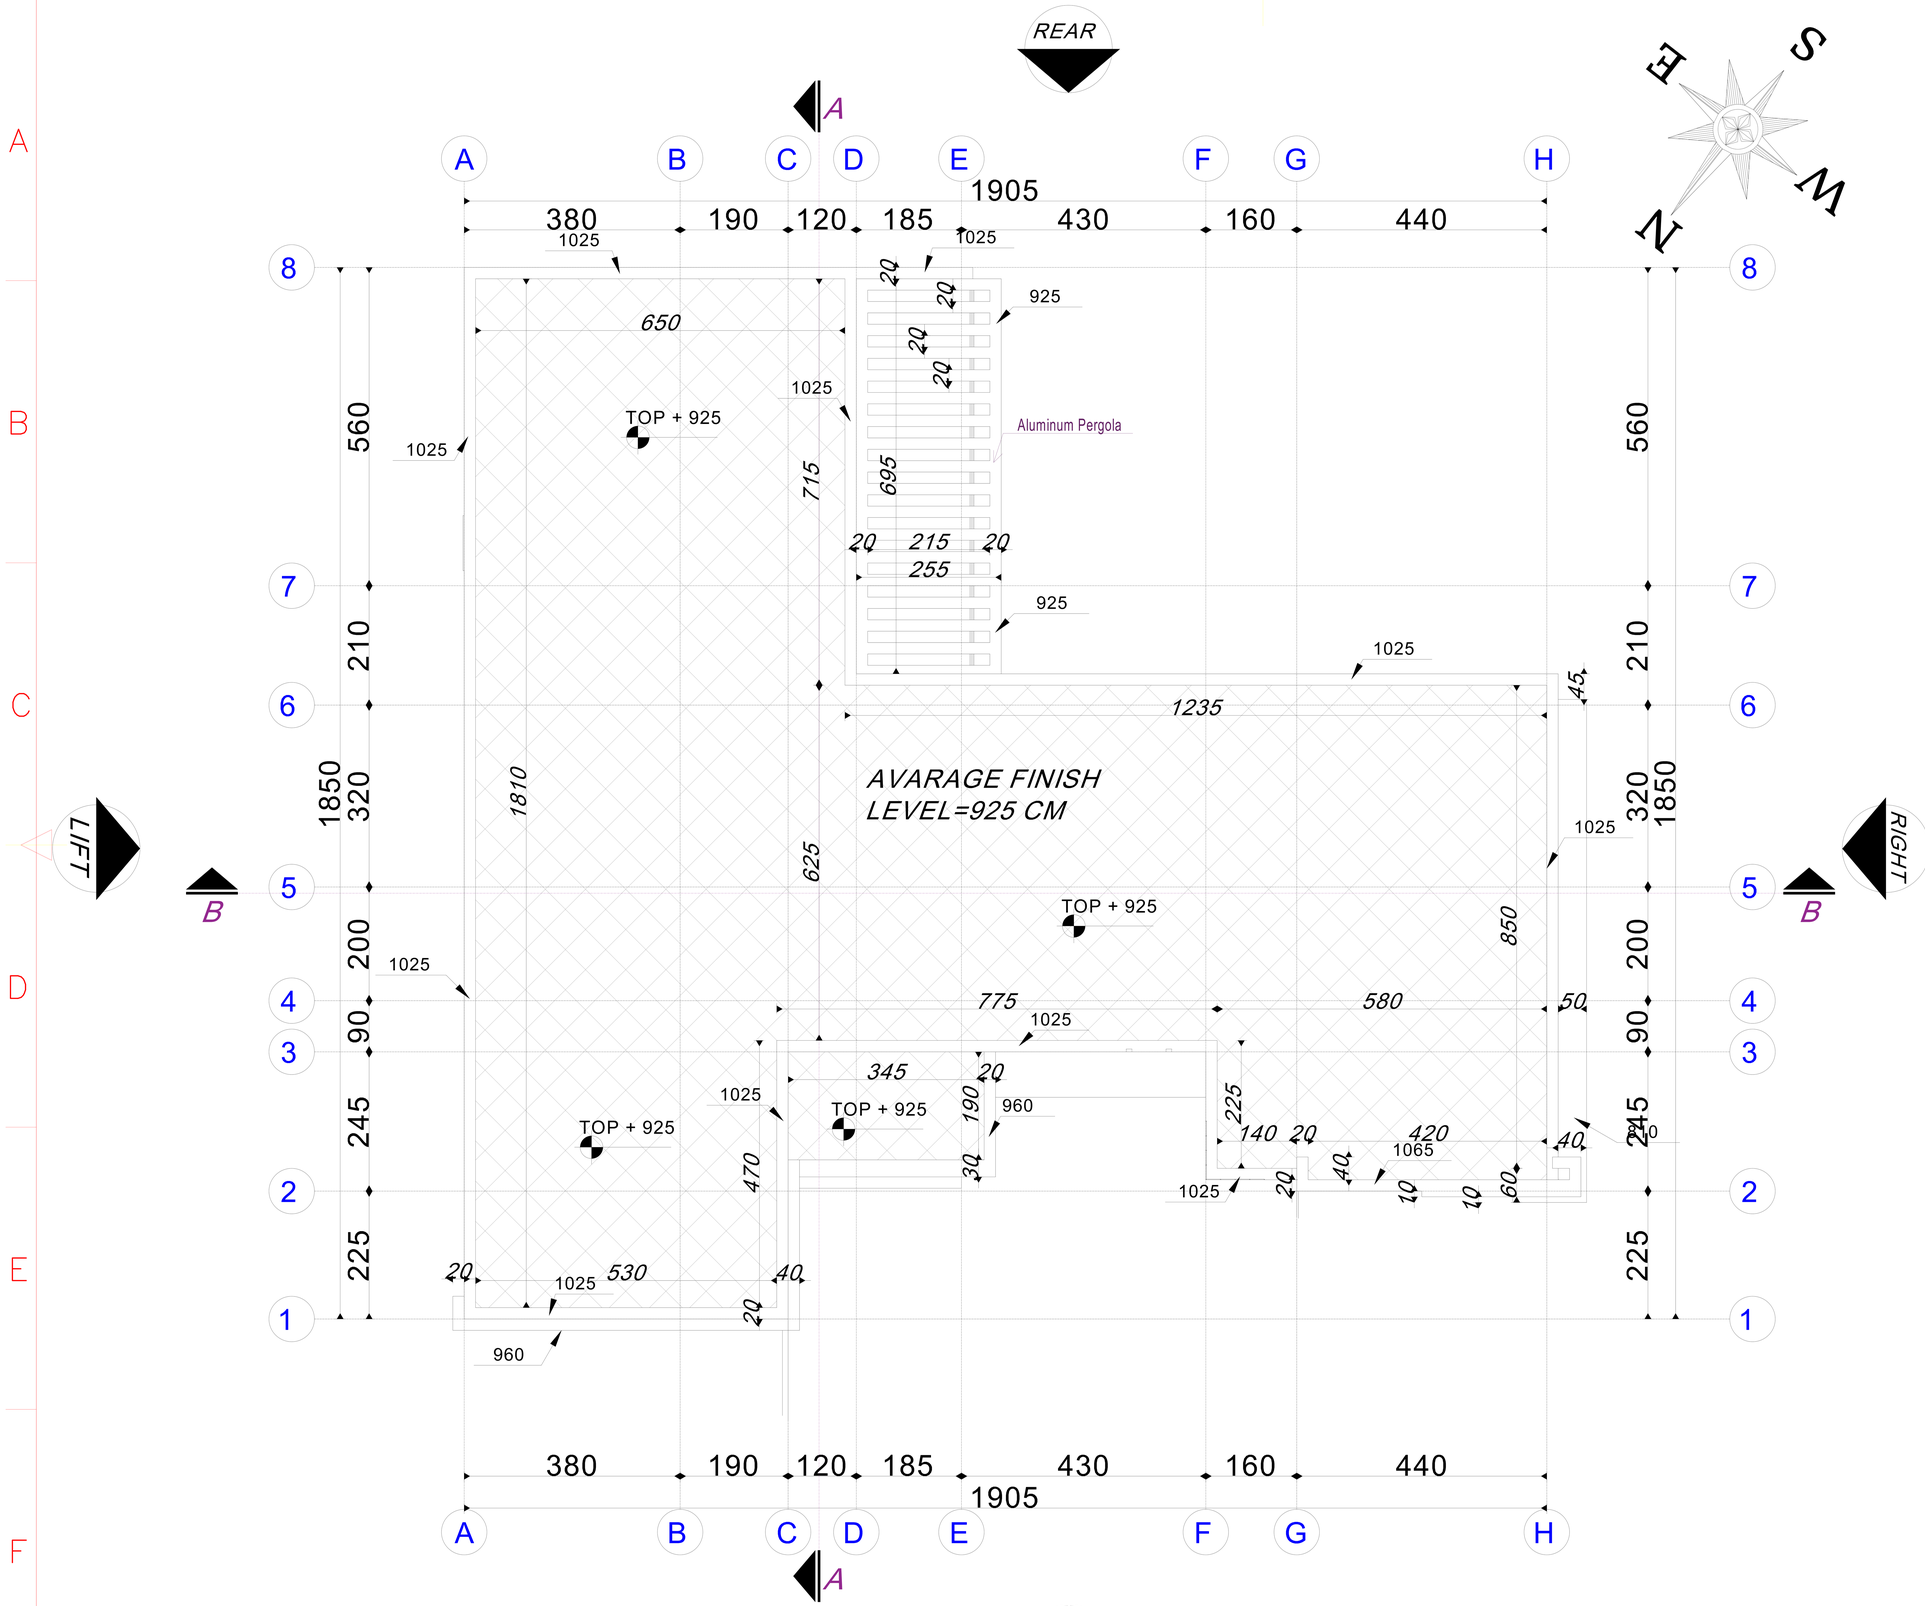

Govvernment Of Ras Al Khaimah
R.A.K. Municipality
Buildings Administration

حكومة رأس الخيمة
دائرة البلدية
إدارة المباني

Approved On — اعتمد في

30 July 2024

Building Permit #: PRMT-24-0004328

Approved By:

FINISHING FOR VERANDAH	FINISHING FOR DRESSING AREA	FINISHING FOR BATH,WC & WASH	
F3 Marble Tiles	F2 Ceramic Tiles (Non Slippery)	F1 Ceramic glazed tiles	FLOORING
W3 Epoxy paint.	W2 Ceramic tiles up to ceiling	W1 Acrylic emulsion paint	WALLS
	S2 Marble tiles 10cm hight	S1 Ceramic Tiles. 10cm hight	SKIRTING
C3 Epoxy paint.	C2 Oil Paint.	C1 Acrylic emulsion paint	CEILING

Savana
Engineering Consultancy & interior design

Client	ISSA LYAS ISSA AL HOUSANI		
Project	Proposed Double Storey Villa		
Drg.Title	TOP ROOF PLAN		
Area	AWAFI	Floortype	
Case ID.	2578043	Draw. Type.	ARCH
Sec No.	1	Com. No.	
Block No.		Plot No.	406131666
Bldg. No.	BLD-24-03821	Floor No.	
Date	JULY 2024	Sht. No.	A06A
Scale	1/100	Job No.	

G.Manager	Architect	Designed By
ENG AYMEN	ENG IMEN	ENG IMEN

TOP ROOF FLOOR PLAN

Govemment Of Ras Al Khaimah
R.A.K. Municipality
Buildings Administration

حكومة رأس الخيمة
دائرة البلدية
إدارة المباني

Approved On — اعتمد في

30 July 2024

Building Permit #: PRMT-24-0004328

Appoved By:

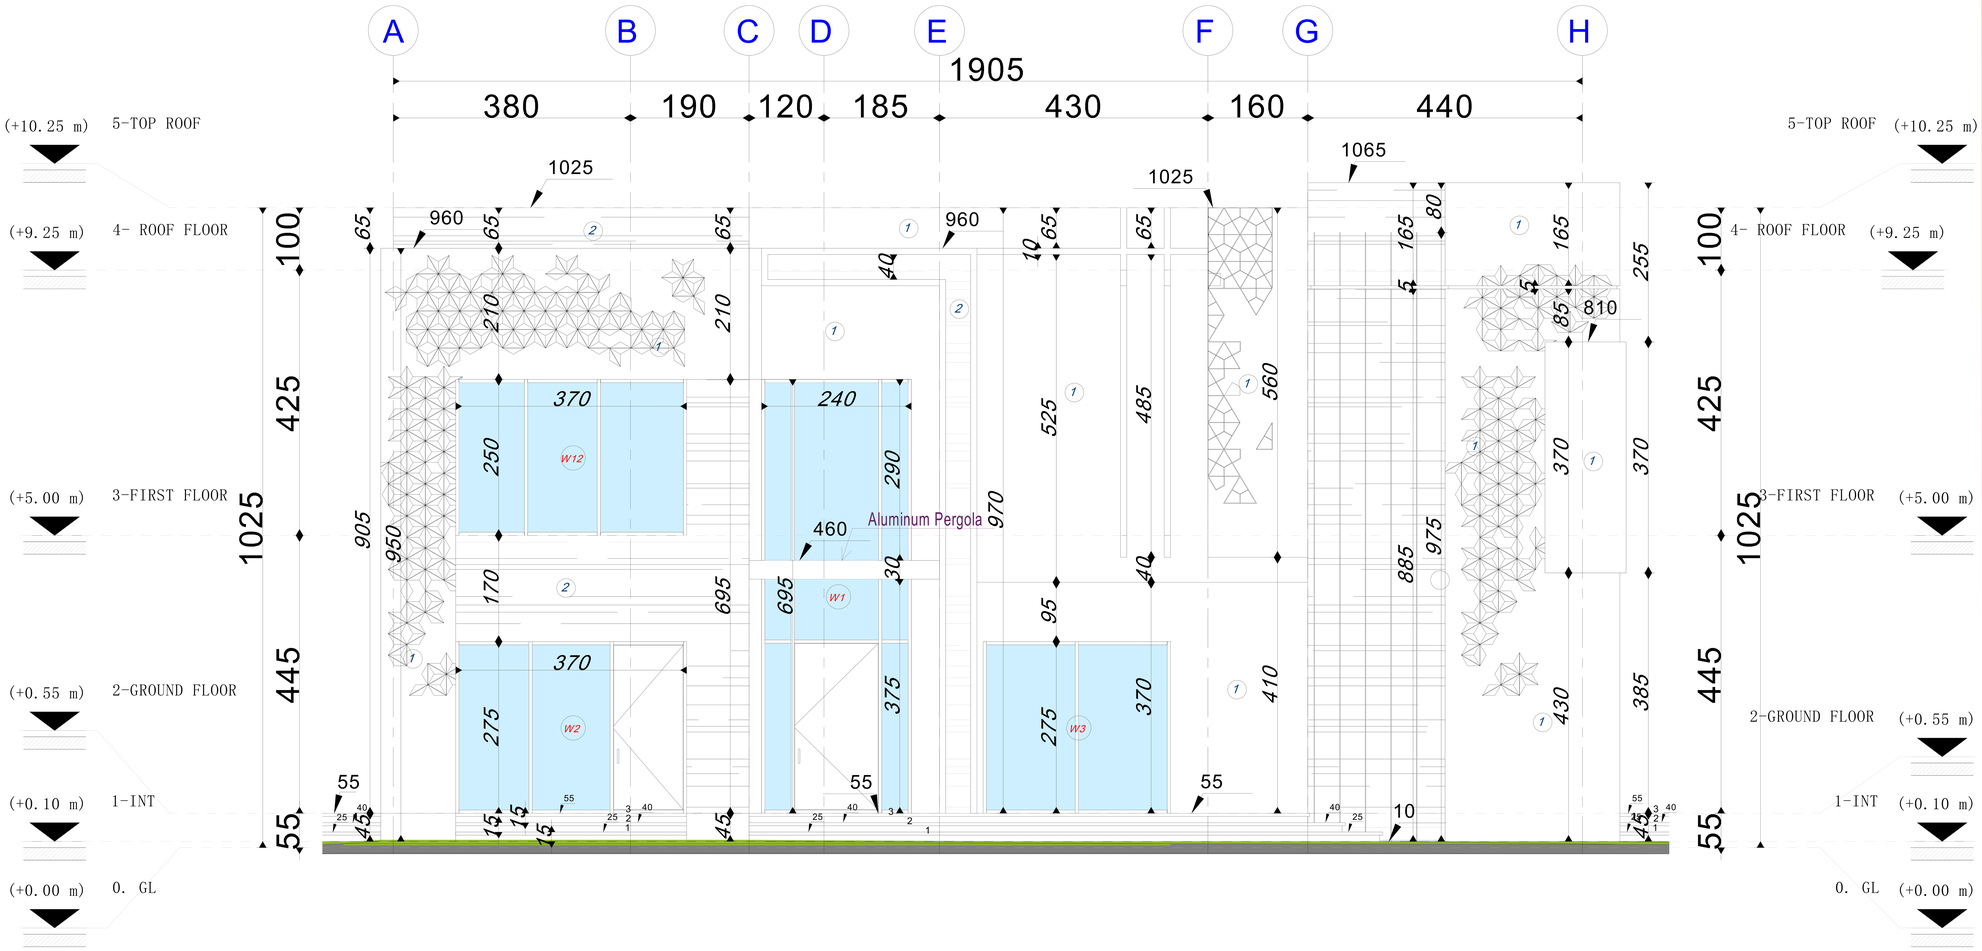

FINSHING	
1	FULL EPOXY PAINT [white]
2	TRAVERTINE STONE
3	
4	

Savana
Engineering Consultancy & interior design

Client	ISSA LYAS ISSA AL HOUSANI		
Project	Proposed Double Storey Villa		
Drg.Title	FRONT ELEVATION		
Area	AWAFI	Floortype	
Case ID.	2578043	Draw. Type.	ARCH
Sec No.	1	Com. No.	
Block No.		Plot No.	406131666
Bldg. No.	BLD-24-03821	Floor No.	
Date	JULY 2024	Sht. No.	A07
Scale	1/100	Job No.	

G.Manager	Architect	Designed By
ENG AYMEN	ENG IMEN	ENG IMEN

FRONT ELEVATION

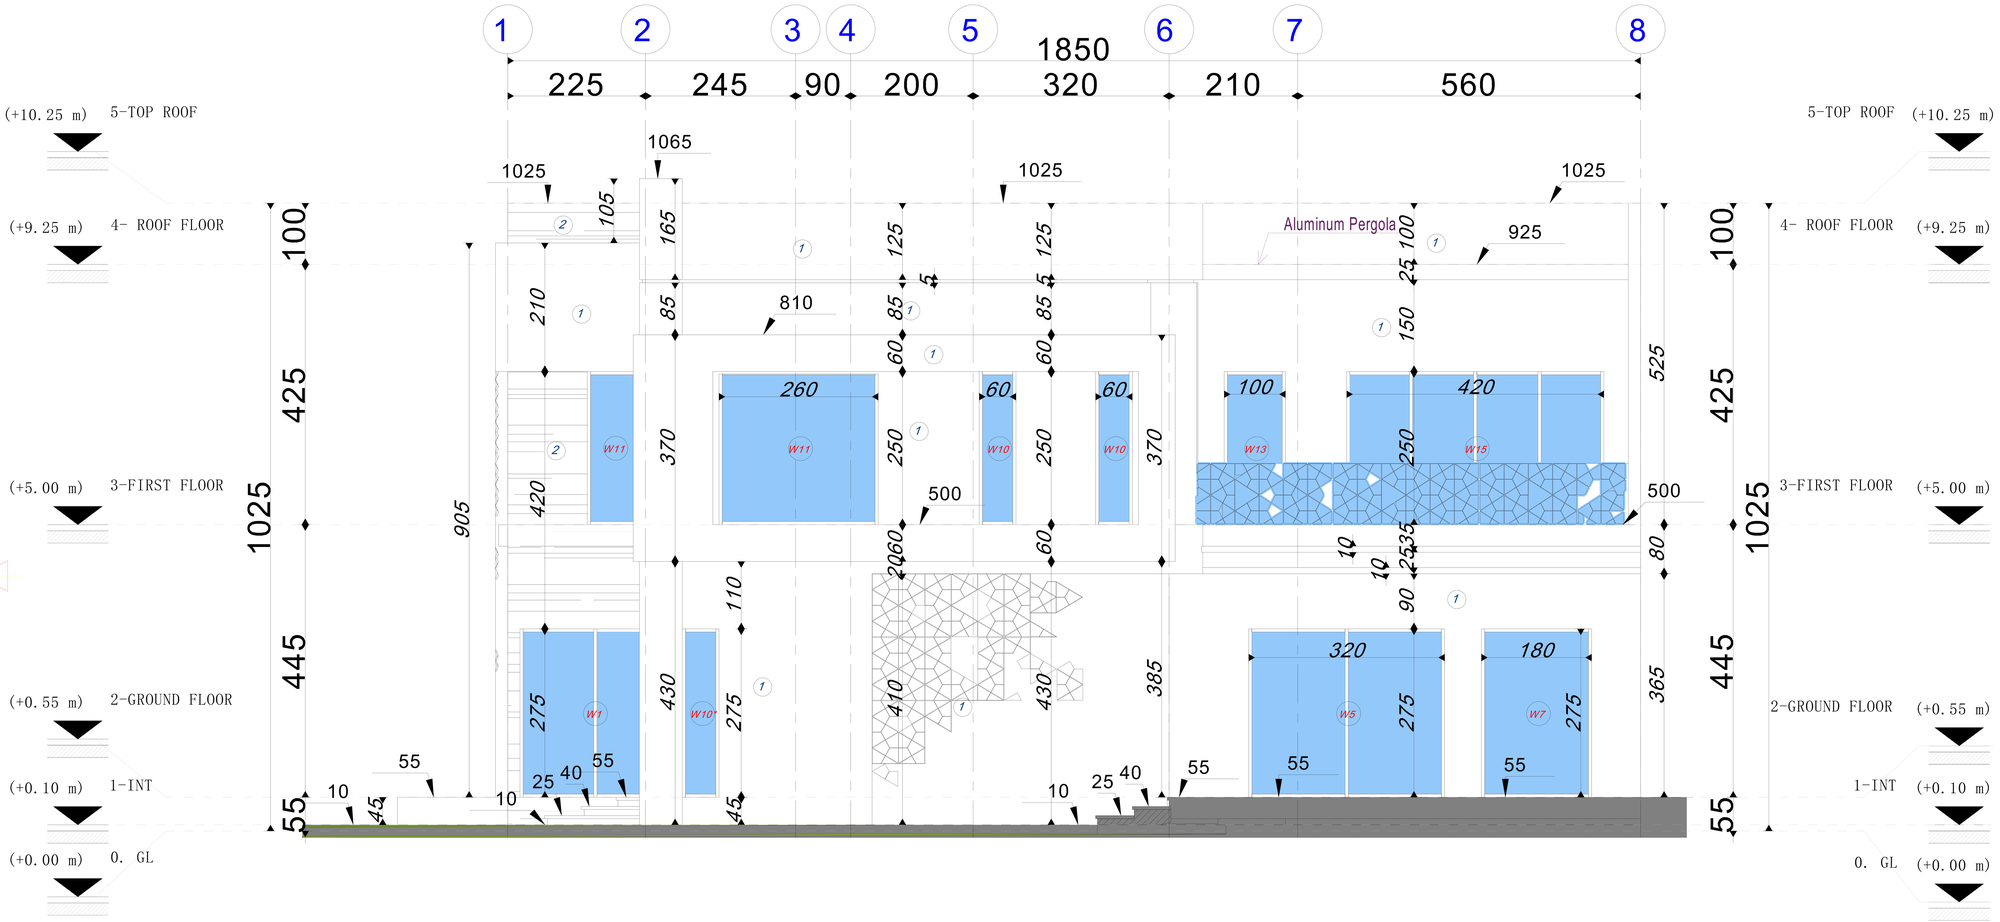

Govvernment Of Ras Al Khaimah
R.A.K. Municipality
Buildings Administration

حكومة رأس الخيمة
دائرة البلدية
إدارة المباني

Approved On / اعتمد في

30 July 2024

Building Permit #: PRMT-24-0004328

Appoved By:

FINSHING	
1	FULL EPOXY PAINT [white]
2	TRAVERTINE STONE
3	
4	

Savana
Engineering Consultancy & Interior design

Client	ISSA LYAS ISSA AL HOUSANI		
Project	Proposed Double Storey Villa		
Drg.Title	RIGHT ELEVATION		
Area	AWAFI	Floortype	
Case ID.	2578043	Draw. Type.	ARCH
Sec No.	1	Com. No.	
Block No.		Plot No.	406131666
Bldg. No.	BLD-24-03821	Floor No.	
Date	JULY 2024	Sht. No.	A08
Scale	1/100	Job No.	

G.Manager	Architect	Designed By
ENG AYMEN	ENG IMEN	ENG IMEN

RIGHT ELEVATION

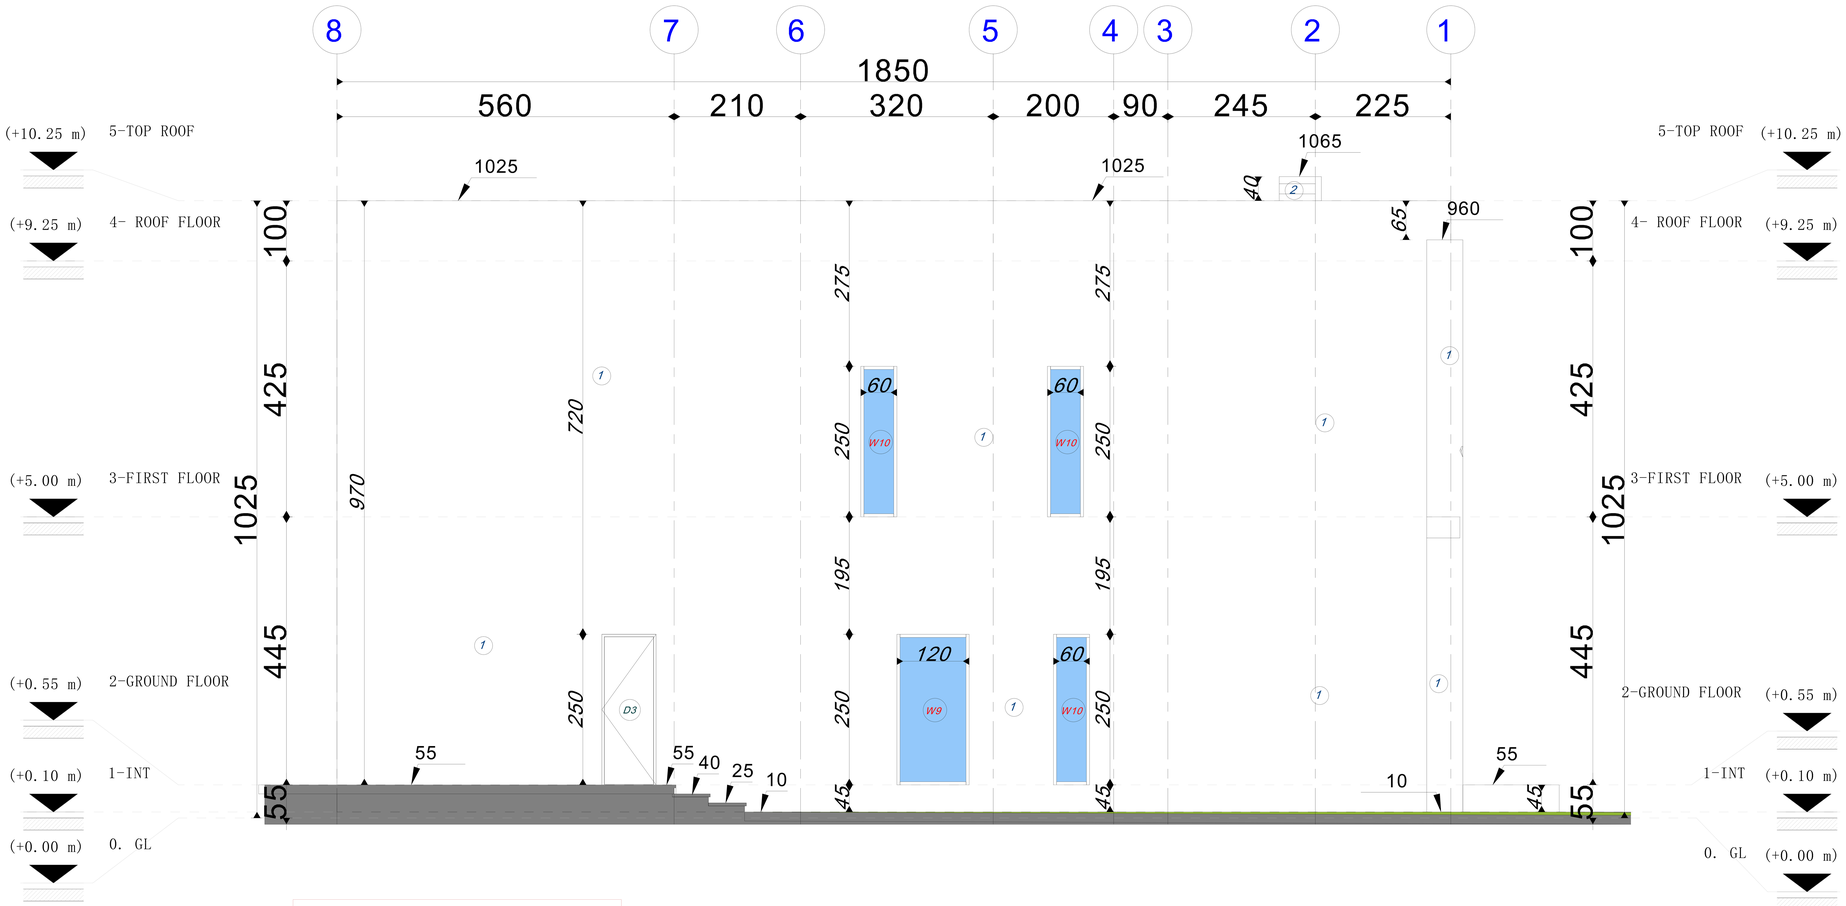

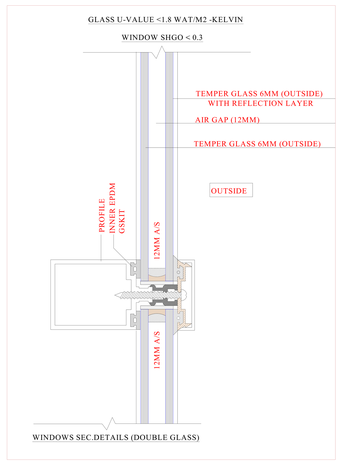

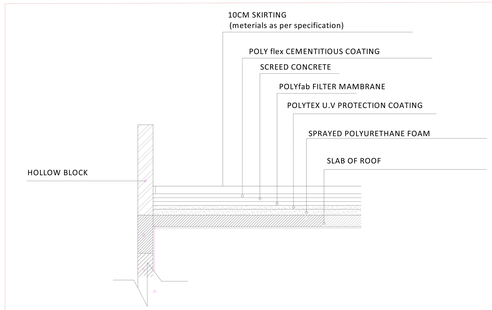

DETAIL FOR COMBO SYSTEM
U-VALUE <0.3 W/M2 K

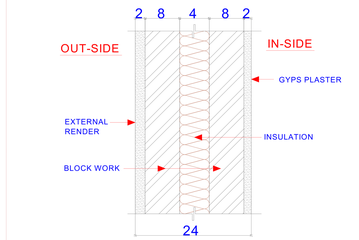

As per E. Walls Predefined Section: W - 1 - A

DETAIL "W1"	TYPICAL FOR EXTERNAL WALL USING INSULATED CONC. BLOCK (200 mm) U-VALUE < 0.5 W/M2 K

LEFT ELEVATION

Govvemment Of Ras Al Khaimah
R.A.K. Municipality
Buildings Administration

حكومة رأس الخيمة
دائرة البلدية
إدارة المباني

Approved On / اعتمد في
30 July 2024
Building Permit #: PRMT-24-0004328
Appoved By:

* Rcc Lintels Must Be Made On Top Of All Doors , Arches And Windows All Of Them Are At Least 0.20 m Thick.
* All Blocks Adjacent To All Doors , Arches And Windows Must Be A Solid Block .

U VALUE AND SHGC

ALL GLASS MUST BE DOUBLE UNITES

GLASS SPECIFICATION:-

U-value (w/m2.k)<_ 1.8

SHADING CO- EFFICIENT (SC) <0.3

FINSHING	
1	FULL EPOXY PAINT [white]
2	TRAVERTINE STONE
3	
4	

Savana
Engineering Consultancy & Interior Design

Client	ISSA LYAS ISSA AL HOUSANI		
Project	Proposed Double Storey Villa		
Drg.Title	LIFT ELEVATION		
Area	AWAFI	Floortype	
Case ID.	2578043	Draw. Type.	ARCH
Sec No.	1	Com. No.	
Block No.		Plot No.	406131666
Bldg. No.	BLD-24-03821	Floor No.	
Date	JULY 2024	Sht. No.	A09
Scale	1/100	Job No.	

G.Manager	Architect	Designed By
ENG AYMEN	ENG IMEN	ENG IMEN

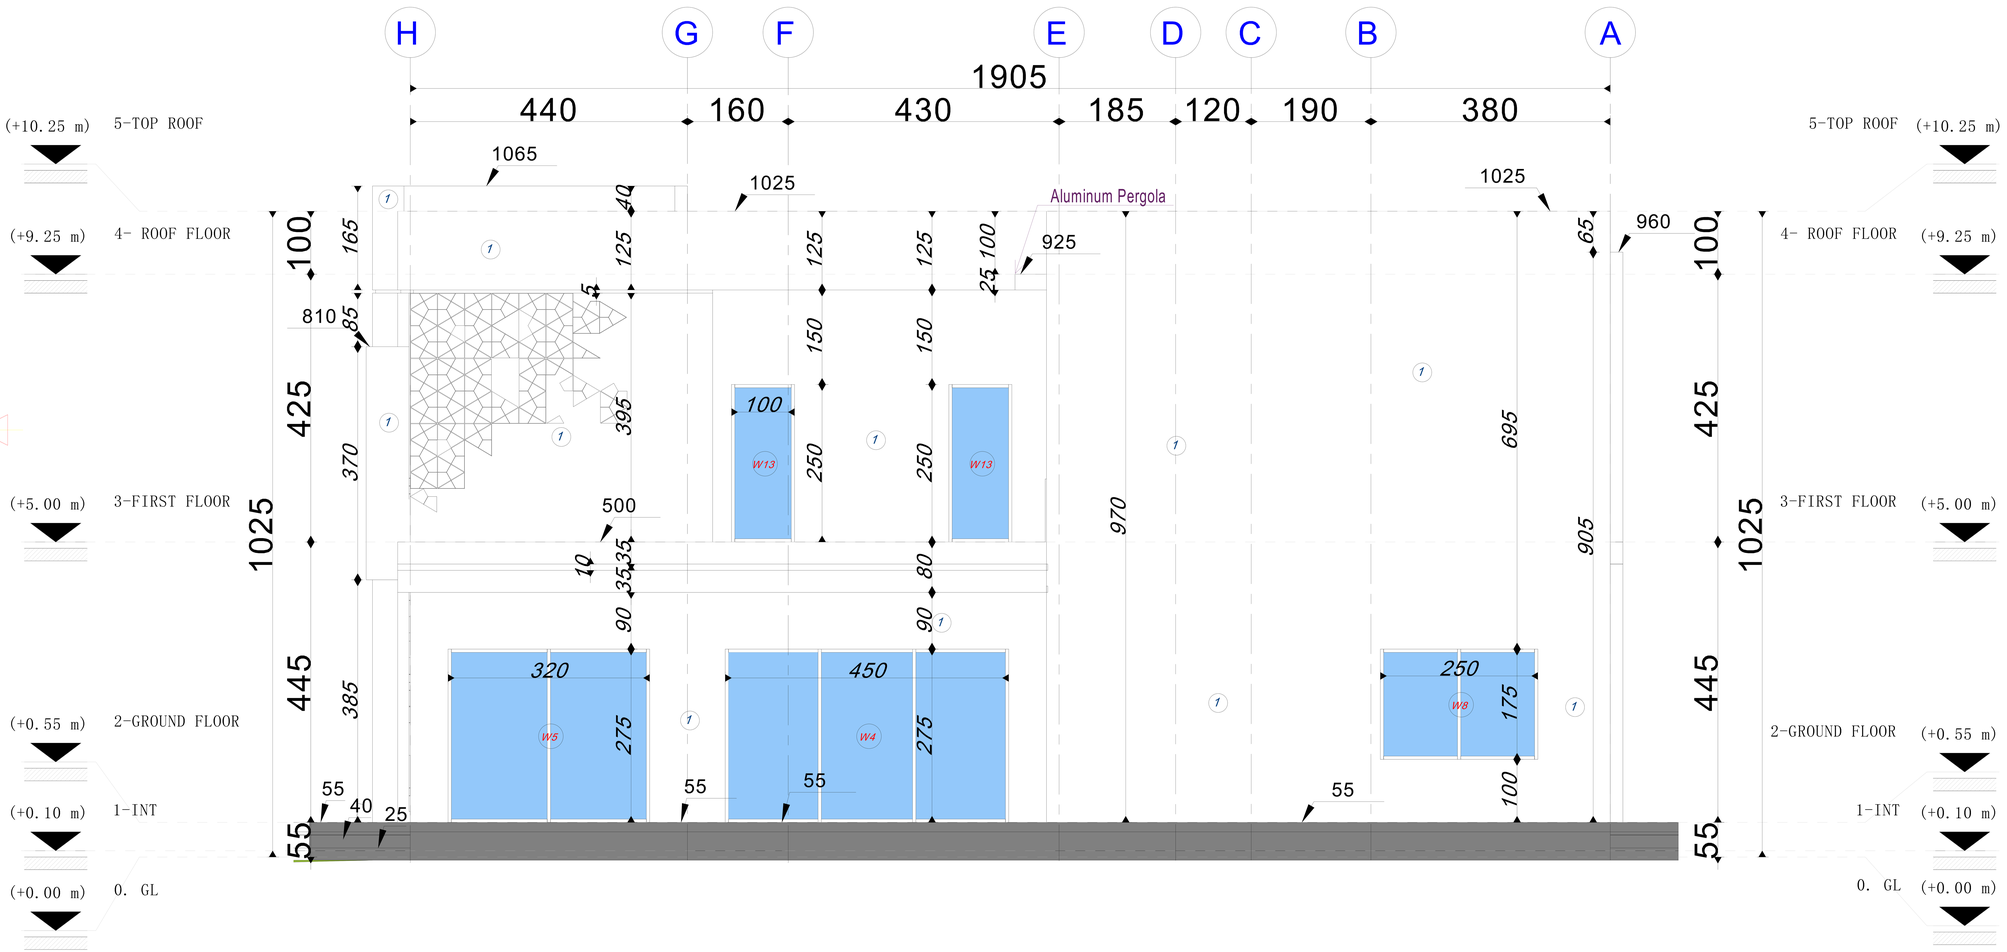

Govement Of Ras Al Khaimah
R.A.K. Municipality
Buildings Administration

حكومة رأس الخيمة
دائرة البلدية
إدارة المباني

Approved On — اعتمد في

30 July 2024

Building Permit #: PRMT-24-0004328

Appoved By:

FINSHING	
1	FULL EPOXY PAINT [white]
2	TRAVERTINE STONE
3	
4	

Savana
Engineering Consultancy & Interior design

Client	ISSA LYAS ISSA AL HOUSANI		
Project	Proposed Double Storey Villa		
Drg.Title	REAR ELEVATION		
Area	AWAFI	Floortype	
Case ID.	2578043	Draw. Type.	ARCH
Sec No.	1	Com. No.	
Block No.		Plot No.	406131666
Bldg. No.	BLD-24-03821	Floor No.	
Date	JULY 2024	Sht. No.	A10
Scale	1/100	Job No.	

G.Manager	Architect	Designed By
ENG AYMEN	ENG IMEN	ENG IMEN

REAR ELEVATION

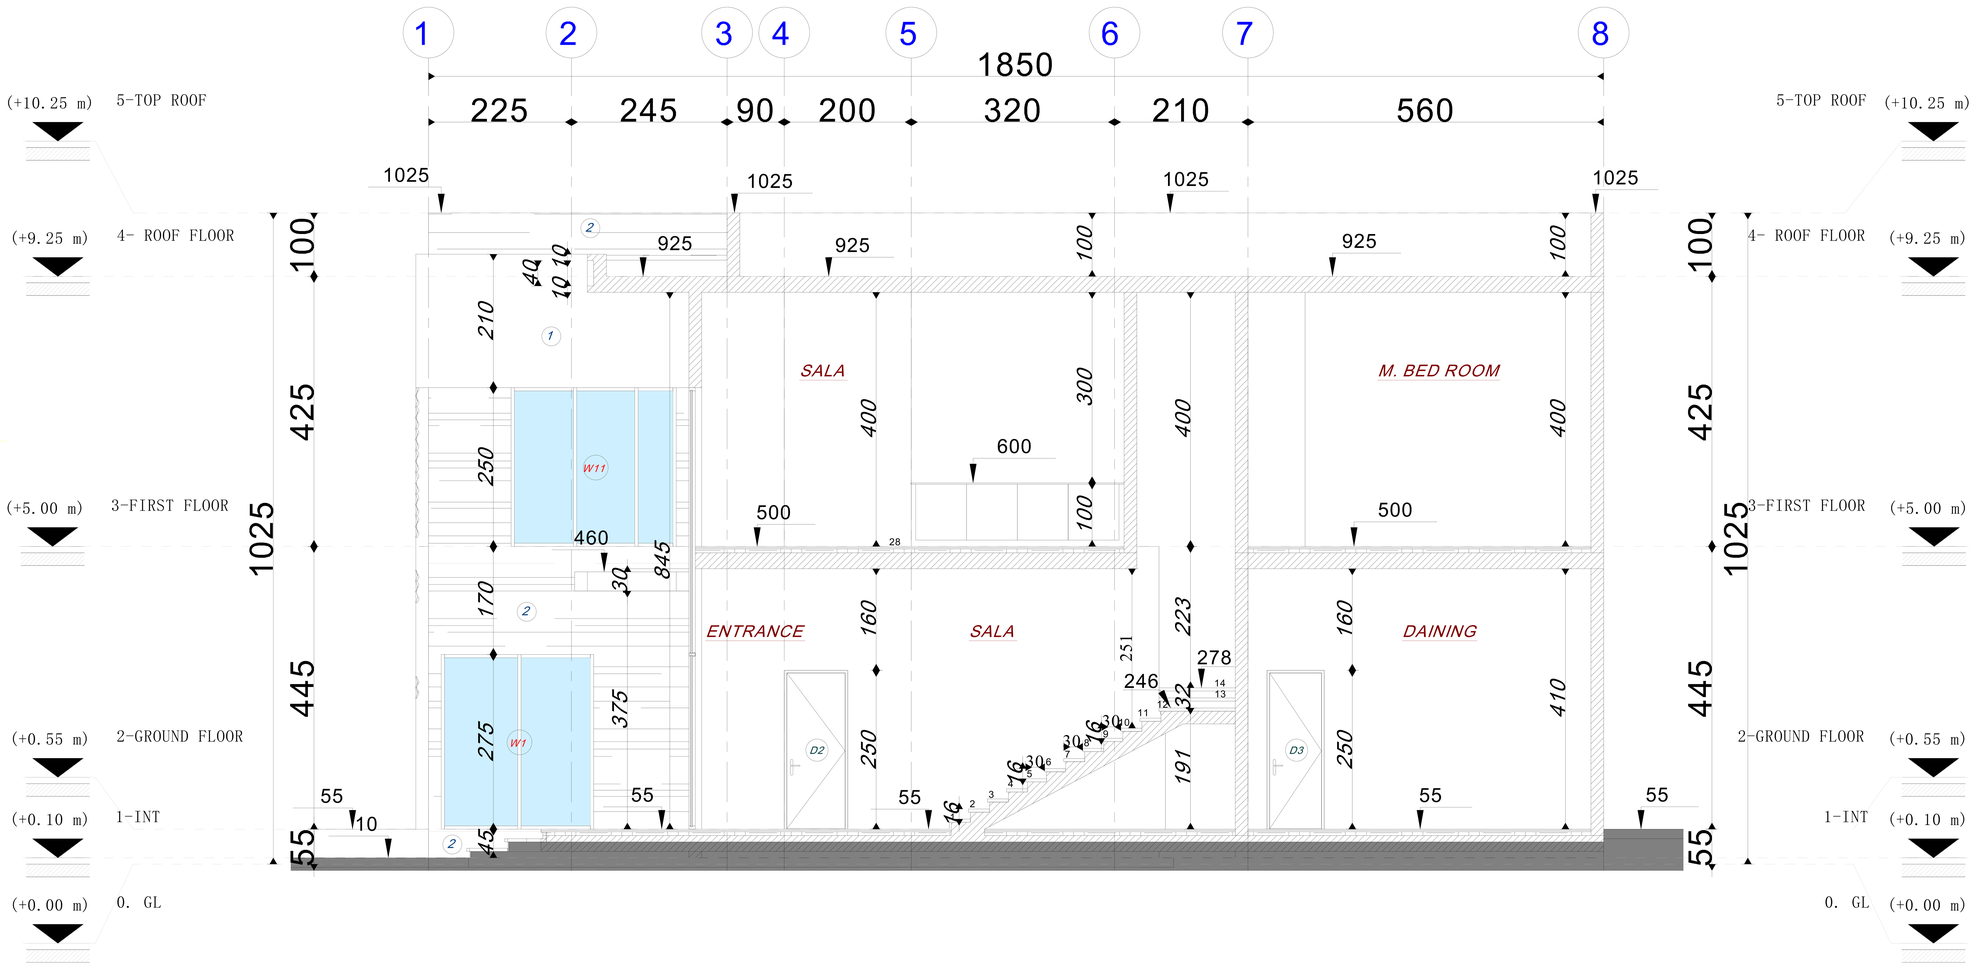

SECTION A-A

ALL GLASS MUST BE DOUBLE UNITES

U-value (w/m2.k)<_ 1.8

SHADING CO- EFFICIENT (SC) <0.3

FINSHING	
1	FULL EPOXY PAINT [white]
2	FULL EPOXY BLACK PAINT
3	WOOD Aluminum
4	

Savana
Engineering Consultancy & interior design

Client	ISSA LYAS ISSA AL HOUSANI		
Project	Proposed Double Storey Villa		
Drg.Title	SECTION A-A		
Area	AWAFI	Floortype	
Case ID.	2578043	Draw. Type.	ARCH
Sec No.	1	Com. No.	
Block No.		Plot No.	406131666
Bldg. No.	BLD-24-03821	Floor No.	
Date	JULY 2024	Sht. No.	A11
Scale	1/100	Job No.	

G.Manager	Architect	Designed By
ENG AYMEN	ENG IMEN	ENG IMEN

Govemment Of Ras Al Khaimah
R.A.K. Municipality
Buildings Administration
حكومة رأس الخيمة
دائرة البلدية
إدارة المباني

Approved On — اعتمد في

30 July 2024

Building Permit #: PRMT-24-0004328

Appoved By:

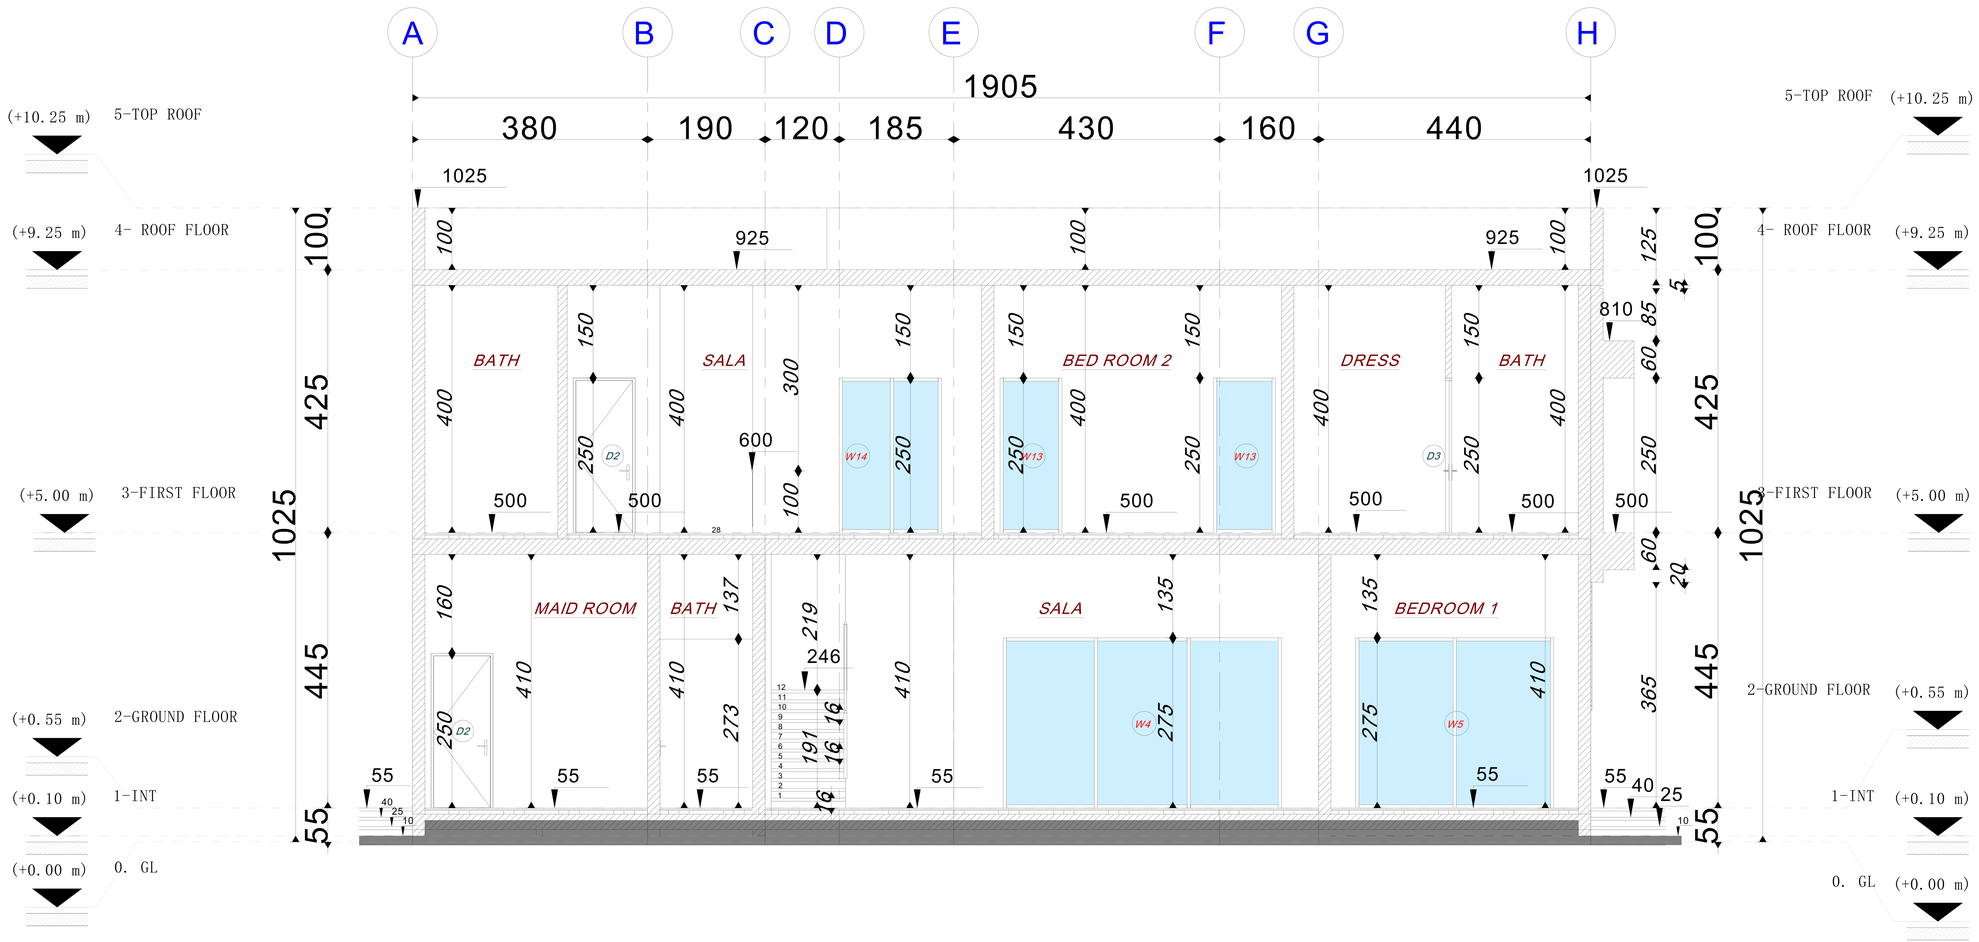

Govemment Of Ras Al Khaimah
R.A.K. Municipality
Buildings Administration

حكومة رأس الخيمة
دائرة البلدية
إدارة المباني

Approved On
اعتمد في

30 July 2024

Building Permit #:
PRMT-24-0004328

Appoved By:

ALL GLASS MUST BE DOUBLE UNITES

GLASS SPECIFICATION:-

U-value (w/m2.k)<_ 1.8

SHADING CO- EFFICIENT (SC) <0.3

FINSHING	
1	FULL EPOXY PAINT [white]
2	FULL EPOXY BLACK PAINT
3	WOOD Aluminum
4	

Savana
Engineering Consultancy & interior design

Client	ISSA LYAS ISSA AL HOUSANI		
Project	Proposed Double Storey Villa		
Drg.Title	SECTION B-B		
Area	AWAFI	Floortype	
Case ID.	2578043	Draw. Type.	ARCH
Sec No.	1	Com. No.	
Block No.		Plot No.	406131666
Bldg. No.	BLD-24-03821	Floor No.	
Date	JULY 2024	Sht. No.	A12
Scale	1/100	Job No.	

G.Manager	Architect	Designed By
ENG AYMEN	ENG IMEN	ENG IMEN

SECTION B-B

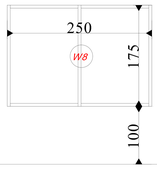

WINDOW 8 (W8) ELEVATION

N=1

G:KITCHEN

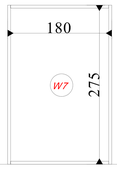

WINDOW 7 (W7) ELEVATION

N=1

G:DINNING

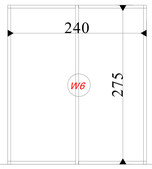

WINDOW6 (W6) ELEVATION

N=1

G:MAJLIS

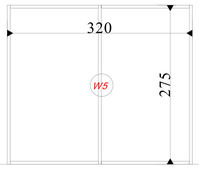

WINDOW 5 (W5) ELEVATION

N=1

G:DINNING

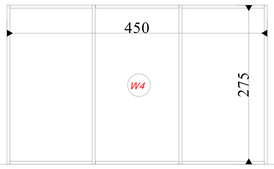

WINDOW 4 (W4) ELEVATION

N=1

G:SALA

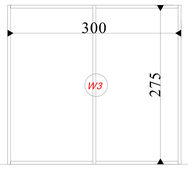

WINDOW 3 (W3) ELEVATION

N=1

G:SALA

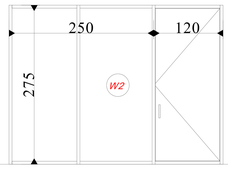

WINDOW DOOR 2 (W2) ELEVATION

N=1

G:MAJLIS

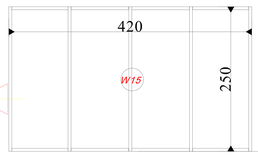

WINDOW 15 (W15) ELEVATION

N=1

F:M.BEDROOM

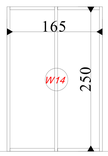

WINDOW 14 (W14) ELEVATION

N=1

F:SALA

WINDOW 13 (W13) ELEVATION

N=3

F:BEDROOM 2+STAIR

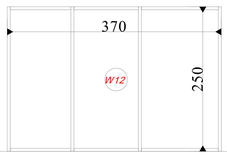

WINDOW 12 (W12) ELEVATION

N=1

F:BEDROOM 3

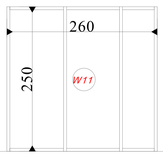

WINDOW11 (W11) ELEVATION

N=2

F:BEDROOM 3+4

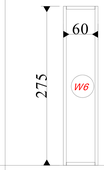

WINDOW10* (W10*) ELEVATION

N=5

G:BATH

WINDOW 10 (W10) ELEVATION

N=5

G:BATH
F:BEDROOM (M+2+3+4)

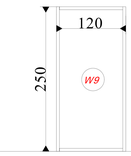

WINDOW 9 (W9) ELEVATION

N=1

G:MAID ROOM

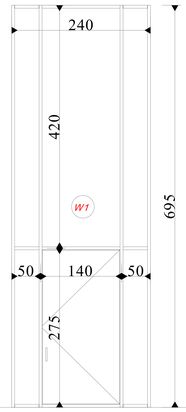

WINDOW DOOT 1 (W1) ELEVATION

N=1

G:ENTRANCE
F:PANTRY

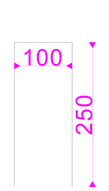

(A01)-ELEVATION

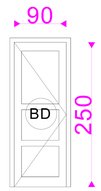

DOOR (D3)-ELEVATION

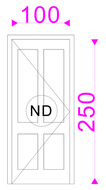

DOOR (D2)ELEVATION

OPENNING DETAILS

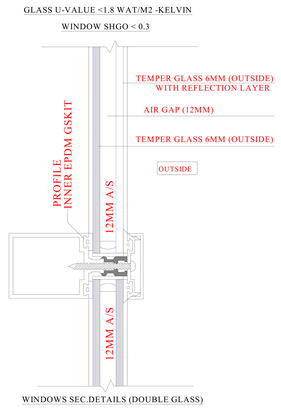

ALL GLASS MUST BE DOUBLE UNITES

GLASS SPECIFICATION:-

U-value (w/m2.k)<_ 1.8

SHADING CO- EFFICIENT (SC) <0.3

Govemment Of Ras Al Khaimah
R.A.K. Municipality
Buildings Administration

حكومة رأس الخيمة
دائرة البلدية
إدارة المباني

Approved On — اعتمد في

30 July 2024

Building Permit #: PRMT-24-0004328

Appoved By:

Savana
Engineering Consultancy & interior design

Client	ISSA LYAS ISSA AL HOUSANI		
Project	Proposed Double Storey Villa		
Drg.Title	Opening Details		
Area	AWAFI	Floortype	
Case ID.	2578043	Draw. Type.	ARCH
Sec No.	1	Com. No.	
Block No.		Plot No.	406131666
Bldg. No.	BLD-24-03821	Floor No.	
Date	JULY 2024	Sht. No.	A13
Scale	1/100	Job No.	

G.Manager	Architect	Designed By
ENG AYMEN	ENG IMEN	ENG IMEN

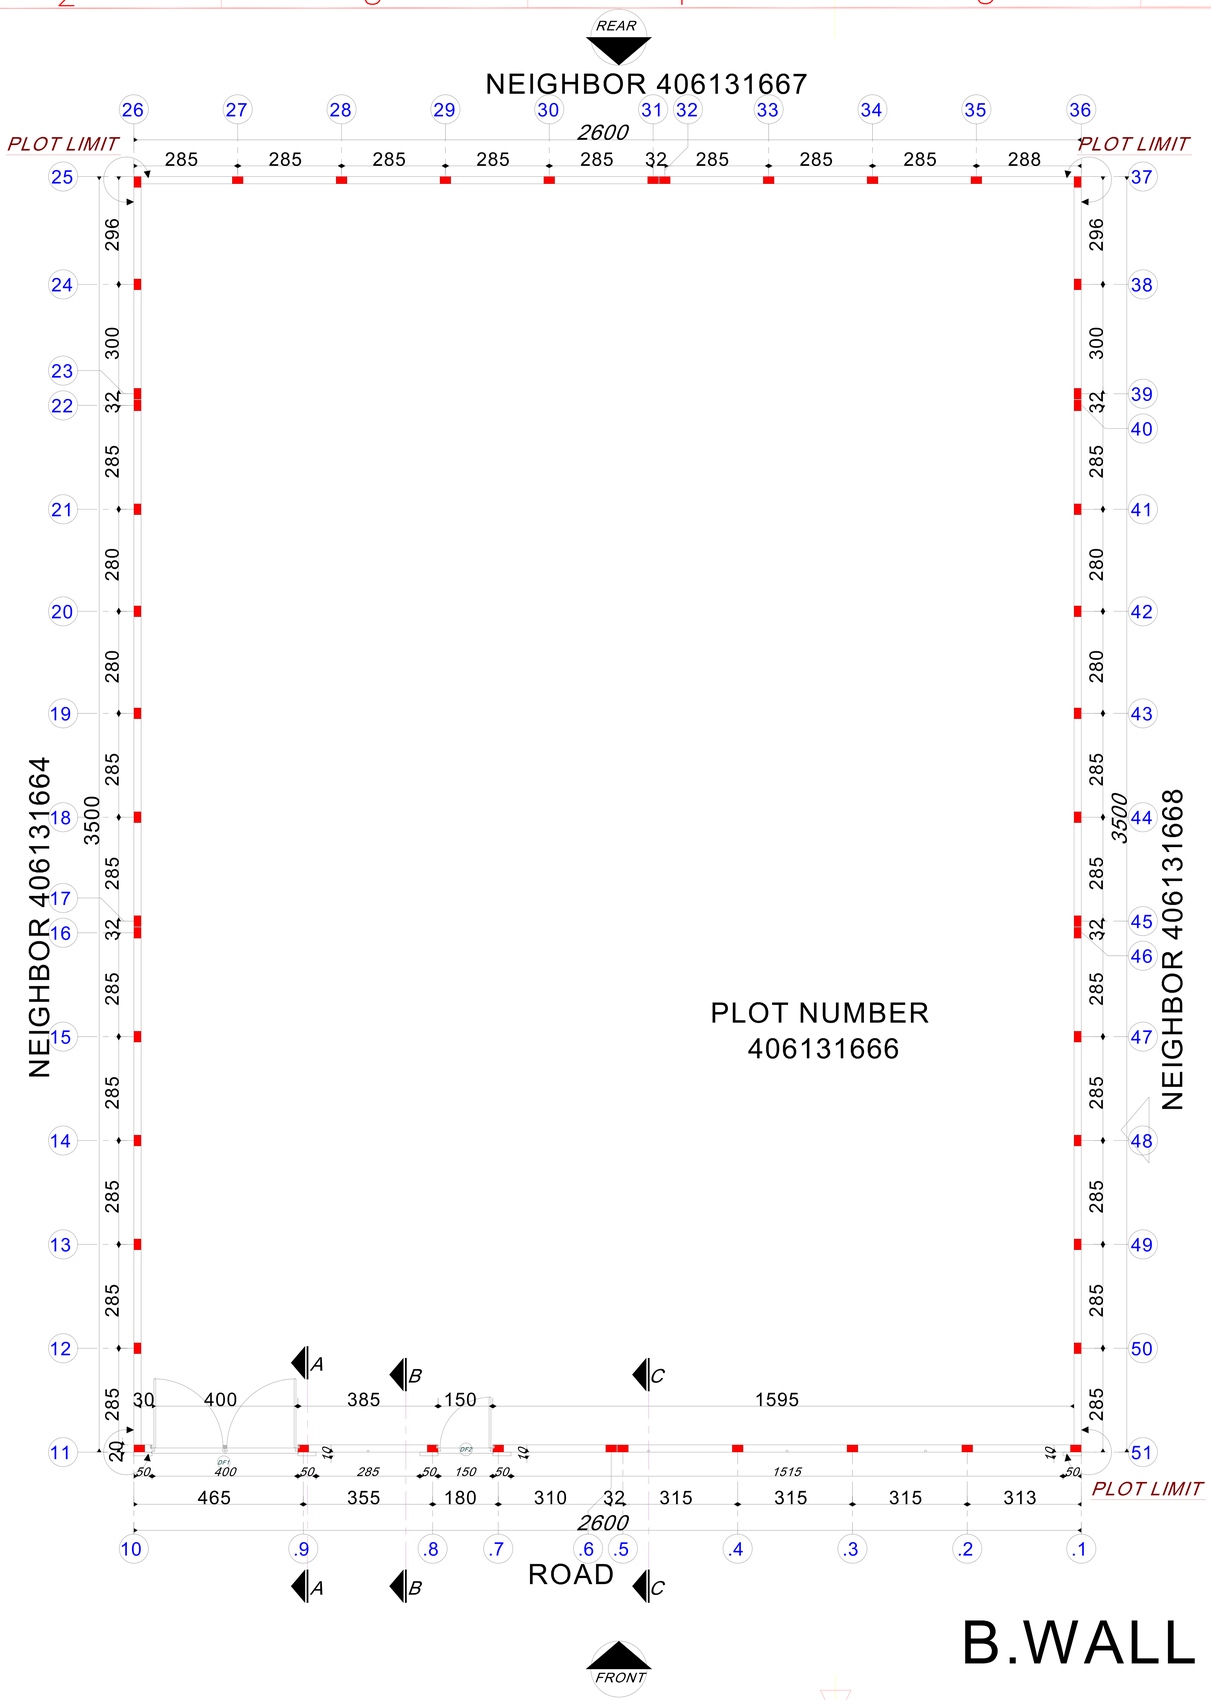

B.WALL SITE PLAN

Govemment Of Ras Al Khaimah
R.A.K. Municipality
Buildings Administration

حكومة رأس الخيمة
دائرة البلدية
إدارة المباني

Approved On — اعتمد في

30 July 2024

Building Permit #: PRMT-24-0004328

Appoved By:

Savana
Engineering Consultancy & interior design

Client	ISSA LYAS ISSA AL HOUSANI		
Project	Proposed Double Storey Villa		
Drg.Title	BOUNDARY WALL LAYOUT PLAN		
Area	AWAFI	Floortype	
Case ID.	2578043	Draw. Type.	ARCH
Sec No.	2	Com. No.	
Block No.		Plot No.	406131666
Bldg. No.	FNC-24-001940	Floor No.	
Date	JULY 2024	Sht. No.	A15
Scale	1/100	Job No.	

G.Manager	Architect	Designed By
ENG AYMEN	ENG IMEN	ENG IMEN

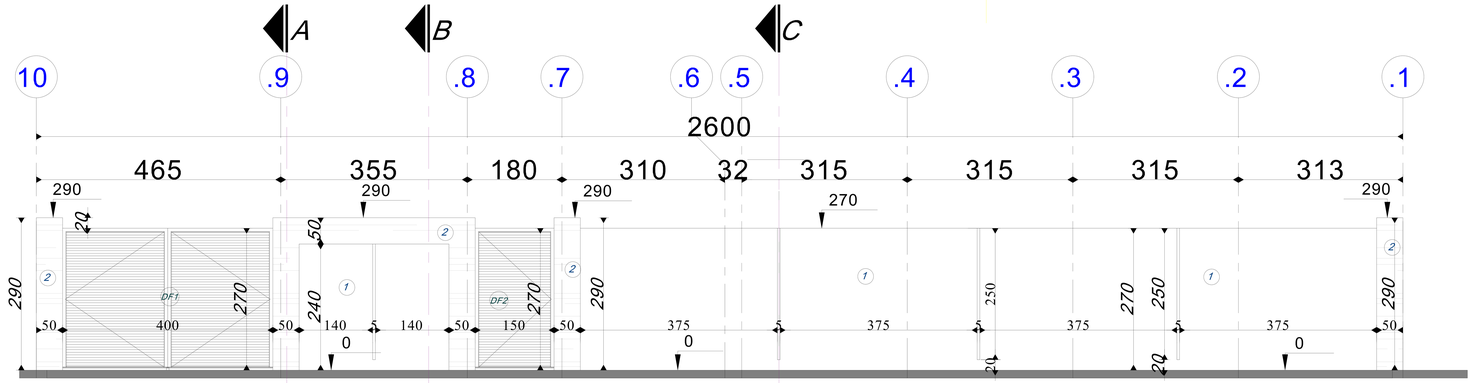

FRONT ELEVATION

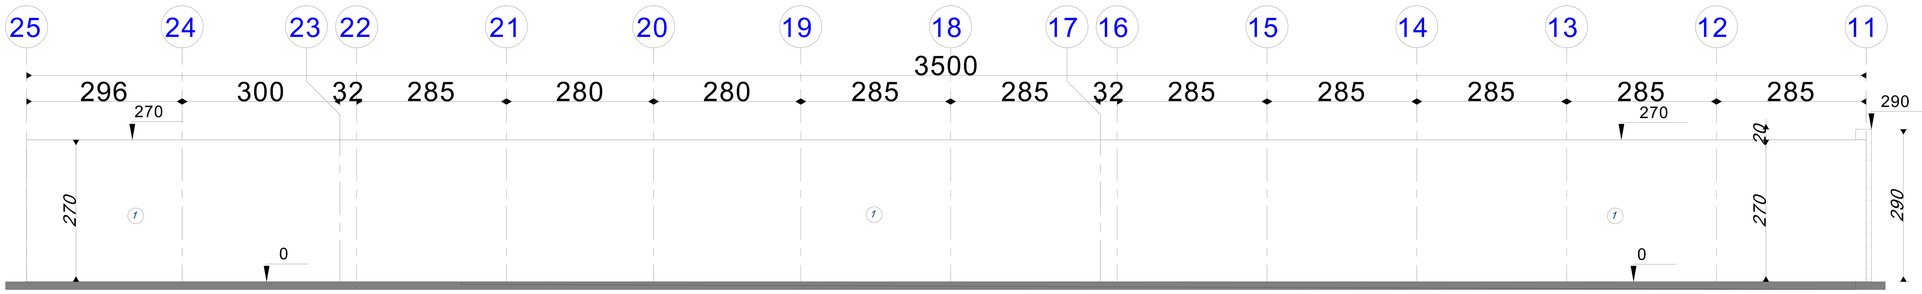

LEFT ELEVATION

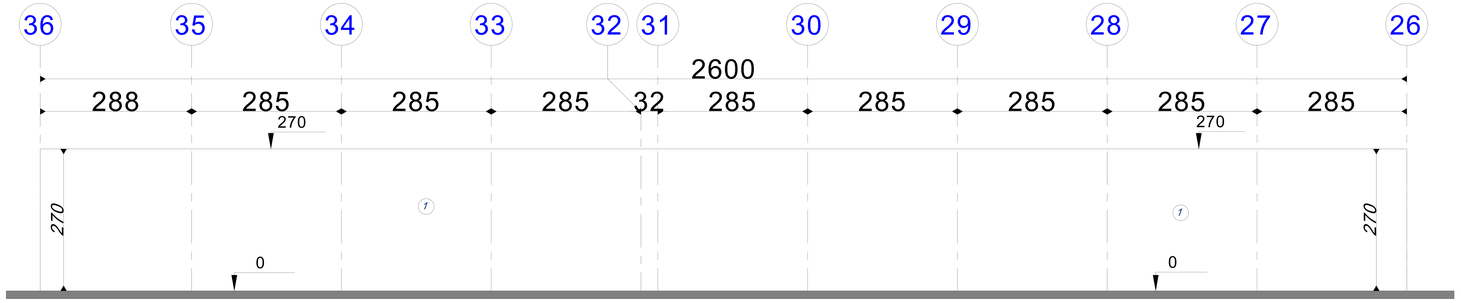

REAR ELEVATION

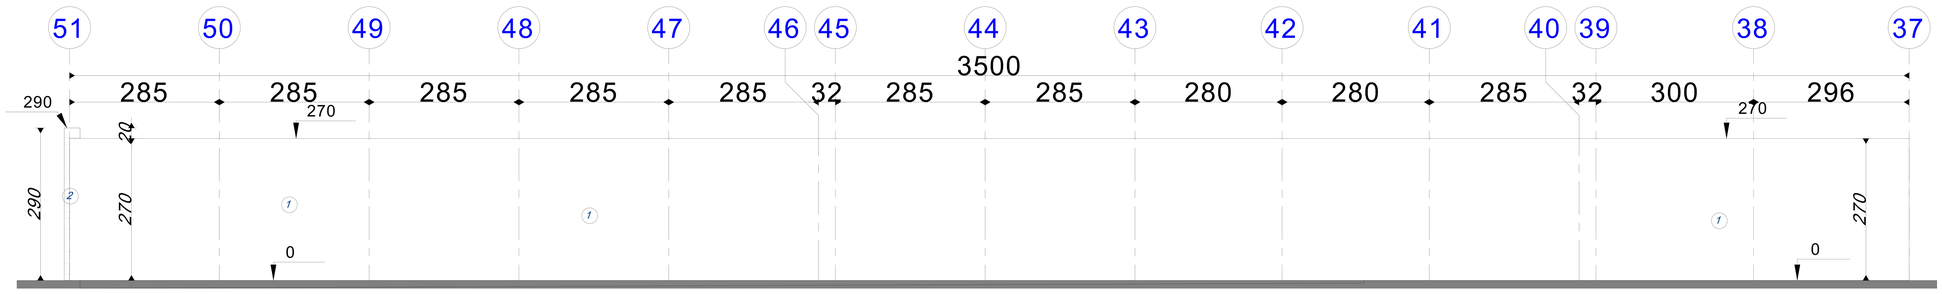

RIGHT ELEVATION

Govemment Of Ras Al Khaimah
R.A.K. Municipality
Buildings Administration

حكومة رأس الخيمة
دائرة البلدية
إدارة المباني

Approved On — اعتمد في

30 July 2024

Building Permit #: PRMT-24-0004328

Appoved By:

Savana
Engineering Consultancy & interior design

Client	ISSA LYAS ISSA AL HOUSANI		
Project	Proposed Double Storey Villa		
Drg.Title	Proposed Boundary Wall Elevations		
Area	AWAFI	Floortype	
Case ID.	2578043	Draw. Type.	ARCH
Sec No.	2	Com. No.	
Block No.		Plot No.	406131666
Bldg. No.	FNC-24-001940	Floor No.	
Date	JULY 2024	Sht. No.	A16
Scale	1/100	Job No.	

G.Manager	Architect	Designed By
ENG AYMEN	ENG IMEN	ENG IMEN

B.WALL ELEVATION

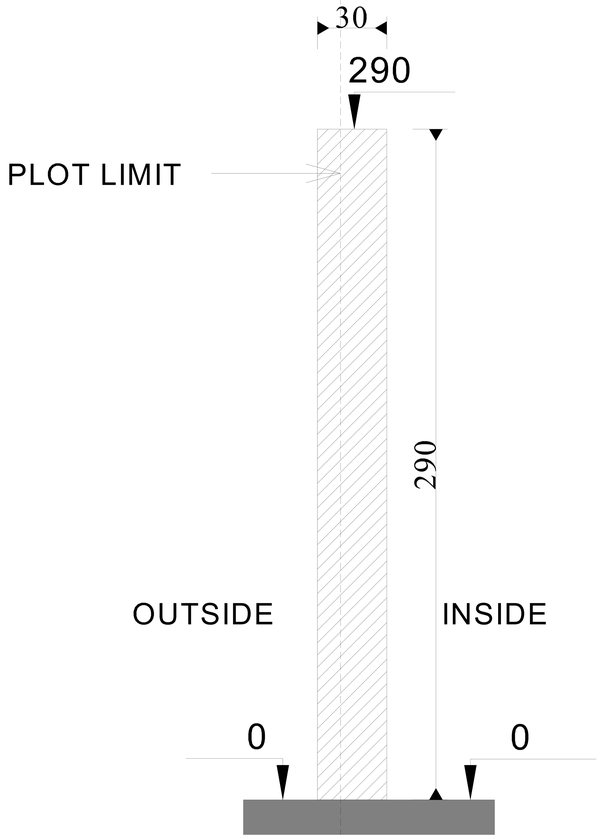

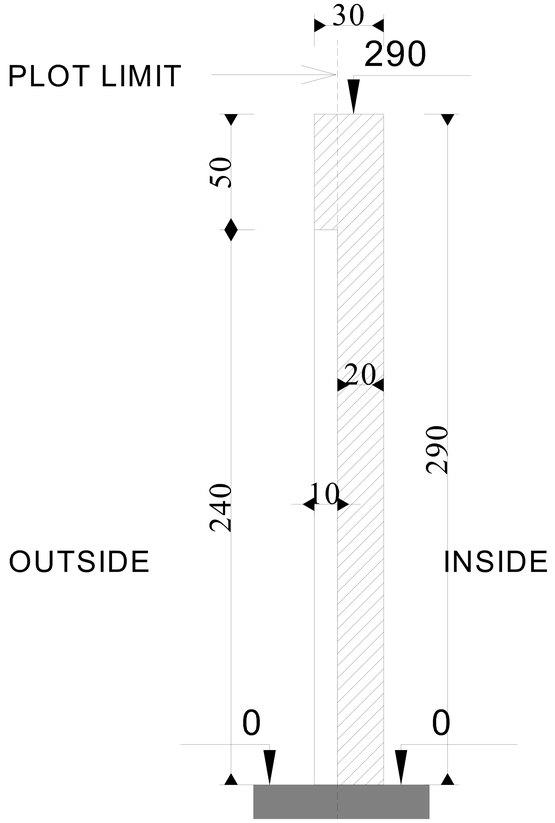

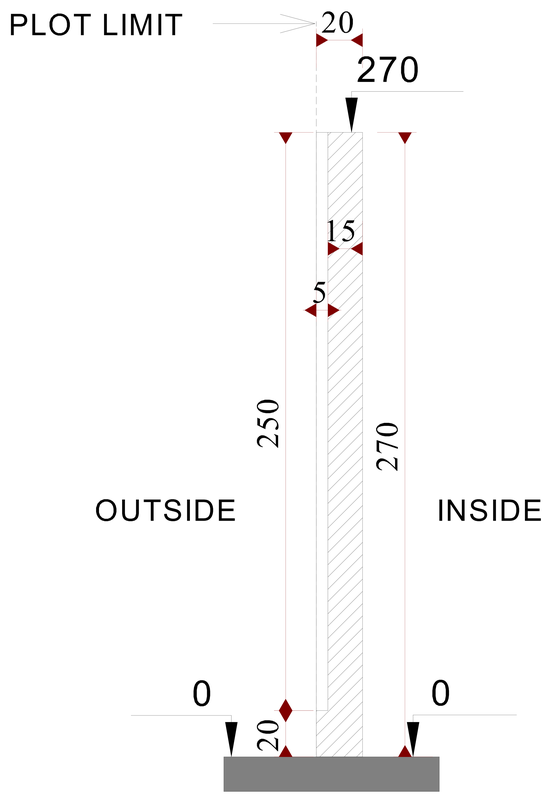

Govemment Of Ras Al Khaimah
R.A.K. Municipality
Buildings Administration

حكومة رأس الخيمة
دائرة البلدية
إدارة المباني

Approved On — اعتمد في

30 July 2024

Building Permit #: PRMT-24-0004328

Appoved By:

SECTION A-A
SCALE 1:25

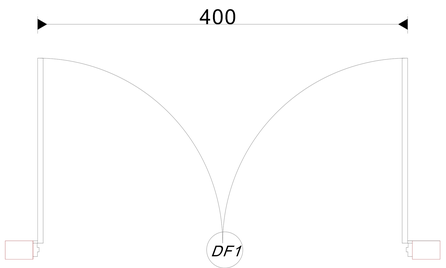

DOOR (DF1)-ELEVATION
SCALE 1:50

SECTION B-B
SCALE 1:25

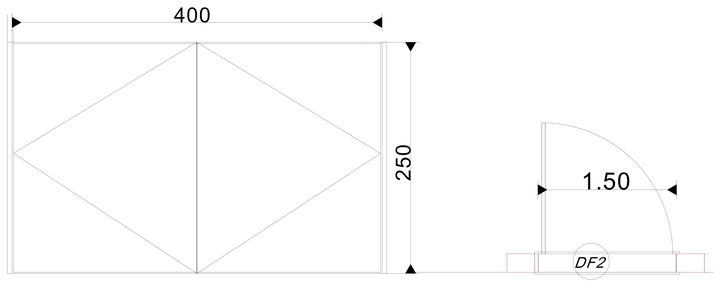

DOOR (DF2)-ELEVATION
SCALE 1:50

SECTION C-C
SCALE 1:25

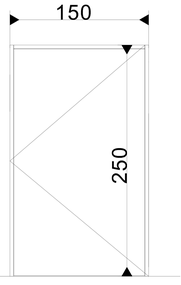

B.WALL SECTION

Savana
Engineering Consultancy & interior design

Client	ISSA LYAS ISSA AL HOUSANI		
Project	Proposed Double Storey Villa		
Drg.Title	Boundary Wall DETAILS		
Area	AWAFI	Floortype	
Case ID.	2578043	Draw. Type.	ARCH
Sec No.	2	Com. No.	
Block No.		Plot No.	406131666
Bldg. No.	FNC-24-001940	Floor No.	
Date	JULY 2024	Sht. No.	A17
Scale	1/100	Job No.	

G.Manager	Architect	Designed By
ENG AYMEN	ENG IMEN	ENG IMEN

Type	SCHEDULE OF FINISHINGS
1	LIGHT IVORY

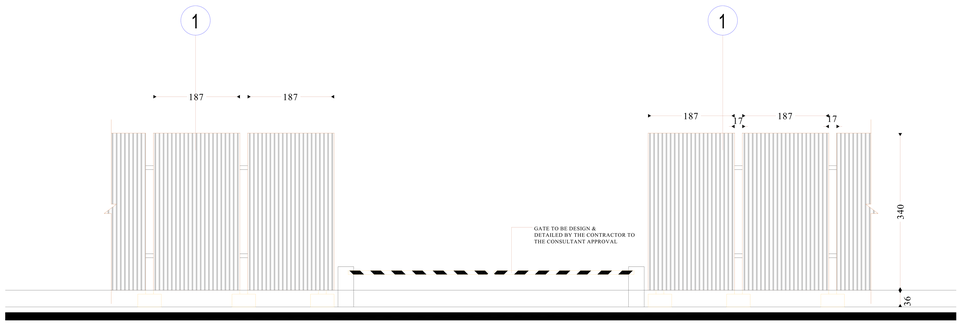

ALUMINIUM TEMPORARY FENCE

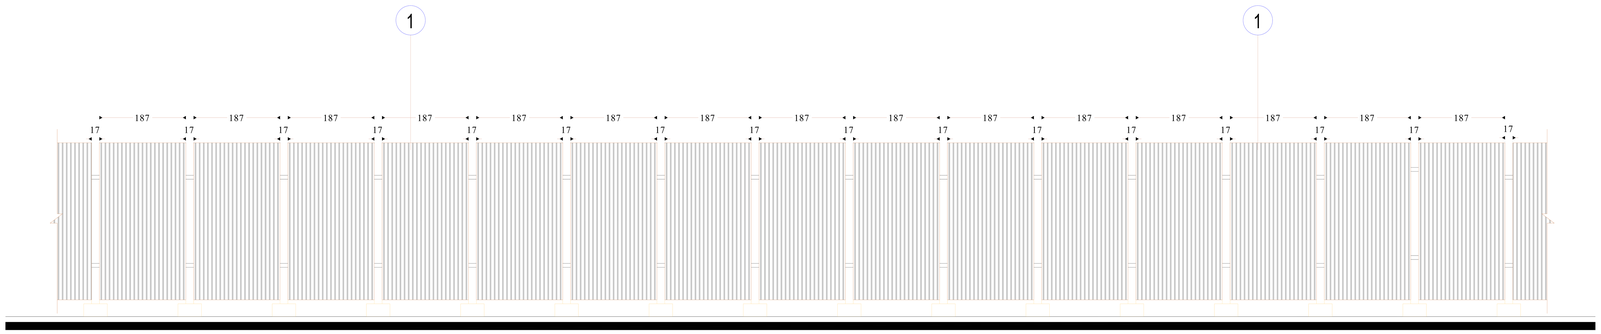

HOARDING ELEVATION

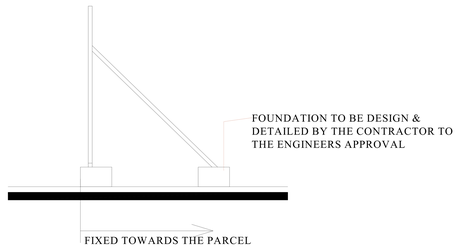

HOARDING SIDE ELEVATION

Govemment Of Ras Al Khaimah
R.A.K. Municipality
Buildings Administration

حكومة رأس الخيمة
دائرة البلدية
إدارة المباني

Approved On — اعتمد في

30 July 2024

Building Permit #: PRMT-24-0004328

Appoved By:

Savana
Engineering Consultancy & interior design

Client	ISSA LYAS ISSA AL HOUSANI		
Project	Proposed Double Storey Villa		
Drg.Title	ALLUMINIUM FENCE		
Area	AWAFI	Floortype	
Case ID.	2578043	Draw. Type.	ARCH
Sec No.	2	Com. No.	
Block No.		Plot No.	406131666
Bldg. No.	BLD-24-03821	Floor No.	
Date	JULY 2024	Sht. No.	A19
Scale	1/100	Job No.	

G.Manager	Architect	Designed By
ENG AYMEN	ENG IMEN	ENG IMEN

ALLUMINIUM FENCE

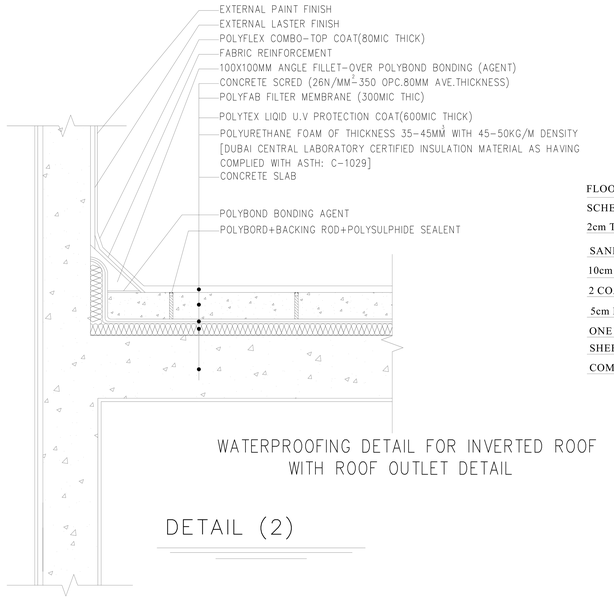

WATERPROOFING DETAIL FOR INVERTED ROOF
WITH ROOF OUTLET DETAIL

DETAIL (2)

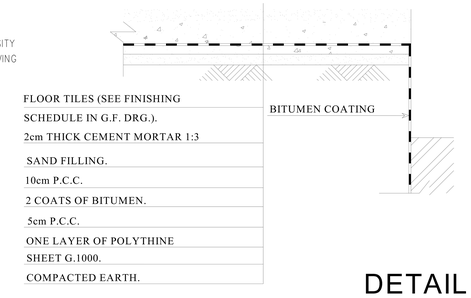

DETAIL (4)

ENTRANCE STEPS DETAIL

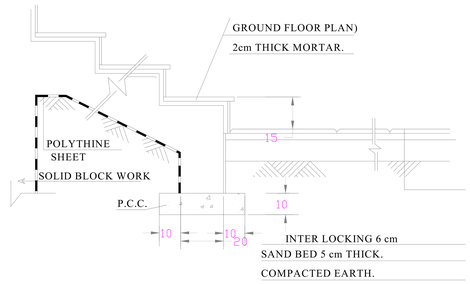

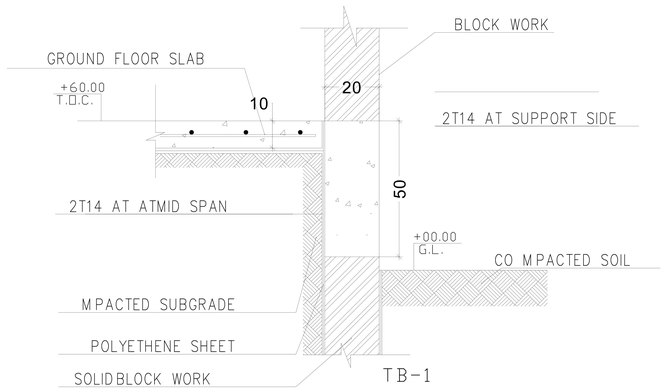

DETAIL (3)

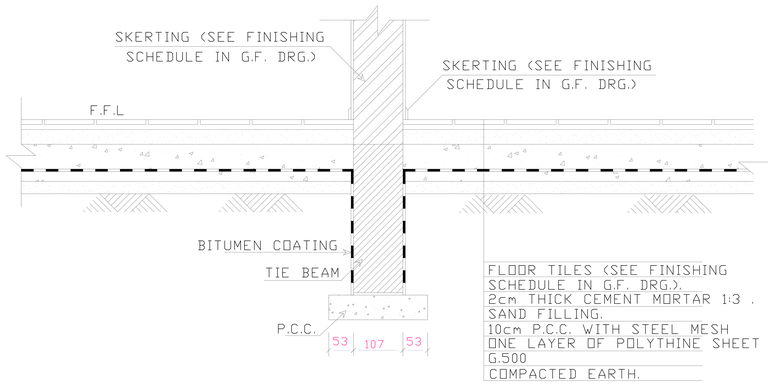

DETAIL (1)

GENERALE DETAILS

Govemment Of Ras Al Khaimah
R.A.K. Municipality
Buildings Administration

حكومة رأس الخيمة
دائرة البلدية
إدارة المباني

Approved On — اعتمد في

30 July 2024

Building Permit #: PRMT-24-0004328

Appoved By:

Savana
Engineering Consultancy & interior design

Client	ISSA LYAS ISSA AL HOUSANI		
Project	Proposed Double Storey Villa		
Drg.Title	GENERALE DETAILS		
Area	AWAFI	Floortype	
Case ID.	2578043	Draw. Type.	ARCH
Sec No.	2	Com. No.	
Block No.		Plot No.	406131666
Bldg. No.	BLD-24-03821	Floor No.	
Date	JULY 2024	Sht. No.	A20
Scale	1/100	Job No.	

G.Manager	Architect	Designed By
ENG AYMEN	ENG IMEN	ENG IMEN