Government Of Ras Al Khaimah
R.A.K. Municipality
Buildings Administration

حكومة رأس الخيمة
دائـرة البلـدية
إدارة المباني

Approved On اعتمد في

31 December 2025

Building Permit #:

Appoved By:

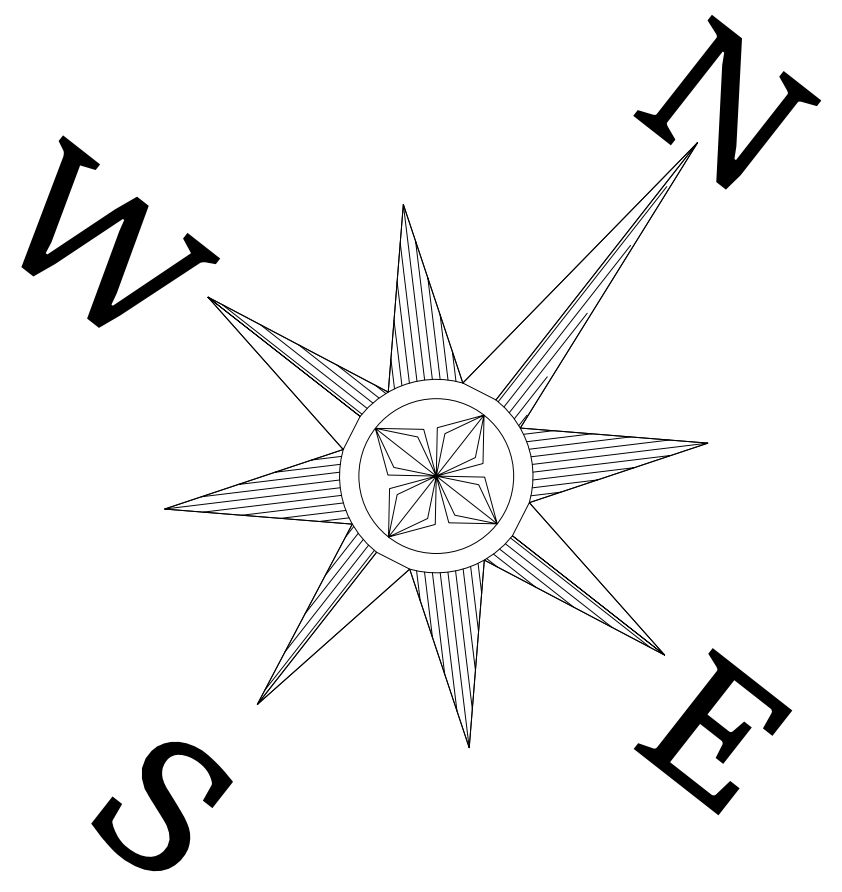

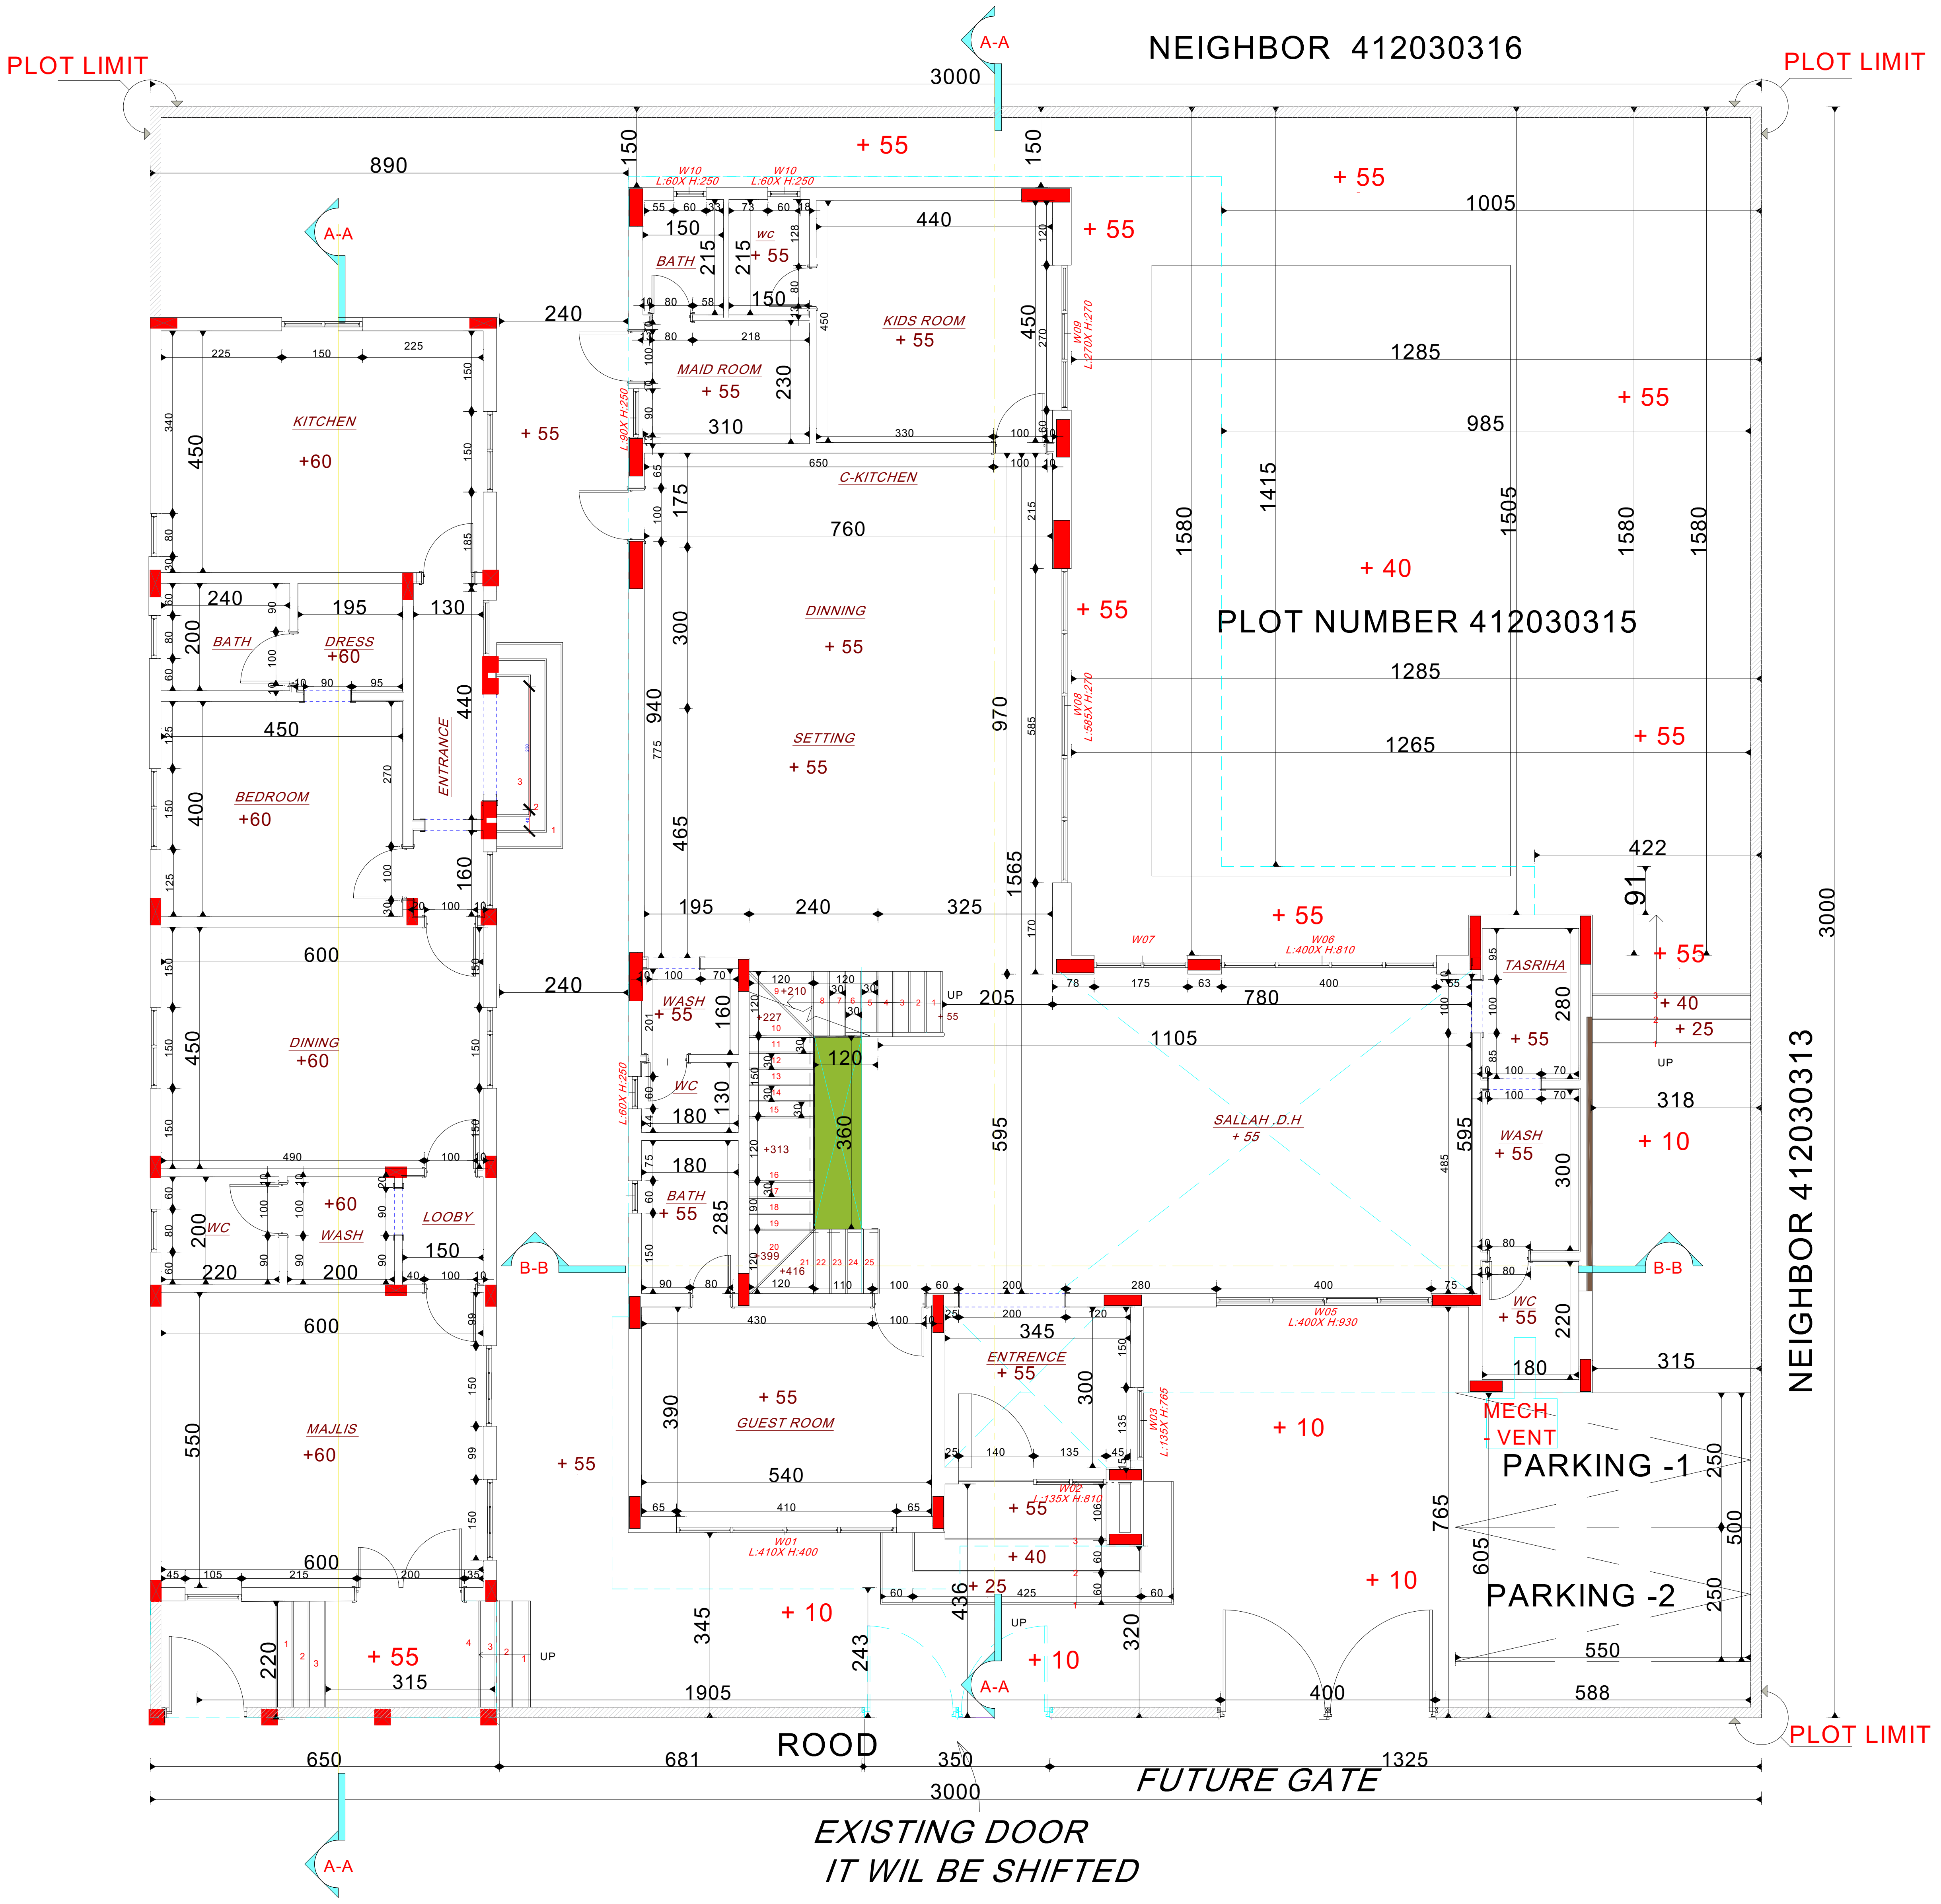

NEIGHBOR 412030316
PLOT LIMIT
PLOT LIMIT
PLOT LIMIT
3000
890
150
150
A-A
+ 55
+ 55
+ 55
1005
1285
985
+ 55
1580
1415
1505
1580
1580
+ 40
PLOT NUMBER 412030315
1285
1265
+ 55
422
91
+ 55
+ 40
+ 25
318
+ 10
315
3000
NEIGHBOR 412030313
W10 L:60X H:250
W10 L:60X H:250
BATH
WC
+ 55
150
215
215
440
KIDS ROOM
+ 55
450
W09 L:270X H:270
MAID ROOM
+ 55
230
310
240
L:90X H:250
C-KITCHEN
650
175
760
DINNING
+ 55
SETTING
+ 55
300
940
465
970
1565
W08 L:585X H:270
195
240
325
KITCHEN
+60
450
225
150
225
240
195
130
BATH
DRESS
+60
200
450
BEDROOM
+60
400
ENTRANCE
440
160
600
DINING
+60
450
240
WASH
+ 55
WC
180
180
BATH
+ 55
160
130
285
360
120
UP
205
W07
W06 L:400X H:810
780
1105
SALLAH .D.H
+ 55
595
TASRIHA
280
+ 55
WASH
+ 55
300
595
WC
+ 55
220
180
WC
WASH
+60
LOOBY
200
220
200
150
B-B
B-B
600
MAJLIS
+60
550
+ 55
390
+ 55
GUEST ROOM
540
W01 L:410X H:400
345
ENTRENCE
+ 55
300
W03 L:135X H:765
W02 L:135X H:810
+ 55
+ 40
+ 25
436
UP
W05 L:400X H:930
+ 10
MECH - VENT
PARKING -1
PARKING -2
765
605
250
500
250
550
588
+ 10
+ 10
+ 10
320
243
345
600
+ 55
315
220
UP
650
681
1905
ROOD
350
FUTURE GATE
1325
400
3000
A-A
A-A
EXISTING DOOR
IT WIL BE SHIFTED

SITE SETTING PLAN

Savana
Engineering Consultancy & interior design

Client	FAHAD SULAIMAN ABDULLA ALSHEHI		
Project	KITCHEN BLOCK		
Drg.Title	SITE SETTING PLAN		
Area	SHEIKH ZAYED	Floortype	
Case ID.	3120158	Draw. Type.	ARCH
Sec No.	1	Com. No.	
Block No.		Plot No.	412030315
Bldg. No.	BLD-25-03487	Floor No.	
Date	12/2025	Sht. No.	A03A
Scale	1/100	Job No.	

G.Manager	Architect	Designed By
ENG AYMEN	ENG IMEN	M. AHMED