


A
B
C
D
E
F

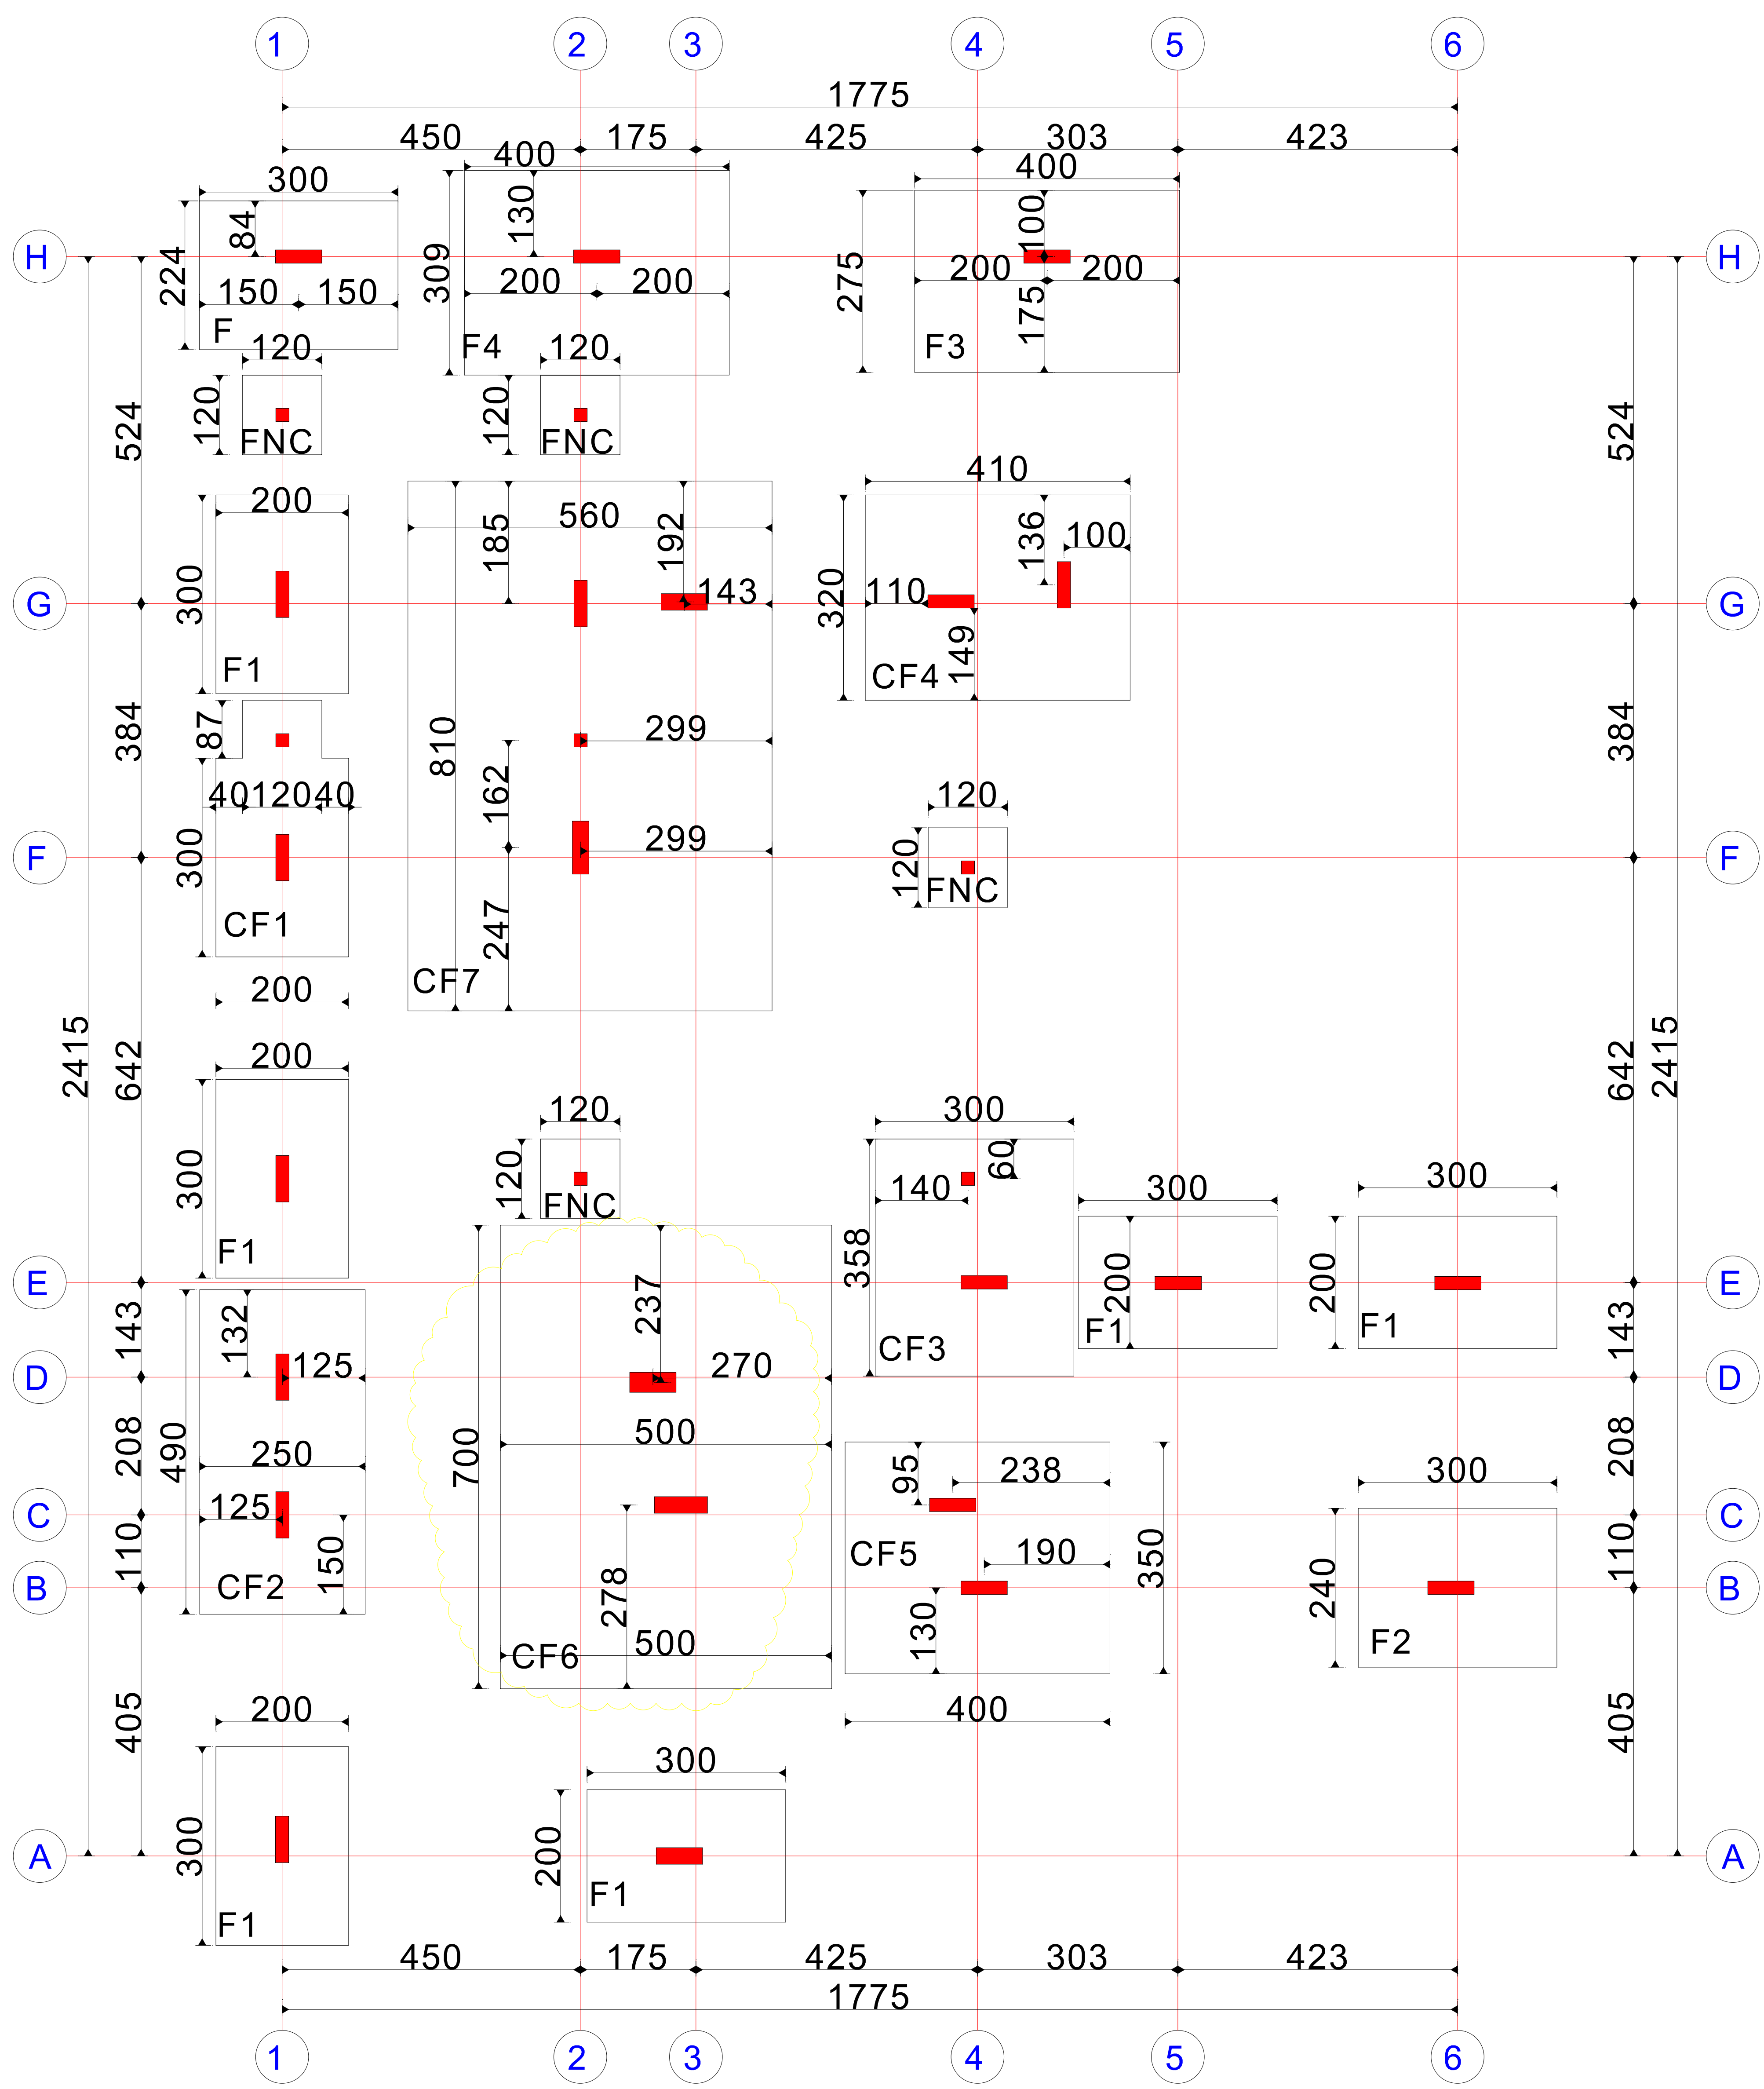

FOUNDATION LAYOUT

Government Of Ras Al Khaimah
R.A.K. Municipality
Buildings Administration



حكومة رأس الخيمة
دائرة البلدية
إدارة المباني

Approved On
21 January 2026

Building Permit #: PRMT-25-0004269

Approved By:


STRUCTURAL NOTES		CONCRETE COVERS :	
ACI 318-11		Foundations cover = 75mm	
F'C/FCU = 28/35 N/mm2		Columns cover = 40mm	
FY = 460N/mm2		Walls cover = 30mm	
FYt = 420N/mm2		Beams cover = 40mm	
		Slabs & Stairs cover = 25mm	



Savana
Engineering Consultancy & Interior Design

Client	ABDULAZIZ TAHNOON AL MANSOORI		
Project	DOUBLE STORY VILLA		
Drg.Title	FOUNDATION LAYOUT		
Area	AWAFI	Floortype	
Case ID.	3145956	Draw. Type.	STRC
Sec No.	1	Com. No.	
Block No.		Plot No.	406132231
Bldg. No.	BLD-25-03478	Floor No.	
Date	01/2026	Sht. No.	S02
Scale	1/100	Job No.	
G.Manager	Architect	Designed By	
ENG AYMEN	ENG IMEN	ENG IMEN	

A

B

C

D

E

F

A

B

C

D

E

F

Government Of Ras Al Khaimah
R.A.K. Municipality
Buildings Administration



حكومة رأس الخيمة
دائرة البلدية
إدارة المباني

Approved On

اعتمد في

21 January 2026

Building Permit #:
PRMT-25-0004269

Approved By:


SCHEDULE OF FOOTINGS

TYPE	SIZE			REINFORCEMENT DETAILS				REMARKS.
	WIDTH (MM)	LENGTH (MM)	DEPTH (MM)	BOTTOM MESH		TOP MESH		
				SHORT BAR	LONG BAR	SHORT BAR	LONG BAR	
FNC	1200	1200	400	T14-200	T14-200	5T14	5T14	
F1	2000	3000	400	T14-125	T14-125	5T14	5T14	
F2	3000	2400	400	T14-125	T14-125	5T14	5T14	
F3	4000	2750	400	T14-125	T14-125	5T14	5T14	
F4	4000	3090	400	T14-125	T14-125	5T14	5T14	
CF1	AS PER LAYOUT		400	T14-100	T14-100	T14-200	T14-200	
CF2	2500	4900	400	T14-100	T14-100	T14-200	T14-200	
CF3	3000	3580	400	T16-125	T16-125	T14-200	T14-200	
CF4	4100	3200	400	T14-100	T14-100	T14-200	T14-200	
CF5	4000	3500	400	T16-125	T16-125	T14-200	T14-200	
CF6	5000	7000	600	T18-100	T18-100	T16-150	T16-150	
CF7	5600	8100	600	T18-100	T18-100	T16-150	T16-150	
F	2240	3000	400	T14-150	T14-150	5T14	5T14	

SCHEDUEL FOUNDATION



Client	ABDULAZIZ TAHHNOON AL MANSOORI		
Project	DOUBLE STORY VILLA		
Drg.Title	FOUNDATION SCHEDULE		
Area	AWAFI	Floortype	
Case ID.	3145956	Draw. Type.	STRC
Sec No.	1	Com. No.	
Block No.		Plot No.	406132231
Bldg. No.	BLD-25-03478	Floor No.	
Date	01/2026	Sht. No.	S03
Scale	1/100	Job No.	
G.Manager		Architect	Designed By
ENG AYMEN		ENG IMEN	ENG IMEN