
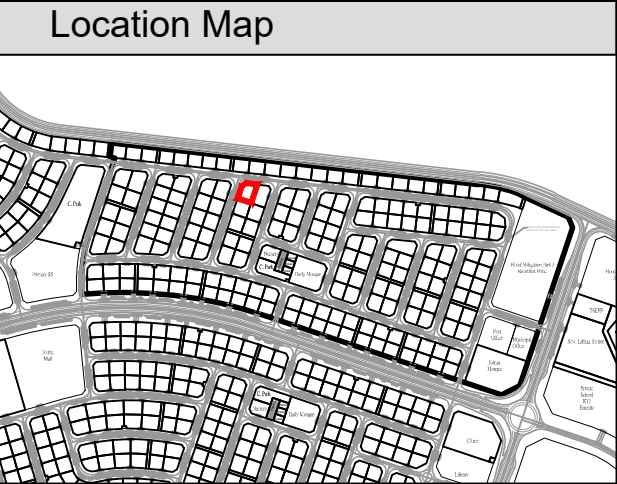



Landuse :Residential

Parcel Details	
Plot Number	406132384
Plot Area	1,116.00 m²
Max. Site Coverage	65 %
Max. Allowable Footprint	725.40 m²
Gate level	+17.05
Massing Control	
Number of Floors	G+1
Setback	
Front	2 m
Side	1.5 m
Rear	1.5 m
GFA Breakdown	
Residential	1,450.80 m²
TOTAL GFA	1,450.80 m²

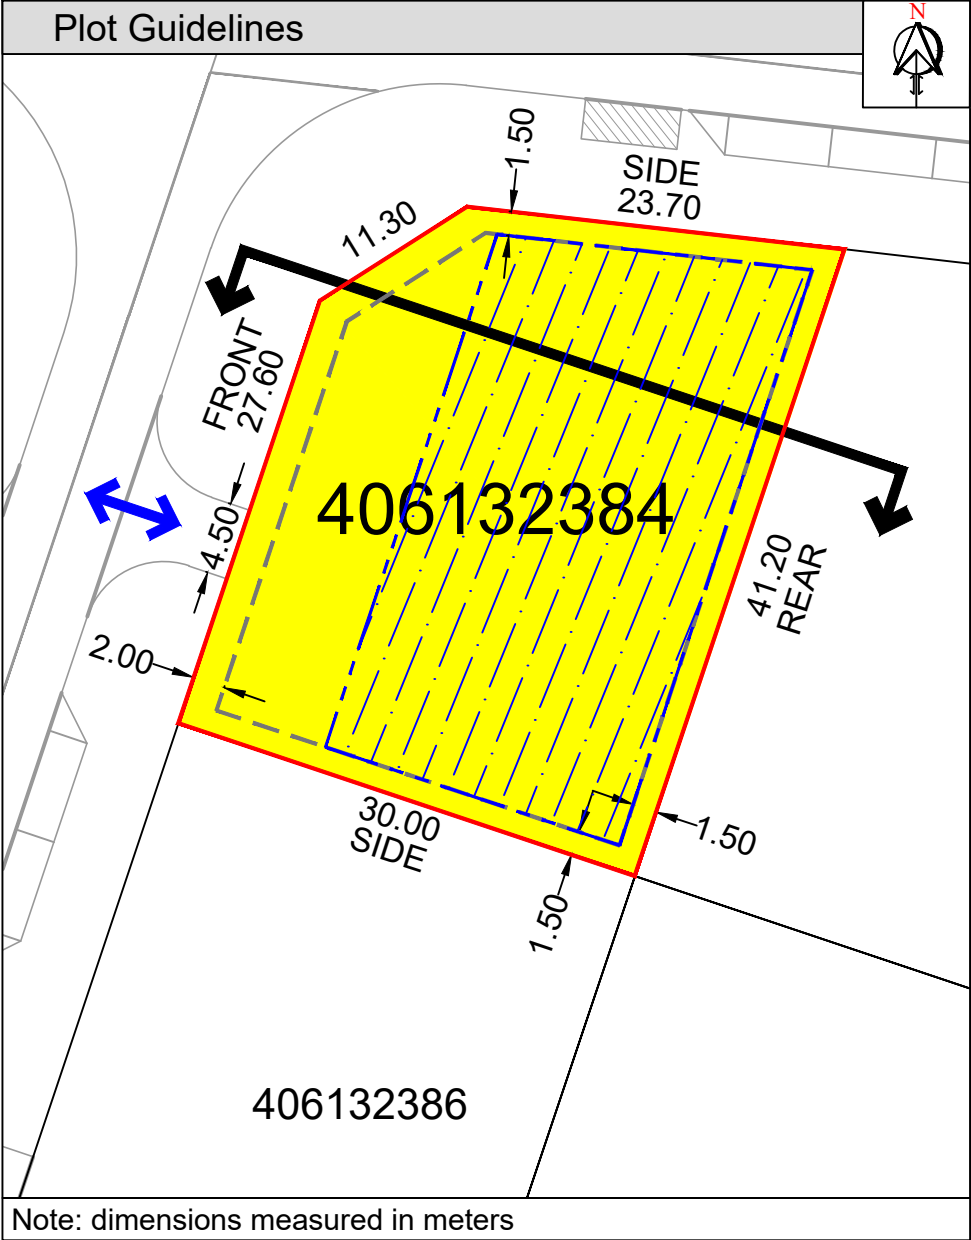

Legend

Yellow	Residential
Red line	Plot Boundary
Grey line	Setback
Blue hatched	Max. Allowable Footprint (indicative)
Blue double arrow	Access

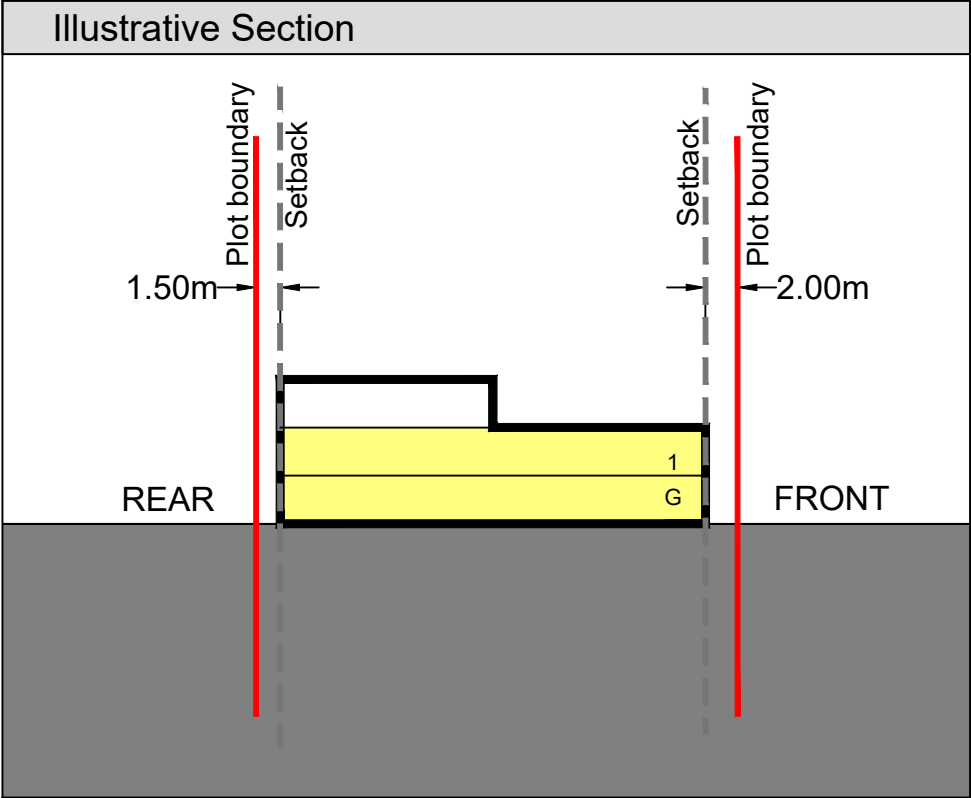

Location	Plot number	Drawn	Date	Scale	SAP Case No.	Drg. No.
Awafi - A3P03	406132384	—	11/11/2024	NTS	0	BR-401

Building Regulations

Director of Town Planning and Survey Administration	● Necessity of providing parking spaces inside plot boundary. ● Service blocks do not require setbacks and can be built directly at the plot limit. ● 50% usable space allowed on the Roof Floor in accordance with RAK Bldg. Regulations. ● No improvements or parking shelters will be allowed within the public realm. ● This authorization expires in one year starting from issuance date ,and considered cancelled after this time limit expires. In this case ,the owner should return to the administration to renew the authorization and abide any possible modifications. ● For highway noise abatement, plot owners may consider using sound insulation and sound proofing methods for building walls, floors and ceilings, such as ceiling panels, flooring material, acoustic doors and windows and other acoustic materials, along with landscape features, within their plot boundaries. Refer to RAK Barjeel Guidelines for guidance.	Building use: Residential	
		Allowed height: G + 1 The architectural and structural design is subject to the approval of the administration of buildings upon obtaining building permit	