

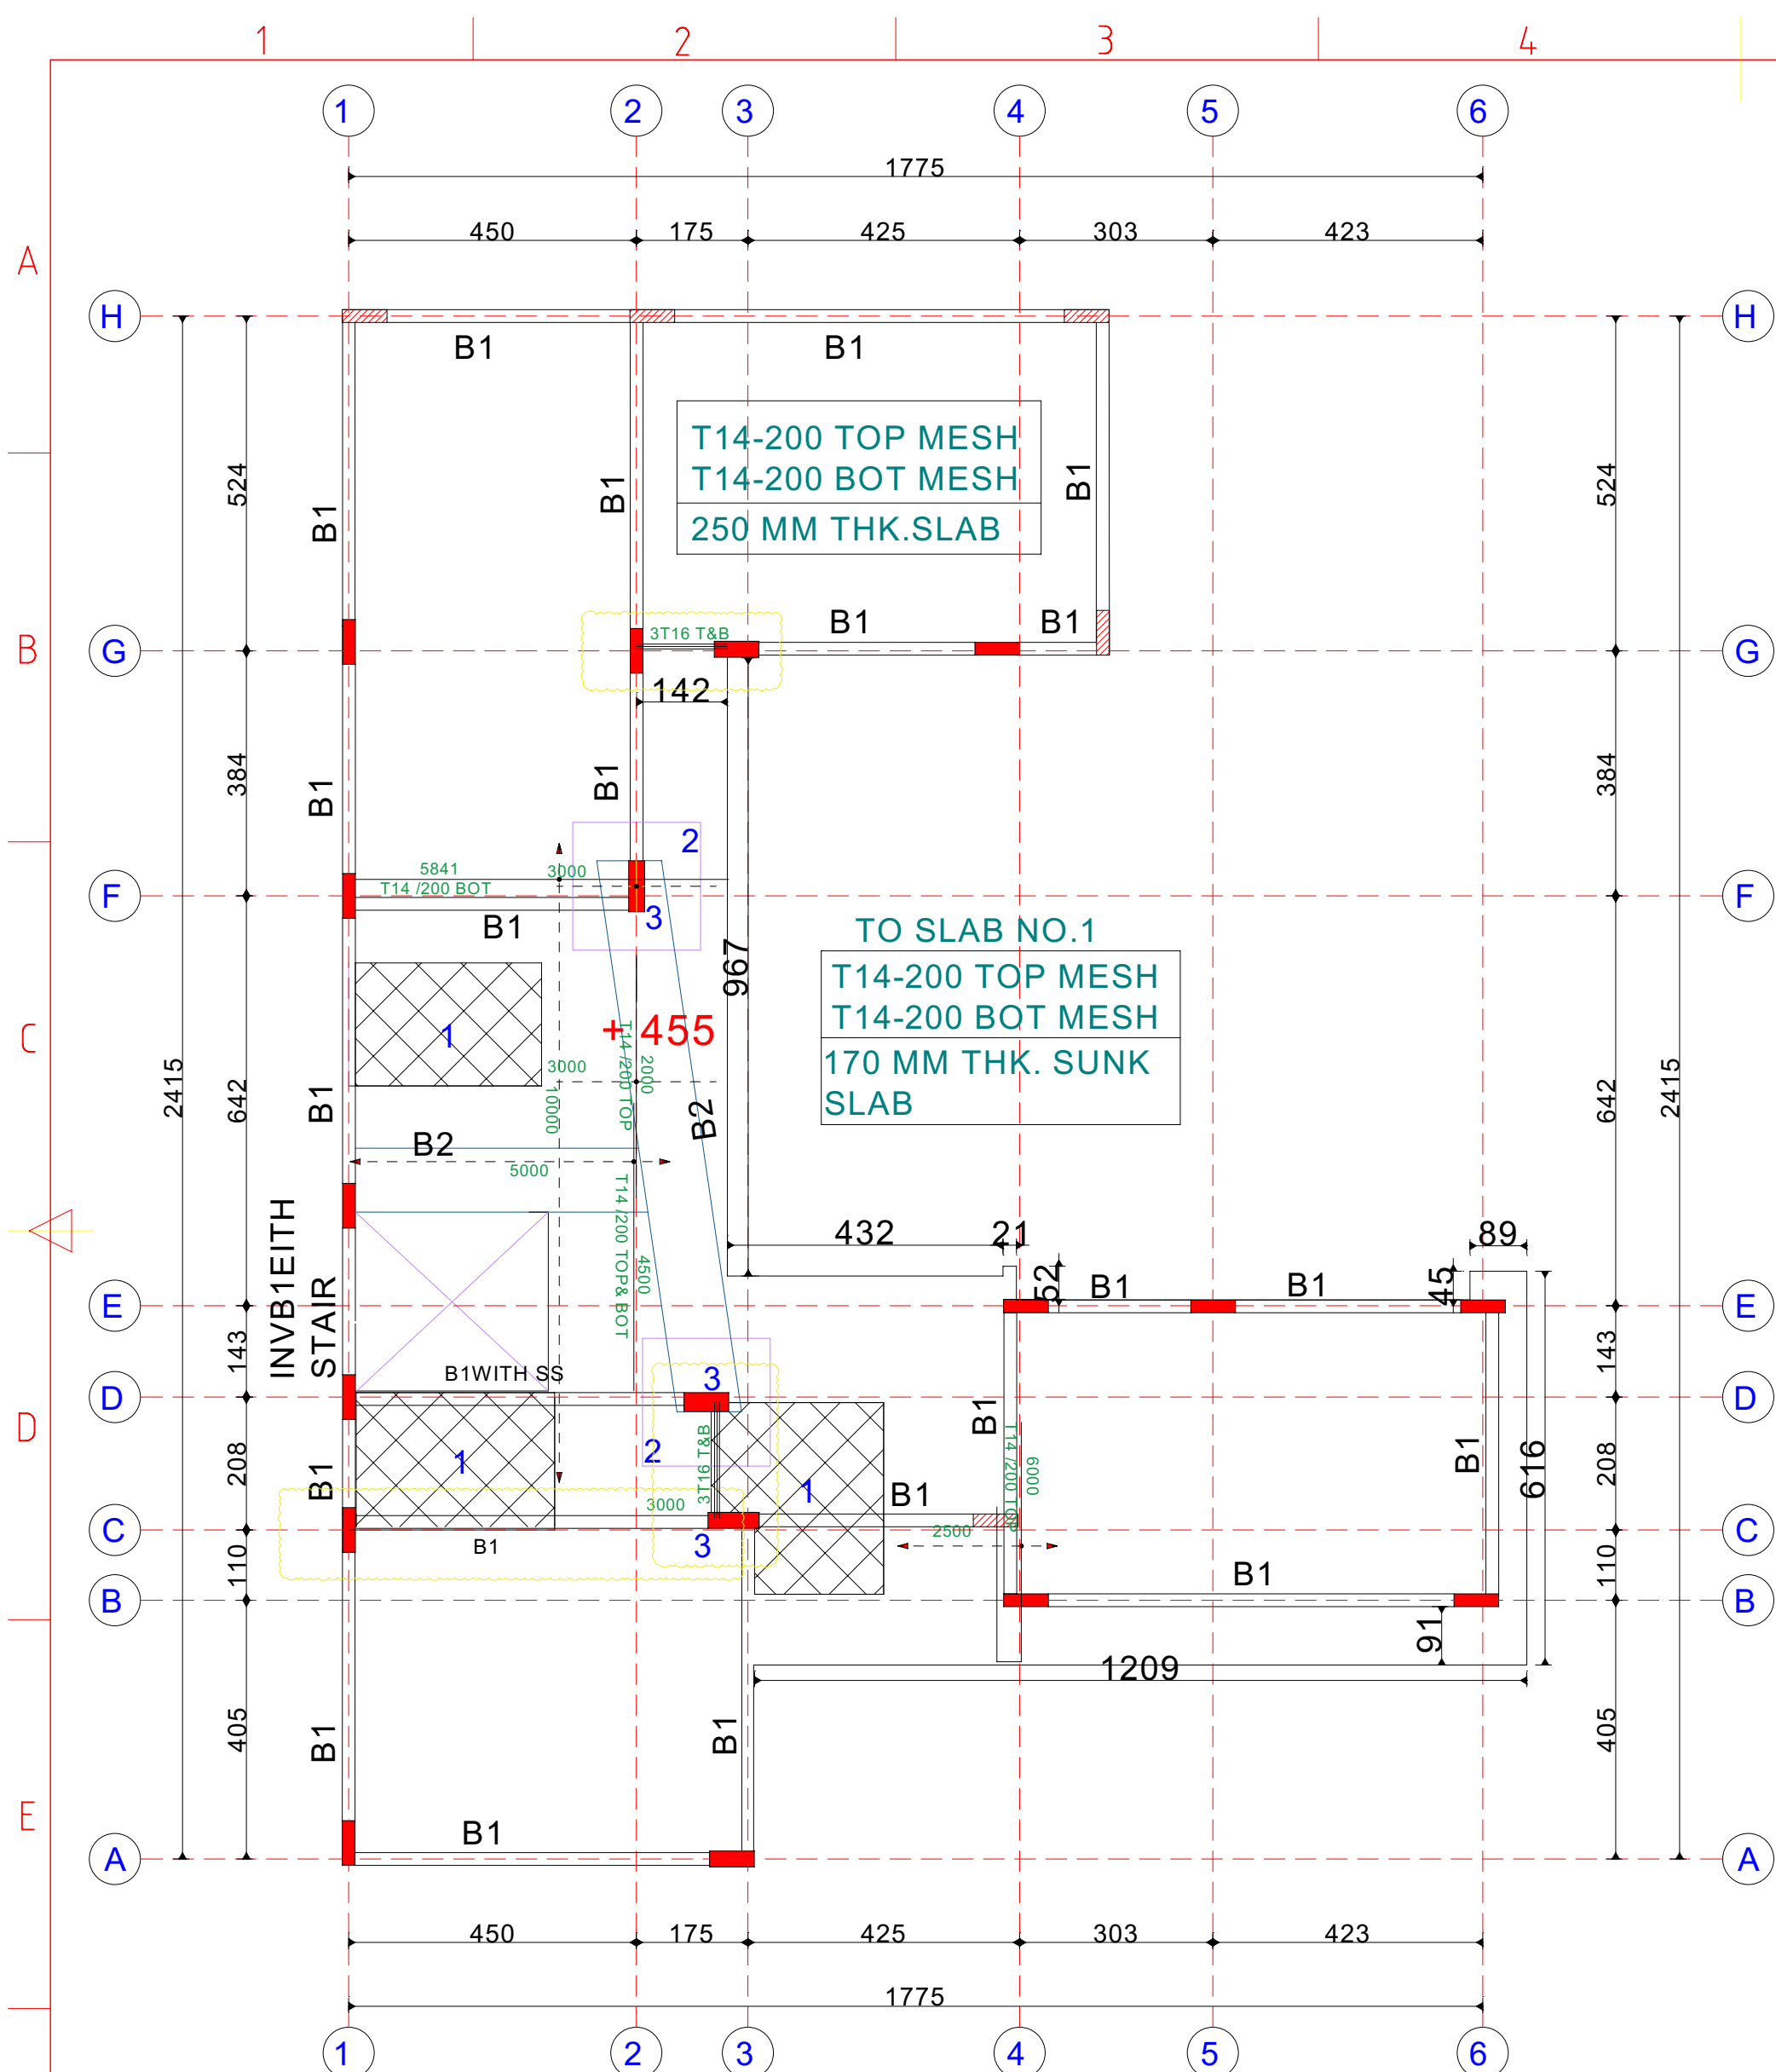
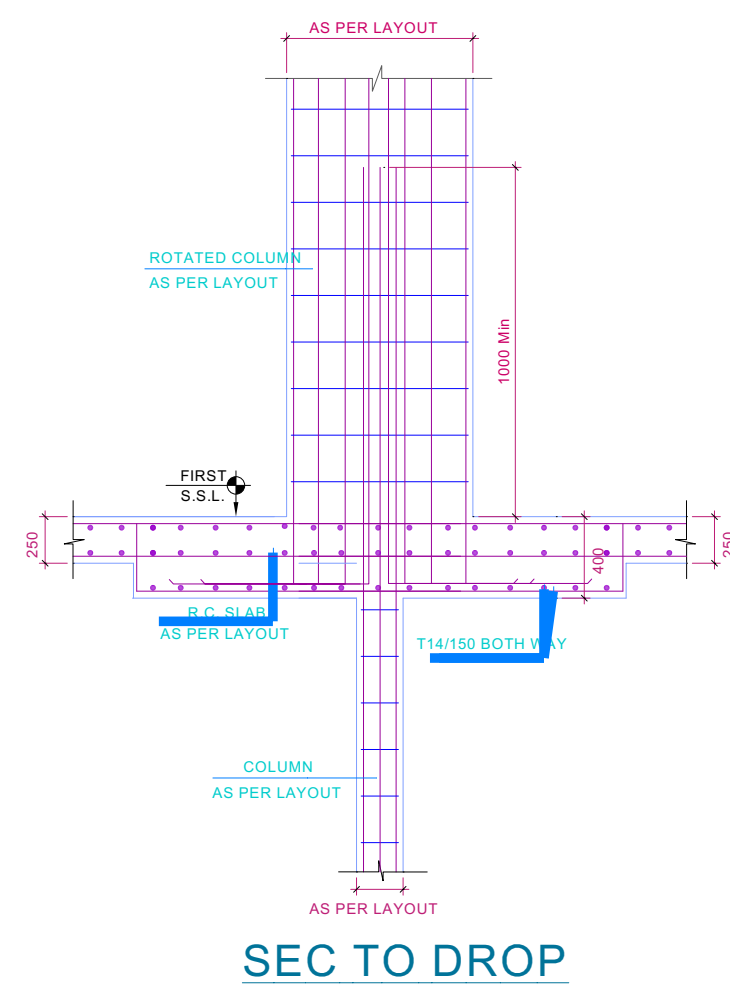
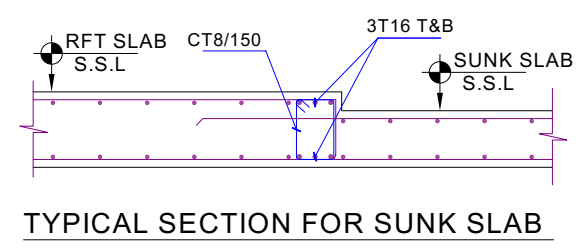


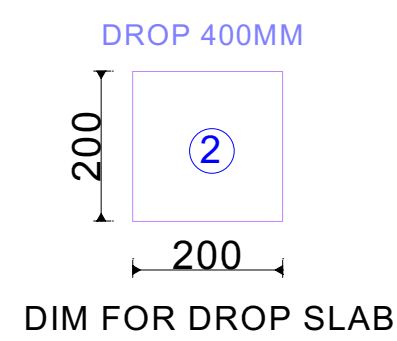

SCHEDULE OF GROUND BEAMS

TYPE	BEAM SIZE MM X MM	BOTTOM REINFORCEMENT		TOP REINFORCEMENT			SIDE BARS (F) EACH SIDE	STIRRUPS		NO OF LEGS	REMARKS
		(A) STRAIGHT	(B) EXTRA AT MID SPAN	(C) STRAIGHT	(D) EXTRA AT SUPPORT	(E) EXTRA AT SUPPORT		AT SUPPORT	AT MID SPAN		
B1	200 X 700	3T16	2T16	3T16	3T16	3T16	1T12	T8-150	T8-200	2	
B2	1000 X 310	4T16	4T16	4T16	4T16	4T16	1T12	T8-150	T8-200	2	

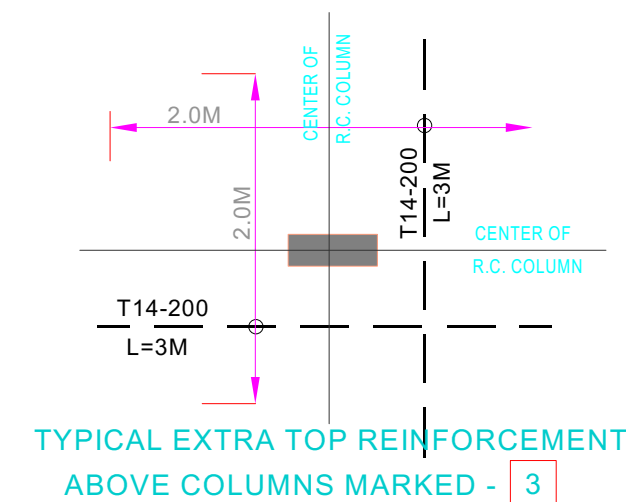

GROUND FLOOR SLAB-BEAMS

Government Of Ras Al Khaimah
R.A.K. Municipality
Buildings Administration

حكومة رأس الخيمة
دائرة البلدية
إدارة المباني

Approved On
16 February 2026

Building Permit #: PRMT-25-0004269

Approved By:

LEGEND:	
1)	COLUMN / WALL TO BE CONTINUED
2)	COLUMN / WALL TO BE TERMINATED

STRUCTURAL NOTES	CONCRETE COVERS :
ACI 318-11	Foundations cover = 75mm
F'C/FCU = 28/35 N/mm ²	Columns cover = 40mm
FY = 460N/mm ²	Walls cover = 30mm
FYt = 420N/mm ²	Beams cover = 40mm
	Slabs & Stairs cover = 25mm

Savana
Engineering Consultancy & Interior Design

Client	ABDULAZIZ TAHNOON AL MANSOORI		
Project	DOUBLE STORY VILLA		
Drg.Title	GROUND FLOOR SLAB-BEAMS		
Area	AWAFI	Floortype	
Case ID.	3174627	Draw. Type.	STRC
Sec No.	1	Com. No.	
Block No.		Plot No.	406132231
Bldg. No.	BLD-25-03478	Floor No.	
Date	02/2026	Sht. No.	S05
Scale	1/100	Job No.	
G.Manager	Architect	Designed By	
ENG AYMEN	ENG IMEN	ENG IMEN	