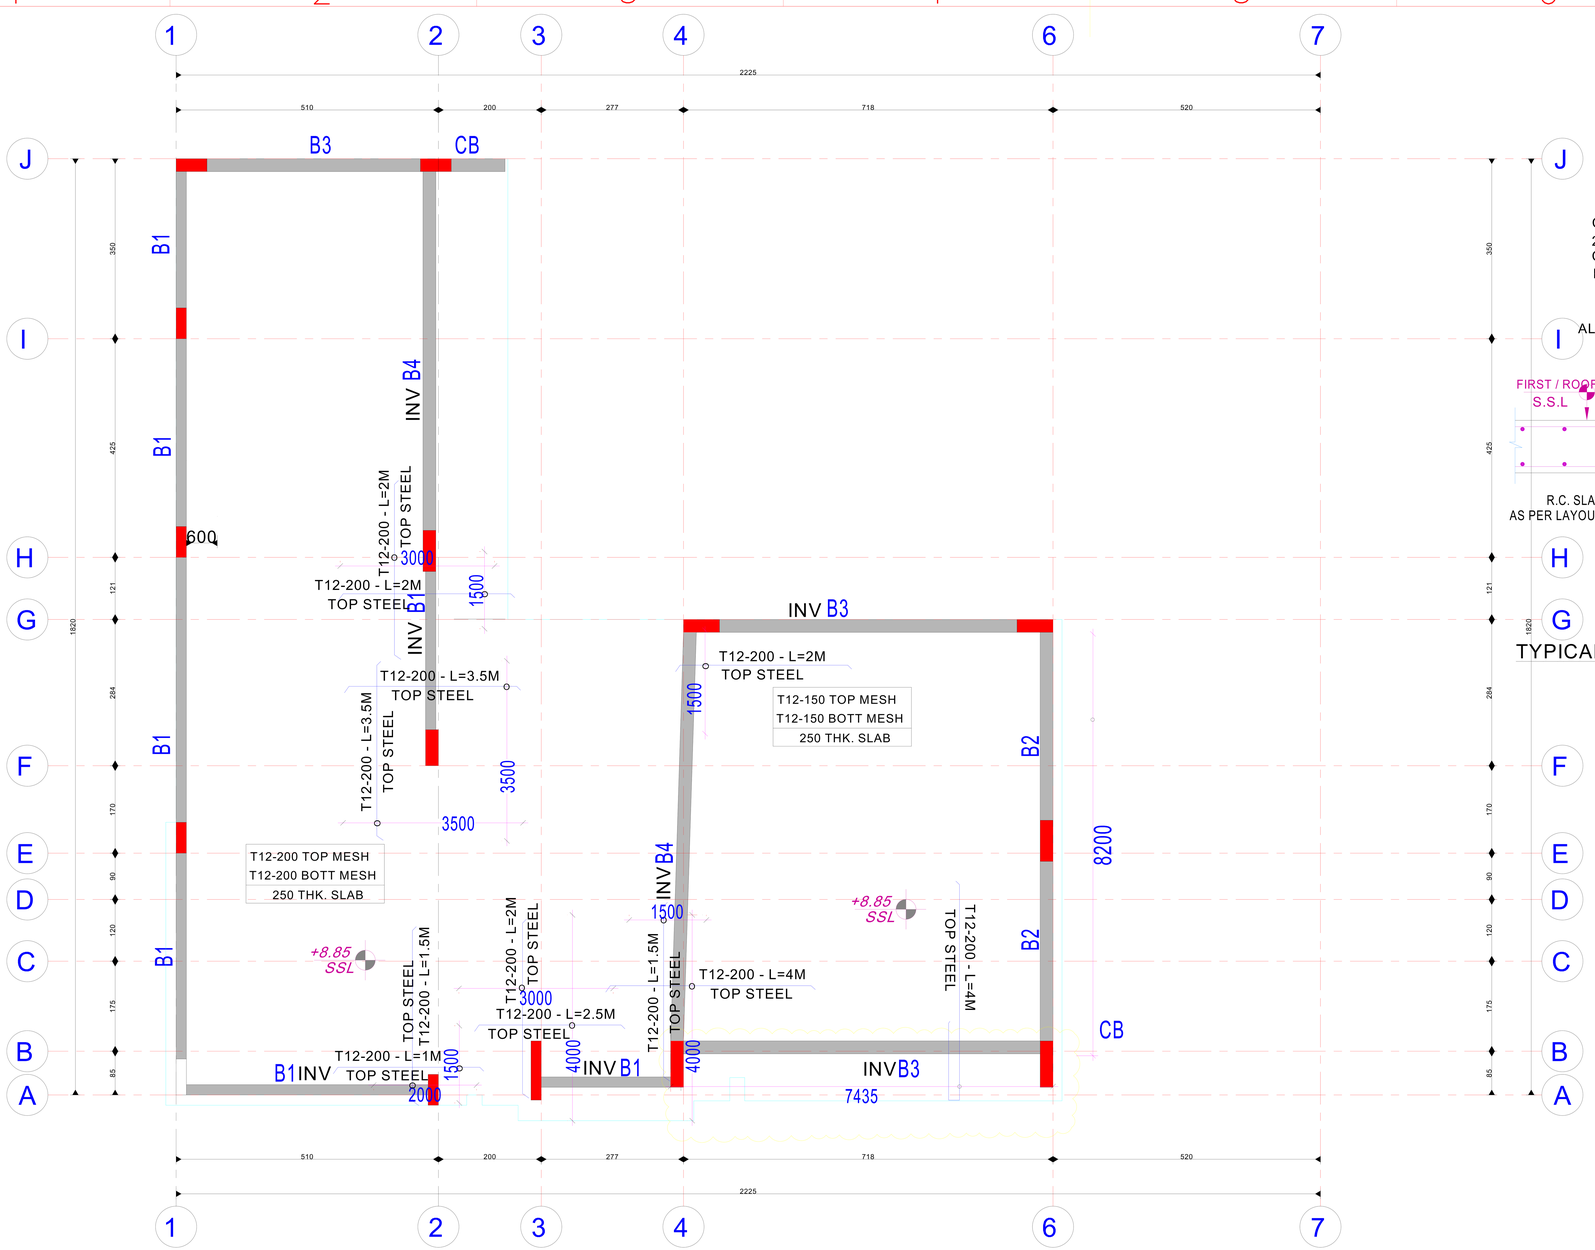

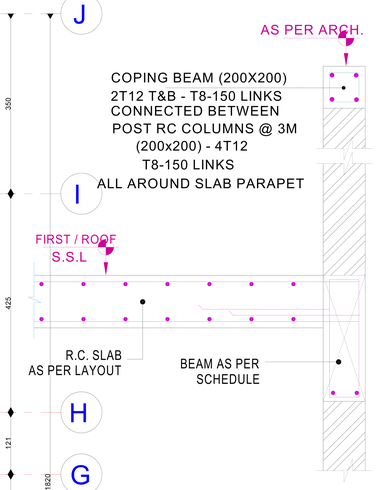

TYPICAL SECTION FOR PARAPET

Govemment Of Ras Al Khaimah
R.A.K. Municipality
Buildings Administration

حكومة رأس الخيمة
دائرة البلدية
إدارة المباني

Approved On — اعتمد في

16 June 2025

Building Permit #: PRMT-24-0004844

Appoved By:

STRUCTURAL NOTES	CONCRETE COVERS :
ACI 318-11	Foundations cover = 75mm
F'C/FCU = 28/35 N/mm2	Columns cover = 40mm
FY = 460N/mm2	Walls cover = 30mm
FYt = 420N/mm2	Beams cover = 40mm
	Slabs & Stairs cover = 25mm

SCHEDULE OF FIRST BEAMS

TYPE	BEAM SIZE	BOTTOM REINFORCEMENT		TOP REINFORCEMENT			SIDE BARS O.E.F (F)	STIRRUPS				NO OF LEGS	REMARKS
								AT SUPPORT		AT MIDSPAN			
	MM XMM	STRAIGHT (A)	EXTRA @ MID SPAN(B)	STRAIGHT (C)	EXTRA @ CONT. SUPPORT (D)	EXTRA @ DISCONT. SUPPORT (E)	EACH SIDE	OUTER (G1)	INNER (G2)	OUTER (H1)	INNER (H2)		
B1	200 X 700	2T16	1T16	2T16	1T16	1T16	1T12	T10-150	--------	T10-200	--------	2	
B2	250X 800	3T18	2T16	2T16	2T16	2T16	2T12	T10-150	--------	T10-200	--------	2	
B3	250 X 900	3T16	3T16	3T16	2T16	2T16	3T12	T10-100	--------	T10-200	--------	2	
B4	250 X 1200	3T18	3T18	3T18	3T16	3T16	4T12	T10-100	--------	T10-200	--------	2	
CB	250 X 900	3T16	---------	3T16+2T16			3T12	T10-100	--------	T10-200	--------	2	

FIRST FLOOR SLAB-BEAMS

Savana
Engineering Consultancy & interior design

Client	KHALED ALI SAEED BEN SHUOOM AL SHEHHI		
Project	DOUBLE STORY VILAA		
Drg.Title	FIRST FLOOR SLAB-BEAMS		
Area	ARIFAA	Floortype	
Case ID.	2906592	Draw. Type.	STRC
Sec No.	1	Com. No.	
Block No.		Plot No.	406131922
Bldg. No.	BLD-24-04245	Floor No.	
Date	JUNE-2025	Sht. No.	S06
Scale	1/100	Job No.	

G.Manager	Architect	Designed By
ENG AYMEN	ENG IMEN	ENG.IBRAHIM