



المخطط الموقعي / منحة


بلدية رأس الخيمة
إدارة التخطيط والمحاكاة
Ras Al Khaimah Municipality
Town Planning and Survey
Administration

بلدية رأس الخيمة
Ras Al Khaimah Municipality

المالك : على محمد على راشد الحبسي

الاشتراطات التخطيطية				مواصفات القسيمة					
منسوب الرصيف		عدد الطوابق		نسبة البناء		اسم المنطقة : سيح الغب		الرقم المميز : 205090049	
		<u>الارتدادات</u>						استخدام الارض : سكني	
الغرب		الشرق		الجنوب		الشمال		المساحة الكلية 1376.55 متر مربع = 14817.05 قدم مربع	
		<u>البيوزات</u>						المساحة المتأثرة 1376.55 متر مربع = 14817.05 قدم مربع	
الغرب		الشرق		الجنوب		الشمال		المساحة المتبقية 1376.55 متر مربع = 14817.05 قدم مربع	
				تاريخ الانتهاء : 03/07/2026		تاريخ الاصدار : 11/07/2025		رقم الكروكي : 202305	
				نوع المنحة : برنامج الشيخ زايد للإسكان		الرقم المرجعي / رقم الرسالة : 2025/9/8			

ملاحظات : تم التحويل من منحة عادية الممنوحة له بموجب الأمر الصادر بتاريخ 2015/2/9 إلى منحة برنامج الشيخ زايد للإسكان بموجب الرسالة الصادرة بتاريخ 2025/1/9

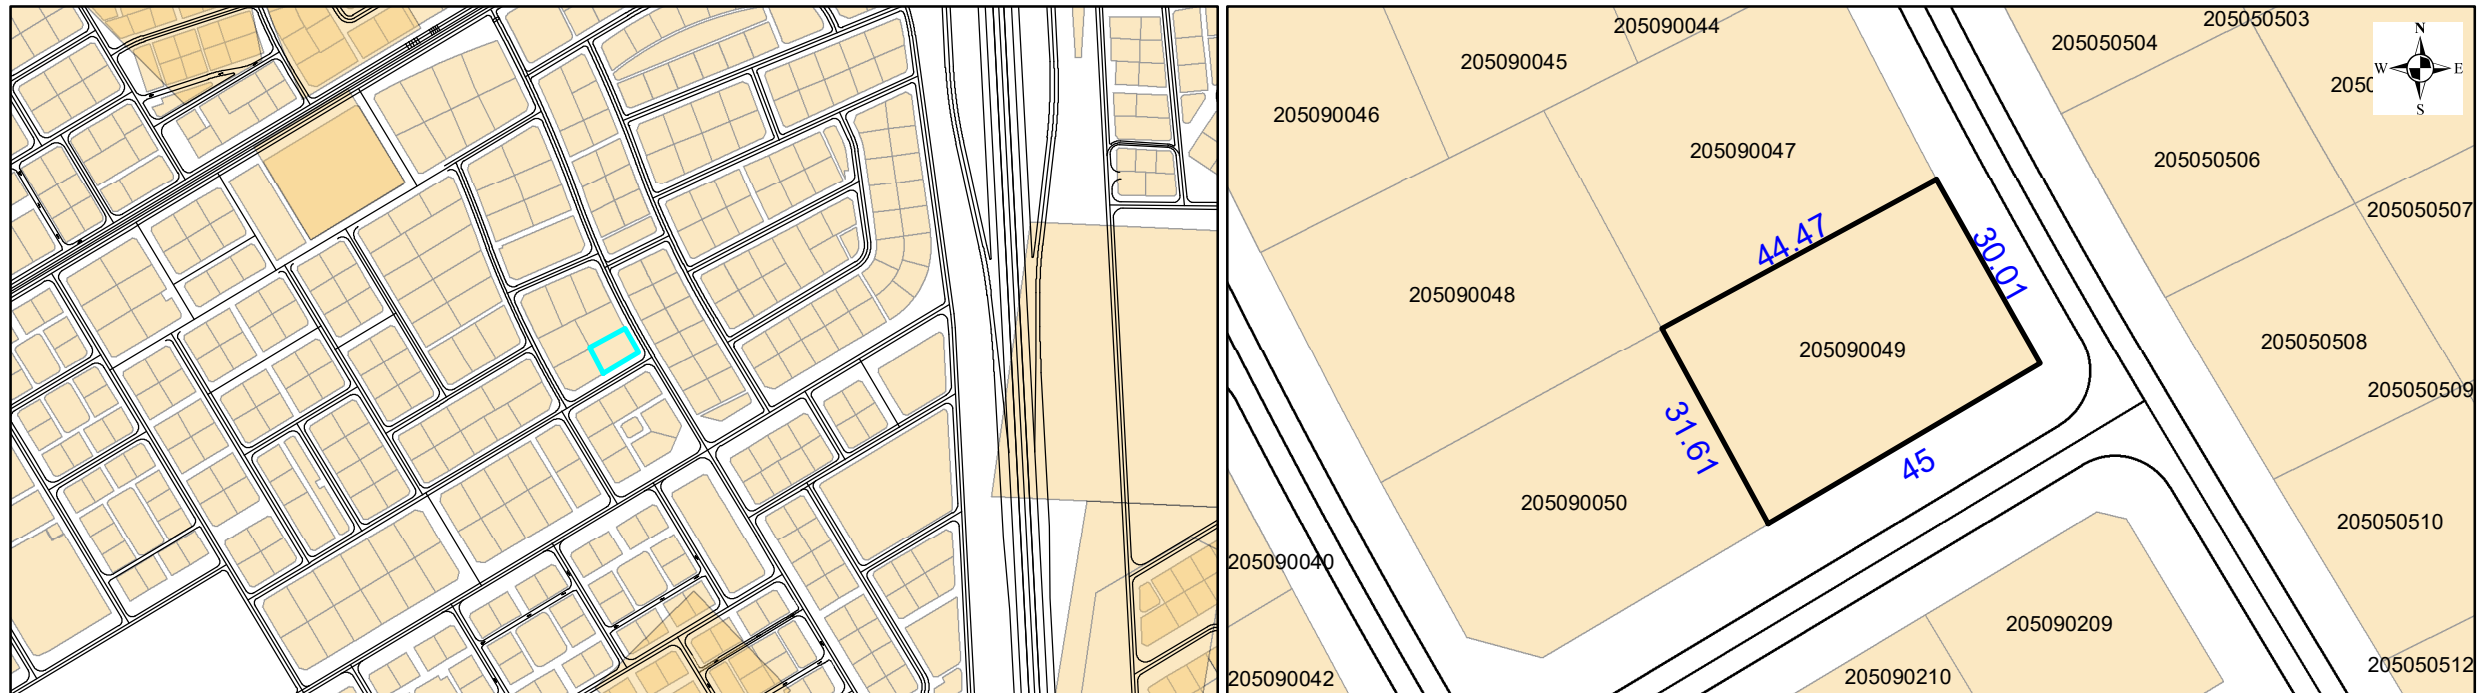

الرؤية بلدية رائدة لإمارة صحية وسعيدة ومستدامة الرسالة الابتكار في تقديم خدمات بلدية متميزة تضمن الاستدامة في التطوير العمراني والصحة العامة من خلال التوظيف الأمثل للموارد لتحقيق السعادة لكافة شرائح المجتمع		اعتماد مدير ادارة التخطيط والمساحة		ممنوع البيع نهائيا بأمر من سمو الحاكم المؤرخ في 2001/01/31 القسيمة مقيدة	
--	--	---------------------------------------	--	---	--