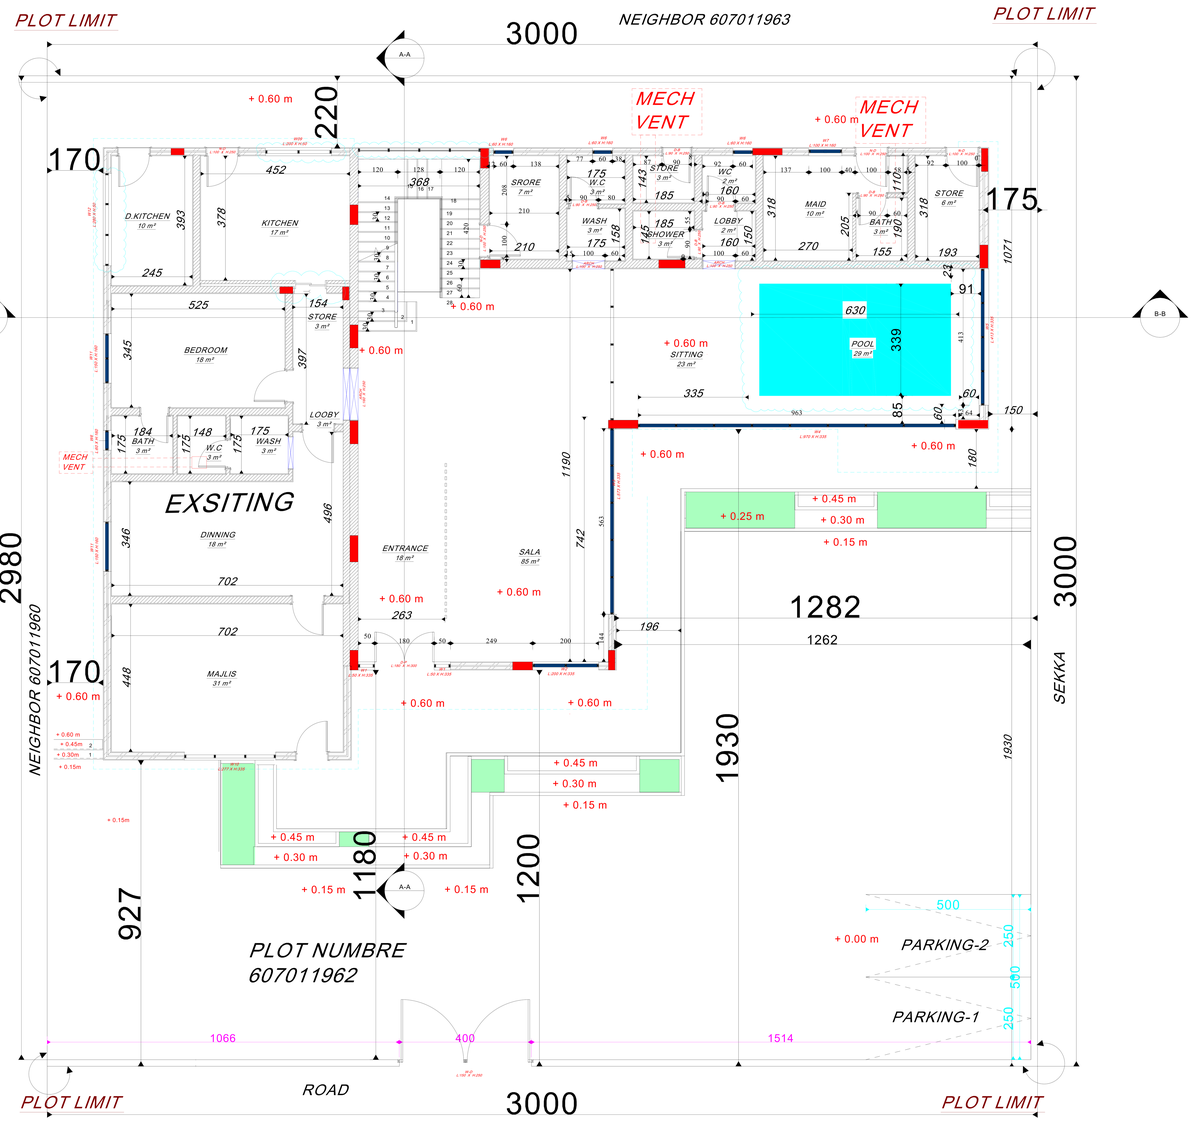

Govemment Of Ras Al Khaimah
R.A.K. Municipality
Buildings Administration

حكومة رأس الخيمة
دائرة البلدية
إدارة المباني

Approved On — اعتمد في

21 May 2025

Building Permit #: PRMT-24-0005227

Appoved By:

SITE SETTING PLAN

Savana
Engineering Consultancy & interior design

Client	SAEED AHMED MOHAMMED HASAN ALMANSORI		
Project	DOUBLE STORY VILAA		
Drg.Title	SITE SETTING PLAN		
Area	ARIFAA	Floortype	
Case ID.	2885318	Draw. Type.	ARCH
Sec No.	1	Com. No.	
Block No.		Plot No.	607011962
Bldg. No.	BLD-24-03157	Floor No.	
Date	OCT-2024	Sht. No.	A03
Scale	1/100	Job No.	

G.Manager	Architect	Designed By
ENG AYMEN	ENG IMEN	ENG IMEN

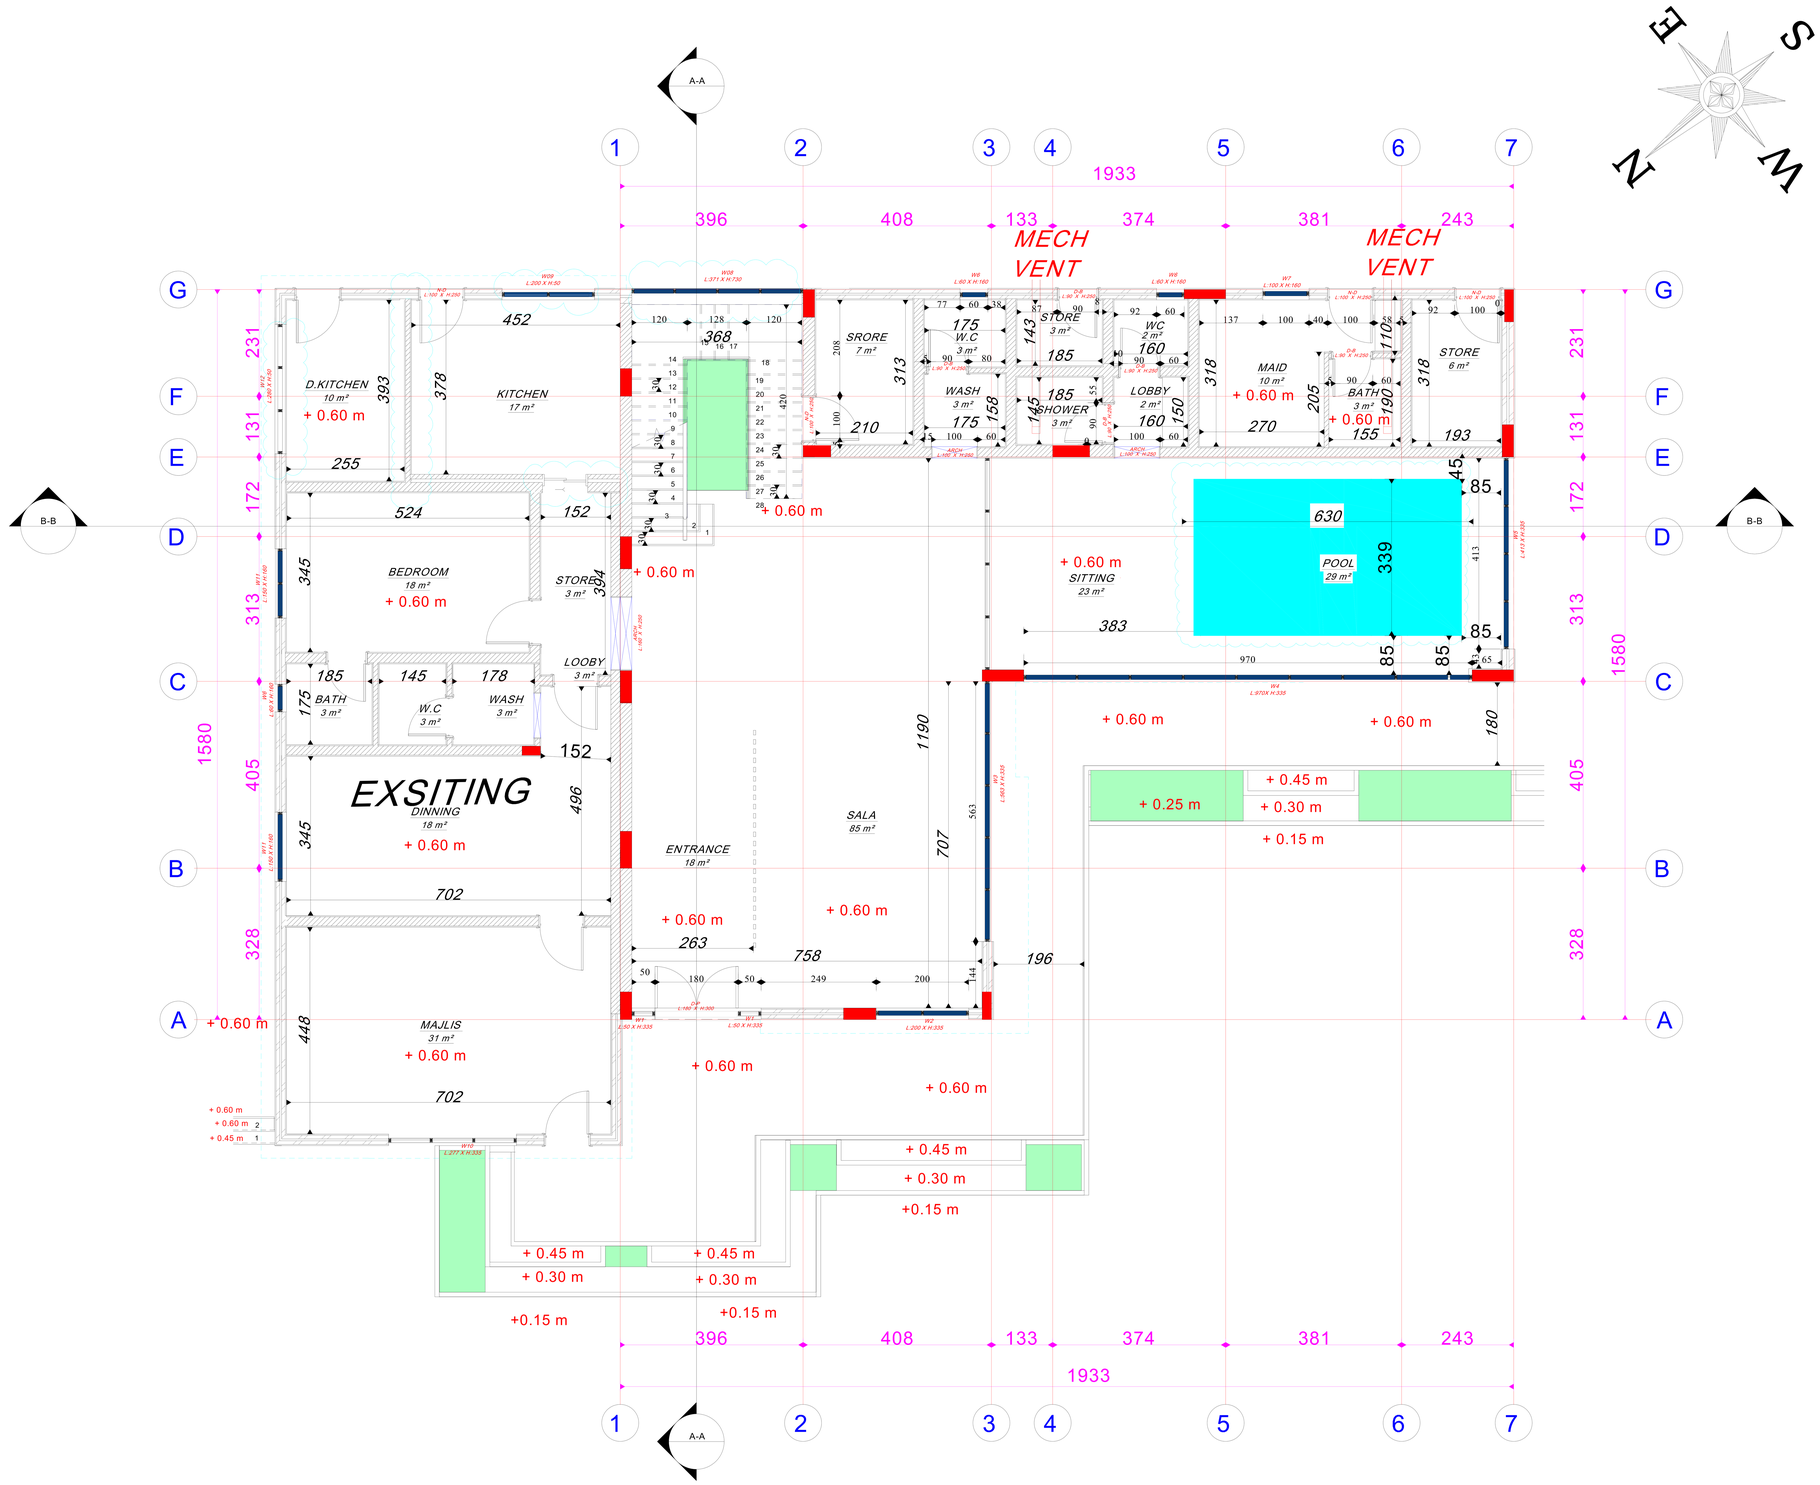

FINISHING FOR VERANDAH	FINISHING FOR DRESSING AREA	FINISHING FOR BATH,WC & WASH

FLOORING	F1 Ceramic glazed tiles	
	F2 Ceramic Tiles (Non Slippery)	
	F3 Marble Tiles	
WALLS	W1 Acrylic emulsion paint	
	W2 Ceramic tiles up to ceiling	
	W3 Epoxy paint.	
SKIRTING	S1 Ceramic Tiles. 10cm hight	
	S2 Marble tiles 10cm hight	
CEILING	C1 Acrylic emulsion paint	
	C2 Oil Paint.	
	C3 Epoxy paint.	

Govemment Of Ras Al Khaimah
R.A.K. Municipality
Buildings Administration

حكومة رأس الخيمة
دائرة البلدية
إدارة المباني

Approved On — اعتمد في

21 May 2025

Building Permit #: PRMT-24-0005227

Approved By:

Note :-

* Rcc Lintels Must Be Made On Top Of All Doors , Arches And Windows All Of Them Are At Least 0.20 m Thick.
* All Blocks Adjacent To All Doors , Arches And Windows Must Be A Solid Block .

Rooms	Space	Number
Residential	383.3	
Commercial		
Industrial		
Goverment		
Resident.-Comm.		
Total		

Savana
Engineering Consultancy & interior design

Client	SAEED AHMED MOHAMMED HASAN ALMANSORI		
Project	DOUBLE STORY VILAA		
Drg.Title	GROUND FLOOR PLAN		
Area	ARIFAA	Floortype	G
Case ID.	2885318	Draw. Type.	ARCH
Sec No.	1	Com. No.	
Block No.		Plot No.	607011962
Bldg. No.	BLD-24-03157	Floor No.	01
Date	OCT-2024	Sht. No.	A04
Scale	1/100	Job No.	

G.Manager	Architect	Designed By
ENG AYMEN	ENG IMEN	ENG IMEN

GROUND FLOOR PLAN