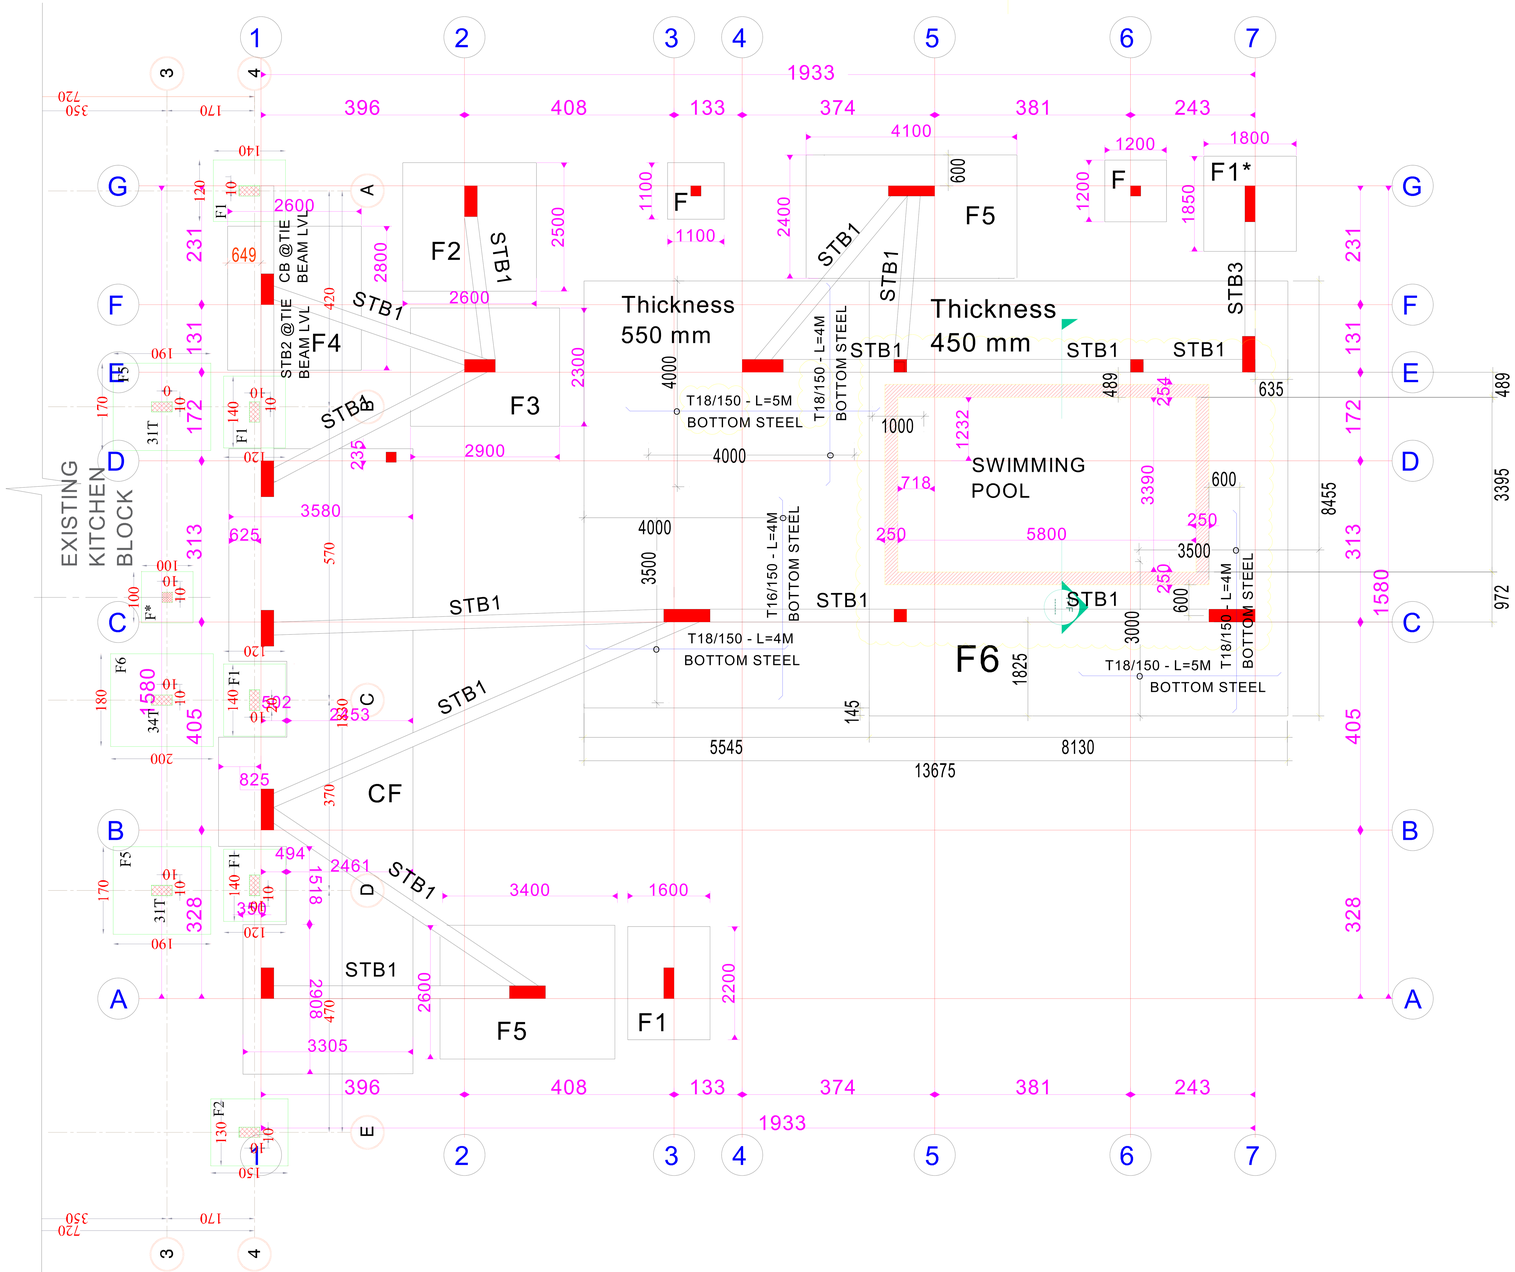

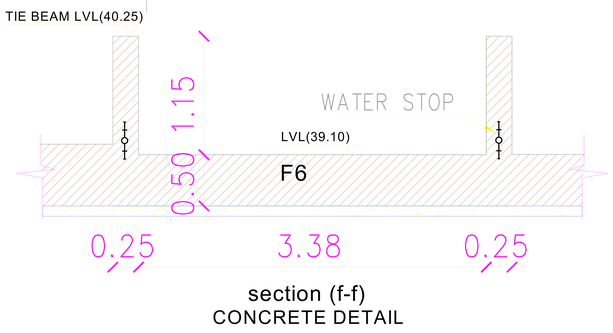

section (f-f)
CONCRETE DETAIL

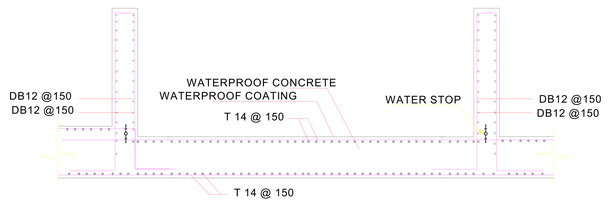

section (f-f)
STEEL DETAIL

FONDATION LAYOUT

Govvernment Of Ras Al Khaimah
R.A.K. Municipality
Buildings Administration

حكومة رأس الخيمة
دائرة البلدية
إدارة المباني

Approved On — اعتمد في

21 May 2025

Building Permit #: PRMT-24-0005227

Approved By:

STRUCTURAL NOTES	CONCRETE COVERS :
ACI 318-11	Foundations cover = 75mm
F'C/FCU = 28/35 N/mm2	Columns cover = 40mm
FY = 460N/mm2	Walls cover = 30mm
FYt = 420N/mm2	Beams cover = 40mm
	Slabs & Stairs cover = 25mm

Rooms	Space	Number
Residential		
Commercial		
Industrial		
Goverment		
Resident.-Comm.		
Total		

Savana
Engineering Consultancy & Interior design

Client	SAEED AHMED MOHAMMED HASAN ALMANSOORI		
Project	DOUBLE STORY VILAA		
Drg.Title	FOUNDATION LAYOUT		
Area	ARIFAA	Floortype	
Case ID.	2885318	Draw. Type.	STRC
Sec No.	1	Com. No.	
Block No.		Plot No.	607011962
Bldg. No.	BLD-24-03157	Floor No.	
Date	MARCH-2025	Sht. No.	S02
Scale	1/100	Job No.	

G.Manager	Architect	Designed By
ENG AYMEN	ENG IMEN	ENG.IBRAHIM

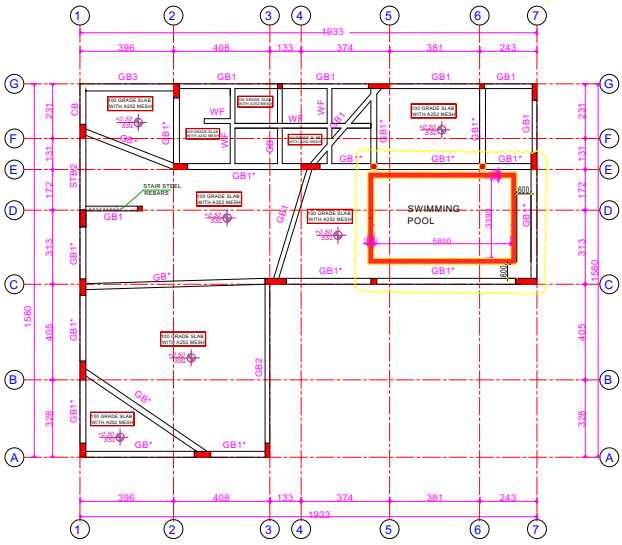

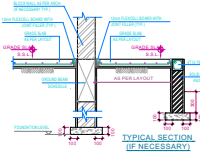

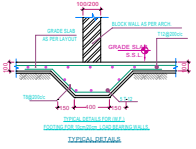

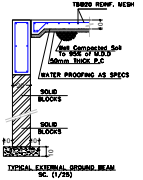

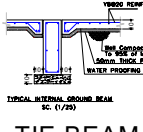

TIE BEAM LAYOUT

SCHEDULE OF GROUND BEAMS

TYPE	BEAM SIZE MM x MM	BOTTOM REINFORCEMENT STRAIGHT (A)	BOTTOM REINFORCEMENT EXTRA @ MID SPAN(B)	TOP REINFORCEMENT STRAIGHT (C)	TOP REINFORCEMENT EXTRA @ CONT SUPPORT (D)	TOP REINFORCEMENT EXTRA @ DISCON SUPPORT (E)	SIDE BARS O.E.F.(F) EACH SIDE	STIRRUPS AT SUPPORT OUTER (G)	STIRRUPS AT SUPPORT INNER (GD)	STIRRUPS AT MIDSPAN OUTER (H)	STIRRUPS AT MIDSPAN INNER (HD)	NO OF LEGS	REMARKS
GB*	250 x 550	2T16	----	2T16	----	----	1T12	T8-150	----	T8-200	----	2	ABOVE STB
GB	200 X 500	2T16	----	2T16	----	----	1T12	T8-150	----	T8-200	----	2	
GB1	200 X 600	2T16	1T16	2T16	1T16	1T16	1T12	T8-150	----	T8-200	----	2	
GB1*	250 X 600	3T16	2T14	2T16	1T16	1T16	1T12	T8-150	----	T8-200	----	2	
GB2	200 X 700	3T16	2T14	2T16	2T14	2T14	2T12	T10-150	----	T10-200	----	2	
GB2	250 X 700	3T16	2T14	2T16	2T14	2T14	2T12	T10-150	----	T10-200	----	2	
GB3	300 X 600	3T16	2T14	2T16	2T14	2T14	2T12	T10-150	----	T10-200	----	2	

SCHEDULE OF STB

TYPE	BEAM SIZE MM x MM	BOTTOM REINFORCEMENT STRAIGHT (A)	BOTTOM REINFORCEMENT EXTRA @ MID SPAN(B)	TOP REINFORCEMENT STRAIGHT (C)	TOP REINFORCEMENT EXTRA @ CONT SUPPORT (D)	SIDE BARS O.E.F.(F) EACH SIDE	STIRRUPS AT SUPPORT OUTER (GI)	STIRRUPS AT SUPPORT INNER (GO)	STIRRUPS AT MIDSPAN OUTER (HI)	STIRRUPS AT MIDSPAN INNER (HO)	NO OF LEGS	REMARKS
STB2	250 x 1200	3T18	------	2T18+2T18	------	4T12	T10-100	------	T10-150	------	2	AT TIE BEAM LEVEL
CB	250 x 1200	3T18	------	3T18+2T18	------	4T12	T10-100	------	T10-150	------	2	AT TIE BEAM LEVEL

Government Of Ras Al Khaimah
R.A.K. Municipality
Buildings Administration

حكومة رأس الخيمة
دائرة البلدية
إدارة المباني

Approved On
اعتمد في
21 May 2025

Building Permit #: PRMT-24-0005227
Approved By:

STRUCTURAL NOTES

ACI 318-11
F'C/F'CU = 28/35 N/mm2
FY = 460N/mm2
FYt = 420N/mm2

CONCRETE COVERS :

Foundations cover = 75mm
Columns cover = 40mm
Walls cover = 30mm
Beams cover = 40mm
Slabs & Stairs cover = 25mm

LEGEND:

1) COLUMN / WALL TO BE CONTINUED
2) COLUMN / WALL TO BE TERMINATED

Savana
Engineering Consultancy & Advisory Services

Client	SAEED AHMED MOHAMMED HASAN ALMANSOORI
Project	DOUBLE STORY VILAA
Drg.Title	TIE BEAM LAYOUT
Area	ARIFAA — Floortype
Case ID.	2885318 — Draw. Type. STRC
Sec No.	1 — Com. No.
Block No.	— Plot No. 607011962
Bldg. No.	BLD-24-03157 — Floor No.
Date	OCT-2024 — Sht. No. S04
Scale	1/100 — Job No.

G.Manager	Architect	Designed By
ENG AYMEN	ENG IMEN	ENG.IBRAHIM

S04 TIE BEAMS LAYOUT